


MC13 | RECORTE DO HIDRANTE


RIPADO DE MADEIRA MACIÇA SOBRE PAINEL DE MDF PRETO RESISTENTE À UMIDADE (ULTRA)
PORTA DE VIDRO DO HIDRANTE SEGUNDO A NORMA DOS BOMBEIROS EM DIMENSÃO E VENTILAÇÃO
02 UNIDADES

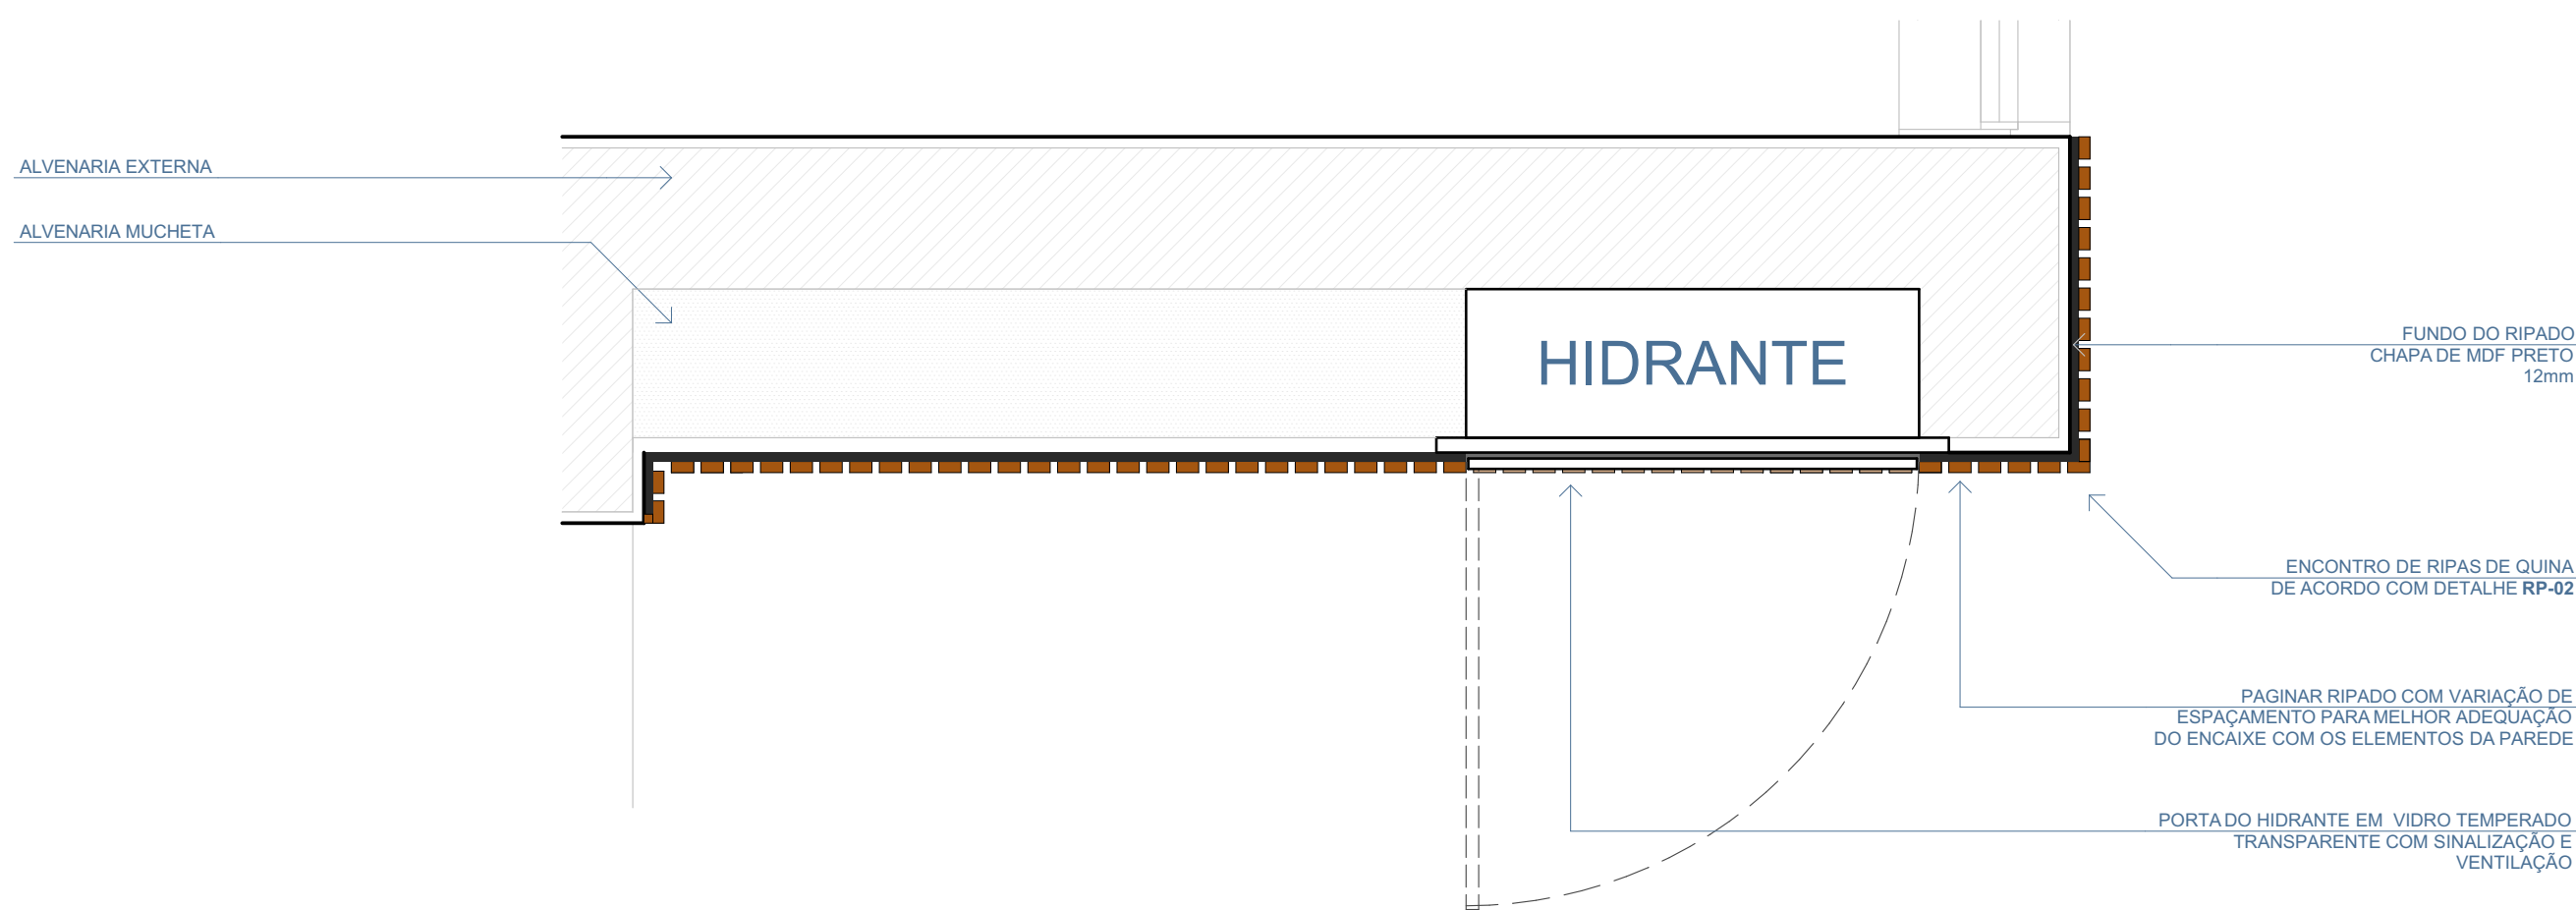


PLANTA BAIXA

MC14 | RECORTE PORTA CORTA-FOGO

RIPADO DE MADEIRA MACIÇA SOBRE PAINEL DE MDF PRETO RESISTENTE À UMIDADE (ULTRA)
04 UNIDADES

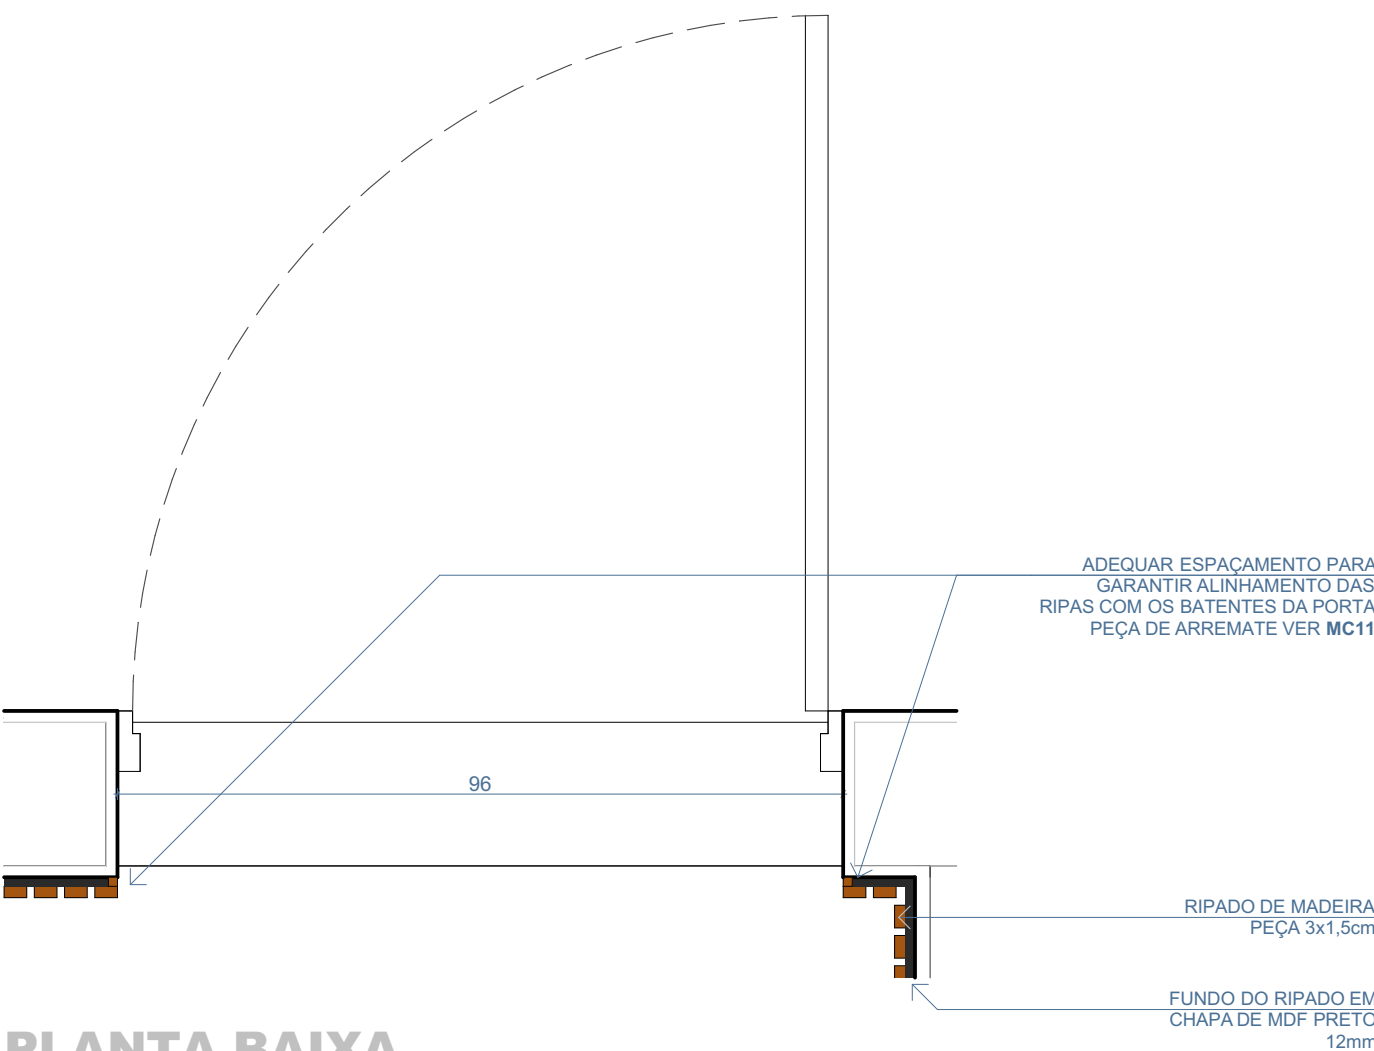


PLANTA BAIXA

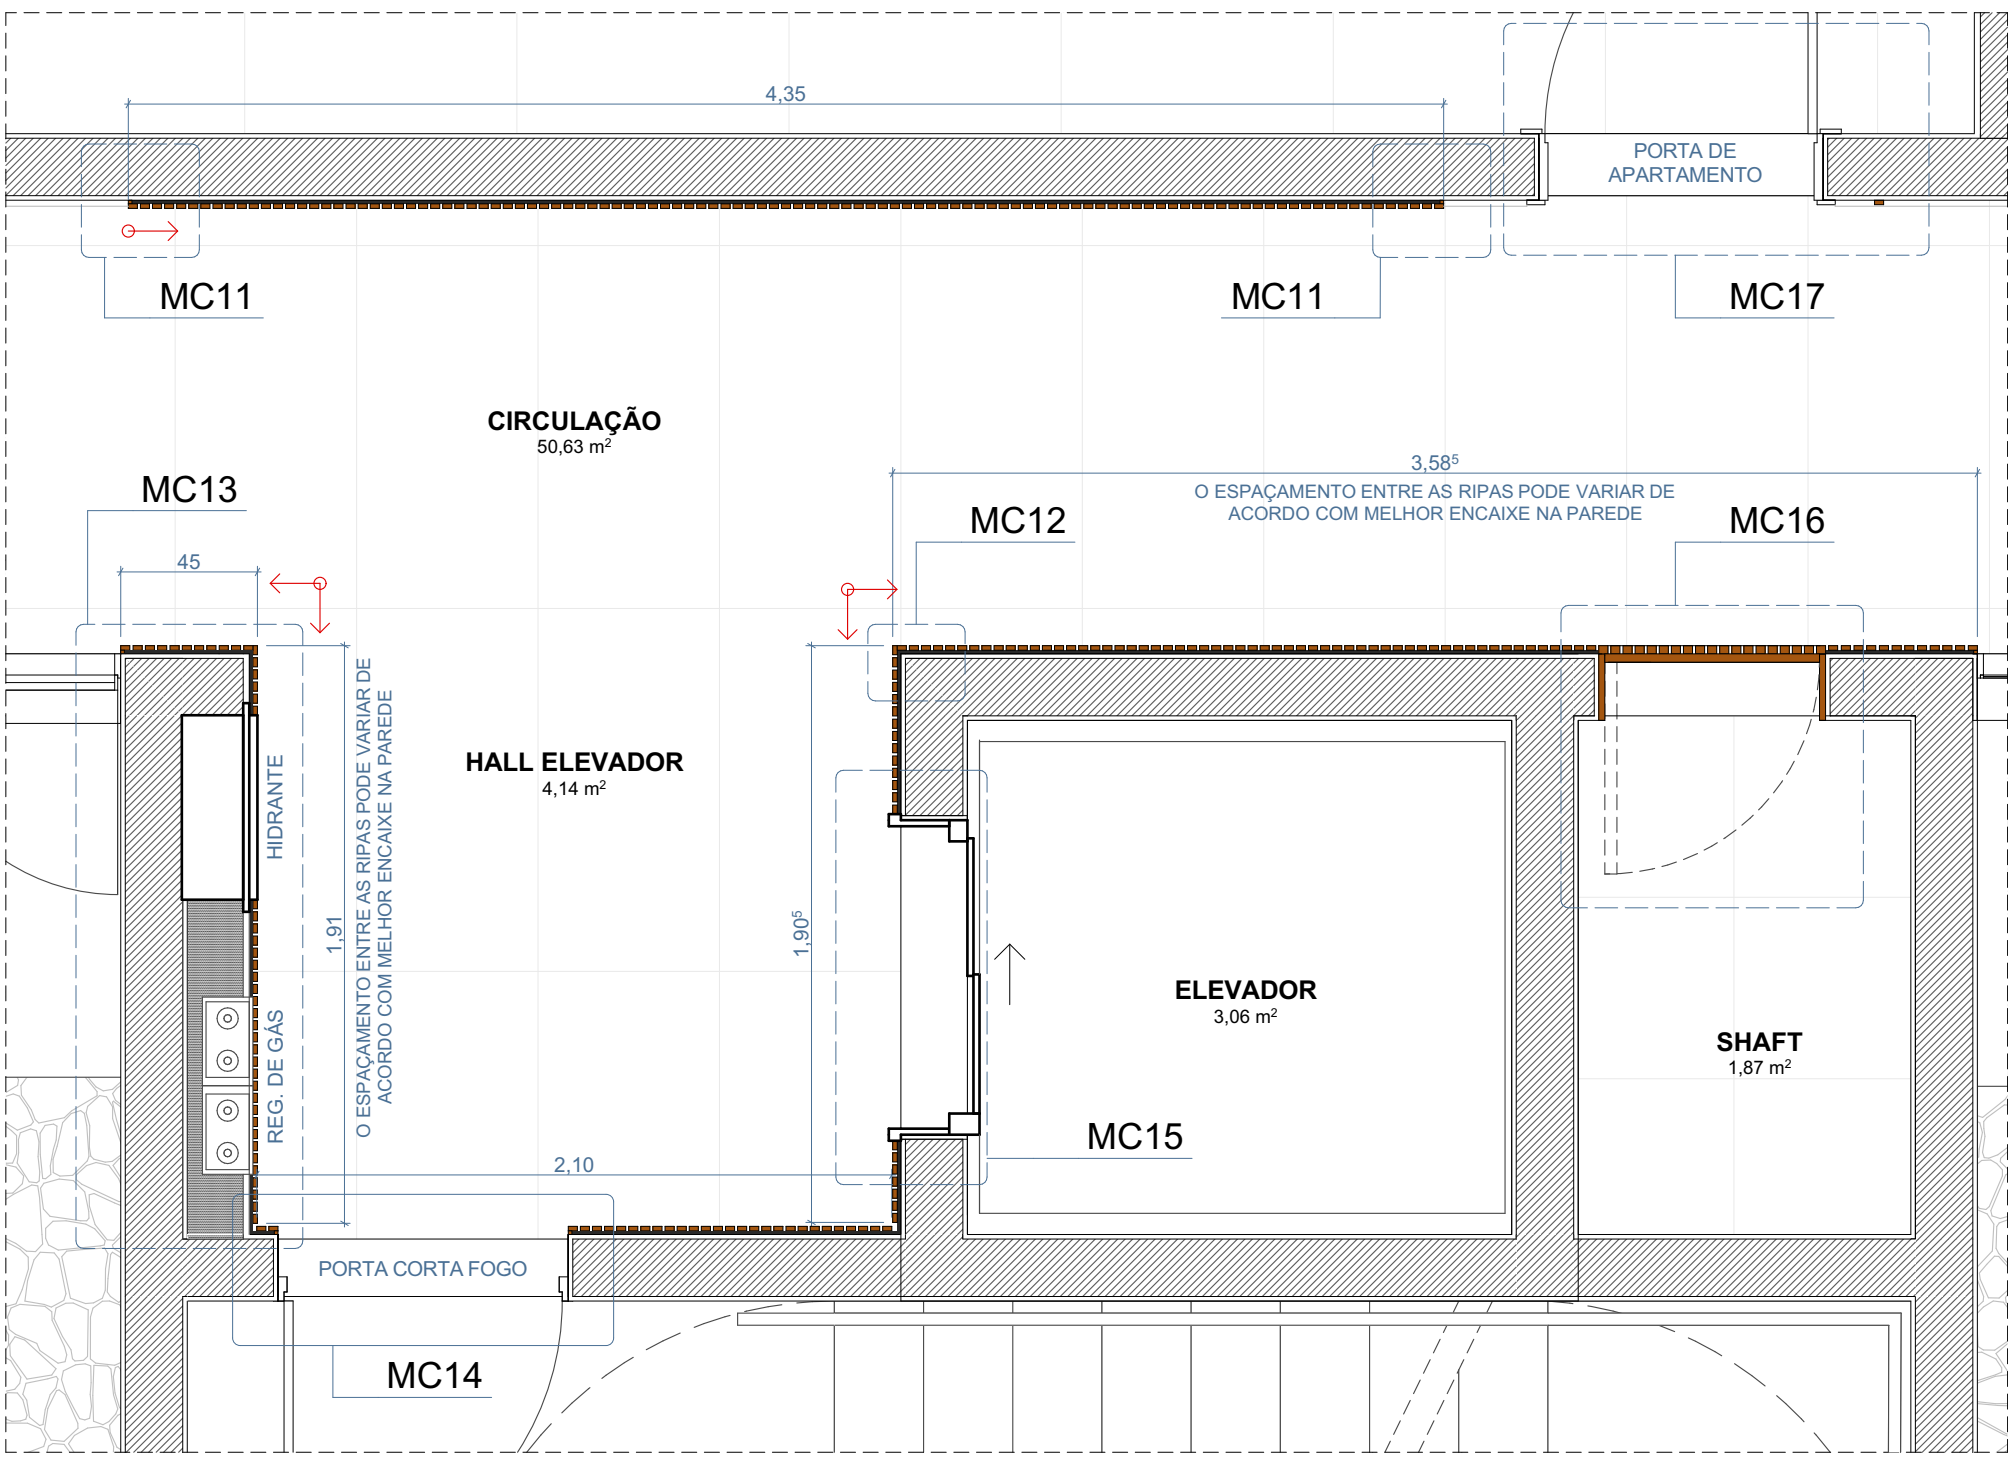

PLANTA BAIXA
ESCALA 1:25

MC11 | DETALHE DO PAINEL RIPADO


RIPADO DE MADEIRA MACIÇA SOBRE PAINEL DE MDF PRETO RESISTENTE À UMIDADE (ULTRA)

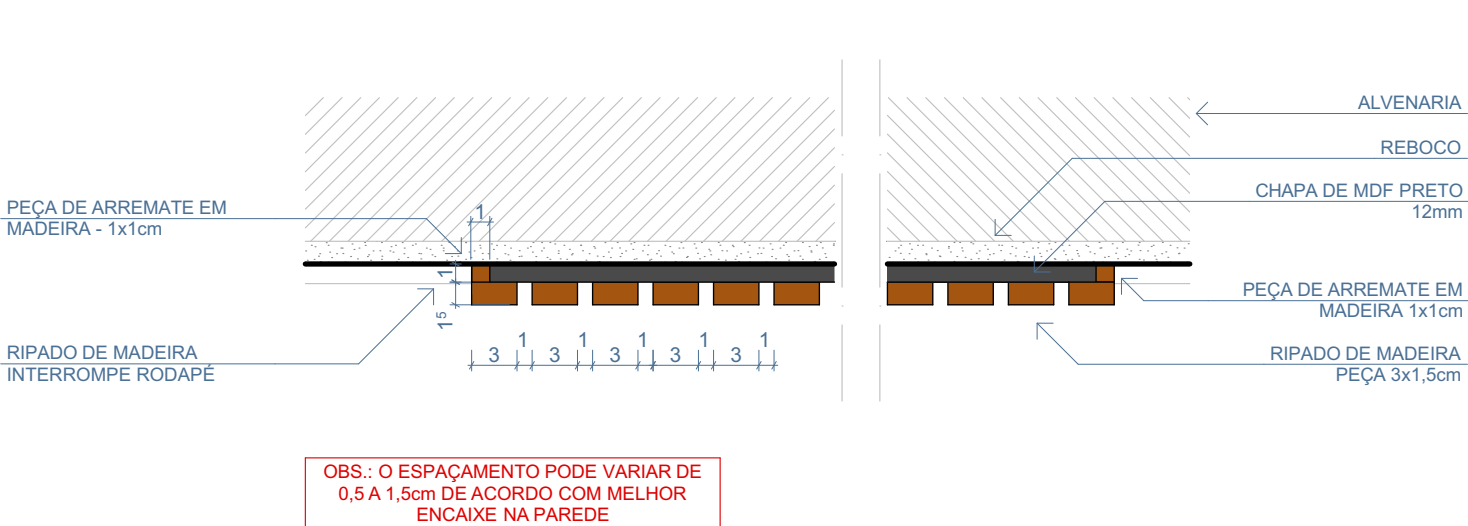


PLANTA BAIXA

MC12 | DETALHE QUINAS DO RIPADO


RIPADO DE MADEIRA MACIÇA SOBRE PAINEL DE MDF PRETO RESISTENTE À UMIDADE (ULTRA)

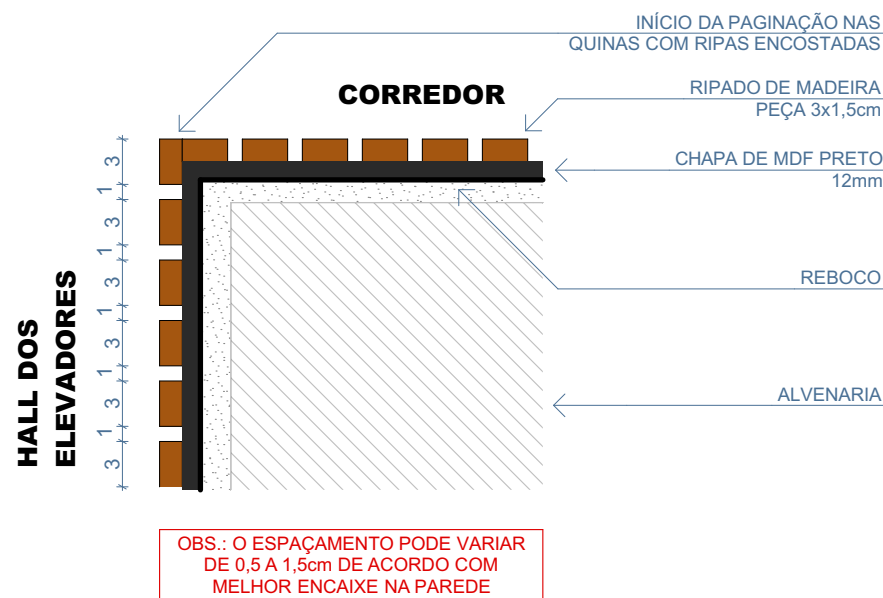


PLANTA BAIXA

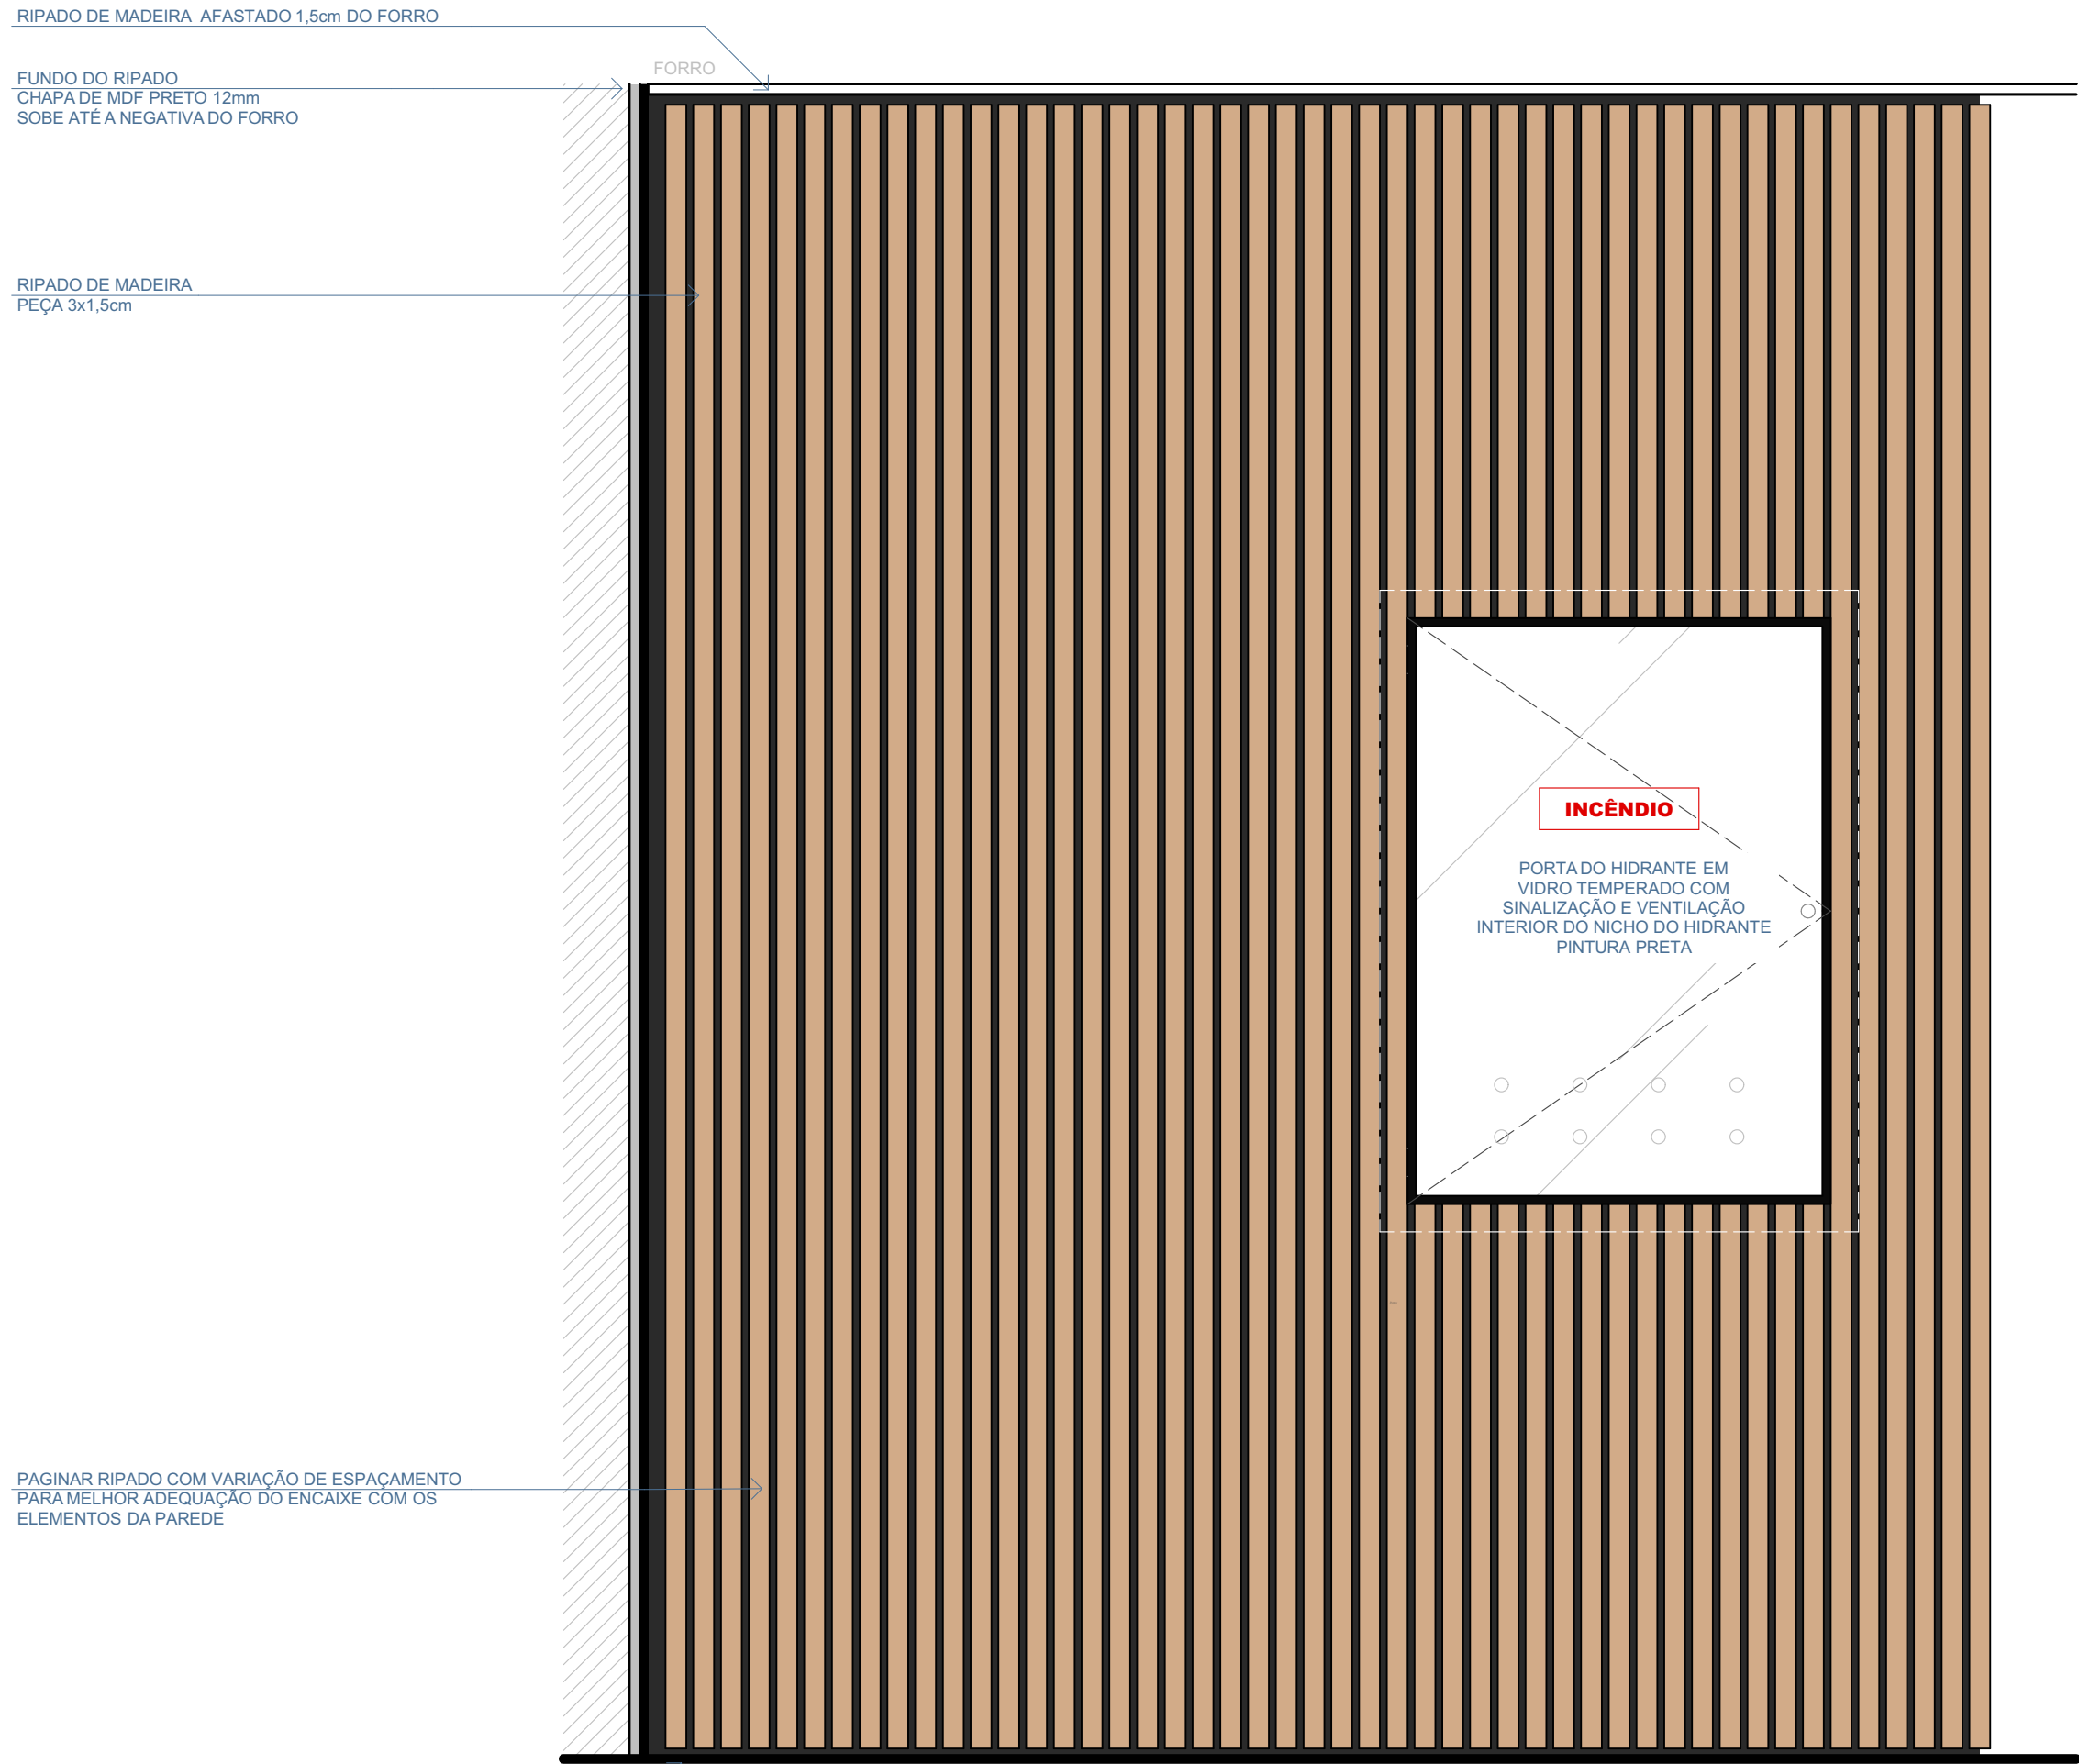

VISTA FRONTAL

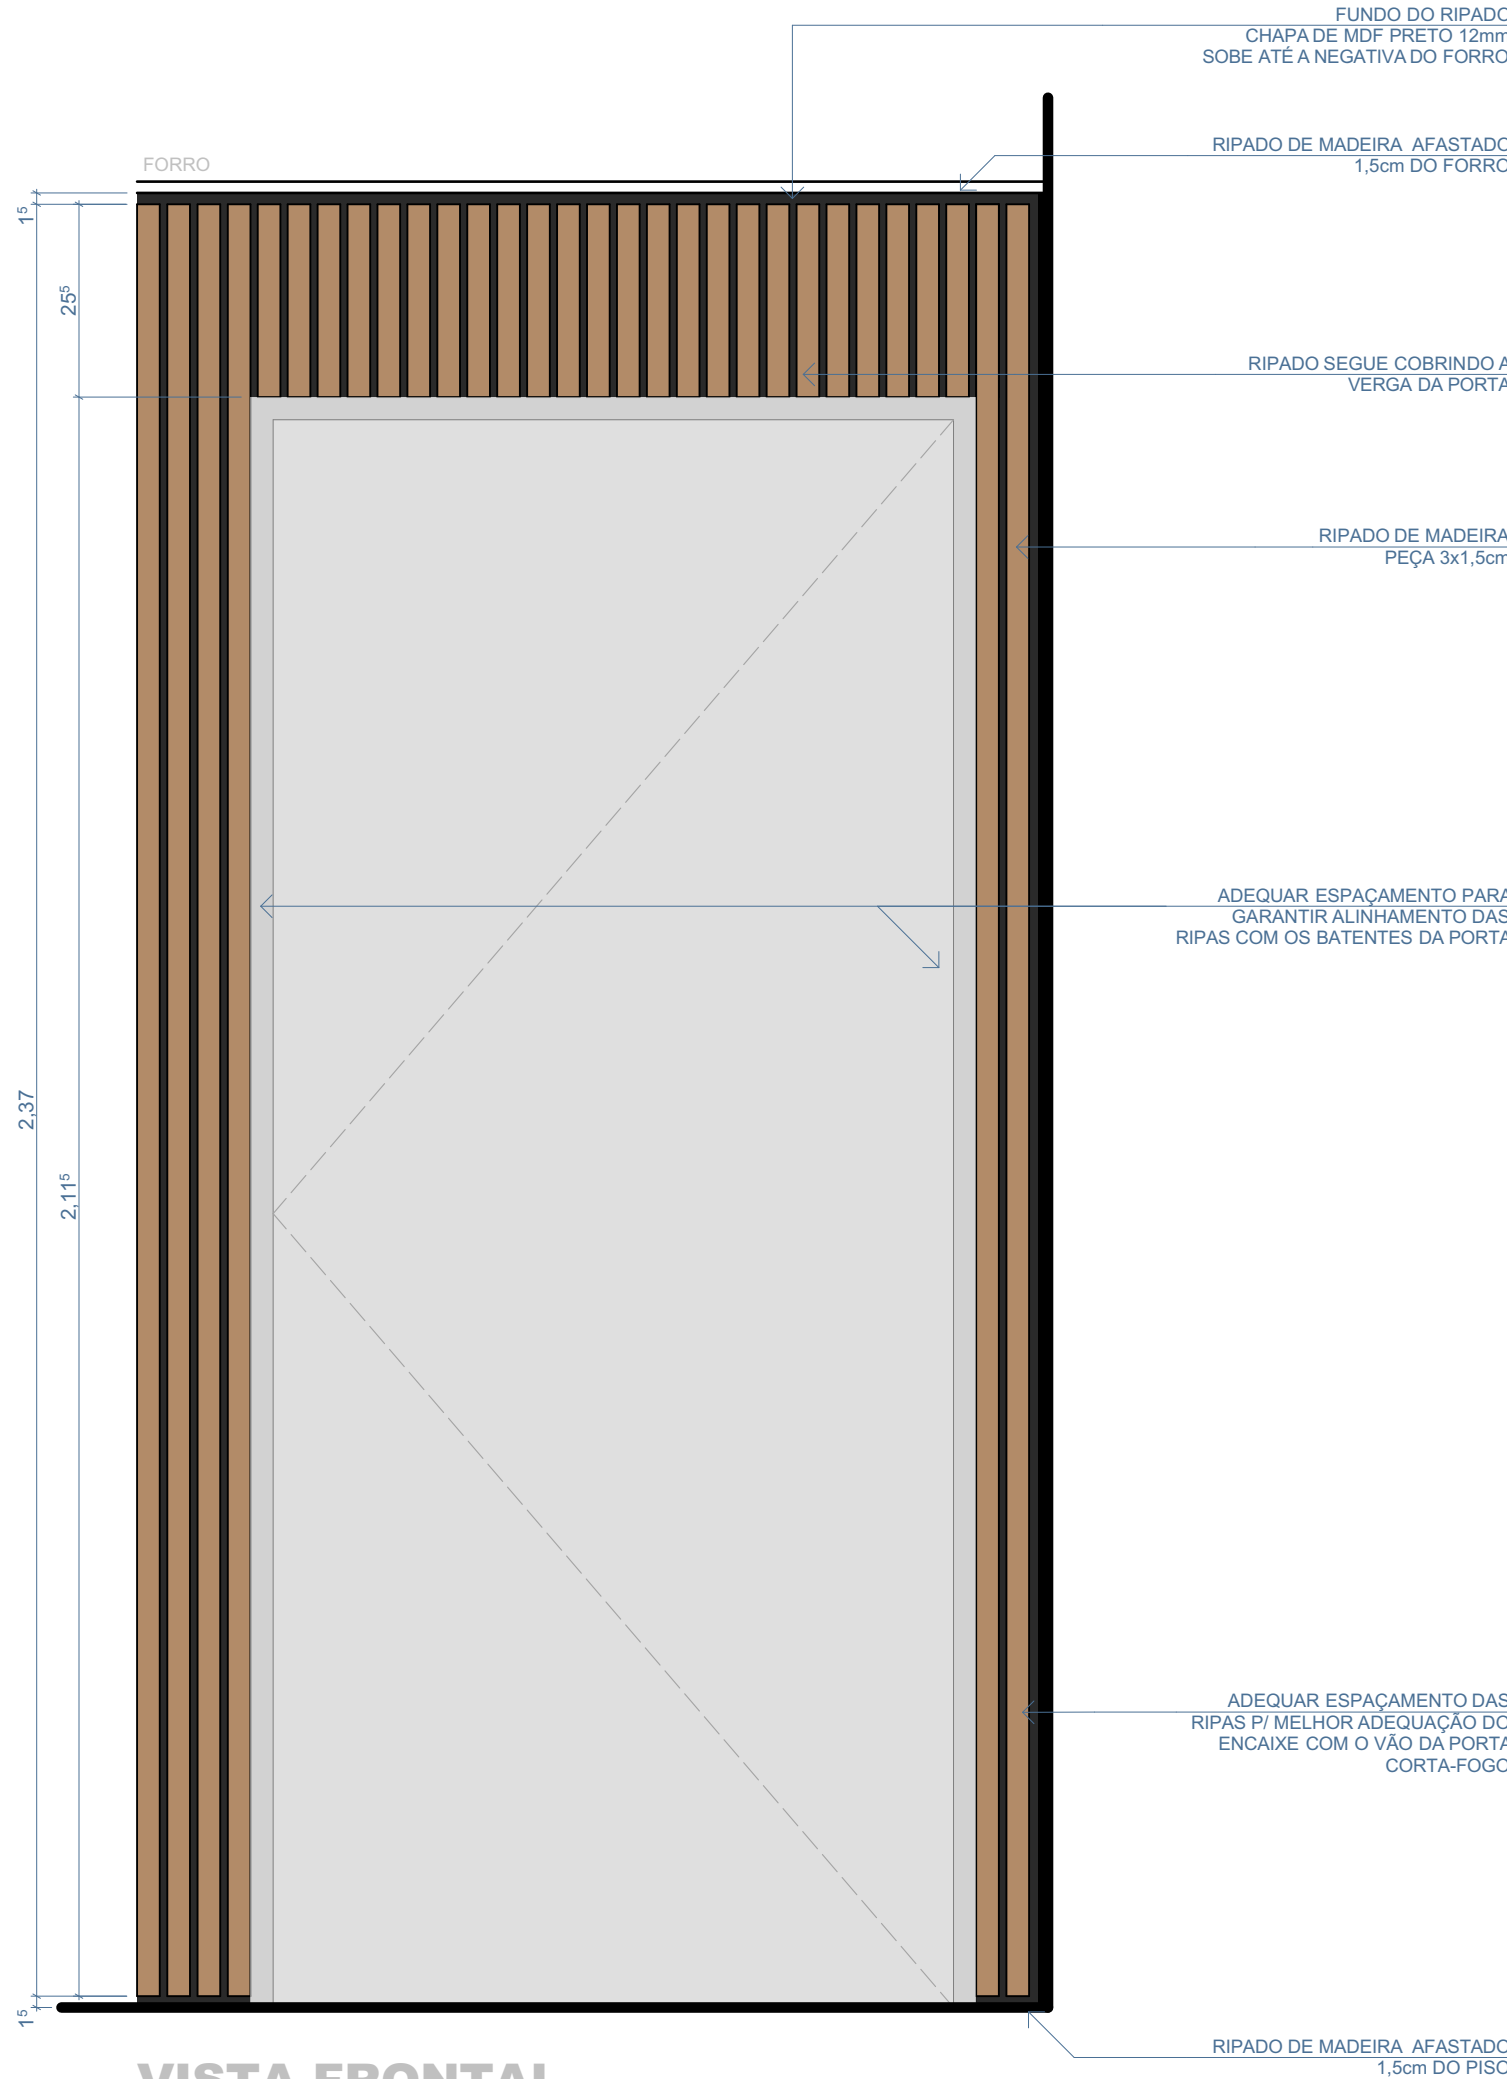

VISTA FRONTAL

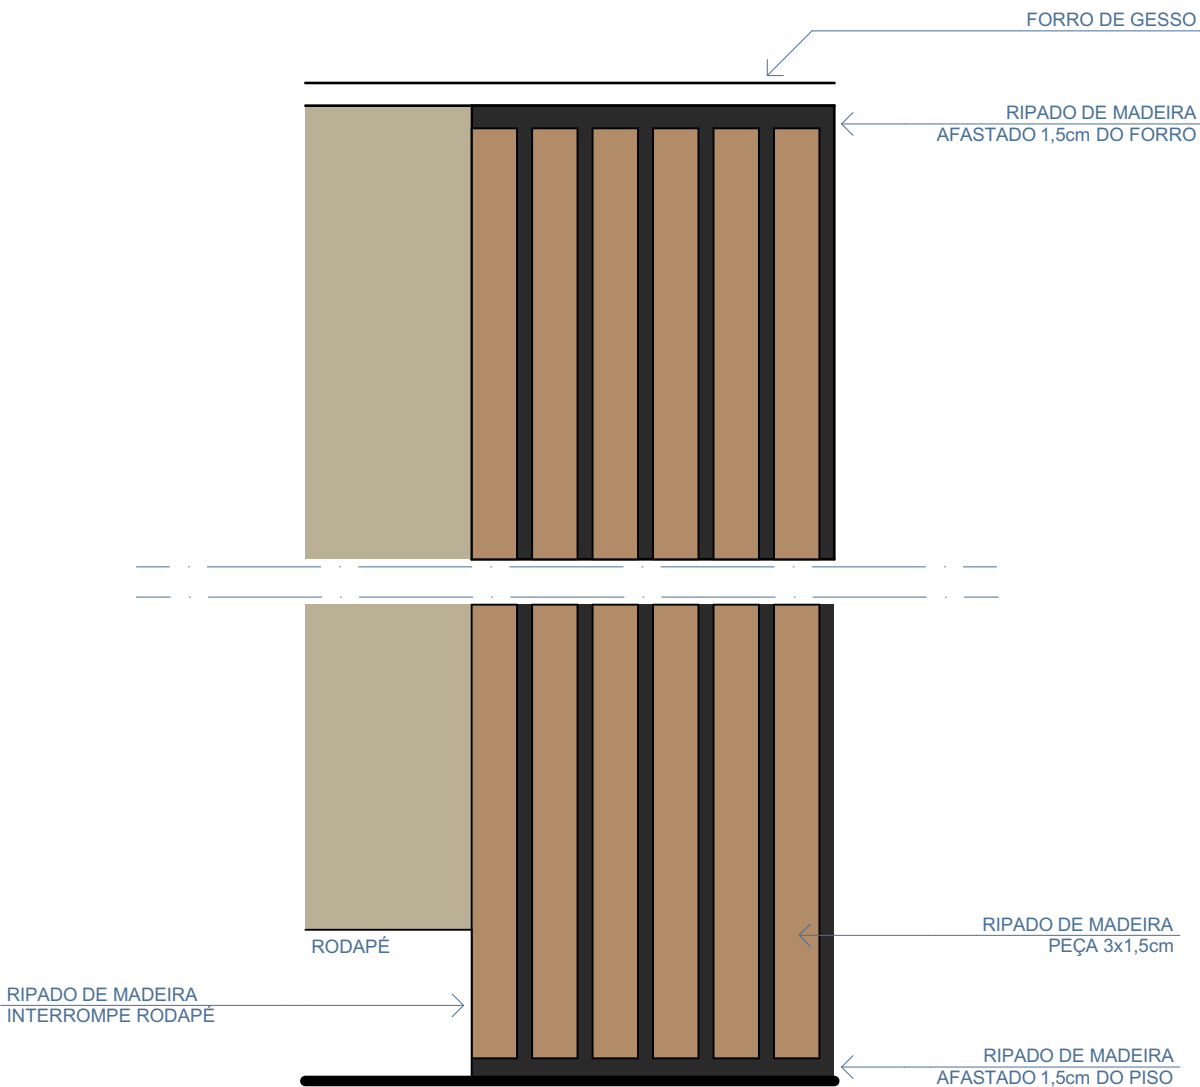

VISTA FRONTAL

PROJETO ARQUITETÔNICO

MAUI
INTERIORES DETALHAMENTO - MARCENARIA -
RIPADOS PAV.TIPO

ETAPA	OUZ MAUI_ARQ_PROJETO EXECUTIVO DETALHAMENTOS	A1 EST.
DATA	AMBIENTAÇÃO 13/03/2025	
ESCALA	1:25, 1:5, 1:10	
ENDEREÇO	Rodovia SC-406, s/n, Praia Mole, Florianópolis, Santa Catarina	
ASSINATURA:		
CLIENTE	OUZ CPF/CNPJ:	
ASSINATURA:		
RESPONSÁVEL:	HENRIQUE PIMONT CAU A 20832-9	
DESENHO:	MAYCON PASSIG; ARTHUR ANDRADE; MIRELA MOSER	