



MM01 | ACABAMENTO ELEVADOR SUBSOLO


PEÇAS EM TRAVERTINO ROMANO RÚSTICO
04 PEÇAS PARA 02 ELEVADORES

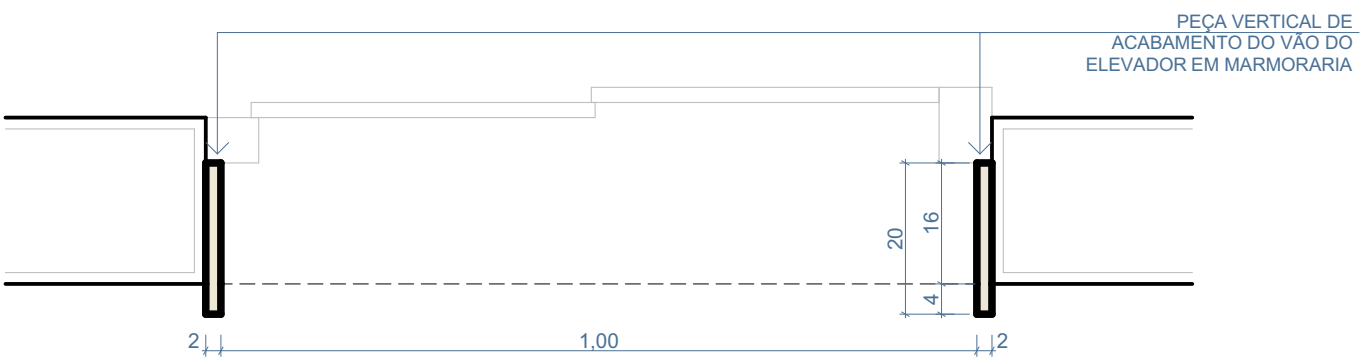

PLANTA BAIXA

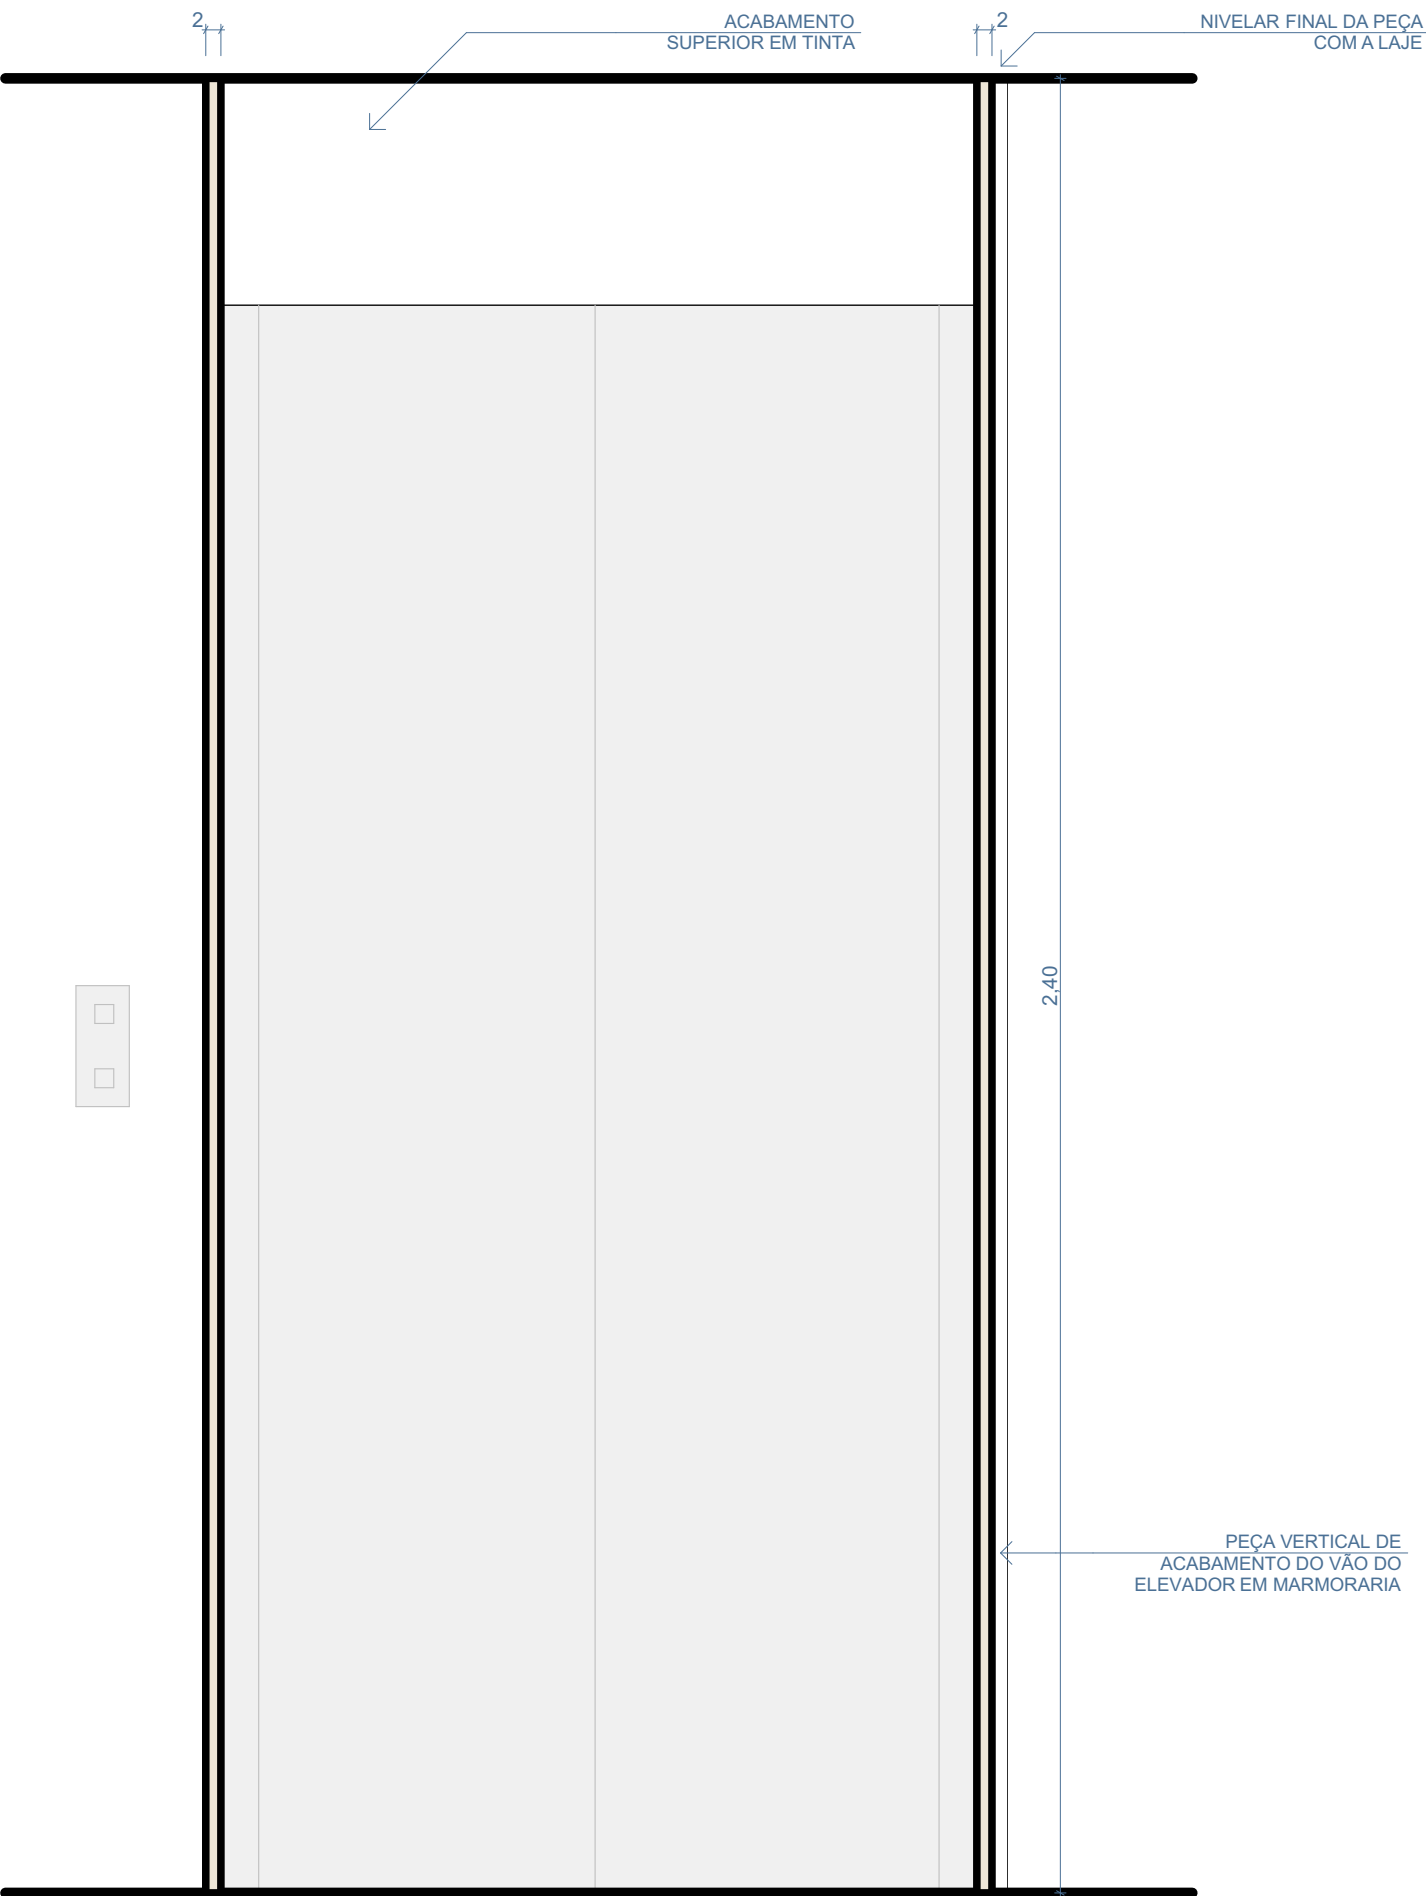


VISTA FRONTAL

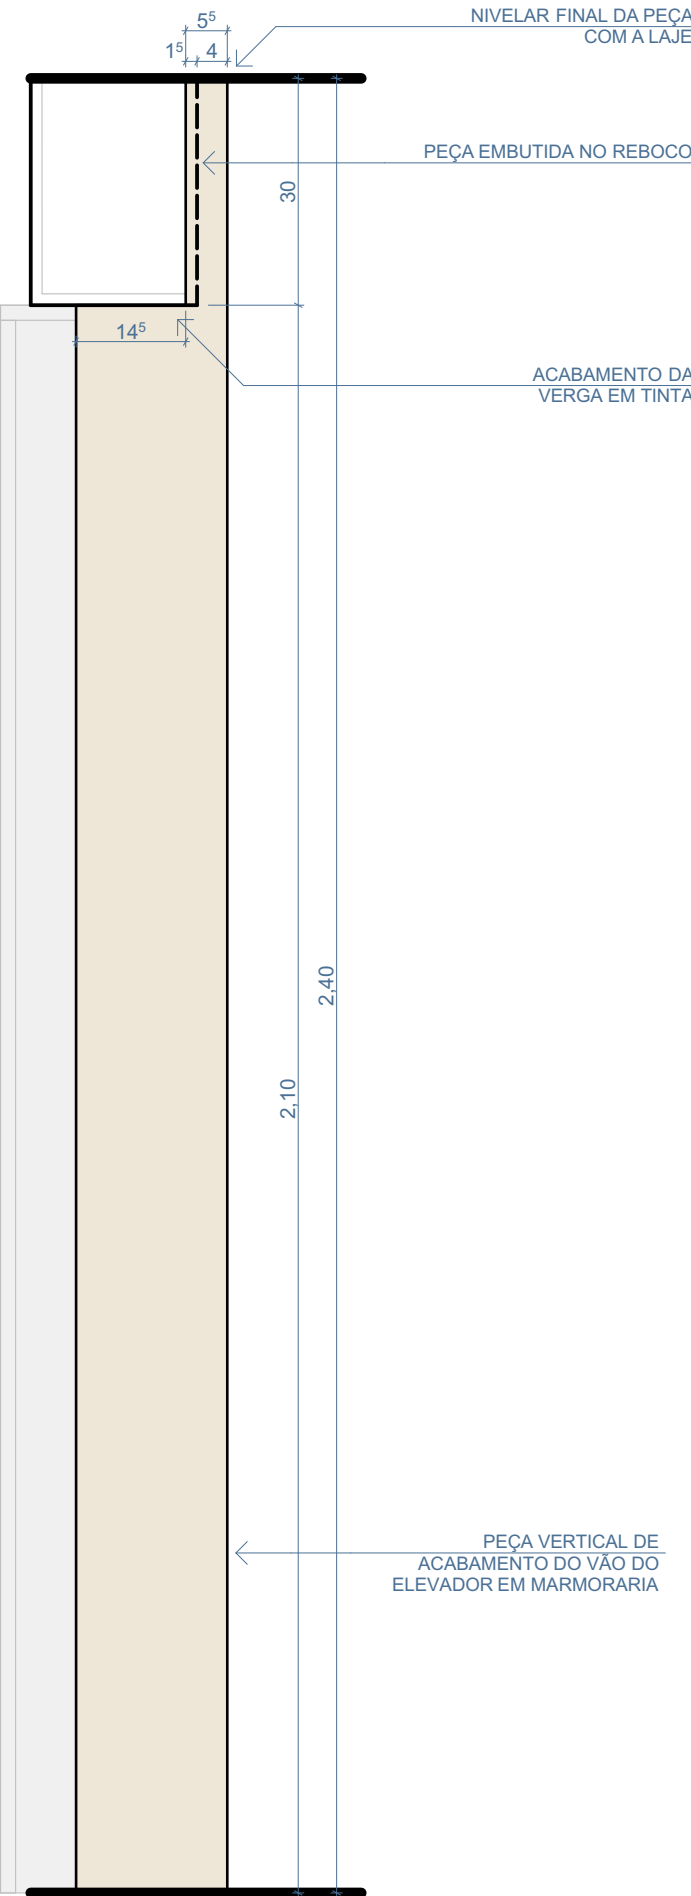


CORTE

MM02 | ACABAMENTO ELEVADOR ROOFTOP


PEÇAS EM TRAVERTINO ROMANO RÚSTICO
04 PEÇAS VERTICAIS PARA 02 ELEVADORES

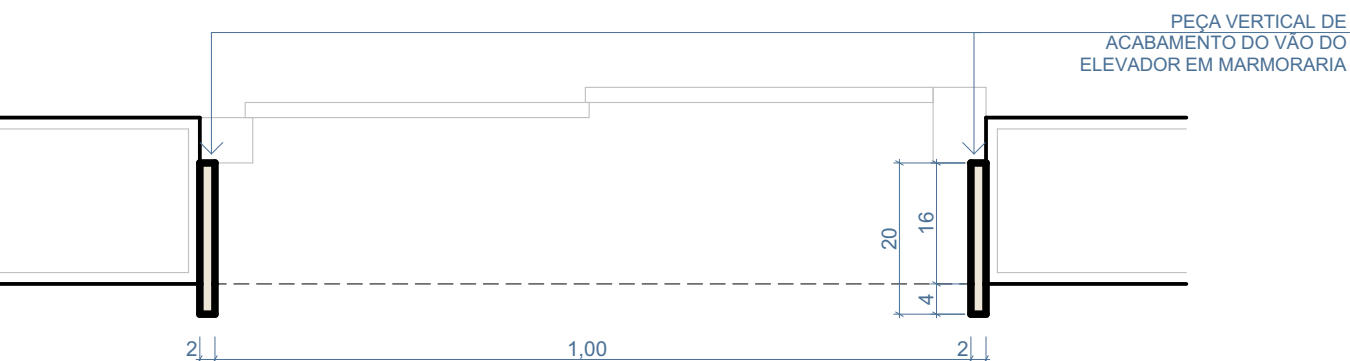

PLANTA BAIXA

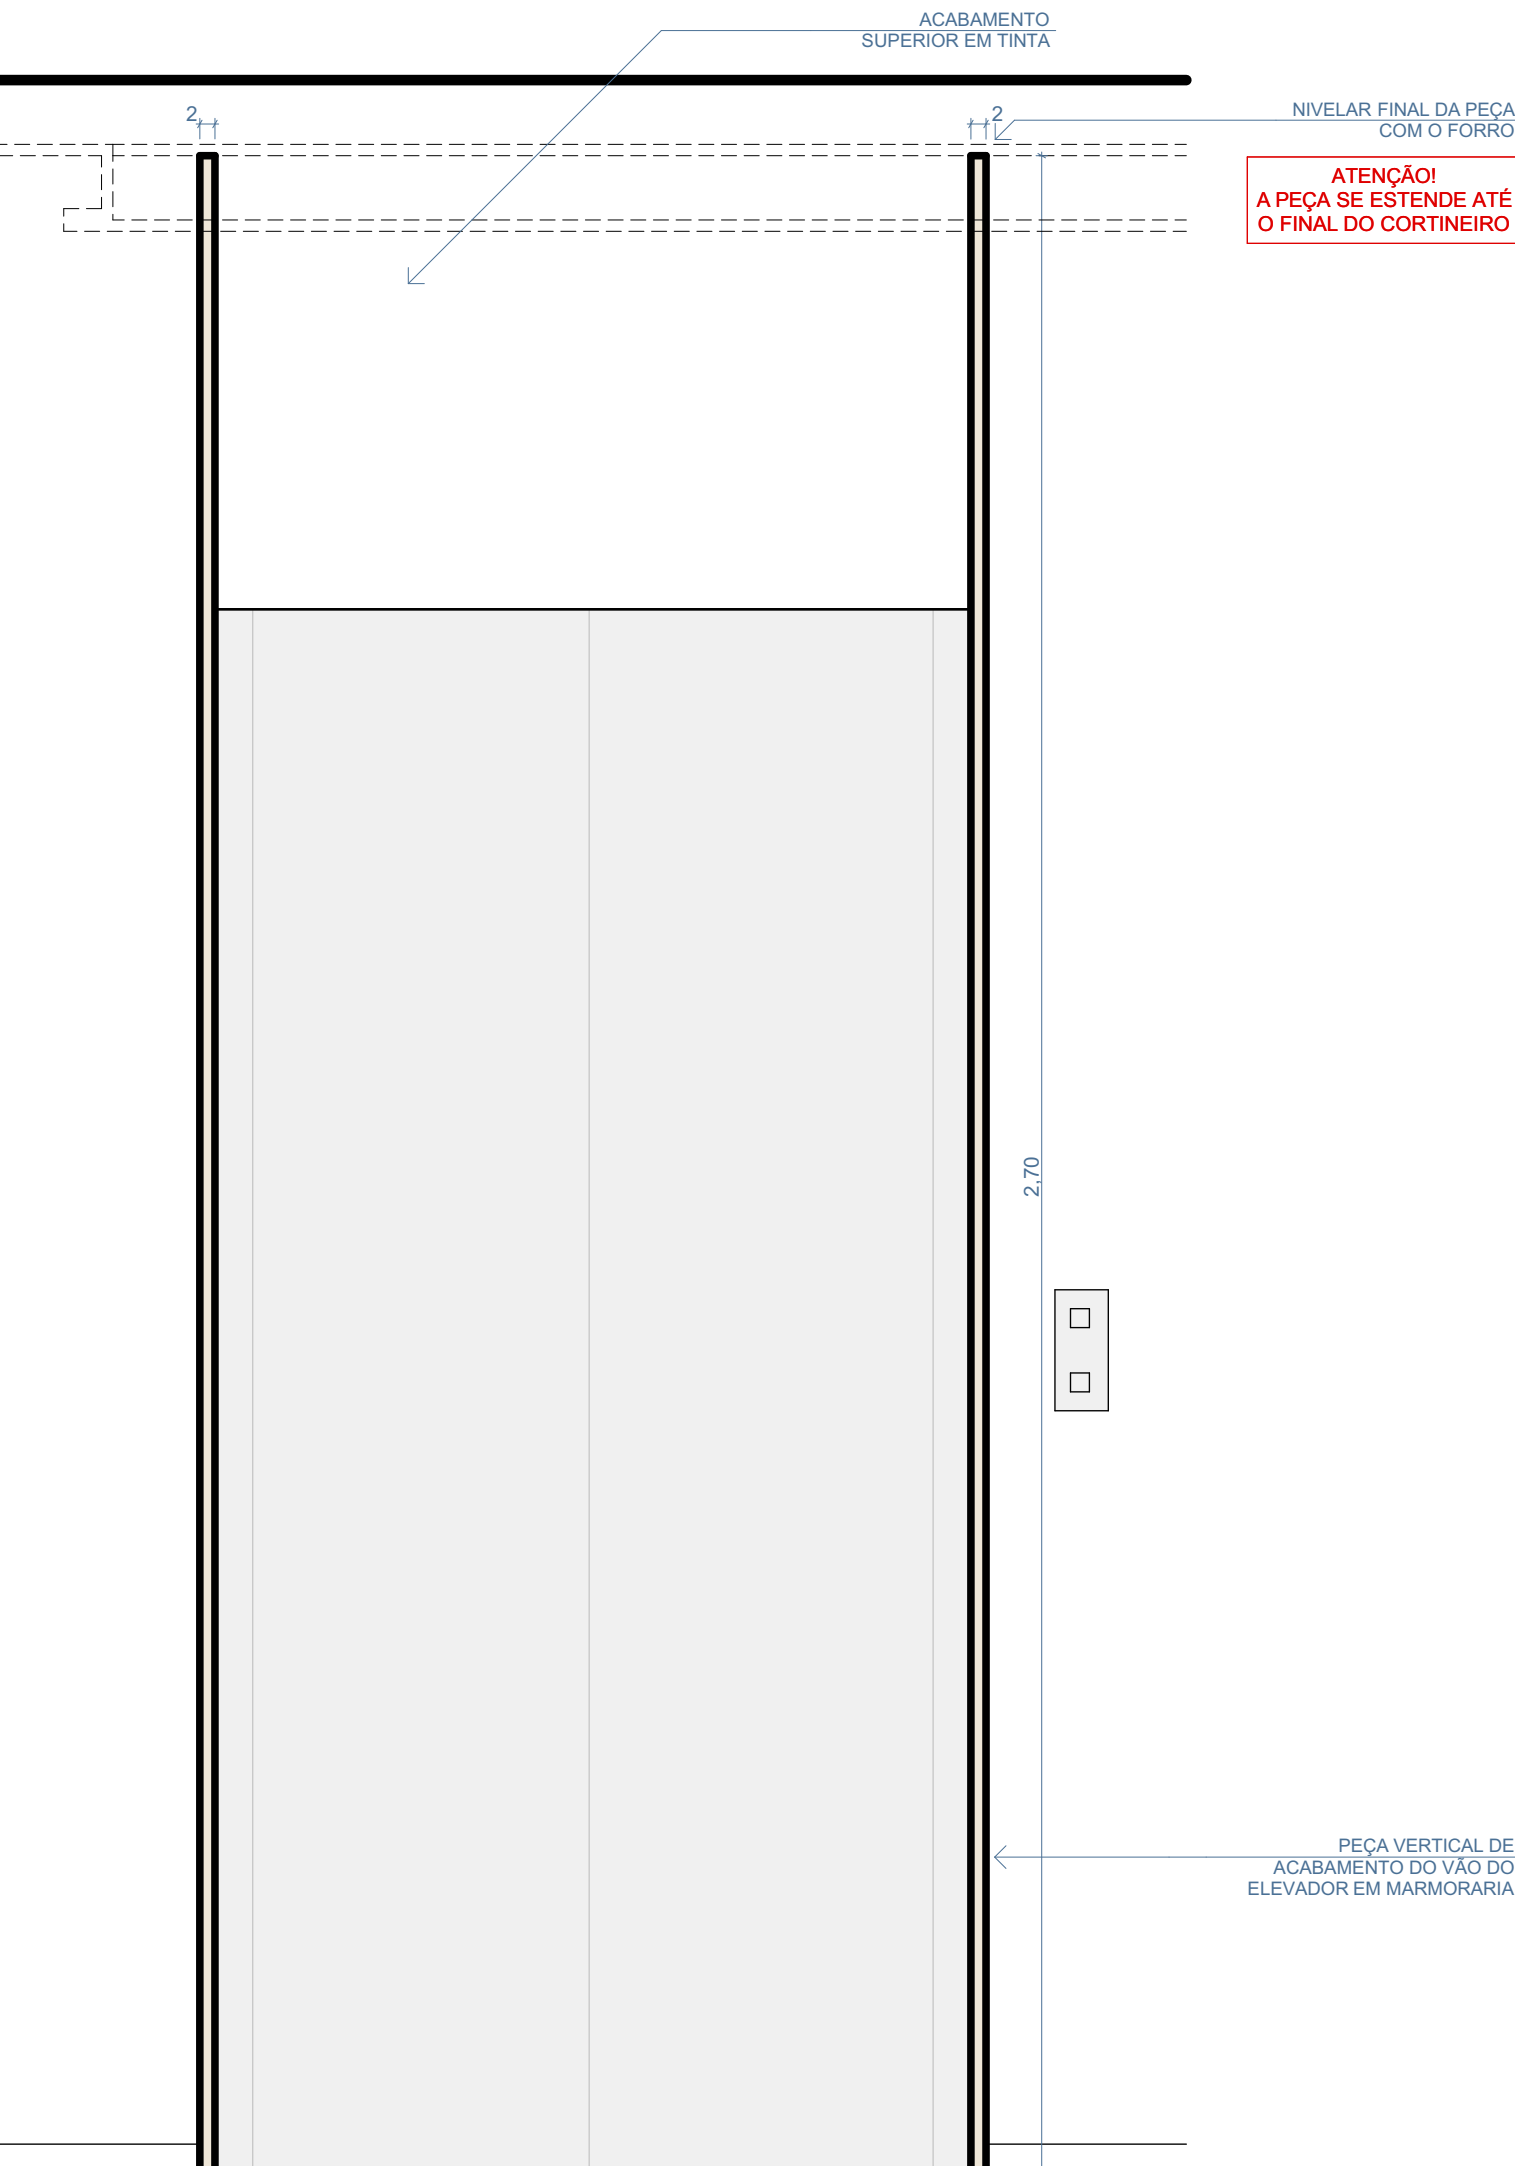

VISTA FRONTAL

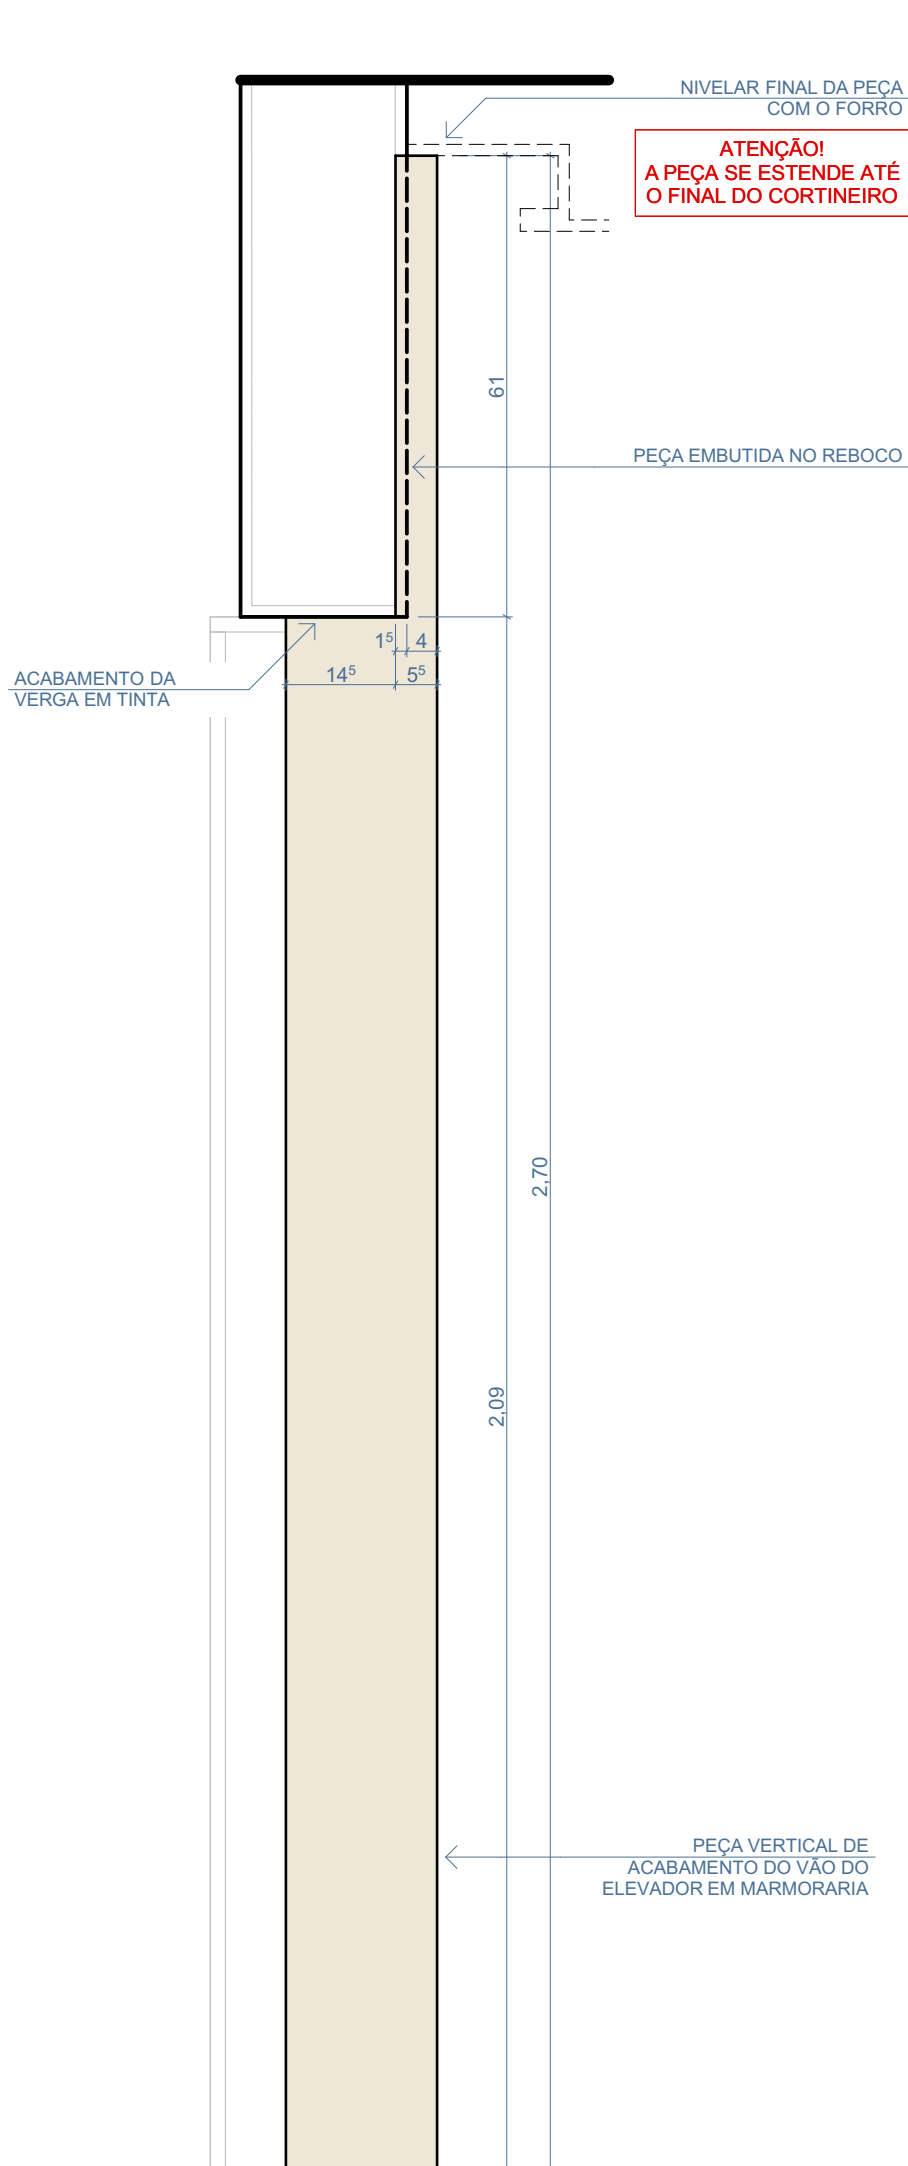

CORTE

PROJETO ARQUITETÔNICO

MAUI
INTERIORES DETALHAMENTO - MARMORARIA -
ELEVADOR SUBSOLO E ELEVADOR ROOFTOP

ETAPA	OUZ, MAUI, ARQ, PROJETO EXECUTIVO DETALHAMENTOS	A1 EST.
DATA	AMBIENTAÇÃO 13/03/2025	
ESCALA	1:10	
ENDEREÇO	Rodovia SC-406, s/n, Praia Mole, Florianópolis, Santa Catarina	
ASSINATURA:		
CLIENTE	OUZ CPF/CNPJ:	
ASSINATURA:		
RESPONSÁVEL:	HENRIQUE PIMONT CAU A 20832-9	
DESENHO:	MAYCON PASSIG; ARTHUR ANDRADE; MIRELA MOSER	