
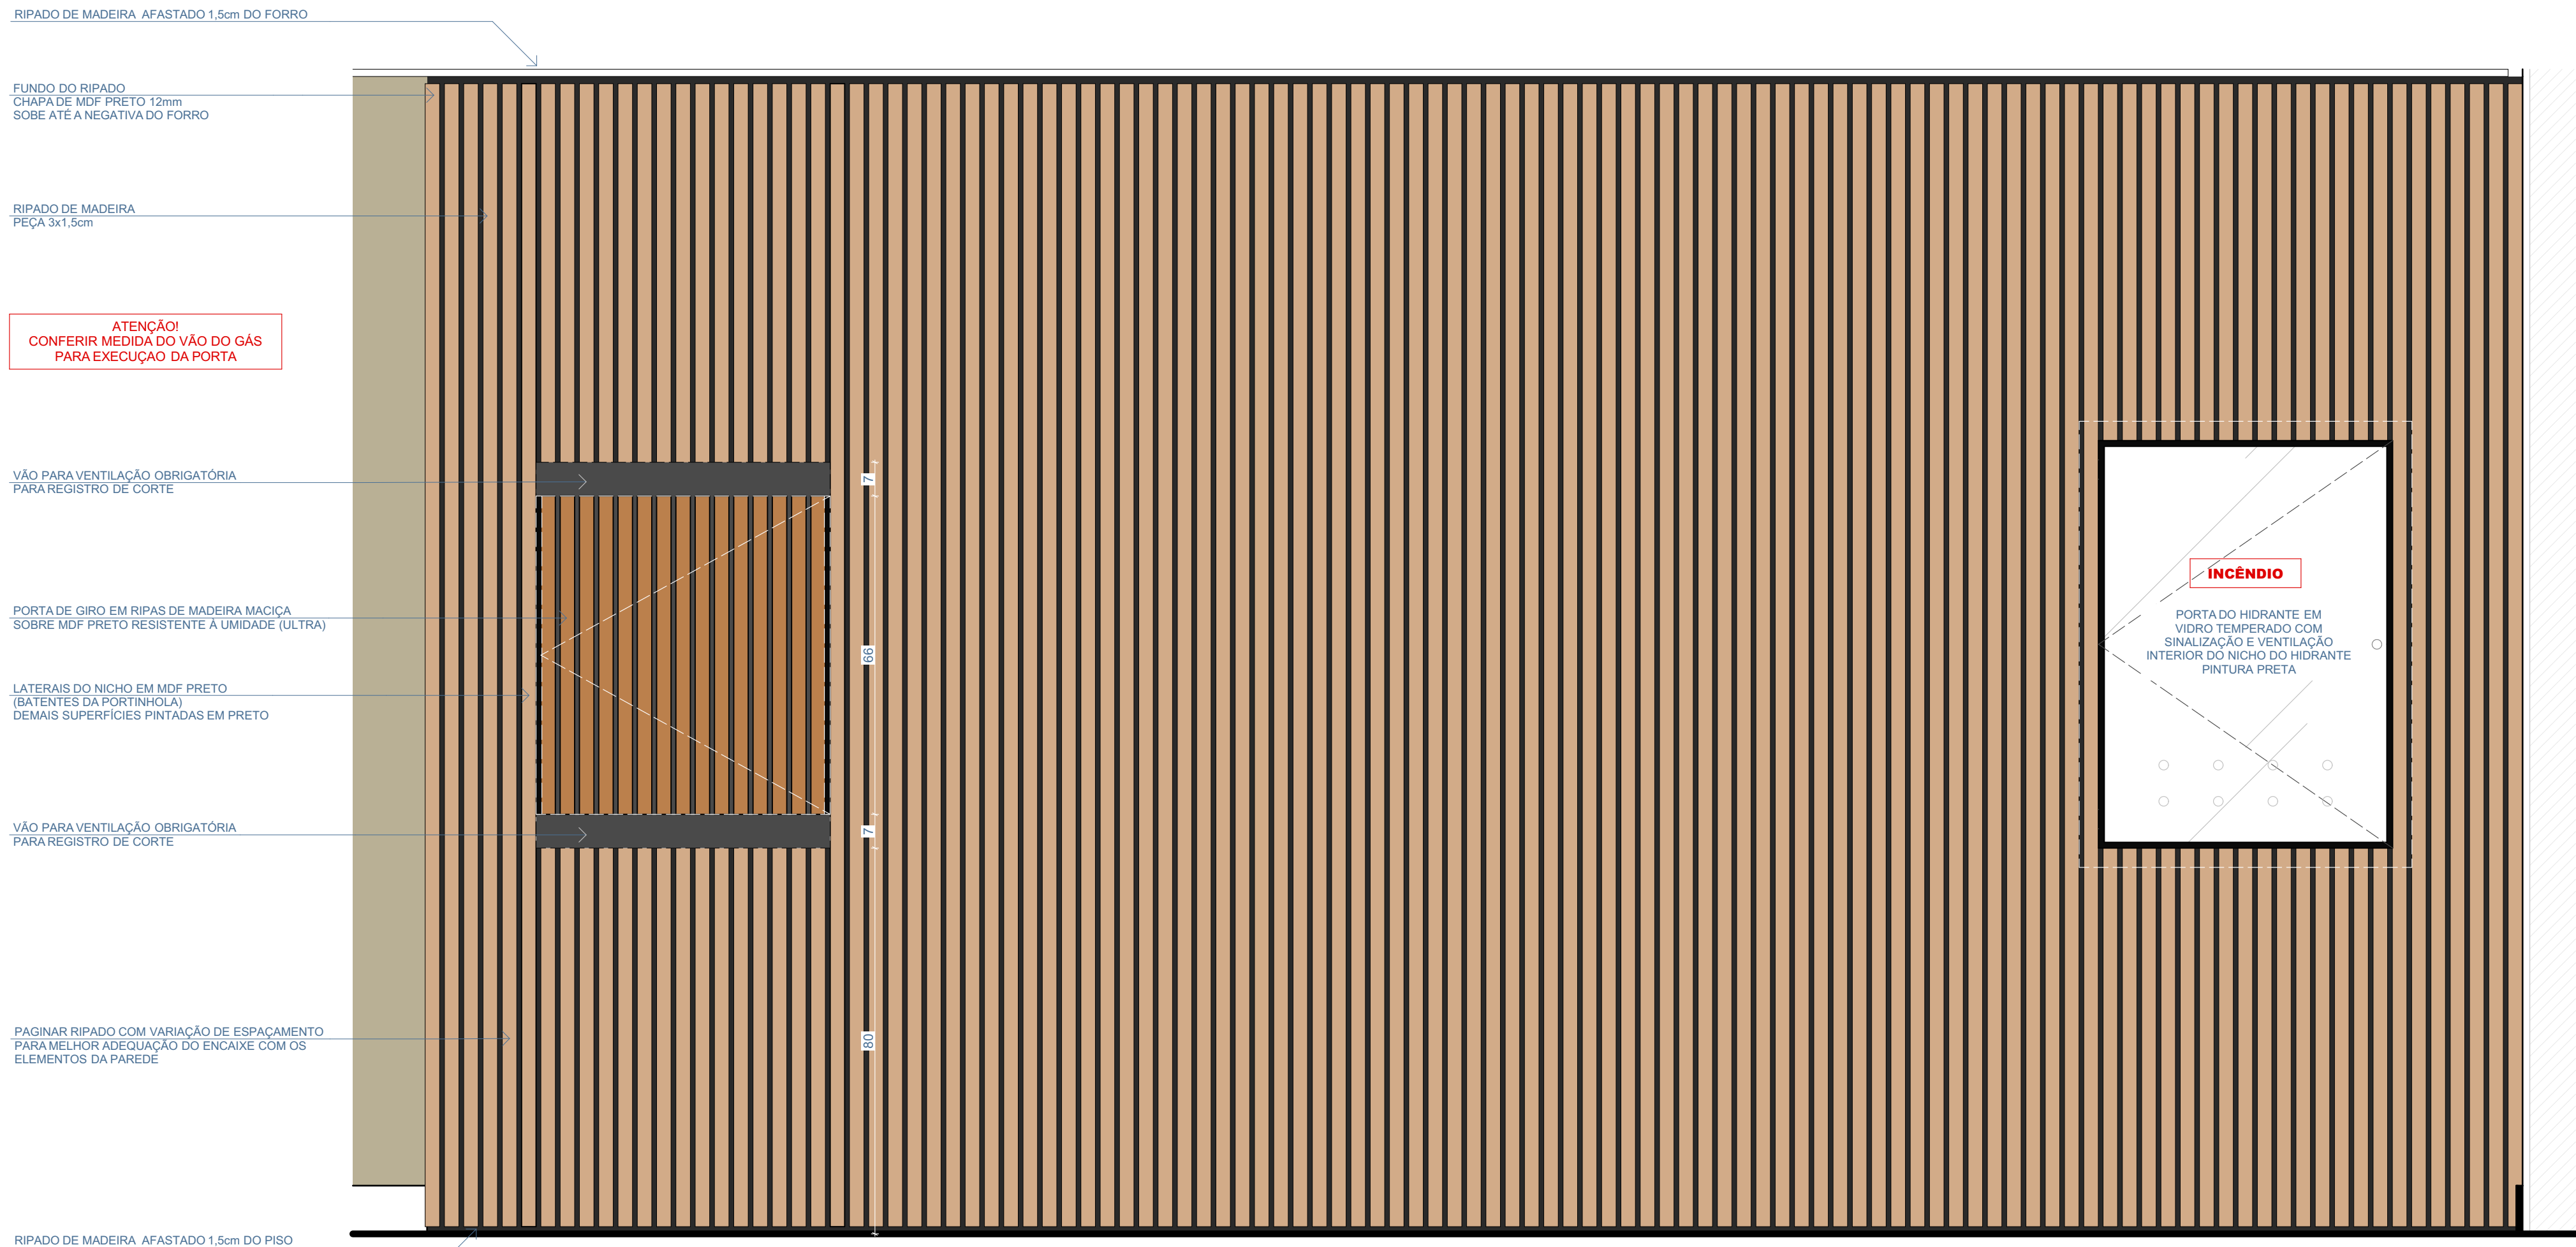



MC19 | RECORTE DO HIDRANTE E REGISTRO DE CORTE DO GÁS

RIPADO DE MADEIRA MACIÇA SOBRE PAINEL DE MDF PRETO RESISTENTE À UMIDADE (ULTRA)
PORTA DE VIDRO DO HIDRANTE SEGUINDO A NORMA DOS BOMBEIROS EM DIMENSÃO E VENTILAÇÃO
02 UNIDADES

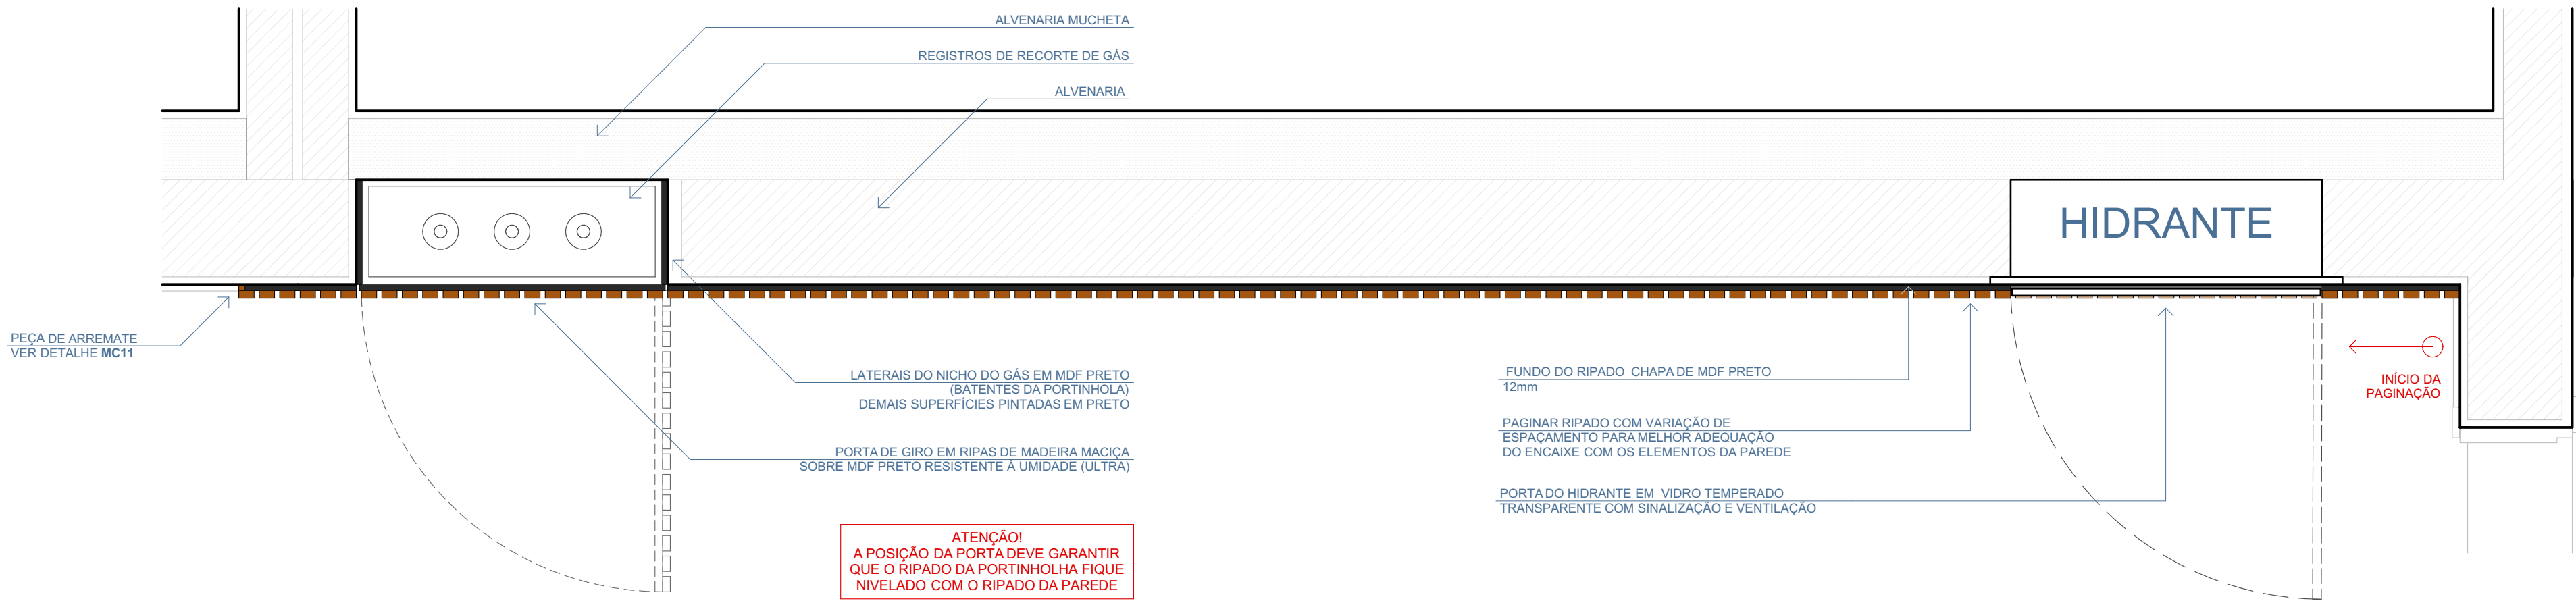


MC11 | DETALHE DO PAINEL RIPADO

RIPADO DE MADEIRA MACIÇA SOBRE PAINEL DE MDF PRETO RESISTENTE À UMIDADE (ULTRA)

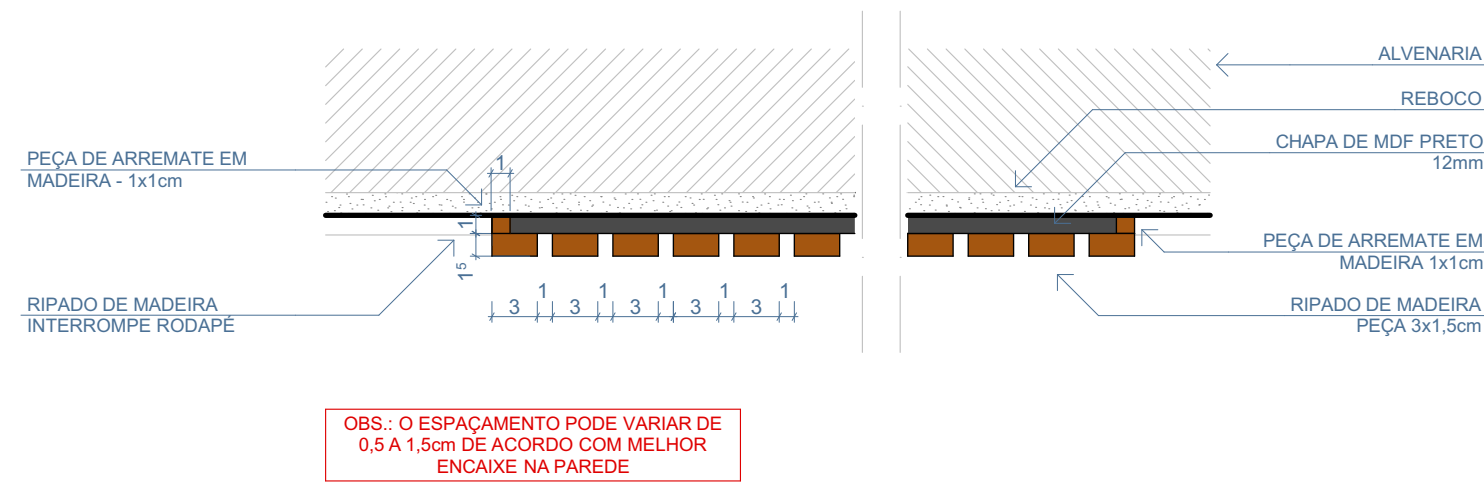

PLANTA BAIXA

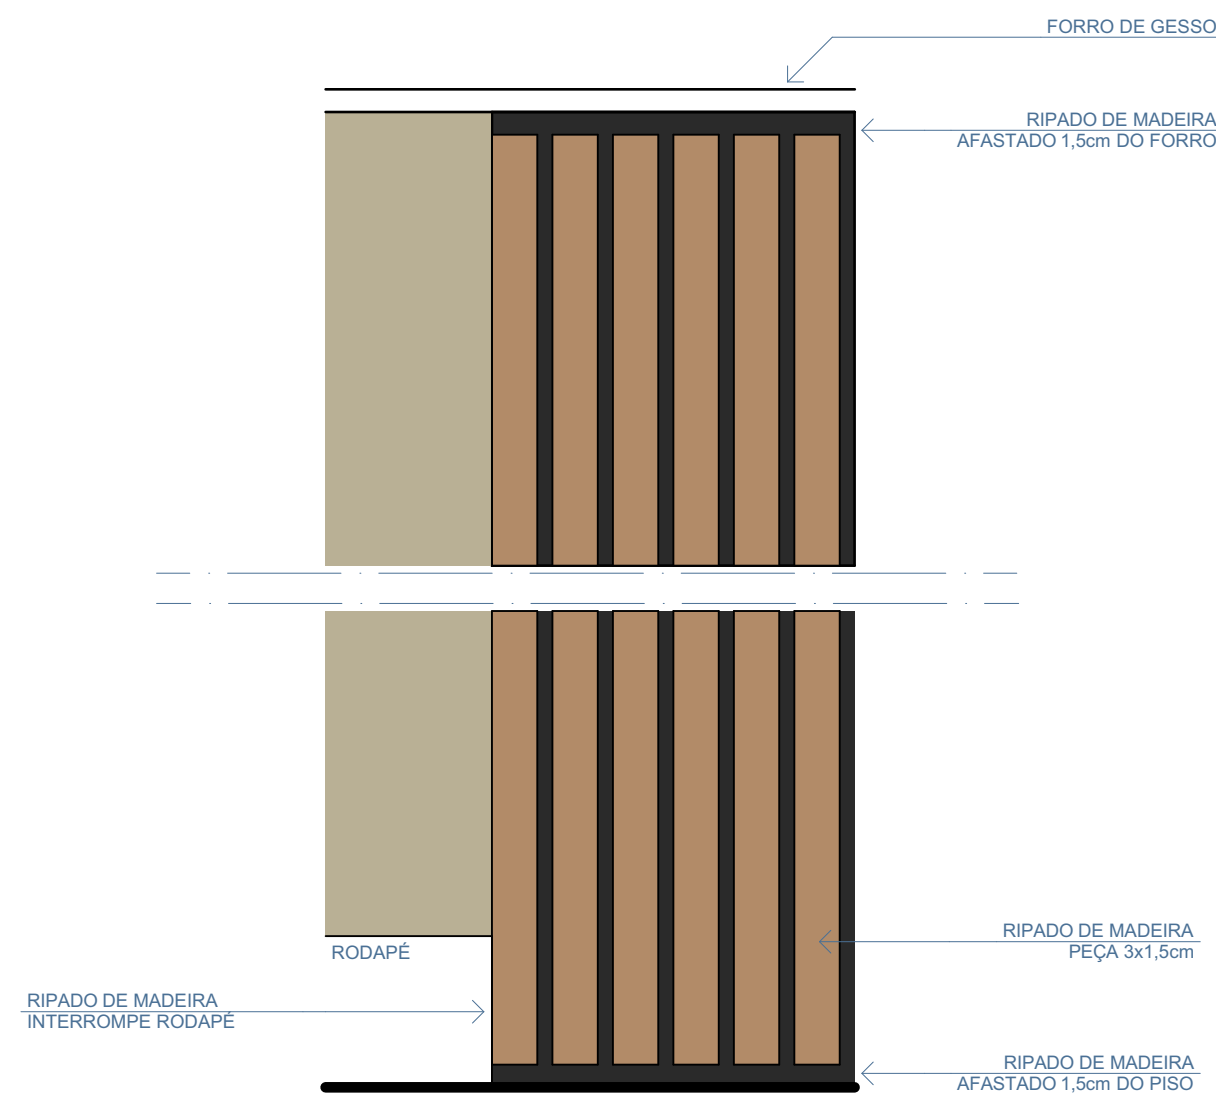

VISTA FRONTAL

PROJETO ARQUITETÔNICO

MAUI
INTERIORES DETALHAMENTO - MARCENARIA -
RIPADOS PAV. TIPO

ETAPA	OUZ_MAUI_ARQ_PROJETO EXECUTIVO DETALHAMENTOS AMBIENTAÇÃO	A1
DATA	13/03/2025	
ESCALA	1:10, 1:5	
ENDEREÇO	Rodovia SC-406, s/n, Praia Mole, Florianópolis, Santa Catarina	
ASSINATURA:		
CLIENTE	OUZ	
	CPF/CNPJ:	
ASSINATURA:		
RESPONSÁVEL:	HENRIQUE PIMONT	
	CAU A 20832-9	
DESENHO:	MAYCON PASSIG; ARTHUR ANDRADE; MIRELA MOSER	