


ROOFTOP - OFURÔ

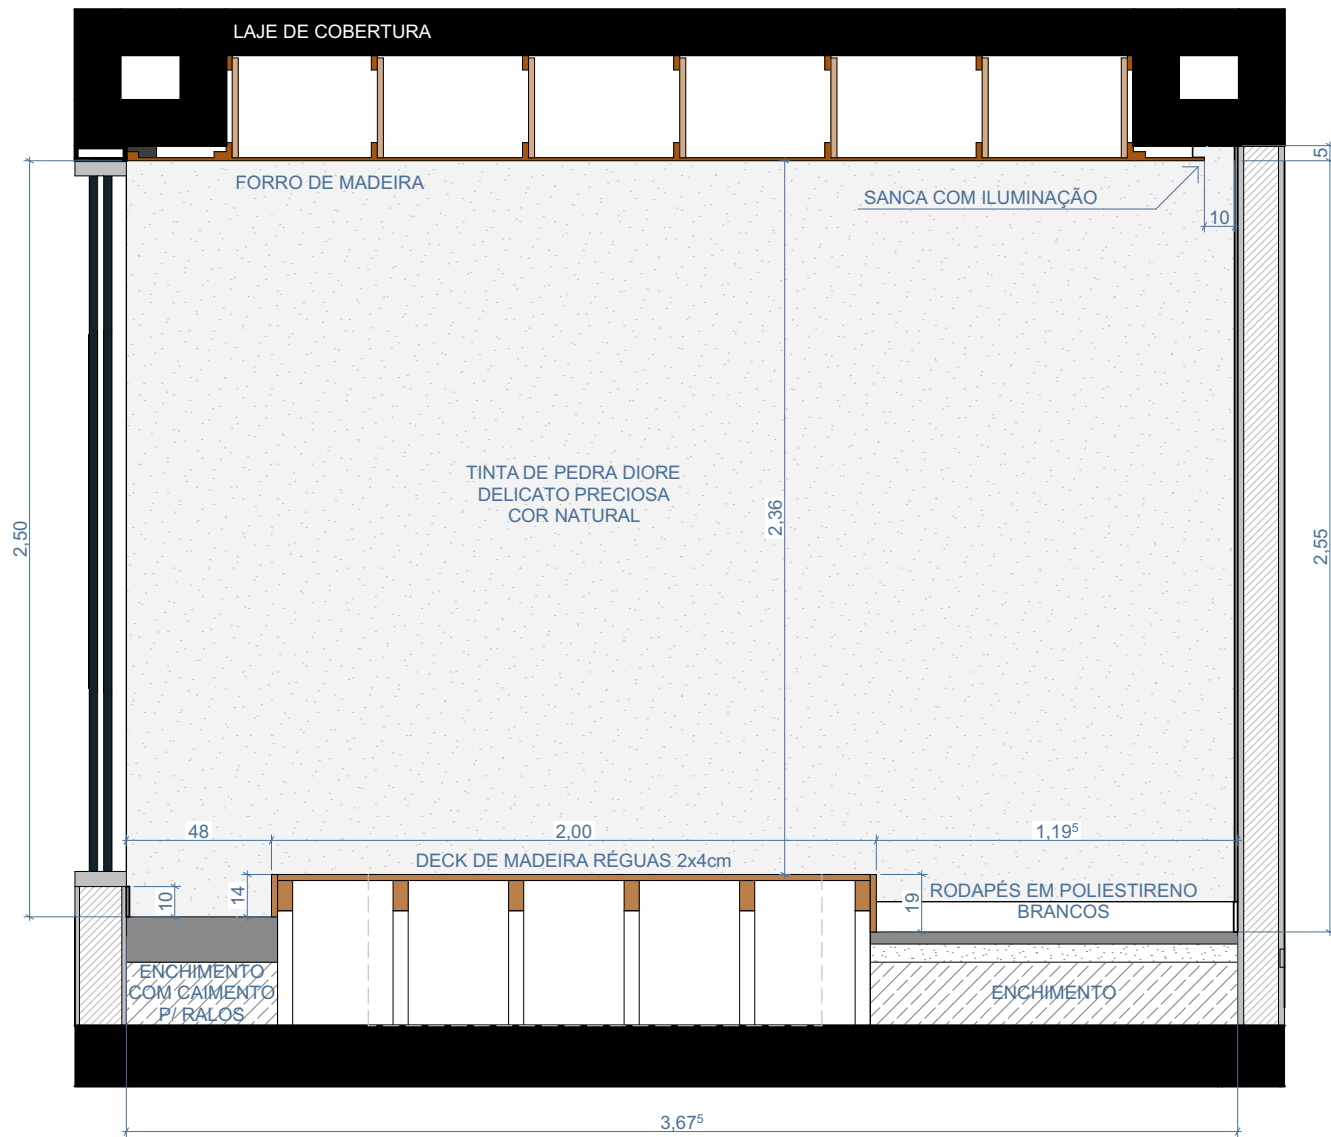


01
ESCALA 1:25




02
ESCALA 1:25



03
ESCALA 1:25

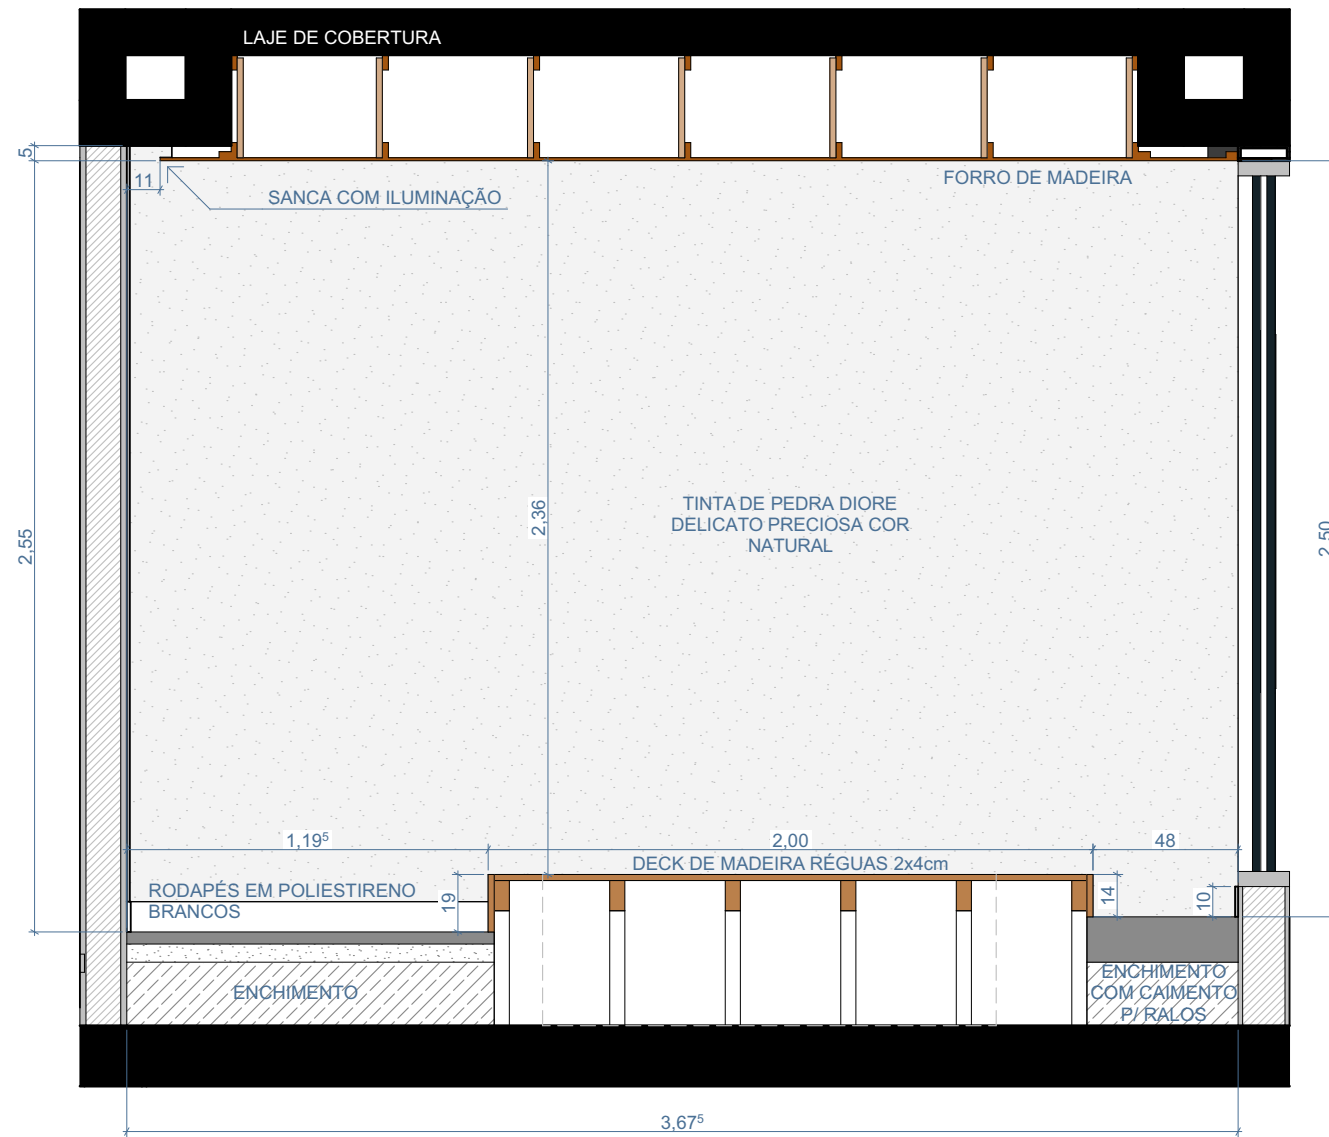

04
ESCALA 1:25

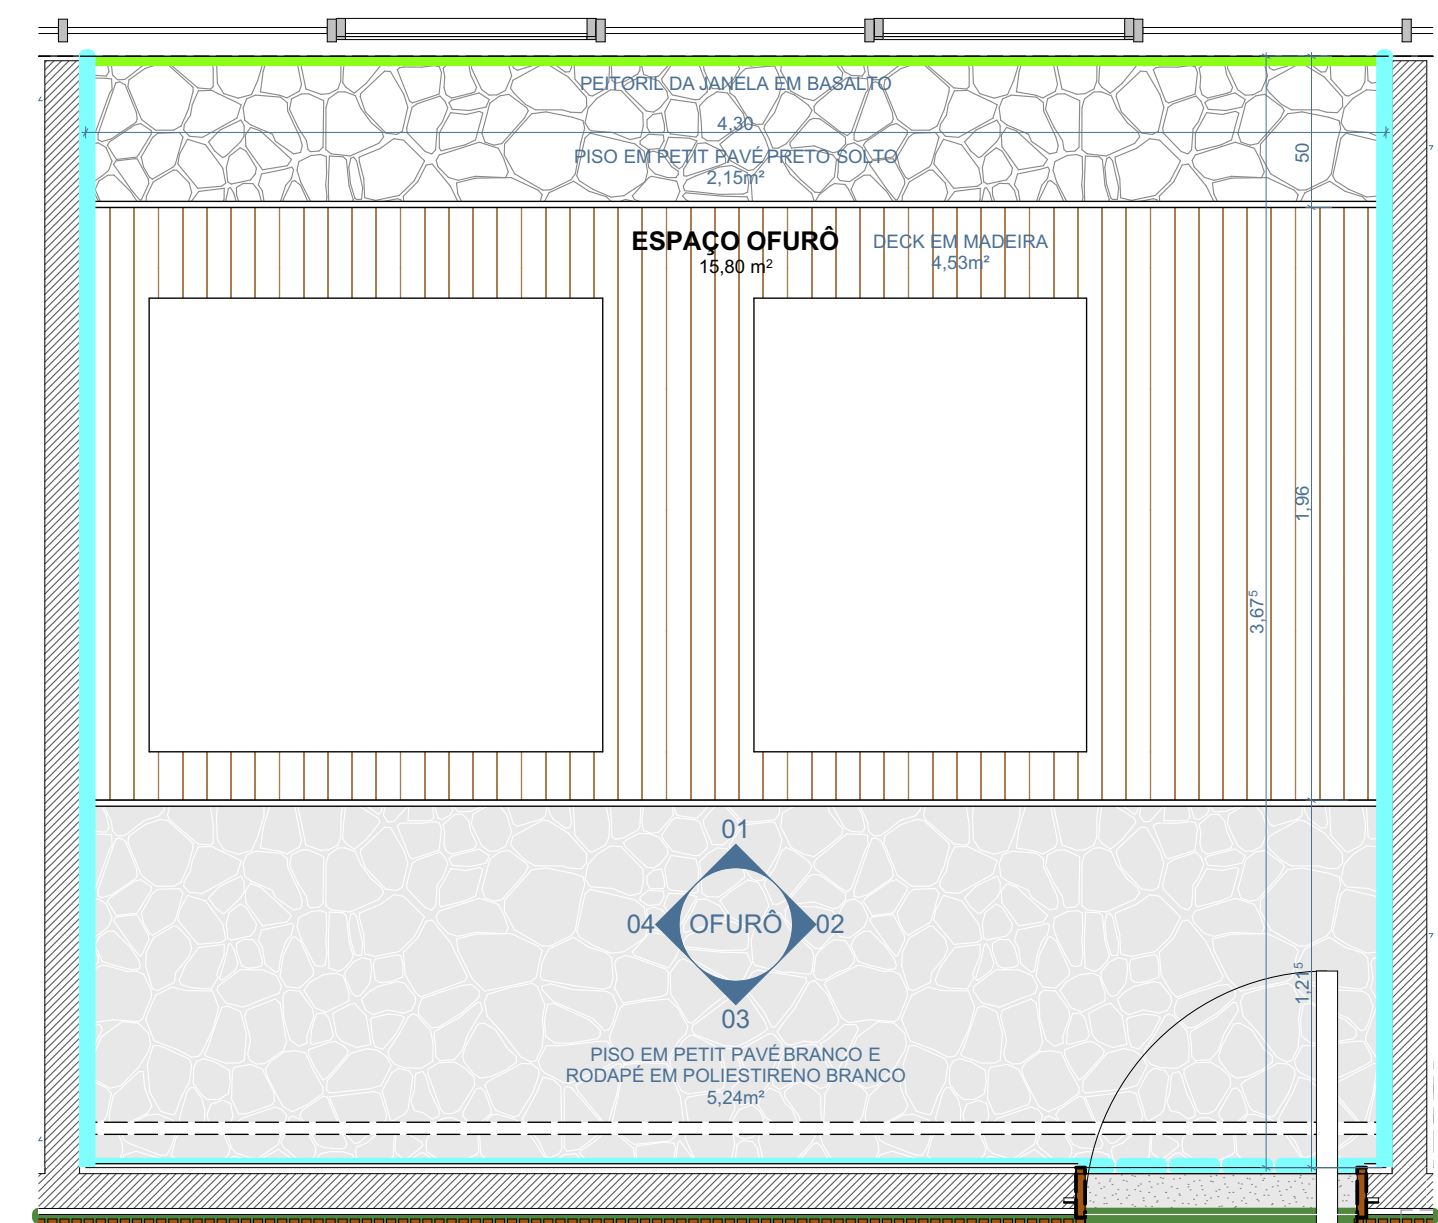

PLANTA BAIXA
ESCALA 1:25



VISTA DOS AMBIENTES



PLANTA BAIXA
ESCALA 1:25

LEGENDA REVESTIMENTOS

	PLACA DE CONCRETO 50x50		AZULEJO 30x60 BRANCO ACETINADO RETIFICADO
	PETIT PAVÉ BRANCO		TINTA DE PEDRA DIORE DELICATO PRECIOSA COR NATURAL
	PETIT PAVÉ PRETO		TINTA DE PEDRA DIORE ORNAMENTAL MAXI COR BEGE ARACEMA
	CIMENTO ALISADO		TEXTURA TERRACOR PREDIAL PRETO
	CONCRETO VASSOURADO		PINTURA ACRÍLICA PRETA - SUVINIL PATATIVA
	PORCELANATO 60x120		BASALTO POLIDO
	PORCELANATO 60x60		REVESTIMENTO EM PEDRA NATURAL MOLEDO
	PORCELANATO 90x90		REVESTIMENTO EM LÂMINA FREIJÓ
	PISO DE MADEIRA		COMPENSADO VIROLA
	DECK DE MADEIRA		ESPELHO CRISTAL COLADO
	PISO ESPORTIVO EMBORRACHADO EM PLACAS 100x100		
	BASALTO RÚSTICO		
	BASALTO POLIDO		
	PISO CIMENTÍCIO SOLARIUM 50x50		

NOTAS

1. PILARES DA GARAGEM E MURETAS DO ACESSO SÃO EM CONCRETO APARENTE.
2. PAREDES INTERNAS SEM INDICAÇÃO DE REVESTIMENTO RECEBERÃO PINTURA ACRÍLICA COR BRANCO FOSCO.
3. PAREDES EXTERNAS SEM INDICAÇÃO DE REVESTIMENTO RECEBERÃO PINTURA TERRACOR PREDIAL BRANCO.
4. SOLEIRAS DAS PORTAS DOS APARTAMENTOS EM PEÇA ÚNICA SEGUNDO ESPECIFICAÇÃO DO PISO DA CIRCULAÇÃO COMUM.

PROJETO ARQUITETÔNICO

MAUI
INTERIORES AMBIENTAÇÃO - RTOP OFURÔ / BEM ESTAR

13/18

ETAPA	OUZ_MAU_ARQ_PROJETO EXECUTIVO AMBIENTAÇÃO	A1 EST.
DATA	14/03/2025	
ESCALA	1:50, 1:25	

ENDEREÇO Rodovia SC-406, s/n, Praia Mole, Florianópolis, Santa Catarina

ASSINATURA: _____
CLIENTE OUZ
CPF/CNPJ: _____

ASSINATURA: _____
RESPONSÁVEL: HENRIQUE PIMONT
CAU A 20832-9

DESENHO: MAYCON PASSIG; ARTHUR ANDRADE; MIRELA MOSER



RUA ALVES DE BRITO, 141 - SALA 701
CENTRO - FLORIANÓPOLIS - SC
CEP: 88015-440
TELEFONE: 48 30251200
CELULAR: 48 97980485
WWW.PIMONTARQUITETURA.COM.BR
CONTATO@PIMONTARQUITETURA.COM.BR

ROOFTOP - BEM ESTAR