




ROOFTOP - PRAÇA 02 - FOGO DE CHÃO

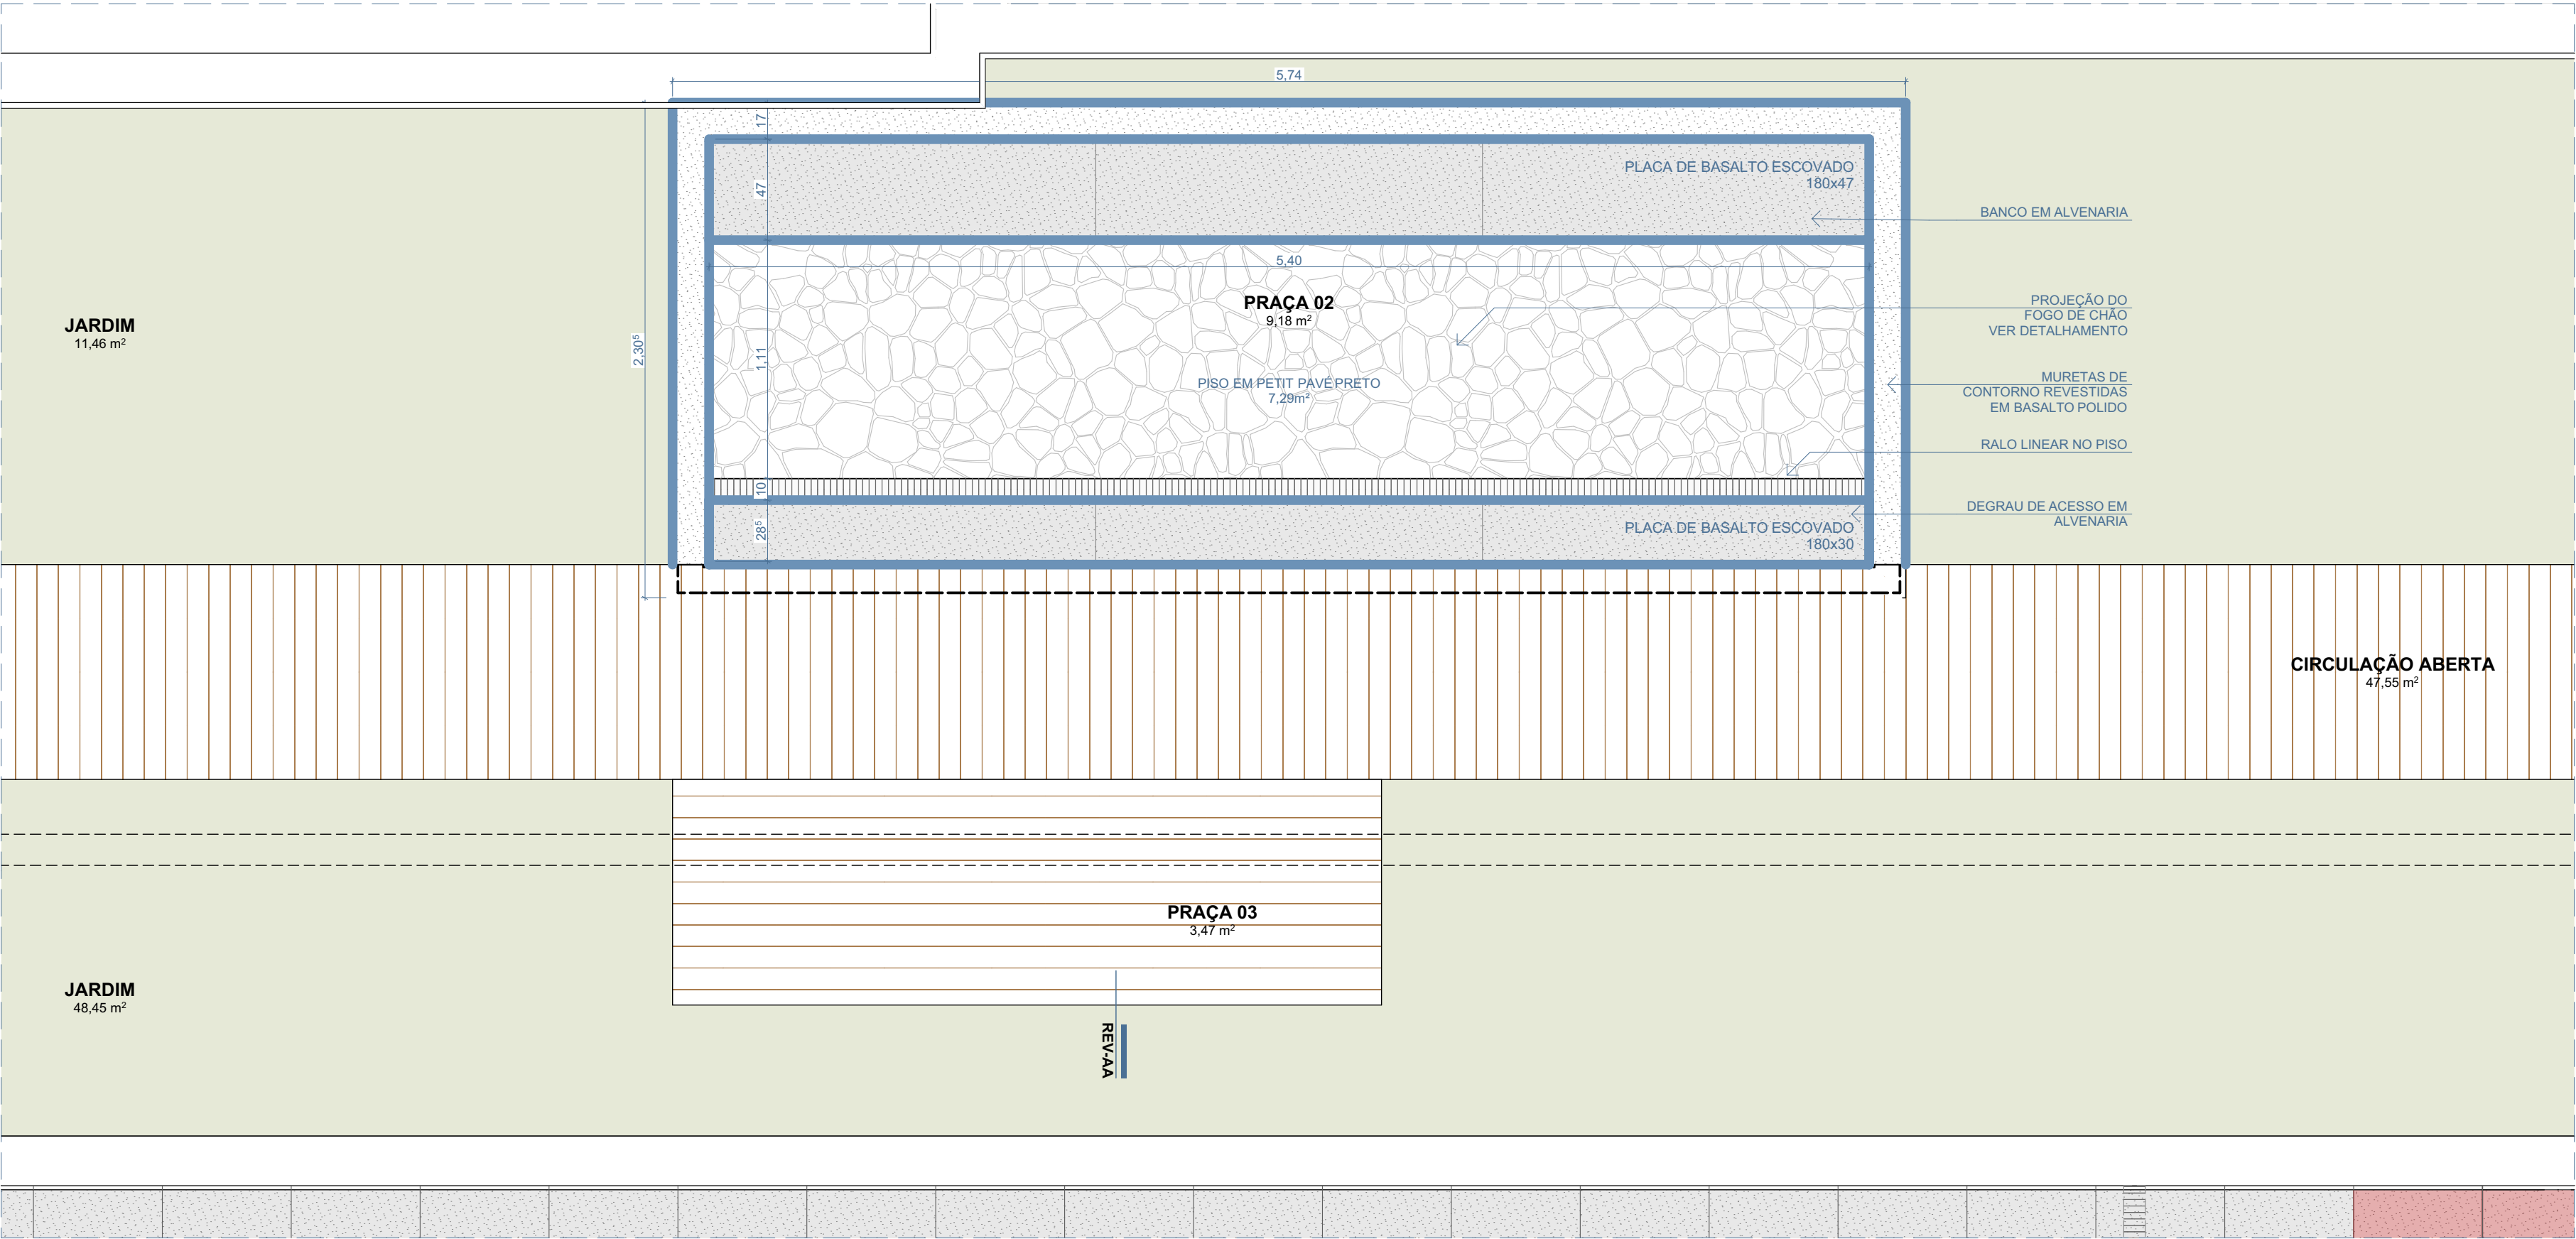


PLANTA BAIXA - PRAÇA DO FOGO
ESCALA 1:25

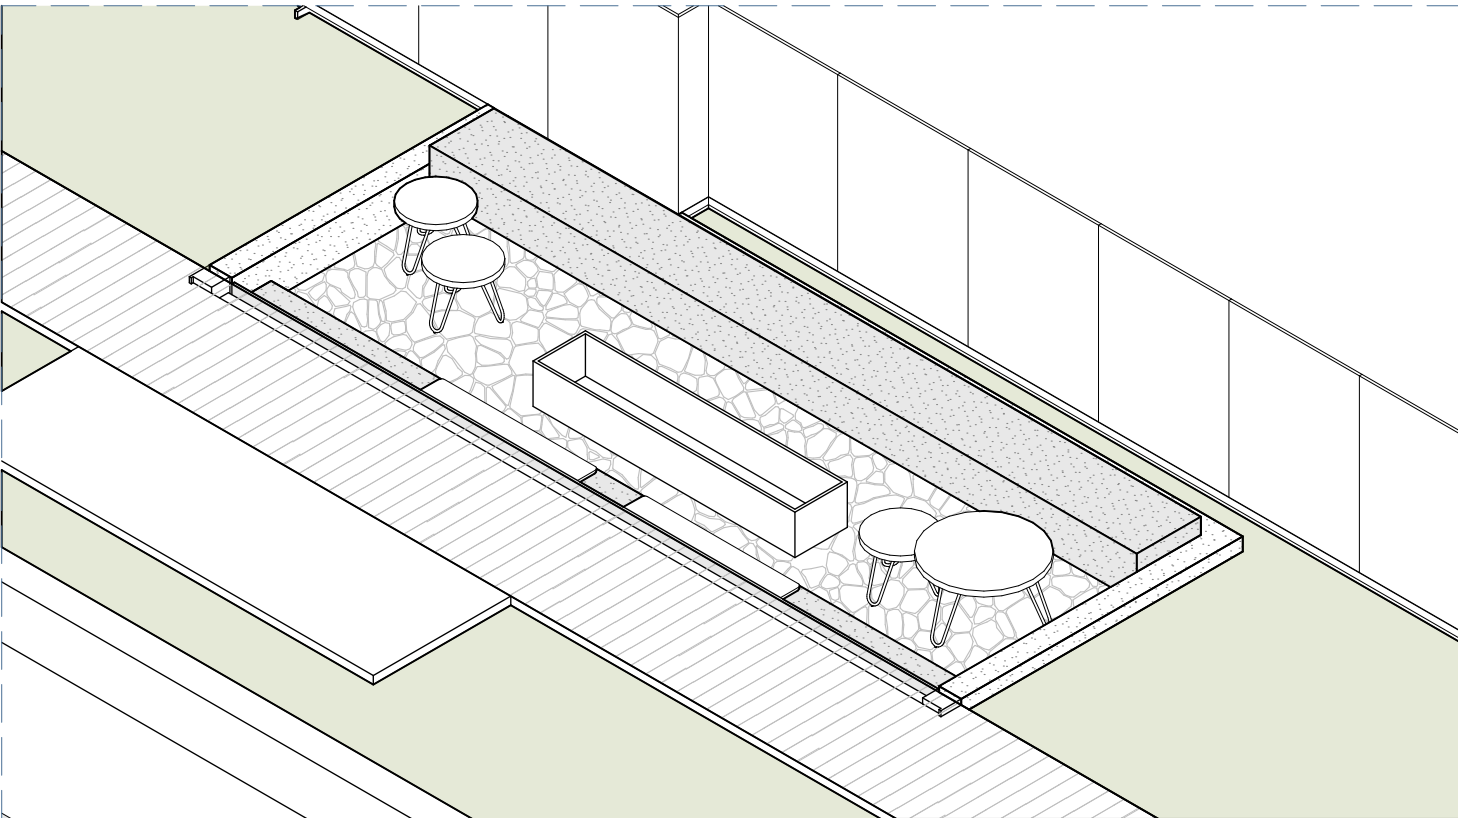


ISOMÉTRICA SUDESTE
ESCALA 1:50

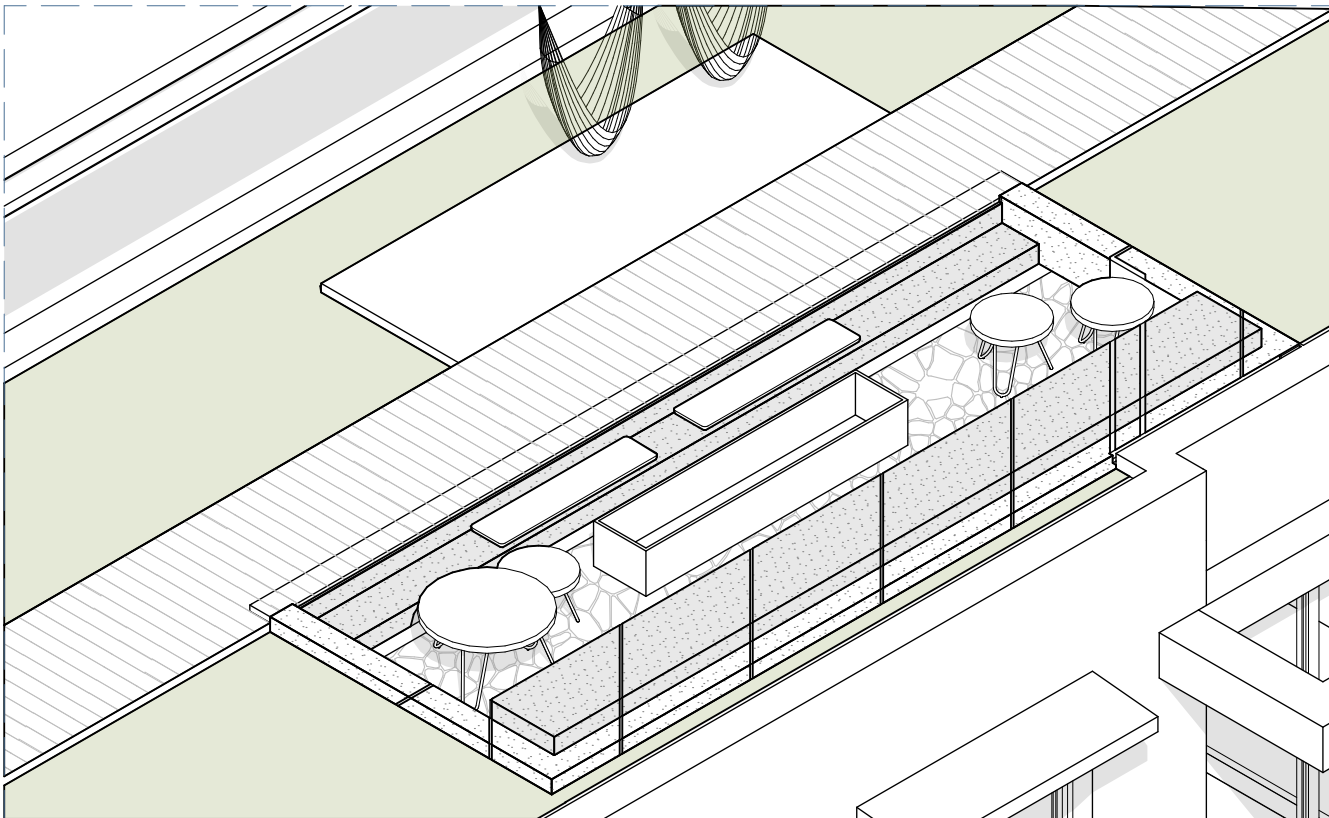

ISOMÉTRICA NORDESTE
ESCALA 1:50

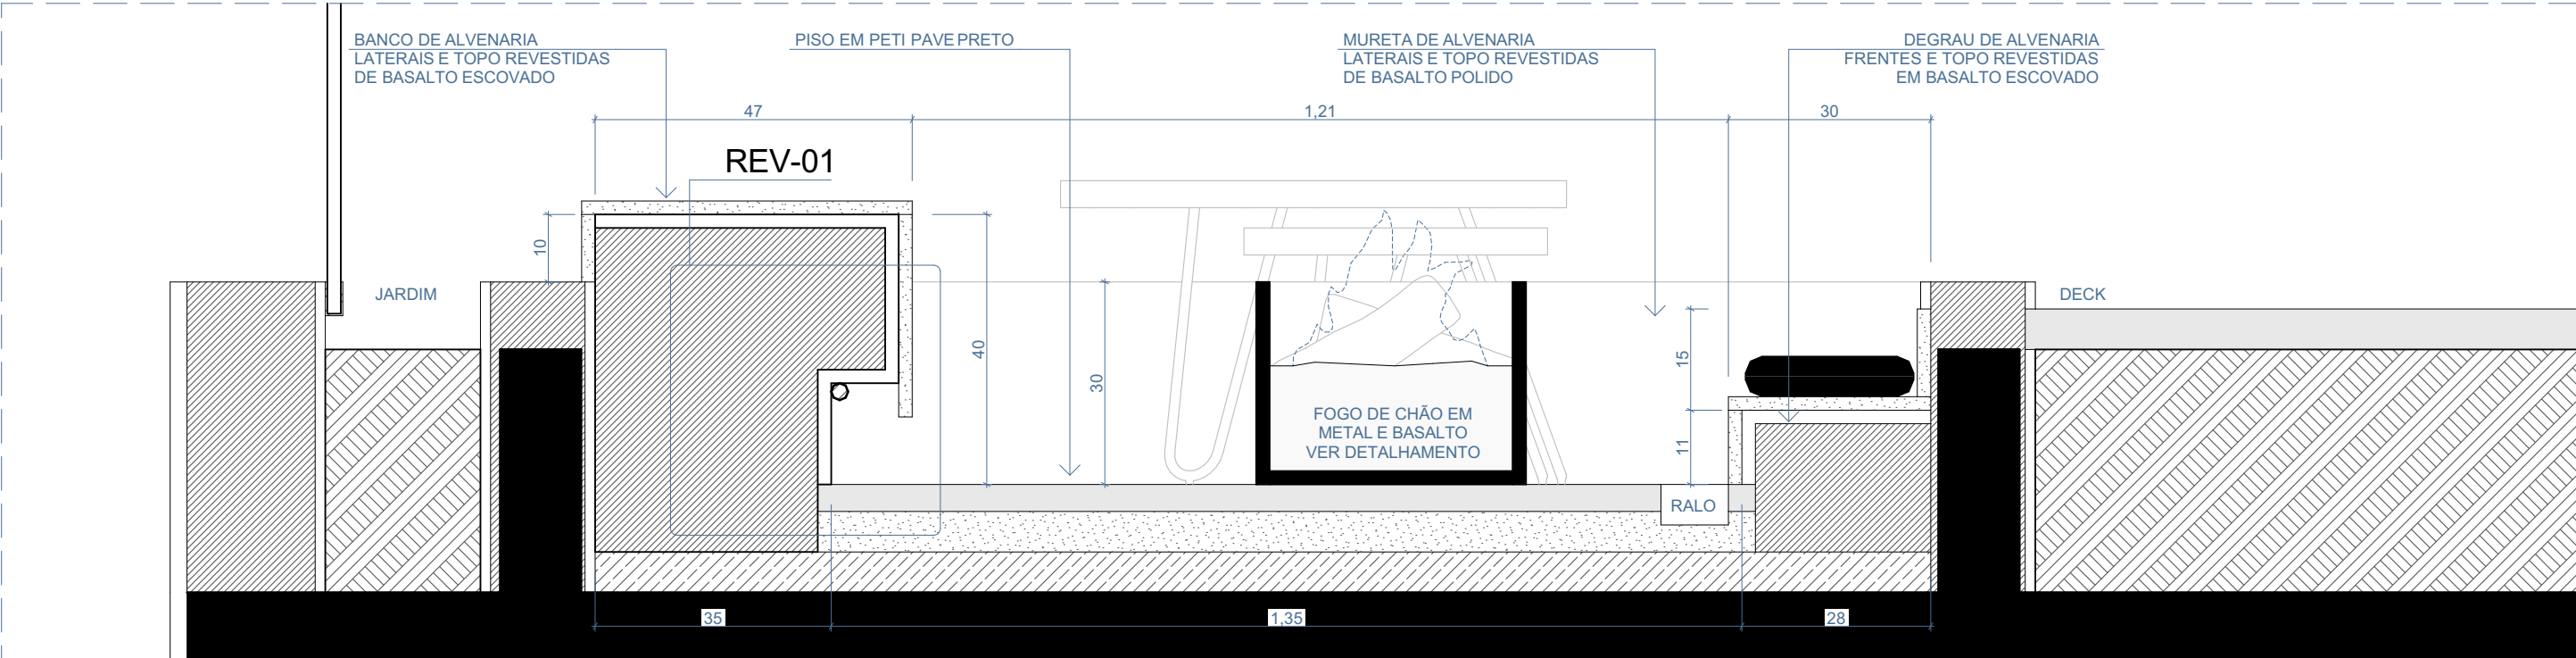

CORTE AA
ESCALA 1:10

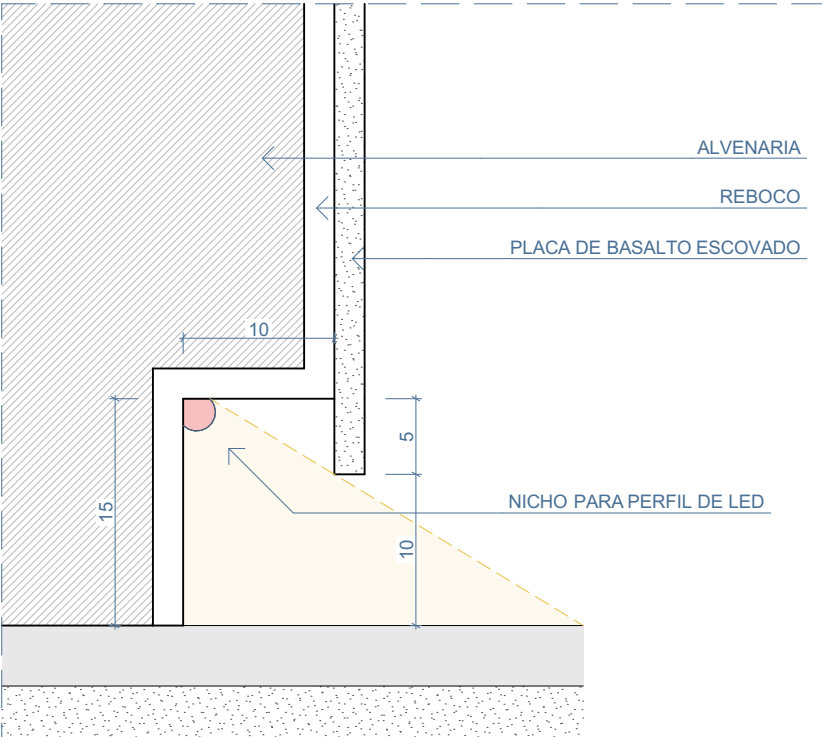

DETALHE REV-01
ESCALA 1:5

LEGENDA REVESTIMENTOS	
	PLACA DE CONCRETO 50x50
	PETIT PAVÉ BRANCO
	PETIT PAVÉ PRETO
	CIMENTO ALISADO
	CONCRETO VASSOURADO
	PORCELANATO 60x120
	PORCELANATO 60x60
	PORCELANATO 90x90
	PISO DE MADEIRA
	DECK DE MADEIRA
	PISO ESPORTIVO EMBORRACHADO EM PLACAS 100x100
	BASALTO RÚSTICO
	BASALTO POLIDO
	PISO CIMENTÍCIO SOLARIUM 50x50
	AZULEJO 30x60 BRANCO ACETINADO RETIFICADO
	TINTA DE PEDRA DIORE DELICATO PRECIOSA COR NATURAL
	TINTA DE PEDRA DIORE ORNAMENTAL MAXI COR BEGE ARACEMA
	TEXTURA TERRACOR PREDIAL PRETO
	PINTURA ACRÍLICA PRETA - SUVINIL PATATIVA
	BASALTO POLIDO
	REVESTIMENTO EM PEDRA NATURAL MOLEDO
	REVESTIMENTO EM LÂMINA FREIJÓ
	COMPENSADO VIROLA
	ESPELHO CRISTAL COLADO

PROJETO ARQUITETÔNICO
MAUI

18/18

INTERIORES AMBIENTAÇÃO - RTOP FOGO DE CHÃO

ETAPA	OUZ_MAUÍ_ARQ_PROJETO EXECUTIVO AMBIENTAÇÃO	A1
DATA	14/03/2025	
ESCALA	1:25, 1:50, 1:10, 1:5	
ENDEREÇO	Rodovia SC-406, s/n, Praia Mole, Florianópolis, Santa Catarina	
ASSINATURA:		
CLIENTE	OUZ	
	CPF/CNPJ:	
ASSINATURA:		
RESPONSÁVEL:	HENRIQUE PIMONT	
	CAU A 20832-9	
DESENHO:	MAYCON PASSIG; ARTHUR ANDRADE; MIRELA MOSER	