



IN01 | ACABAMENTO ELEVADOR TIPO


ACABAMENTO EM INOX ESCOVADO
04 UNIDADES

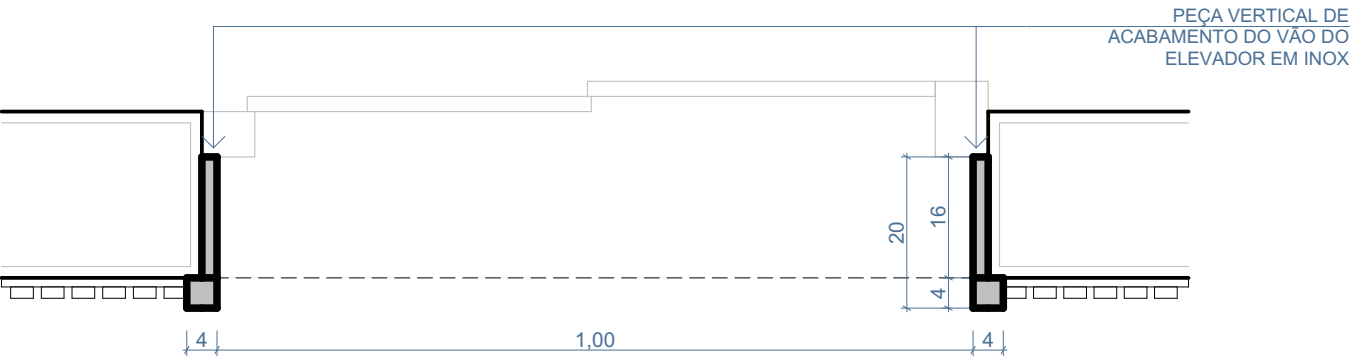

PLANTA BAIXA

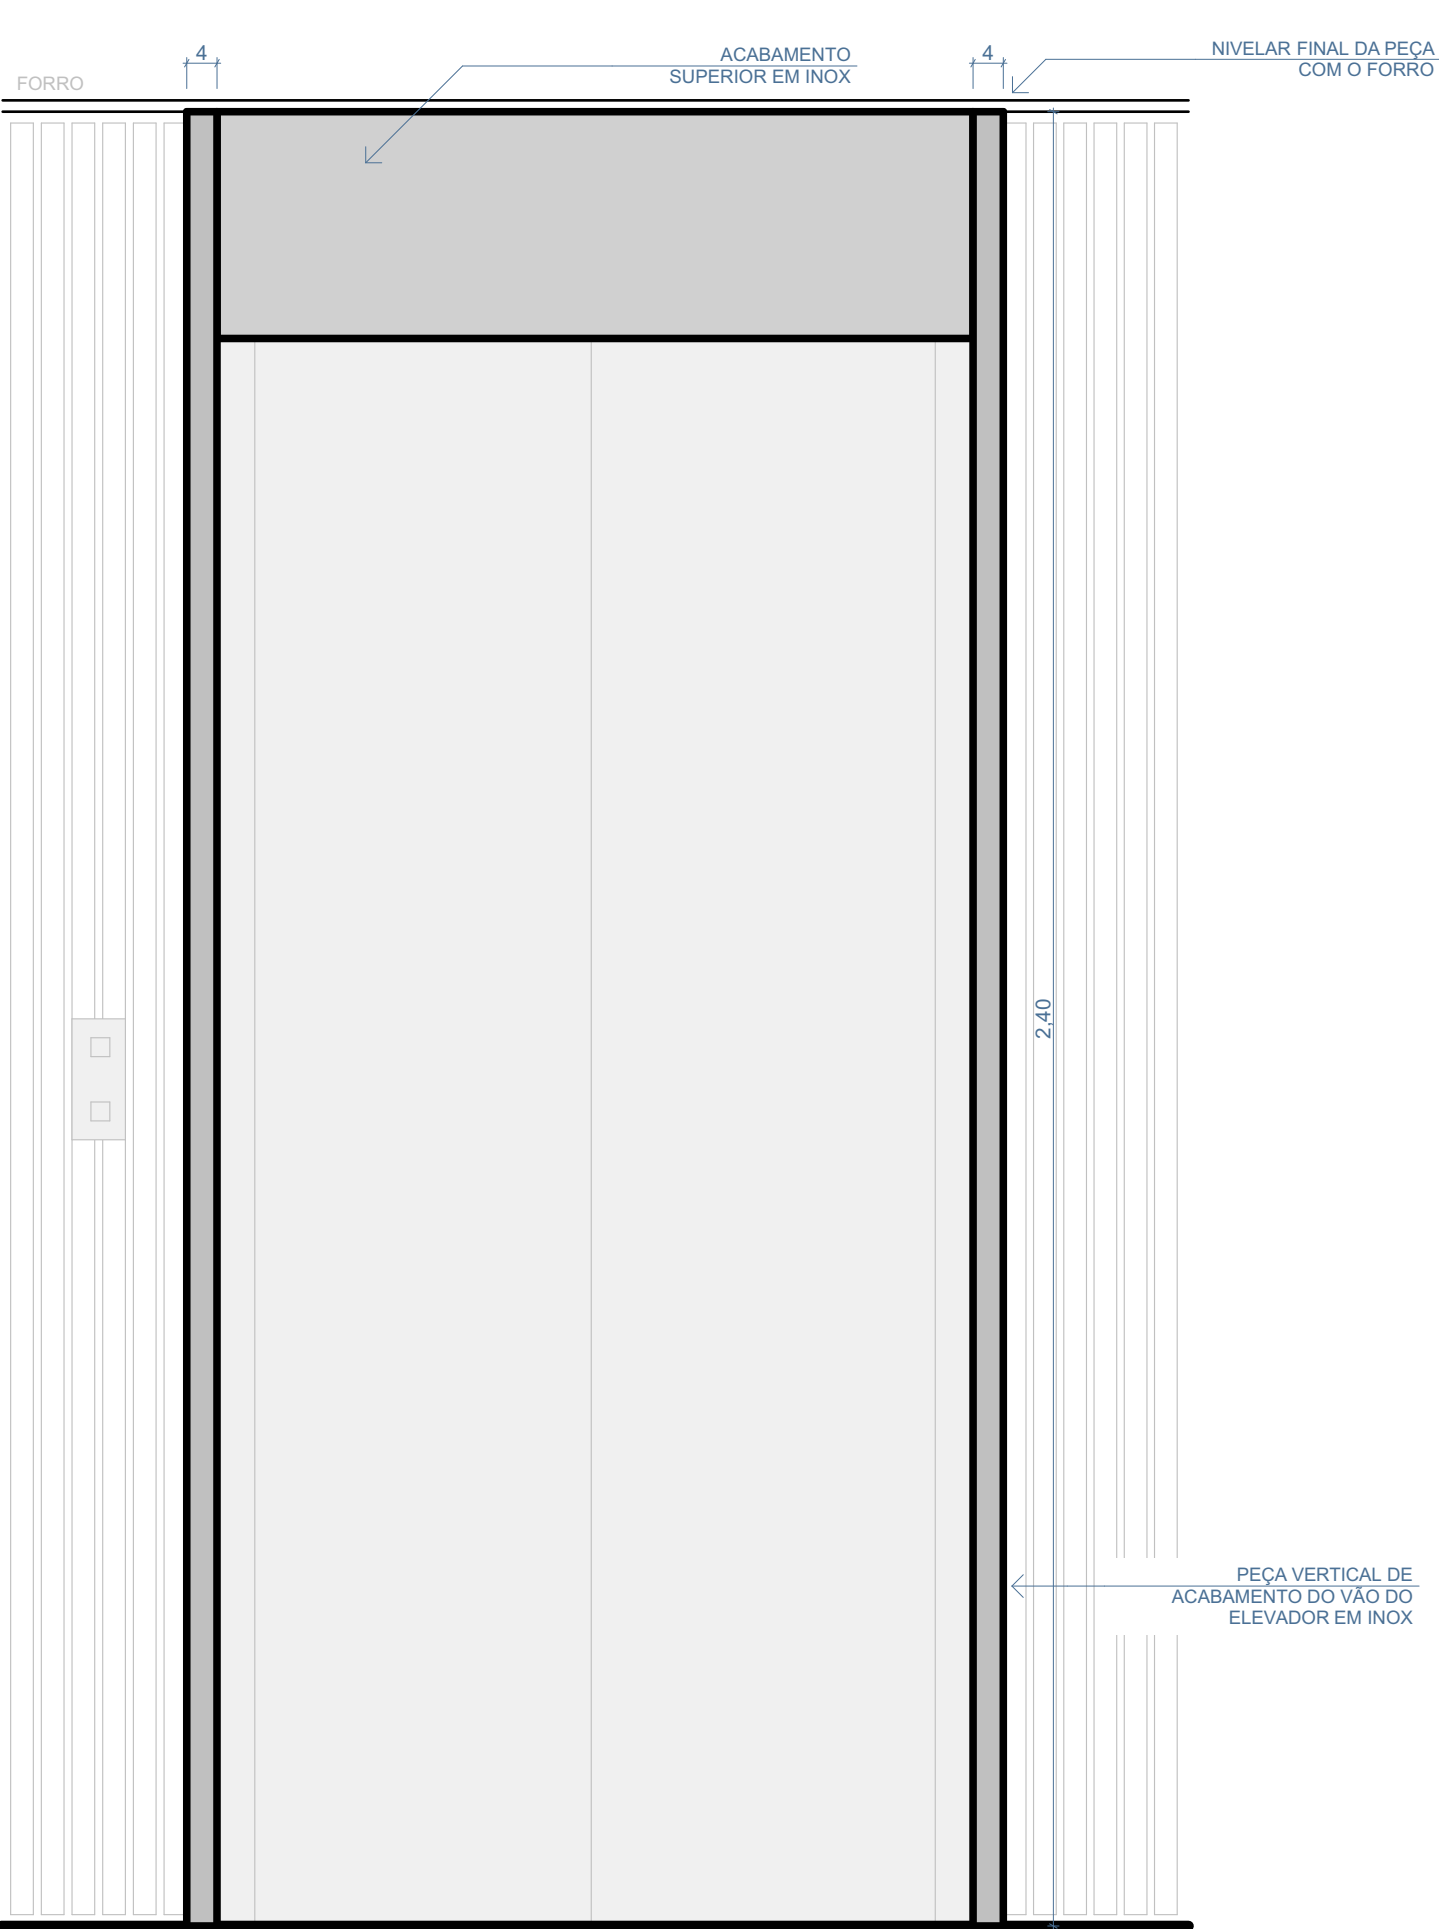

VISTA FRONTAL

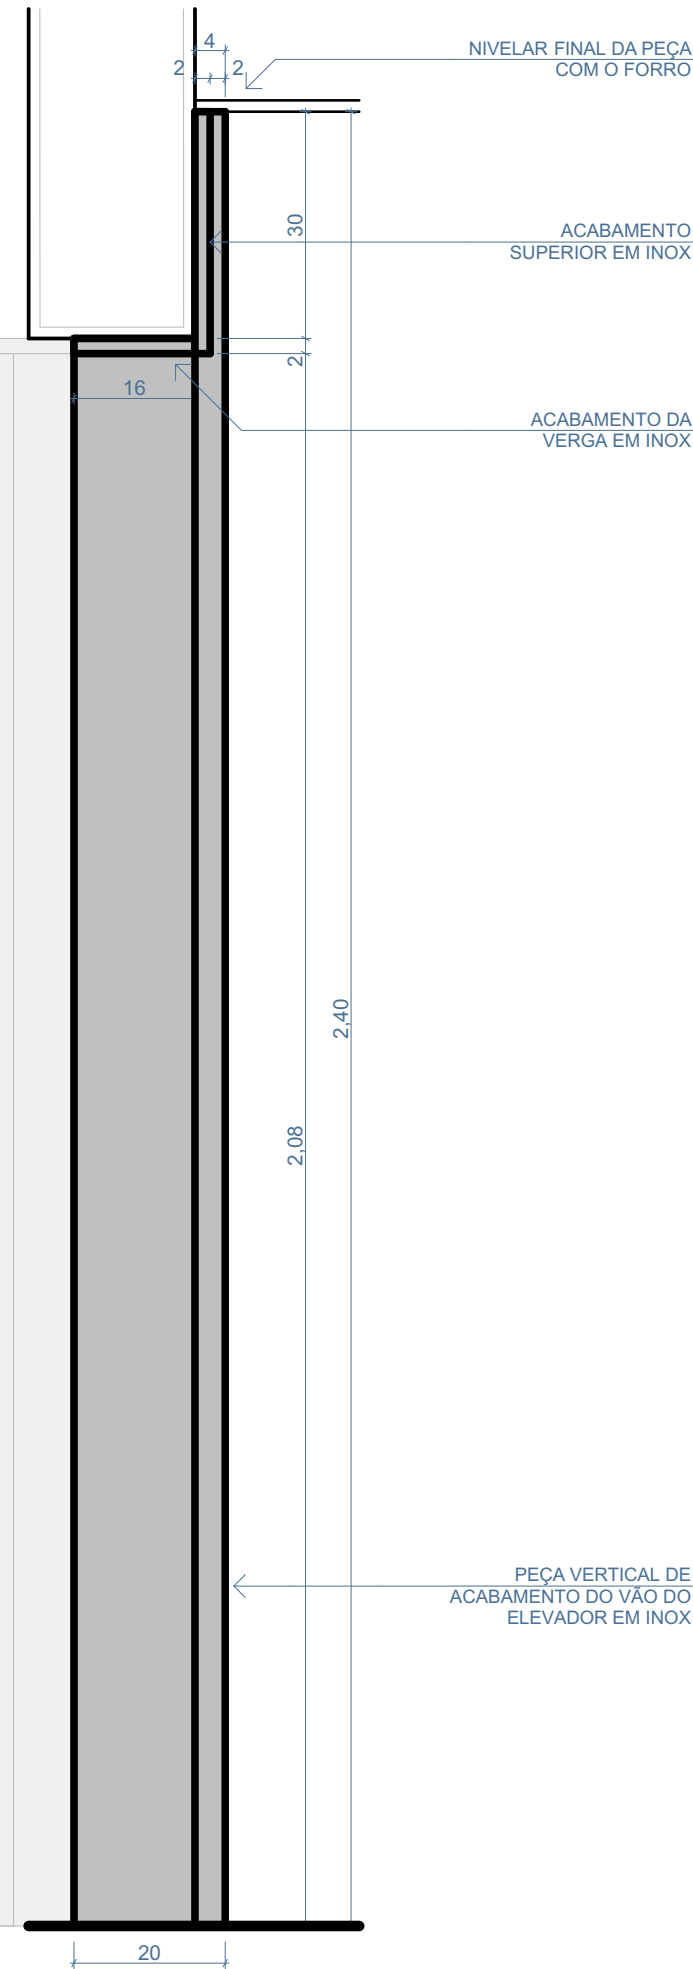

CORTE

PROJETO ARQUITETÔNICO

MAUI 10/10
INTERIORES DETALHAMENTO - INOX -
ELEVADORES PAV. TIPO

ETAPA	OUZ_MAU_ARQ_PROJETO EXECUTIVO DETALHAMENTO	A2
DATA	AMBIENTAÇÃO	
	13/03/2025	
ESCALA	1:10	

ENDEREÇO Rodovia SC-406, s/n, Praia Mole,
Florianópolis, Santa Catarina

ASSINATURA: _____
CLIENTE OUZ
CPF/CNPJ: _____

ASSINATURA: _____
RESPONSÁVEL: HENRIQUE PIMONT
CAU A 20832-9

DESENHO: MAYCON PASSIG; ARTHUR ANDRADE; MIRELA MOSER



RUA ALVES DE BRITO, 141 - SALA 701
CENTRO - FLORIANÓPOLIS - SC
CEP: 88015-440

TELEFONE: 48 30251200
CELULAR: 48 99806485

WWW.PIMONTARQUITETURA.COM.BR
CONTATO@PIMONTARQUITETURA.COM.BR