




ROOFTOP - DUCHAS

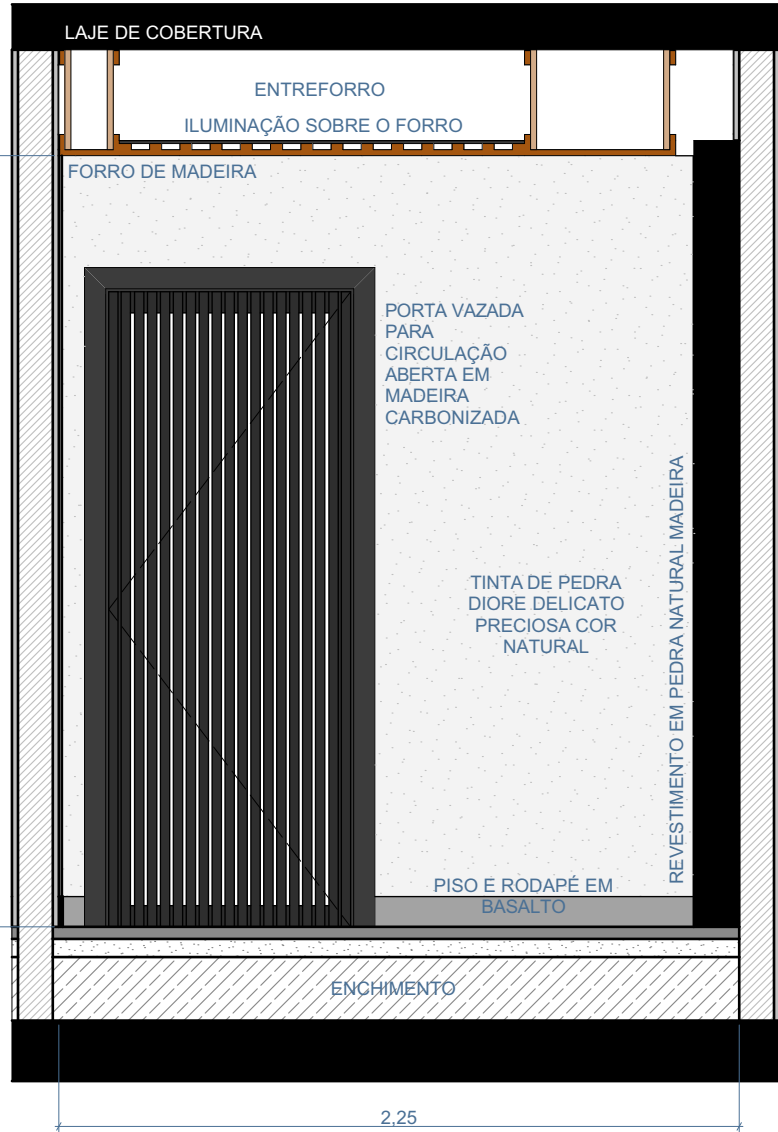


01
ESCALA 1:25

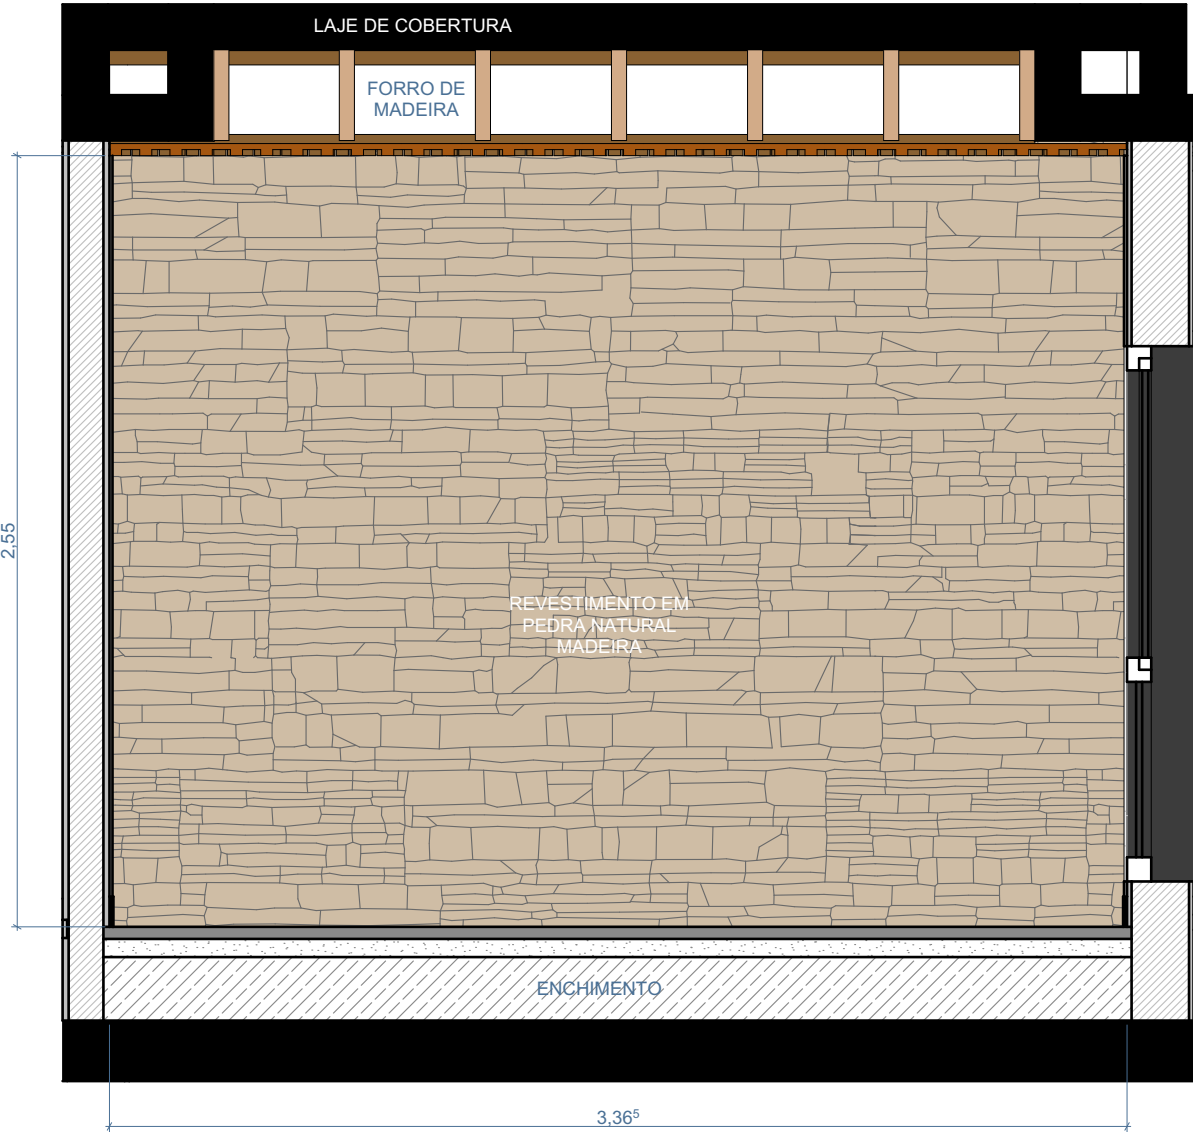


02
ESCALA 1:25

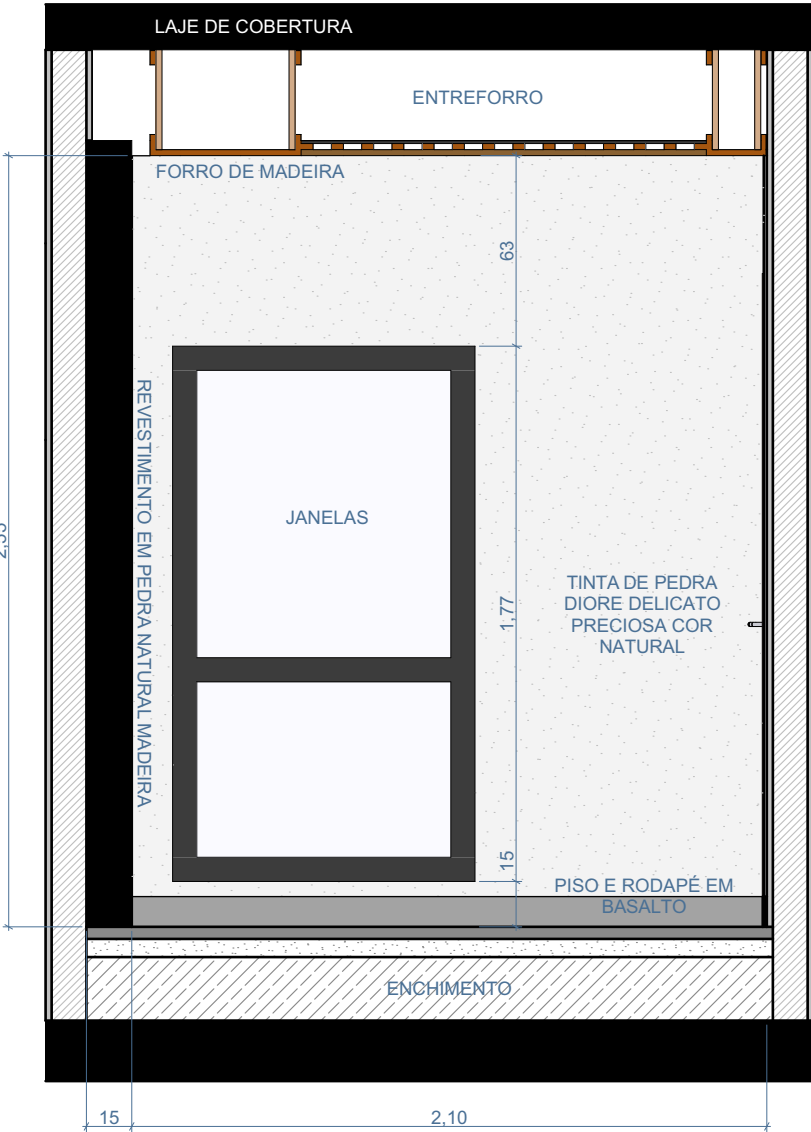

03
ESCALA 1:25

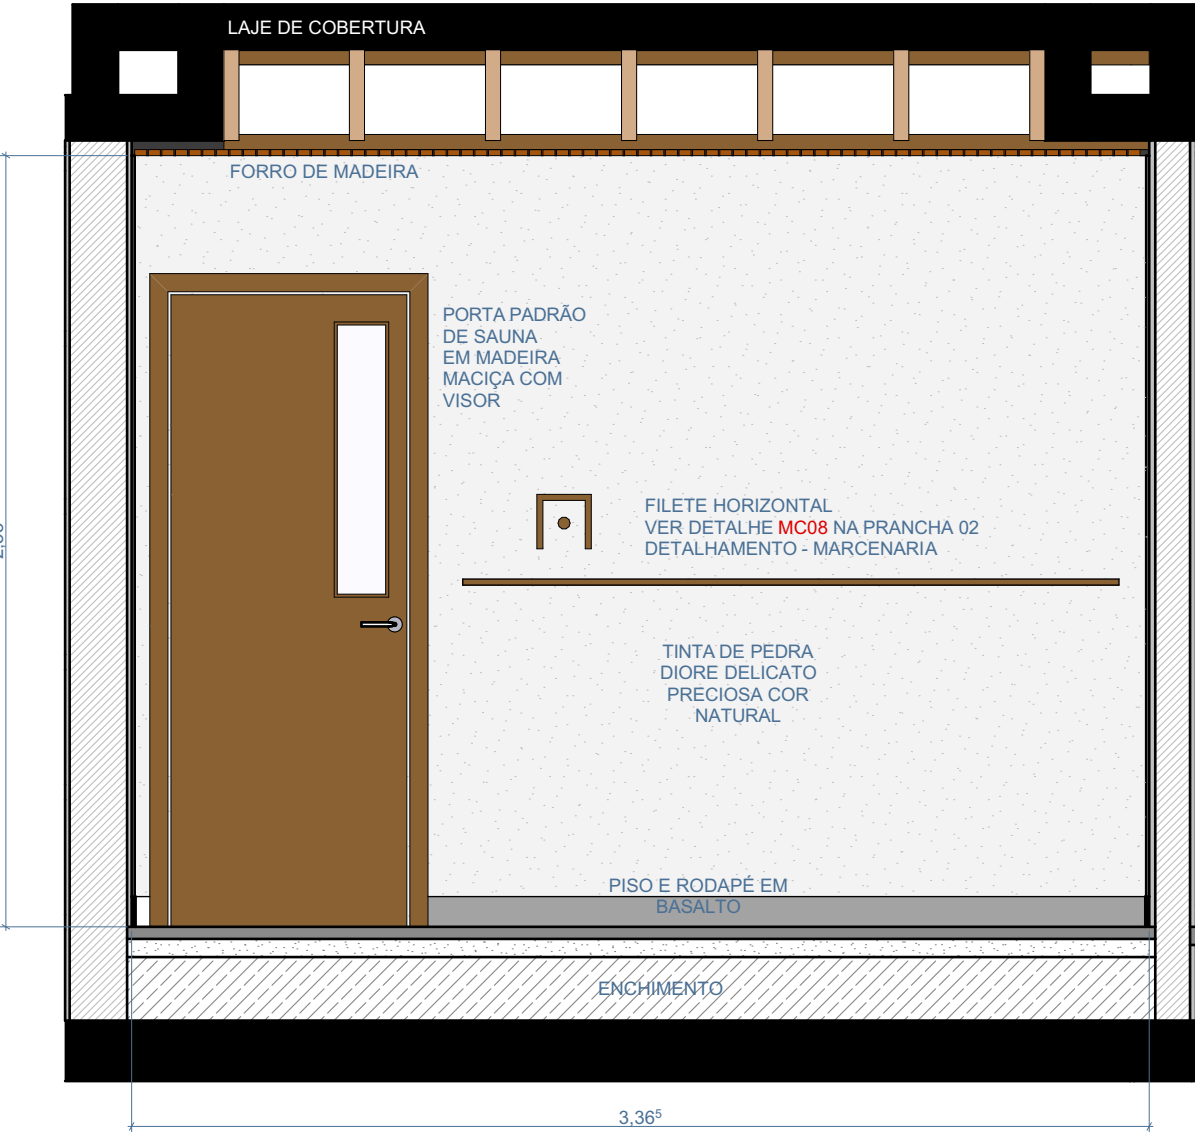


04
ESCALA 1:25

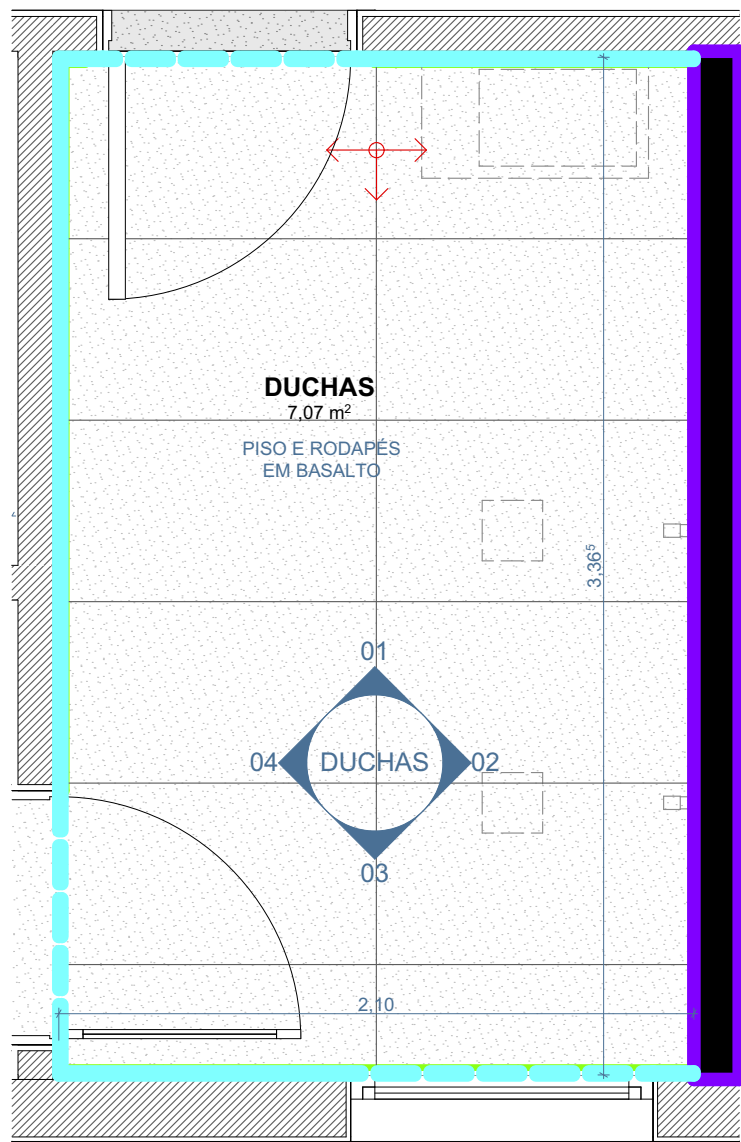


PLANTA BAIXA
ESCALA 1:25



VISTA SUPERIOR

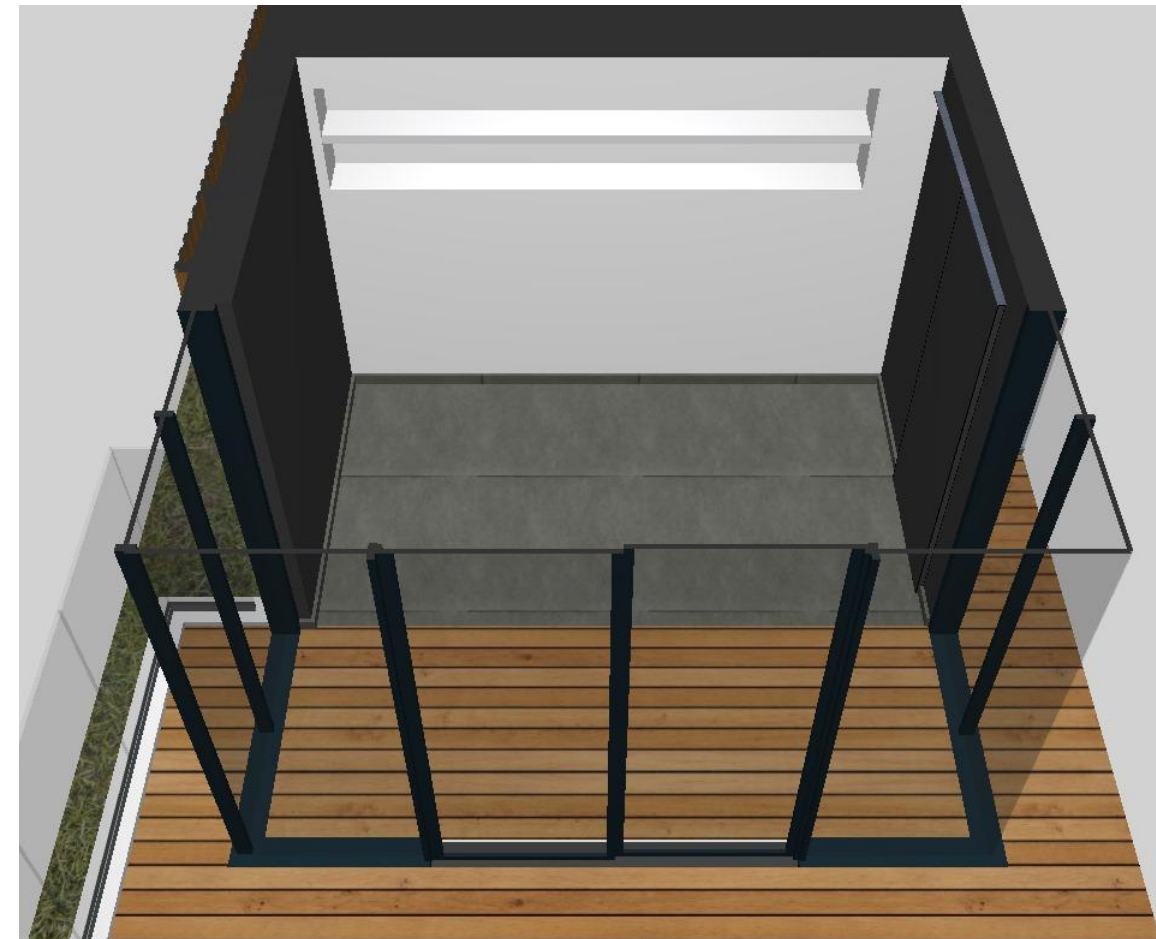

VISTA SUPERIOR

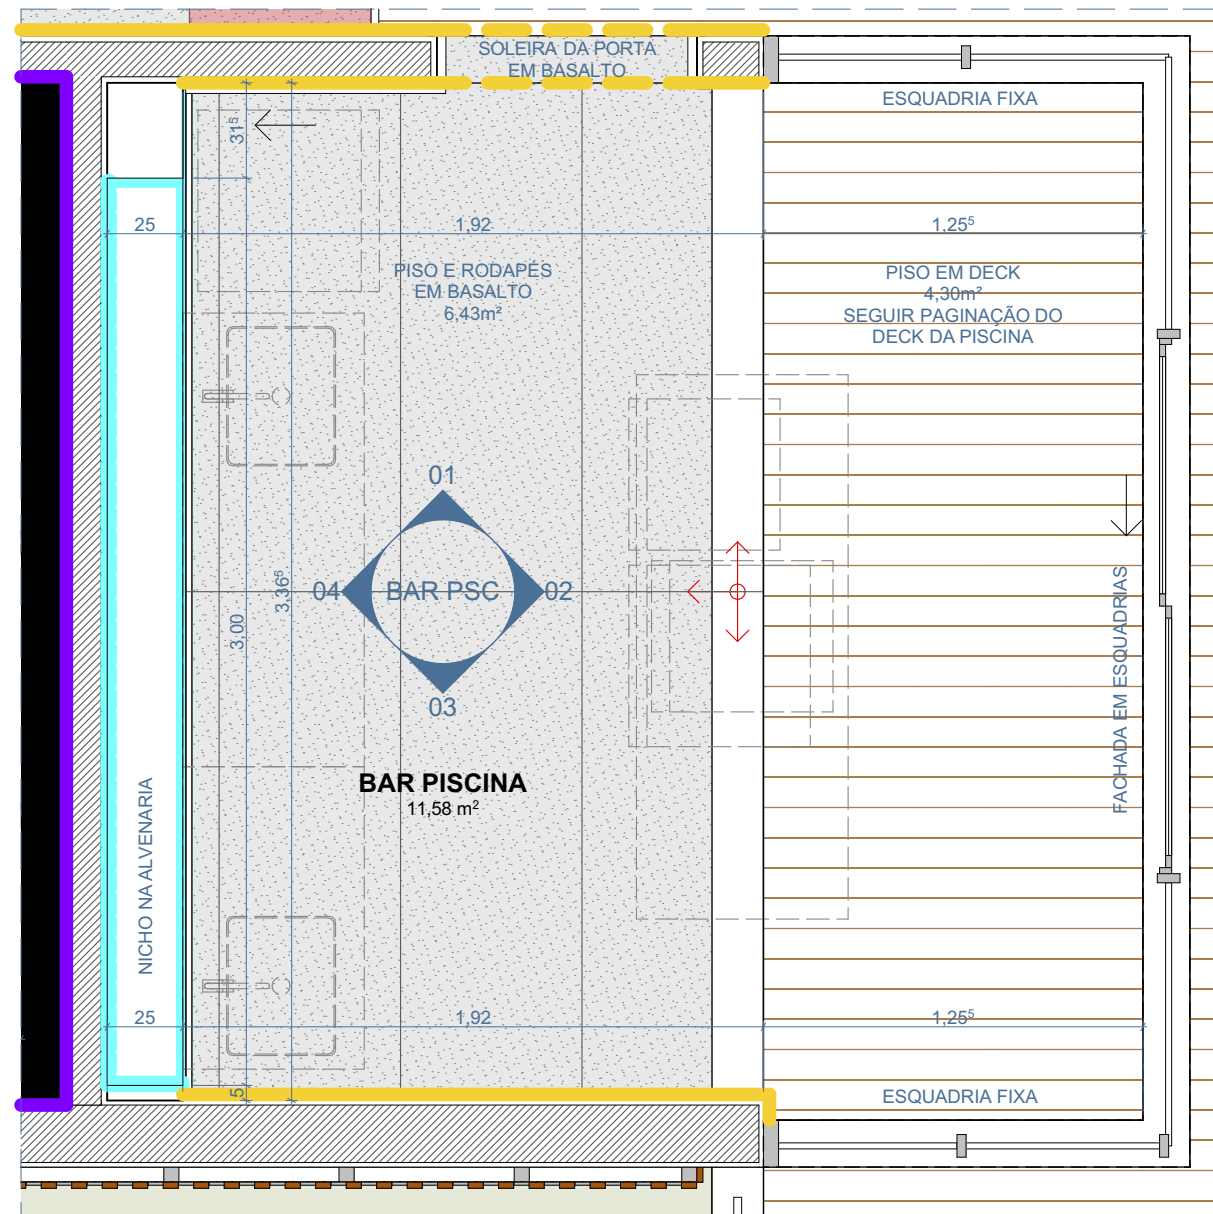

PLANTA BAIXA
ESCALA 1:25


LEGENDA REVESTIMENTOS			
	PLACA DE CONCRETO 50x50		AZULEJO 30x60 BRANCO ACETINADO RETIFICADO
	PETIT PAVÉ BRANCO		TINTA DE PEDRA DIORE DELICATO PRECIOSA COR NATURAL
	PETIT PAVÉ PRETO		TINTA DE PEDRA DIORE ORNAMENTAL MAXI COR BEGE ARAÇAMA
	CIMENTO ALISADO		TEXTURA TERRACOR PREDIAL PRETO
	CONCRETO VASSOURADO		PINTURA ACRILICA PRETA - SIVINIL PATATIVA
	PORCELANATO 60x120		BASALTO POLIDO
	PORCELANATO 60x60		REVESTIMENTO EM PEDRA NATURAL MOLEDO
	PORCELANATO 90x90		REVESTIMENTO EM LÂMINA FREIJÓ
	PISO DE MADEIRA		COMPENSADO VIROLA
	DECK DE MADEIRA		ESPELHO CRISTAL COLADO
	PISO ESPORTIVO EMBORRACHADO EM PLACAS 100x100		

NOTAS


1. PILARES DA GARAGEM E MURETAS DO ACESSO SÃO EM CONCRETO APARENTE;
2. PAREDES INTERNAS SEM INDICAÇÃO DE REVESTIMENTO RECEBERÃO PINTURA ACRILICA COR BRANCO FOSCO.
3. PAREDES EXTERNAS SEM INDICAÇÃO DE REVESTIMENTO RECEBERÃO PINTURA TERRACOR PREDIAL BRANCO
4. SOLEIRAS DAS PORTAS DOS APARTAMENTOS EM PEÇA ÚNICA SEGUNDO ESPECIFICAÇÃO DO PISO DA CIRCULAÇÃO COMUM




02
ESCALA 1:25

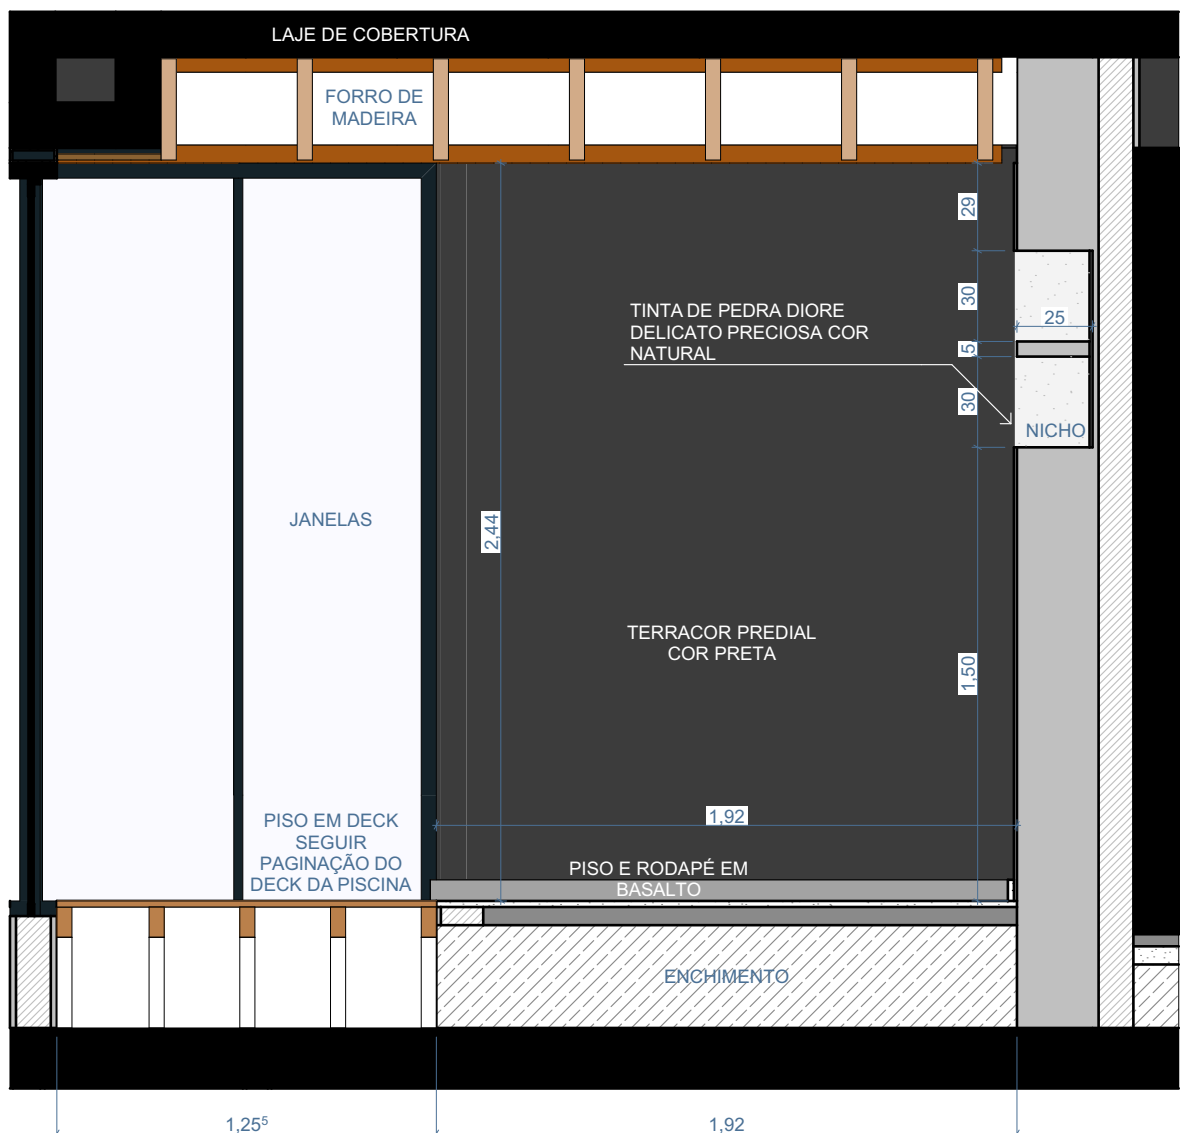

03
ESCALA 1:25

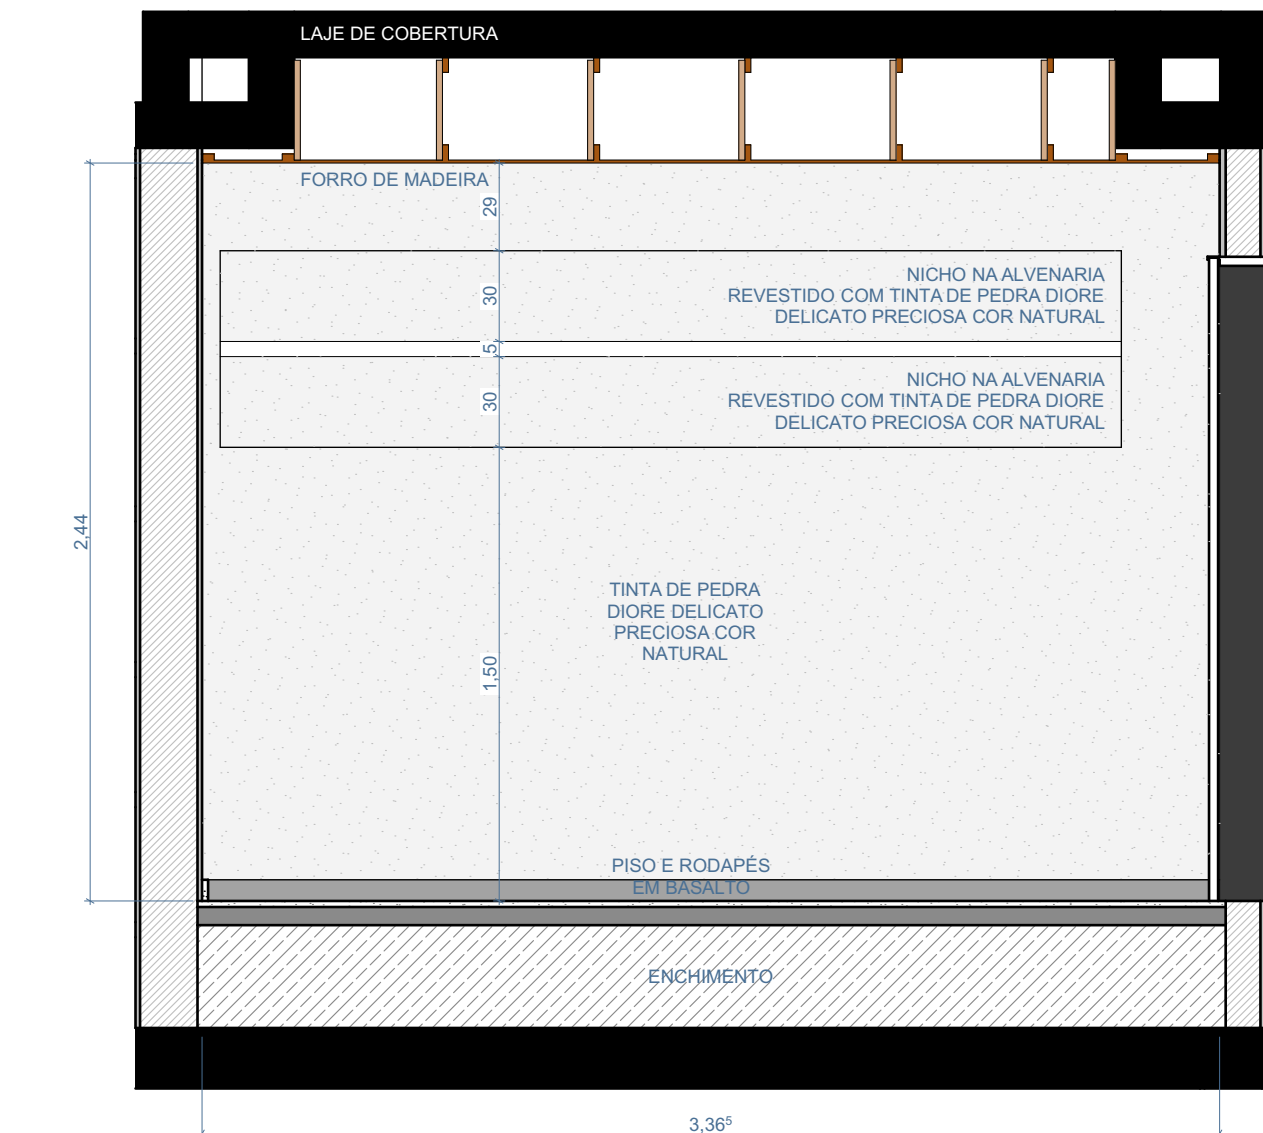

04
ESCALA 1:25

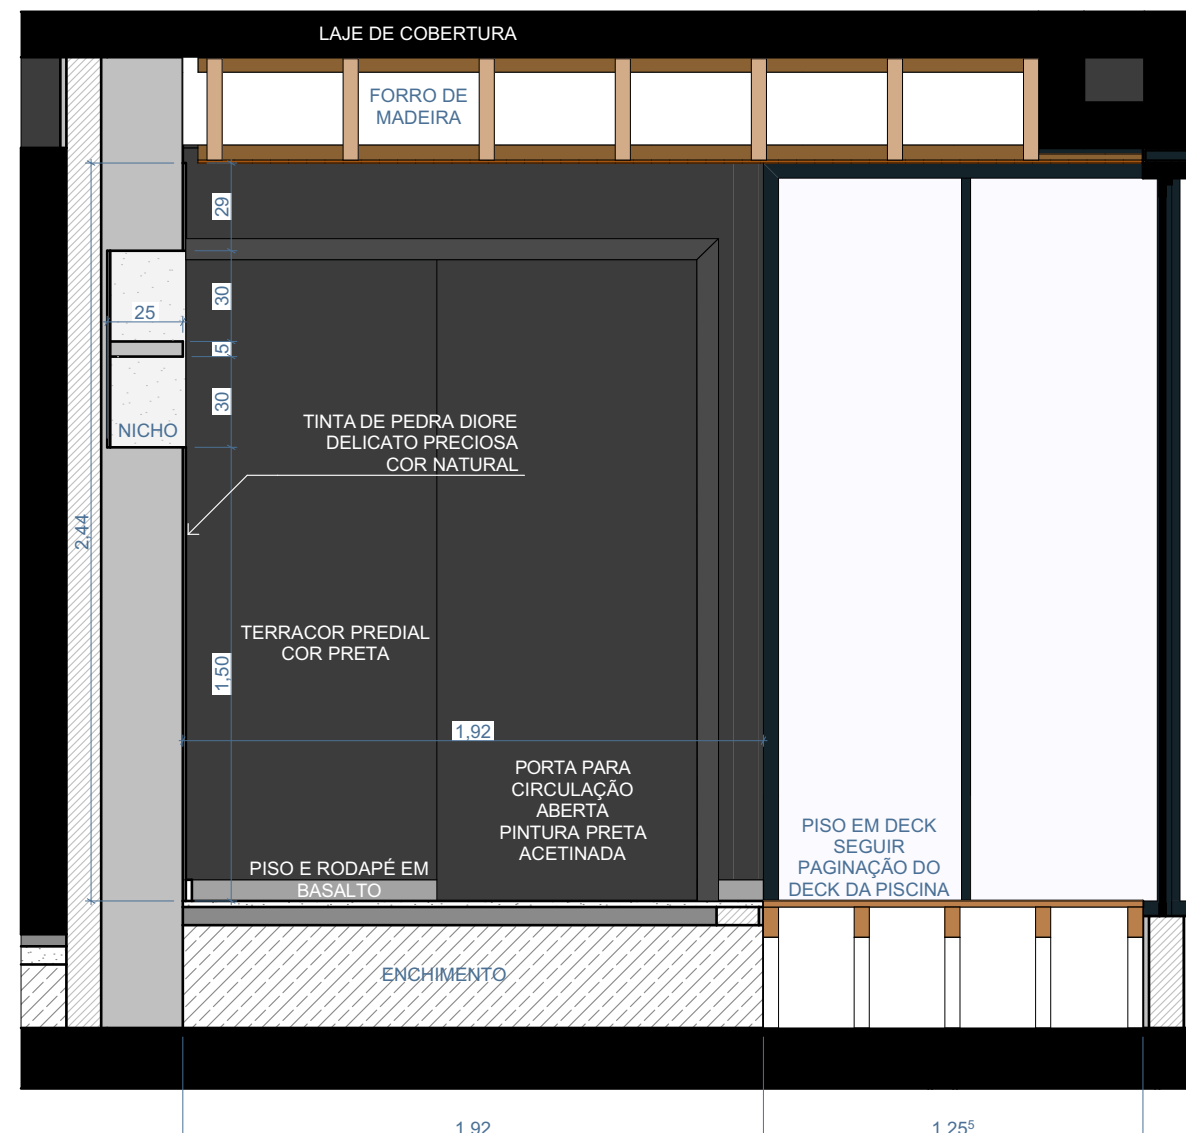

01
ESCALA 1:25

PROJETO ARQUITETÔNICO

MAUI
INTERIORES AMBIENTAÇÃO - RTOP DUCHAS / BAR
PISCINA

ETAPA	OUZ_MAU_ARQ_PROJETO EXECUTIVO AMBIENTAÇÃO	A1 EST.
DATA	14/03/2025	
ESCALA	1:25, 1:50	
ENDEREÇO	Rodovia SC-406, s/n, Praia Mole, Florianópolis, Santa Catarina	
ASSINATURA:		
CLIENTE	OUZ	
	CPF/CNPJ:	
ASSINATURA:		
RESPONSÁVEL:	HENRIQUE PIMONT	
	CAU A 20832-9	
DESENHO:	MAYCON PASSIG; ARTHUR ANDRADE; MIRELA MOSER	



RUA ALVES DE BRITO, 141 - SALA 701
CENTRO - FLORIANÓPOLIS - SC
CEP: 88015-440
TELEFONE: 48 30251200
CELULAR: 48 99806485
WWW.PIMONTARQUITETURA.COM.BR
CONTATO@PIMONTARQUITETURA.COM.BR

ROOFTOP - BAR PISCINA