




SUBSOLO - HALL TORRE B

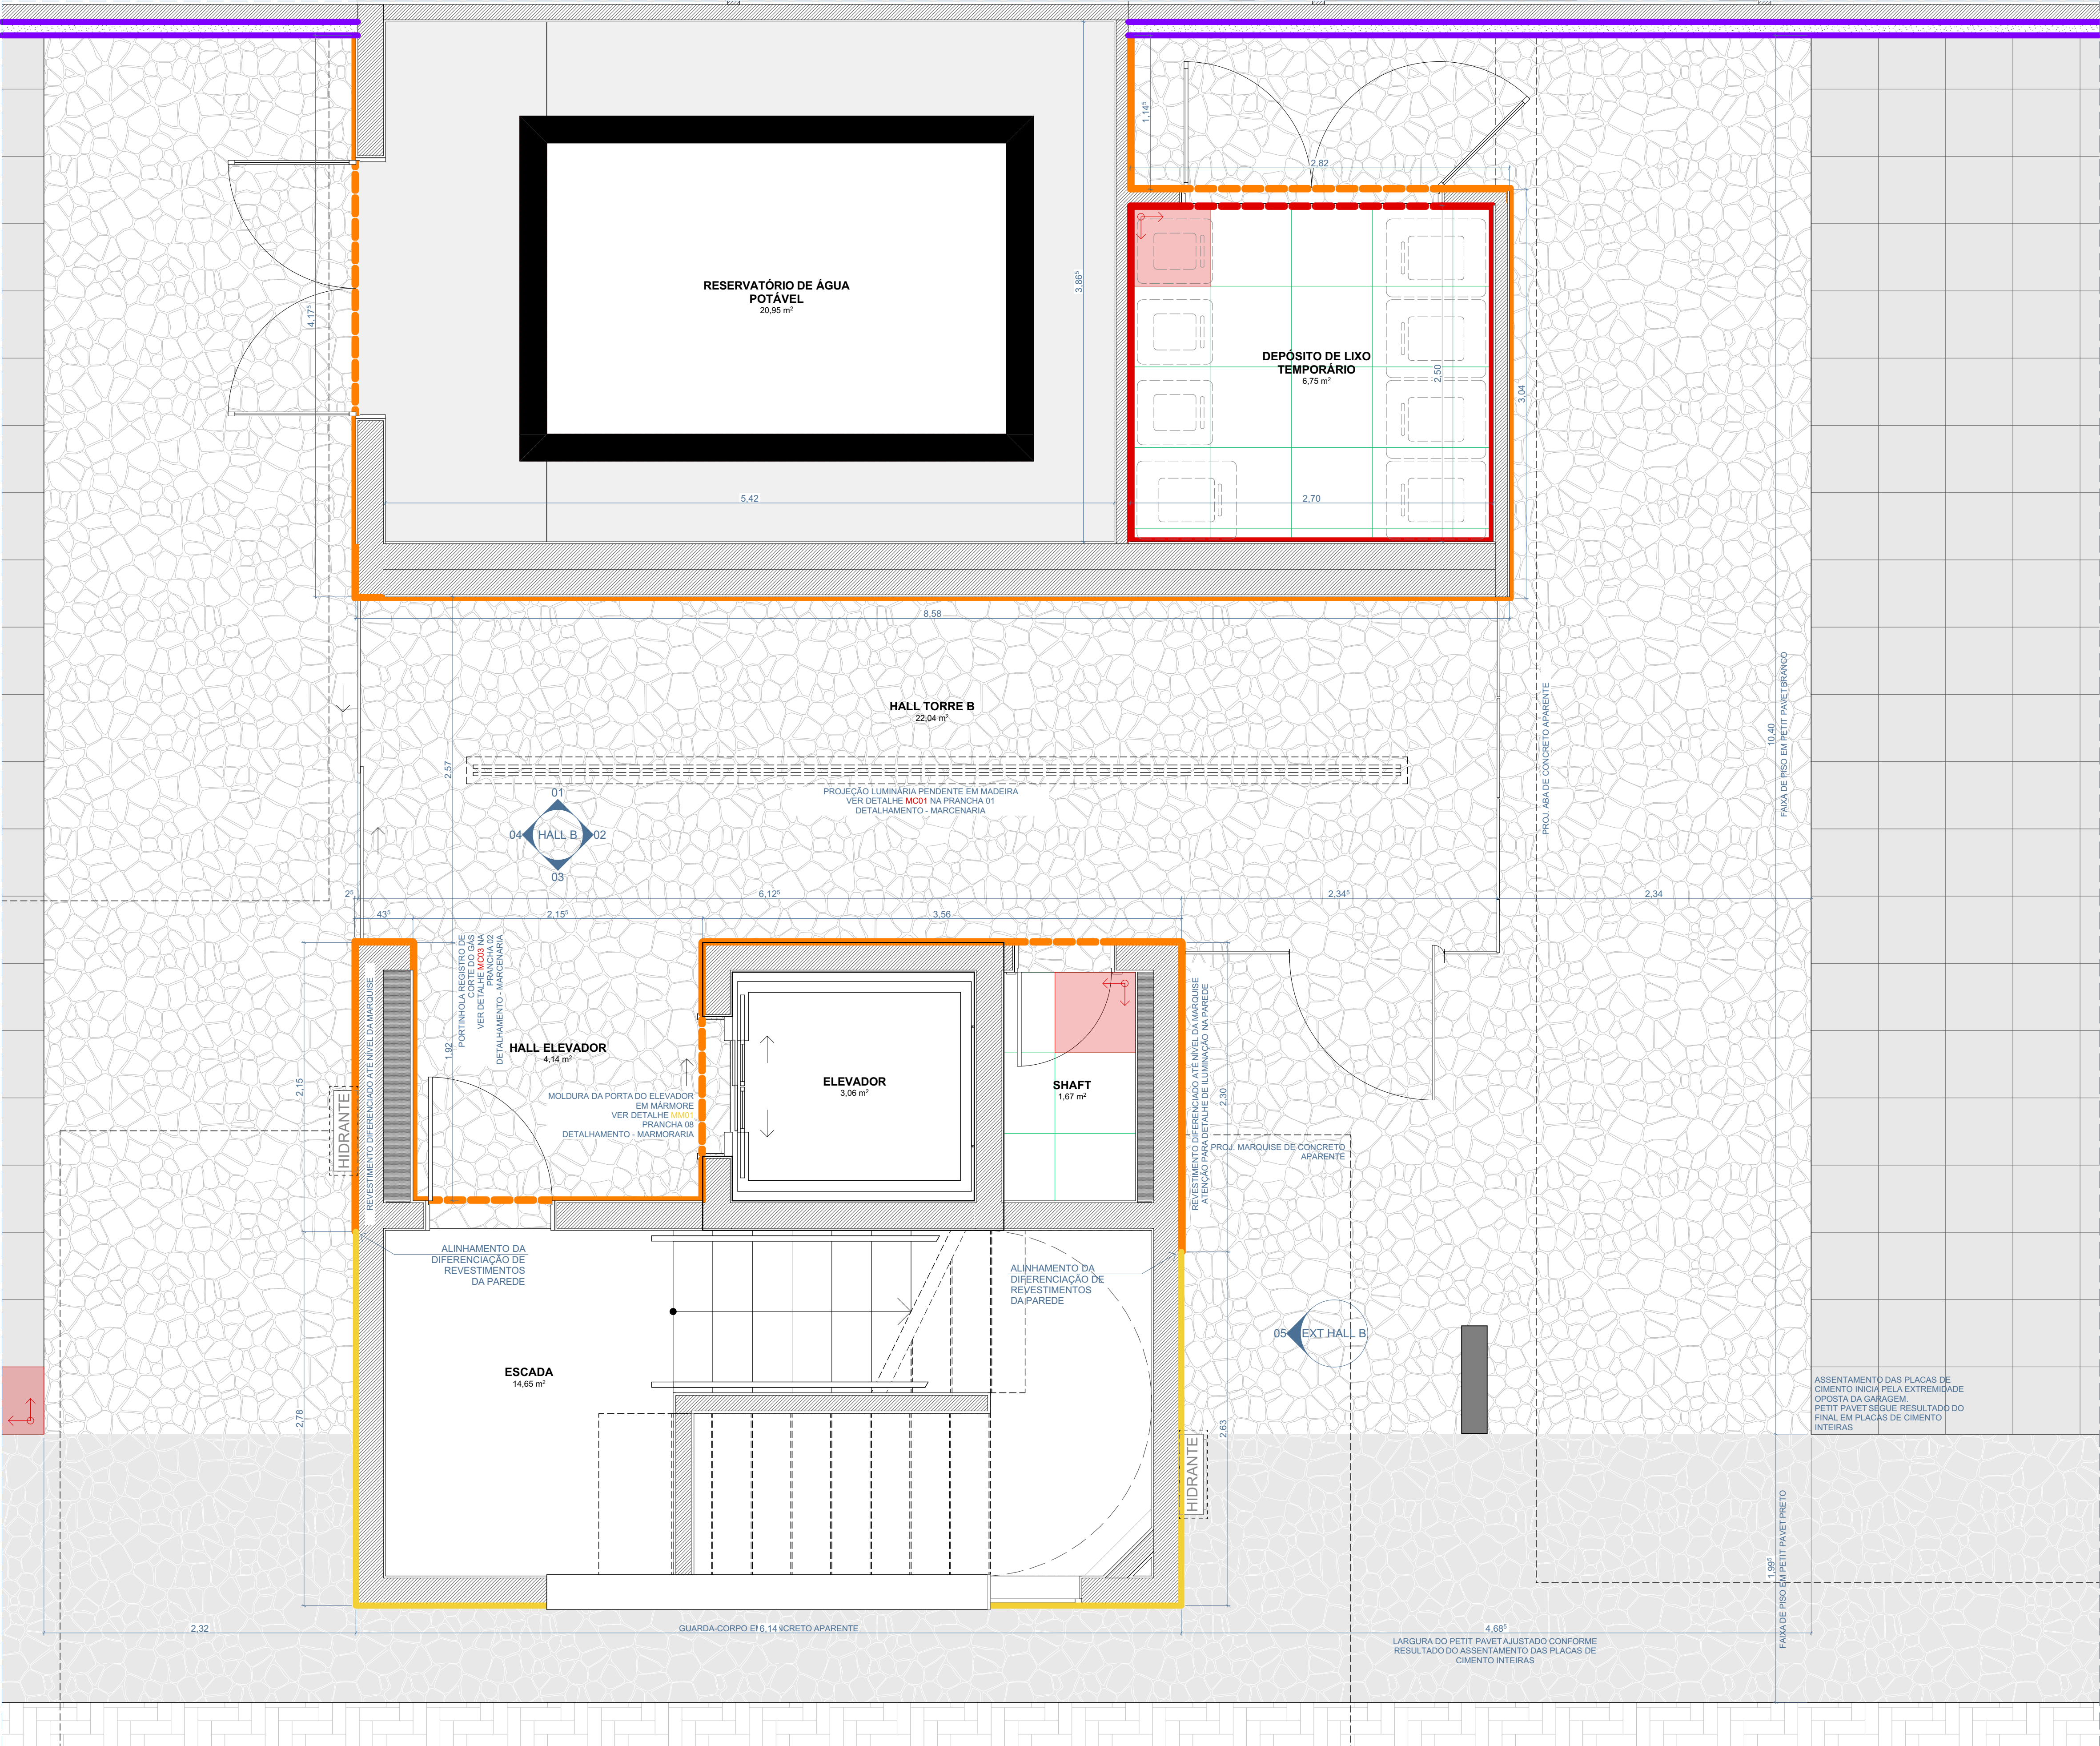


PLANTA BAIXA - HALL B
ESCALA 1:25

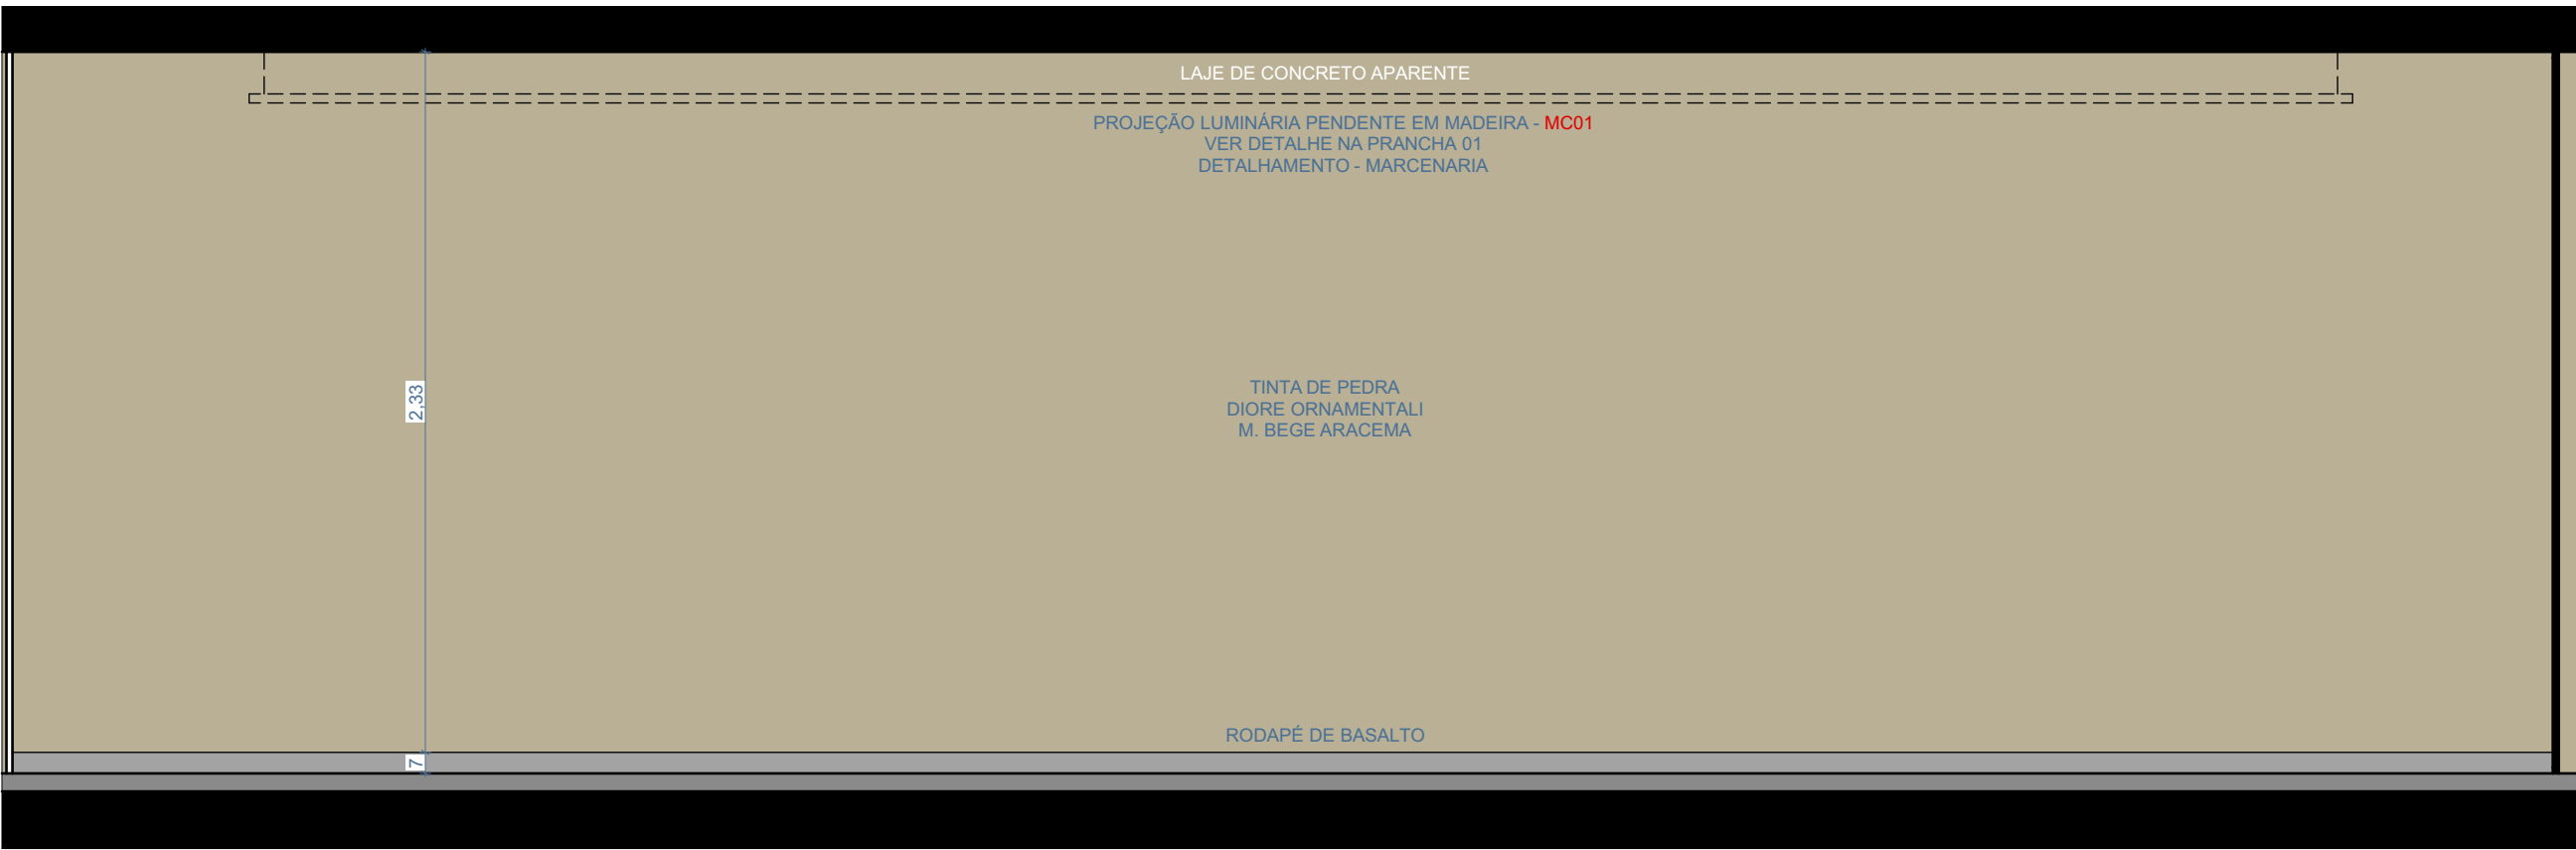


01
ESCALA 1:25

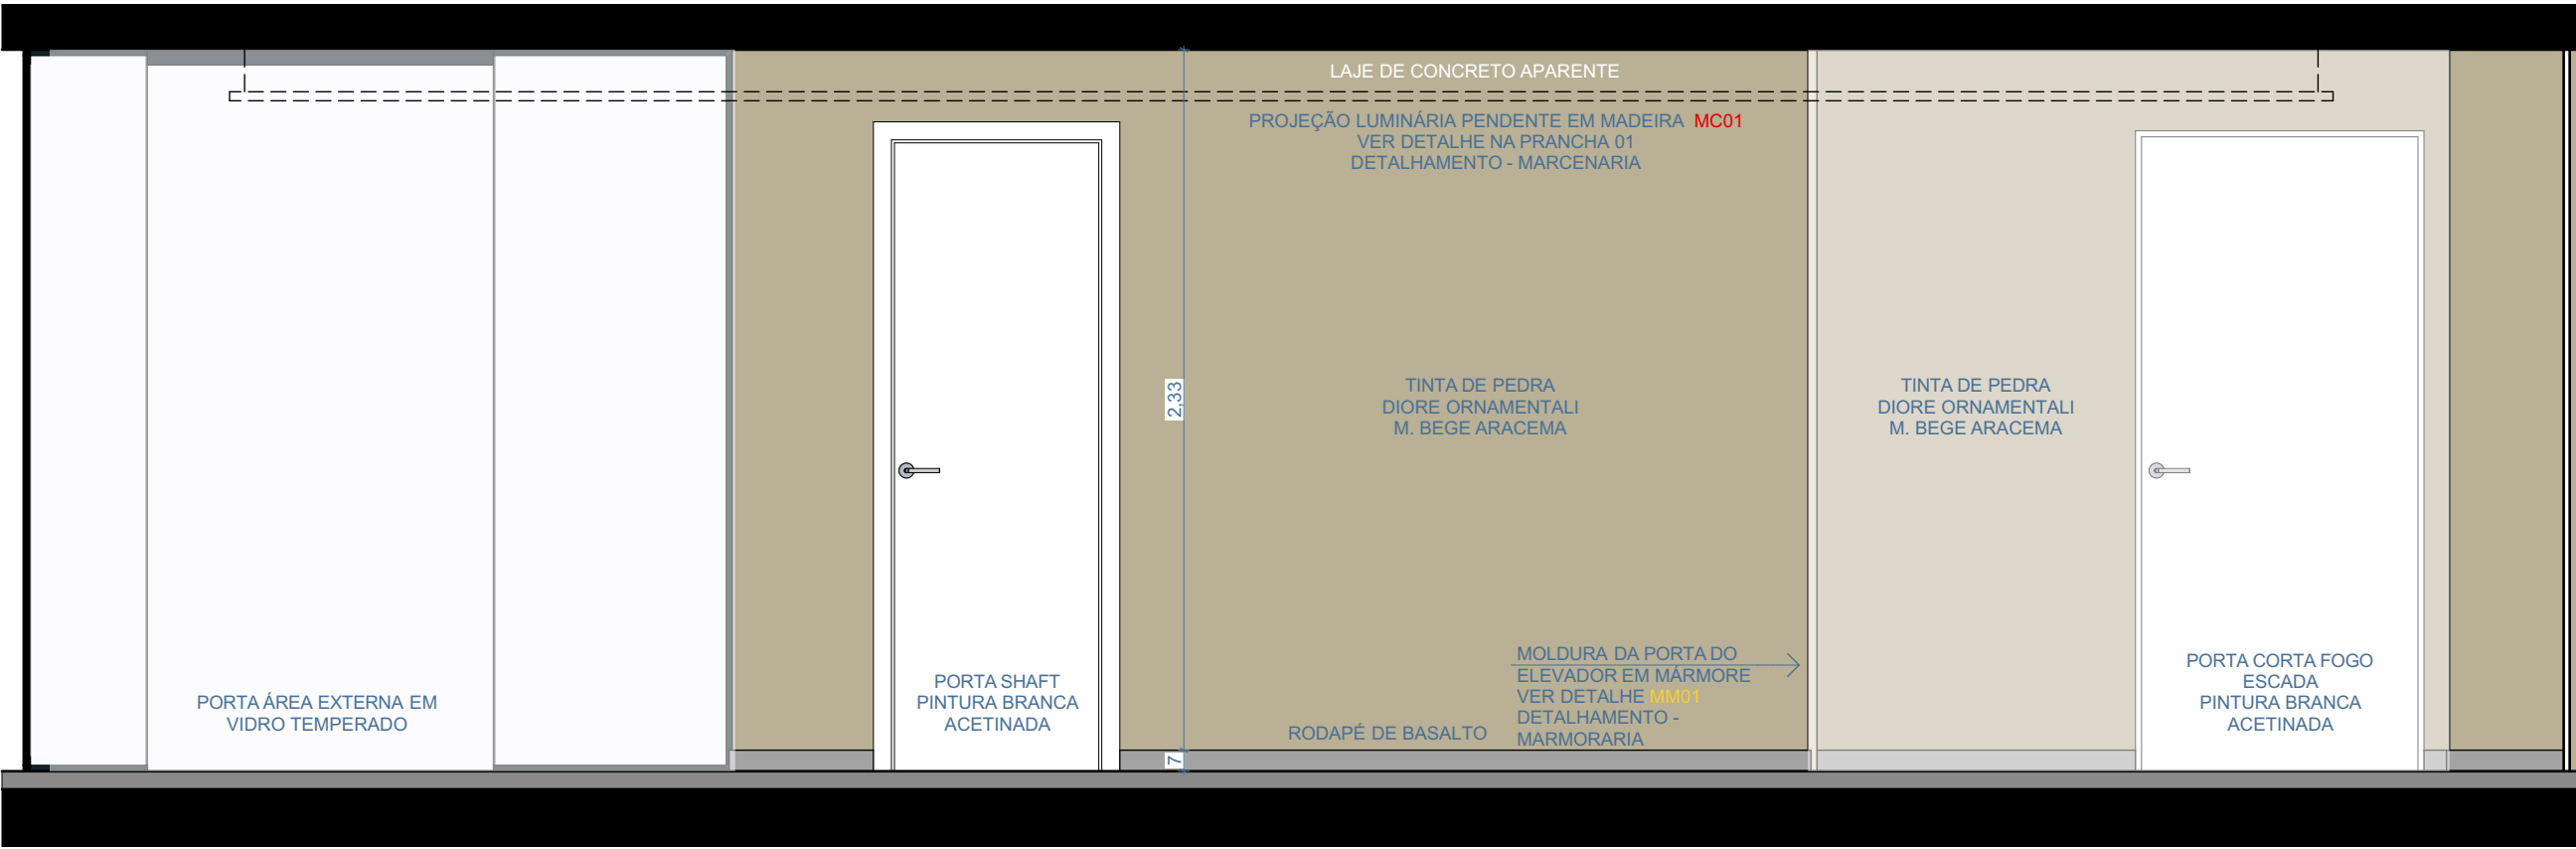

02
ESCALA 1:25

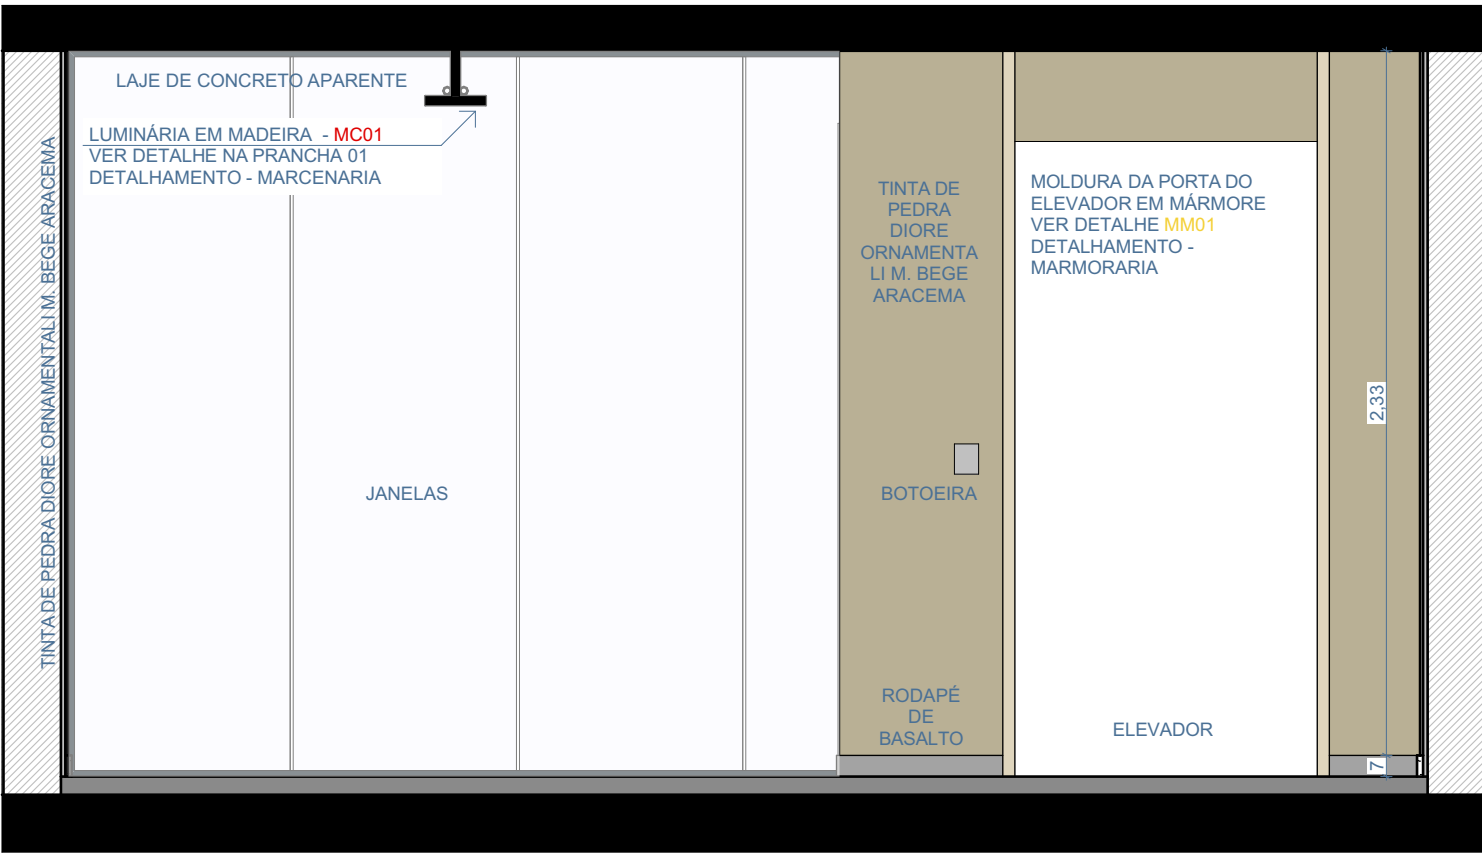

03
ESCALA 1:25

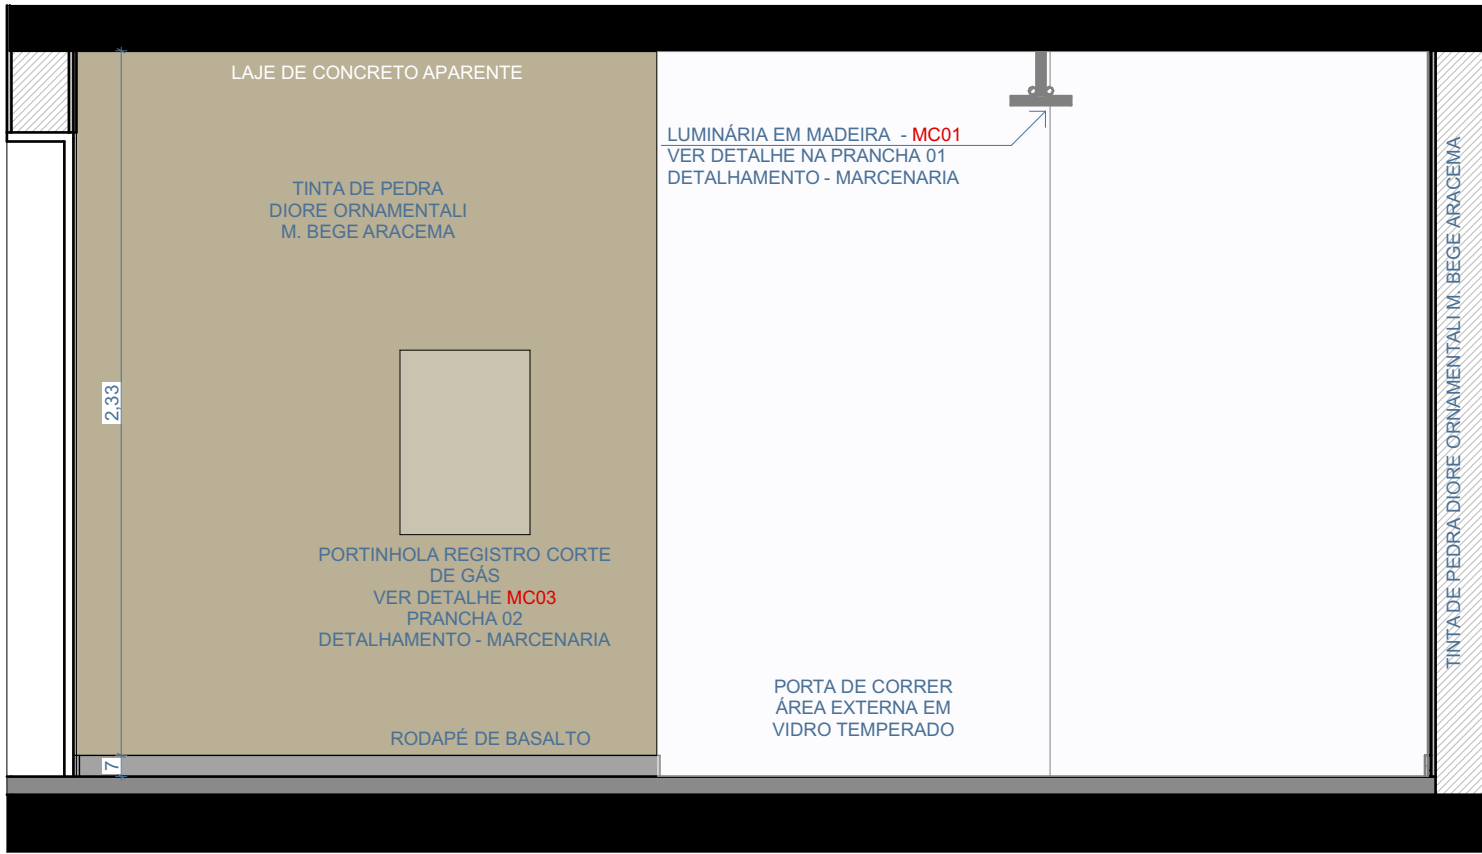

04
ESCALA 1:25



05 - VISTA DA PAREDE EXTERNA DO HALL DE ENTRADA
ESCALA 1:25

LEGENDA REVESTIMENTOS	
	PLACA DE CONCRETO 50x50
	PETT PAVE BRANCO
	PETT PAVE PRETO
	CIMENTO ALISADO
	CONCRETO VASSOURADO
	PORCELANATO 60x120
	PORCELANATO 60x60
	PORCELANATO 90x90
	PISO DE MADEIRA
	DECK DE MADEIRA
	PISO ESPORTIVO EMBORRACHADO EM PLACAS 100x100
	BASALTO RUSTICO
	BASALTO POLIDO
	PISO CIMENTÍCIO SOLARIUM 50x50
	AZULEJO 30x60 BRANCO ACETINADO RETIFICADO
	TINTA DE PEDRA DIÓRE DELICATO PRECOSA COR NATURAL
	TINTA DE PEDRA DIÓRE ORNAMENTAL MAO COR BEGE ARACEMA
	TEXTURA TERRACOR PREDIAL PRETO
	PINTURA ACRILICA PRETA - SILVINE PATATIVA
	BASALTO POLIDO
	REVESTIMENTO EM PEDRA NATURAL MOLEDO
	REVESTIMENTO EM LÂMINA FRIELO
	COMPENSADO VIROLA
	ESPELHO CRISTAL COLADO
NOTAS	
1. PILARES DA GARAGEM E MURTEAS DO ACESSO SÃO EM CONCRETO APARENTE;	
2. PAREDES INTERNAS SEM INDICAÇÃO DE REVESTIMENTO RECEBERÃO PINTURA ACRILICA COR BRANCO FOSCO;	
3. PAREDES EXTERNAS SEM INDICAÇÃO DE REVESTIMENTO RECEBERÃO PINTURA TERRACOR PEDRA BRANCA;	
4. SOL EIRAS DAS PORTAS DOS APARTAMENTOS EM PEÇA ÚNICA SEGUNDO ESPECIFICAÇÃO DO PISO DA CIRCULAÇÃO COMUM	

PROJETO ARQUITETÔNICO
MAUI

2/18

INTERIORES AMBIENTAÇÃO - SUB HALL TORRE B

ETAPA	OUZ MAUI ARQ PROJETO	A1 EST.
DATA	14/03/2025	
ESCALA	1:25, 1:50	
ENDEREÇO	Rodovia SC-406, s/n, Praia Mole, Florianópolis, Santa Catarina	
ASSINATURA:		
CLIENTE	OUZ	
	CPF/CNPJ	
ASSINATURA:		
RESPONSÁVEL:	HENRIQUE PIMONT	
	CAU A 20832-9	
DESENHO:	MAYCON PASSIG; ARTHUR ANDRADE; MIRELA MOSER	



RUA ALVES DE BRITO, 141 - SALA 701
CENTRO - FLORIANÓPOLIS - SC
CEP: 88015-440
TELEFONE: 48 30251200
CELULAR: 48 97804485
WWW.PIMONTARQUITETURA.COM.BR
CONTATO@PIMONTARQUITETURA.COM.BR