

 


01 B
ESCALA 1:25

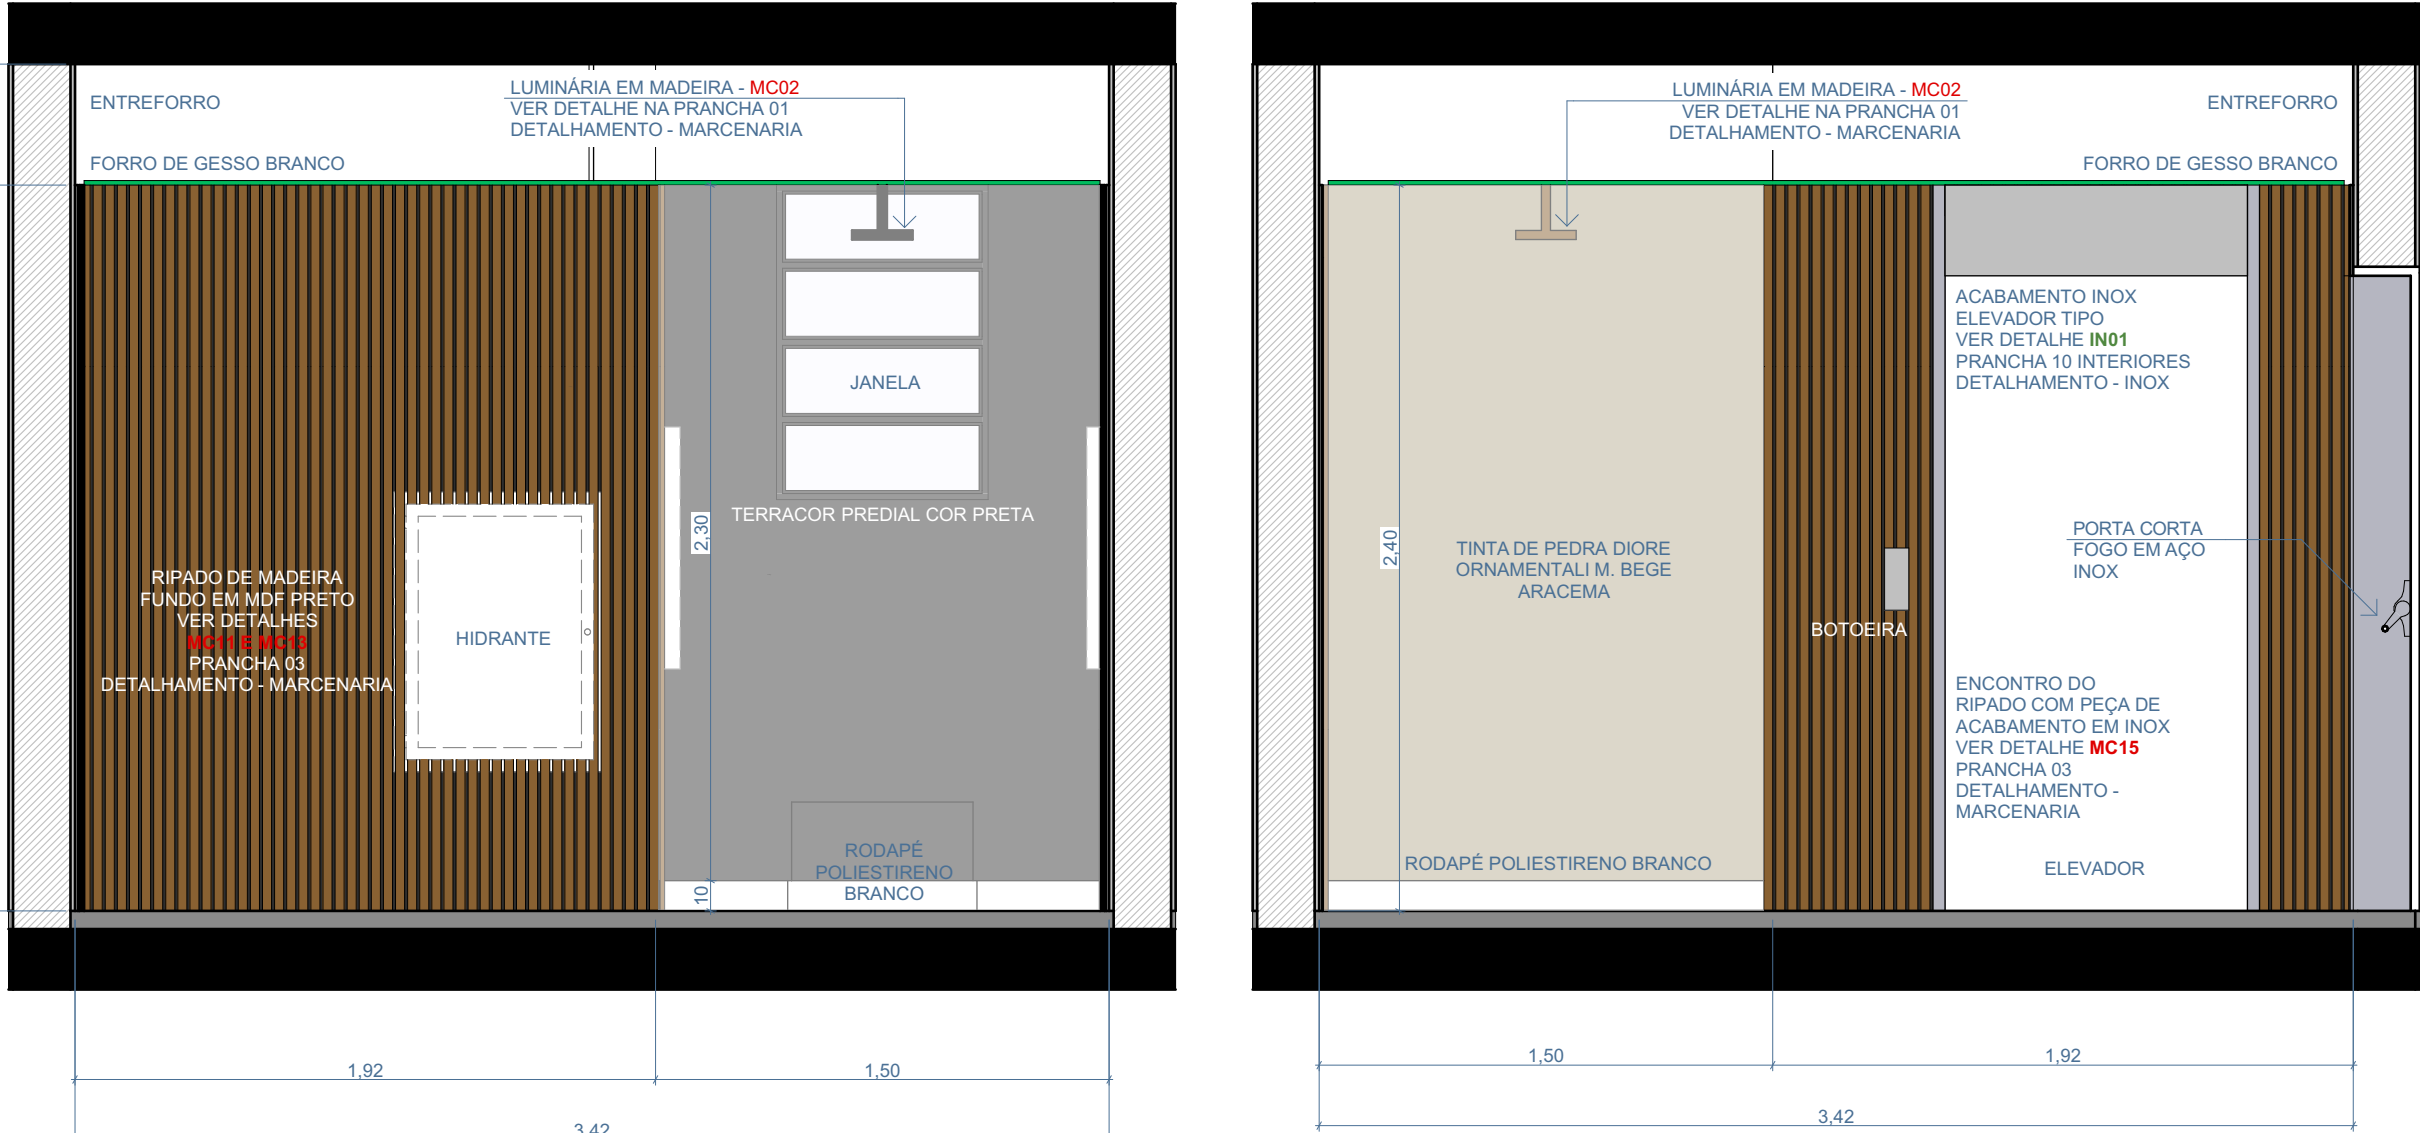

03 B
ESCALA 1:25

 

04 B
ESCALA 1:25

02 B
ESCALA 1:25

LEGENDA REVESTIMENTOS

	PLACA DE CONCRETO 50x60		AZULEJO 30x40 BRANCO ACETINADO RETIFICADO
	PETRI PAVÉ BRANCO		TINTA DE PEDRA DIÓREO
	PETRI PAVÉ PRETO		TINTA DE PEDRA DIÓREO NATURAL
	CIMENTO ALUSADO		TINTA DE PEDRA DIÓREO ORNAMENTAL
	CONCRETO VASSOURADO		TEXTURA TERRACOTA PREDIAL
	PORCELANATO 60x120		PINTURA ACRÍLICA PRETA - SÚPER PATIVATA
	PORCELANATO 80x80		BASALTO POLIDO
	PORCELANATO 90x90		REVESTIMENTO EM PEDRA NATURAL
	PISO DE MADEIRA		COMPENSADO VIRADO
	DECK DE MADEIRA		ESPELHO CRISTAL COLADO
	PISO ESPORTIVO EMBORRACHADO EM PLACAS 50x50		
	BASALTO RÚSTICO		
	BASALTO POLIDO		
	PISO CIMENTÍCIO SOLARIUM 50x50		

NOTAS

1. PLÁCIDAS DA GARAGEM E MURETAS DO ACESSO SÃO EM CONCRETO APARENTE.
2. PAREDES INTERNAS SEM INDICAÇÃO DE REVESTIMENTO RECEBERÃO PINTURA ACRÍLICA COR BRANCA FOSCO.
3. PAREDES EXTERNAS SEM INDICAÇÃO DE REVESTIMENTO RECEBERÃO PINTURA TERRACOTA PREDIAL BRANCA.
4. SOLERA DAS PORTAS DOS APARTAMENTOS EM PEÇA ÚNICA SEQUENDO ESPECIFICAÇÃO DO PISO DA CIRCULAÇÃO COMUM.

PROJETO ARQUITETÔNICO

MAUI

INTERIORES AMBIENTAÇÃO - PAV CIRCULAÇÃO

TORRE B

5/18

ETAPA	OUZ MAULARQ PROJETO EXECUTIVO AMBIENTAÇÃO	A1 EST.
DATA	14/03/2025	
ESCALA	1:25, 1:50	
ENDEREÇO	Rodovia SC-406, s/n, Praia Mole, Florianópolis, Santa Catarina	
ASSINATURA:	CLIENTE	
ASSINATURA:	RESPONSÁVEL:	
RESPONSÁVEL:	HENRIQUE PIMONT	CAU A 20832-9
DESENHO:	MAYCON PASSIG; ARTHUR ANDRADE; MIRELA MOSER	

PIMONT
ARQUITETURA

RUA ALVES DE MELLO, 141 - SALA 701
CENTRO - FLORIANÓPOLIS - SC
CEP: 88015-440
TELEFONE: 48 30251200
CELULAR: 48 97004445
WWW.PIMONTARQUITETURA.COM.BR
CONTATO@PIMONTARQUITETURA.COM.BR