



ROOFTOP - TERRAÇO E CIRCULAÇÃO LADO LAGOA E CIRCULAÇÃO INTERMEDIÁRIA

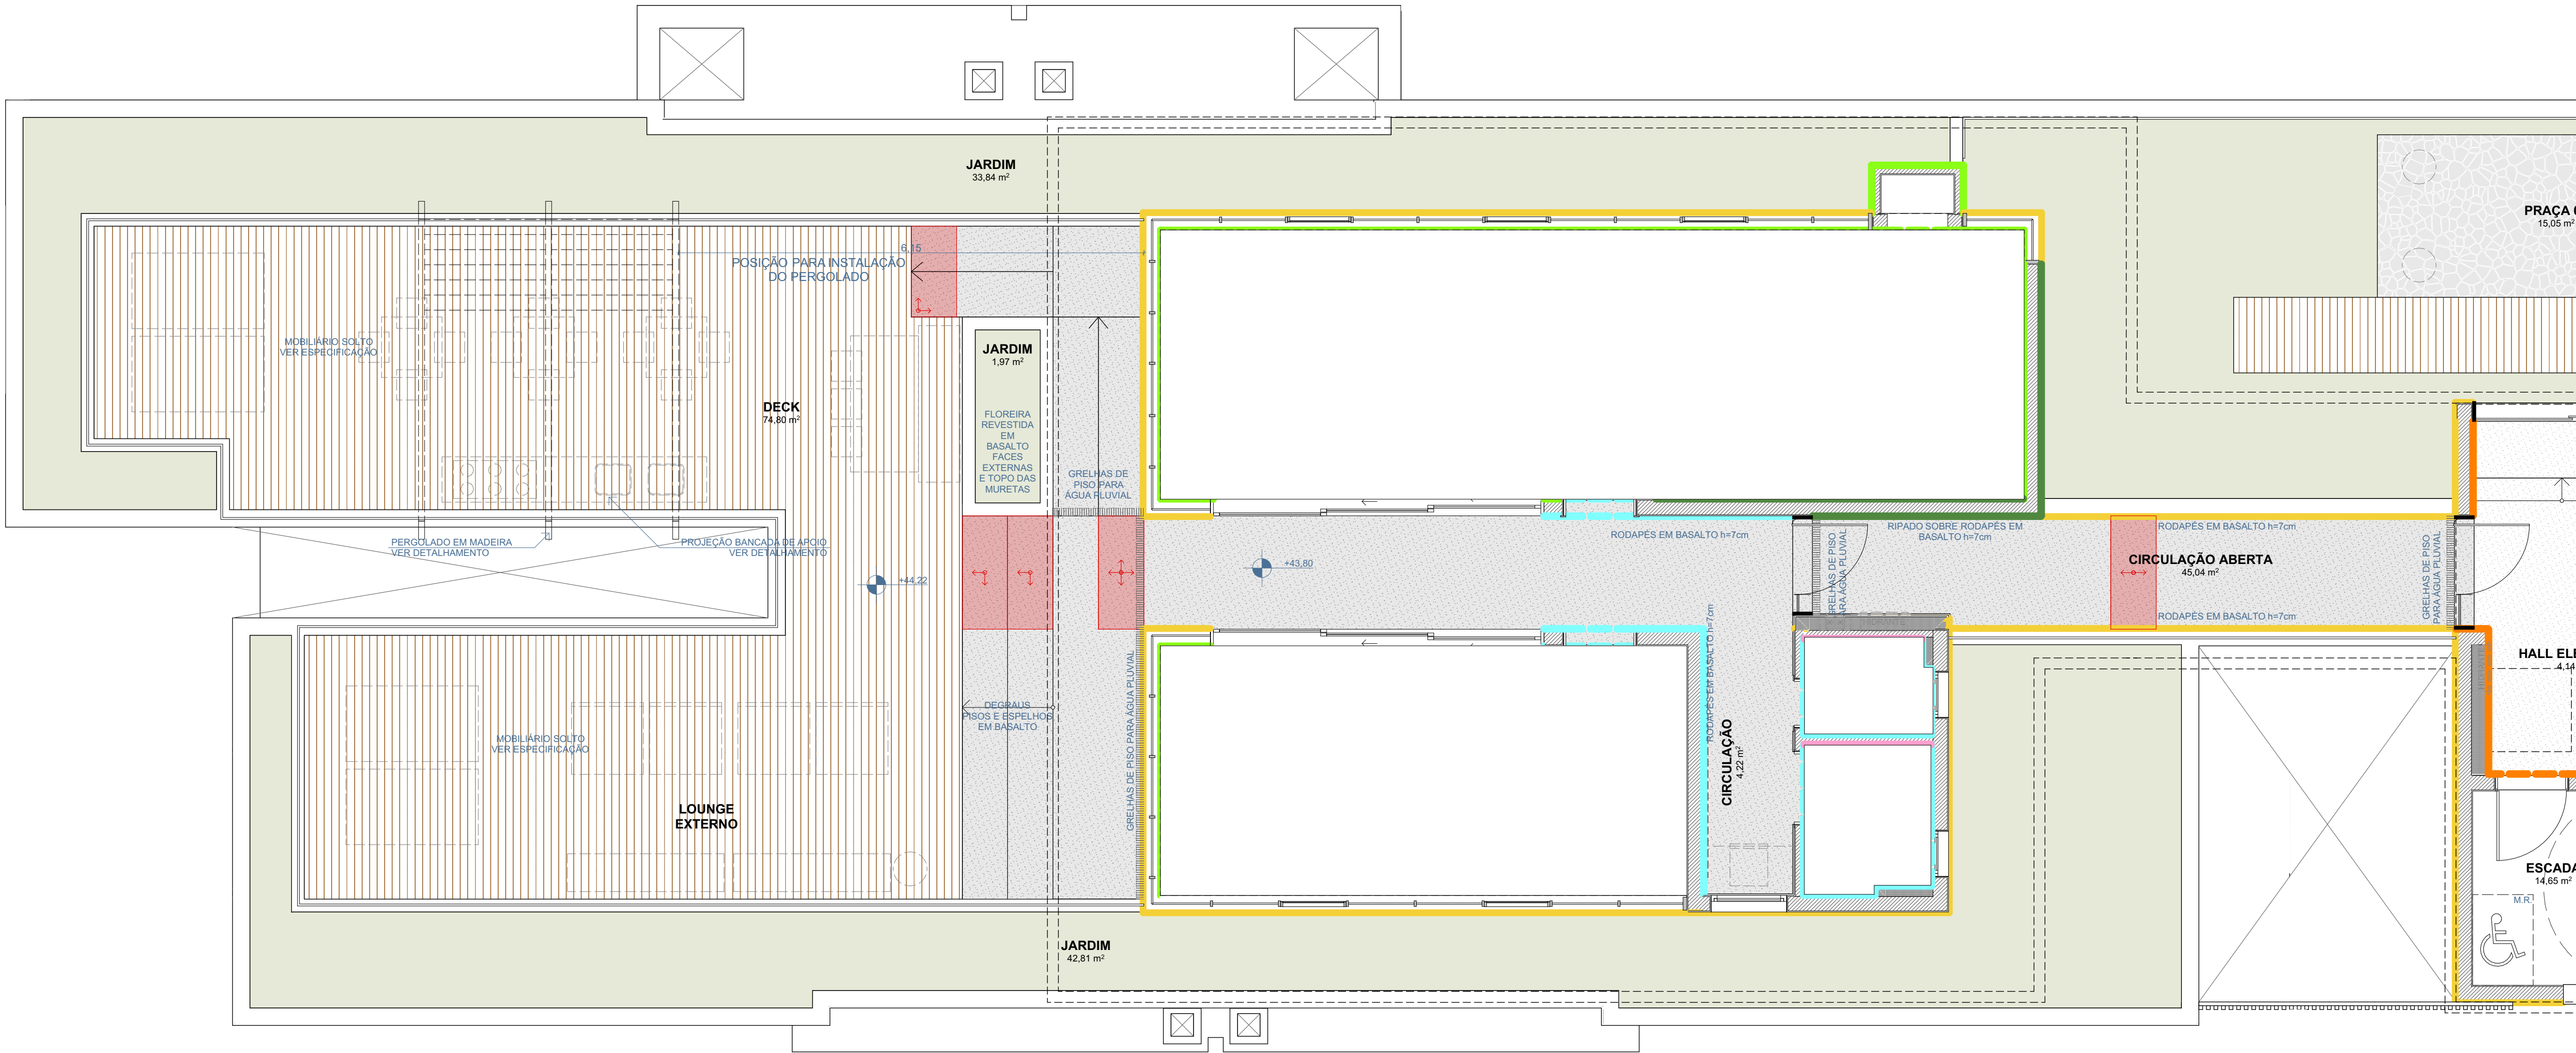

PLANTA BAIXA TERRAÇO LAGOA
ESCALA 1:50

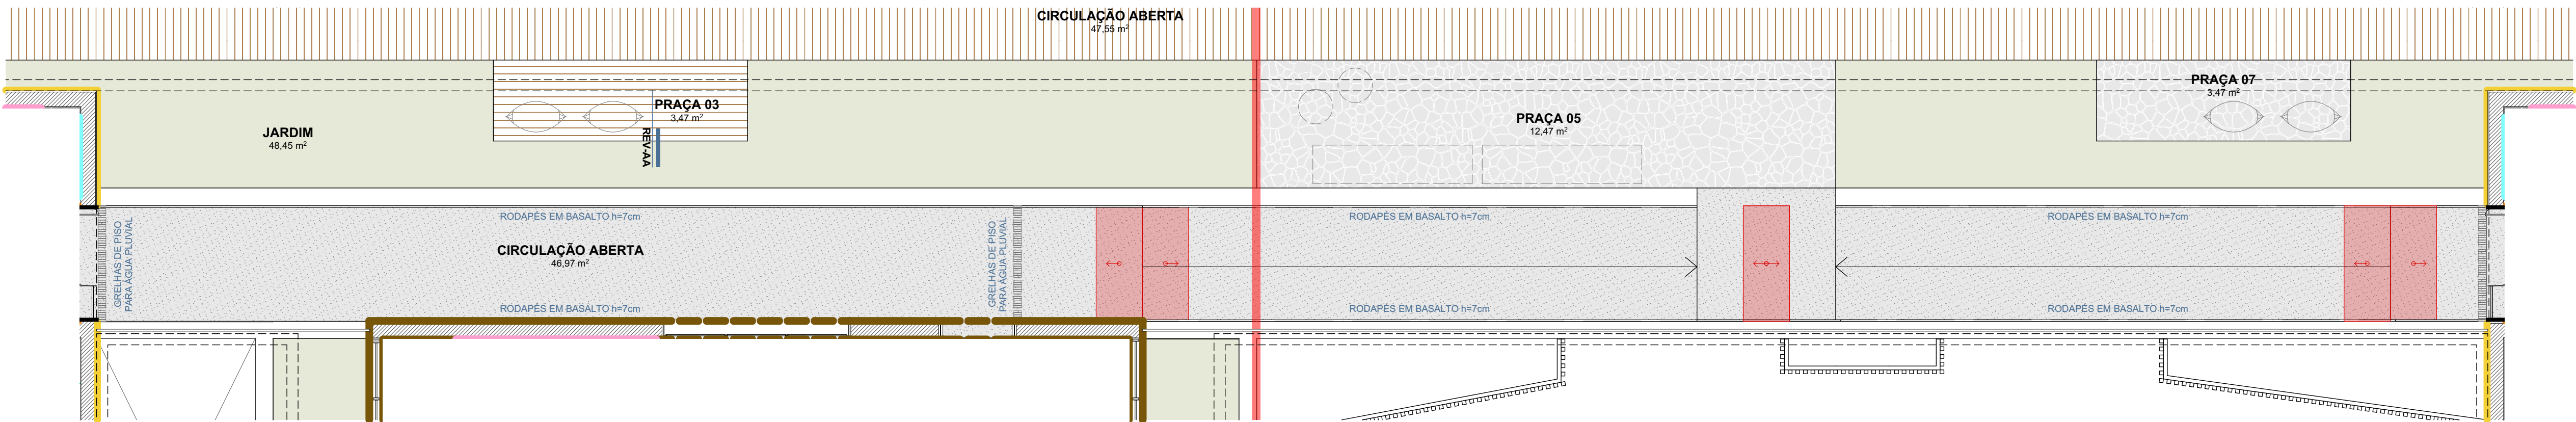

PLANTA BAIXA CIRCULAÇÃO INTERMEDIÁRIA
ESCALA 1:50

LEGENDA REVESTIMENTOS



PLACA DE CONCRETO 50x50



PETIT PAVÉ BRANCO



PETIT PAVÉ PRETO



CIMENTO ALISADO



CONCRETO VASSOURADO



PORCELANATO 60x120



PORCELANATO 60x60



PORCELANATO 90x90



PISO DE MADEIRA



DECK DE MADEIRA



PISO ESPORTIVO EMBORRACHADO EM PLACAS 100x100



BASALTO RÚSTICO



BASALTO POLIDO



PISO CIMENTÍCIO SOLARIUM 50x50



AZULEJO 30x60 BRANCO ACETINADO RETIFICADO



TINTA DE PEDRA DIORE DELICATO PRECIOSA COR NATURAL



TINTA DE PEDRA DIORE ORNAMENTAL MAXI COR BEGE ARACEMA



TEXTURA TERRACOR PREDIAL PRETO



PINTURA ACRÍLICA PRETA - SUVINIL PATATIVA



BASALTO POLIDO



REVESTIMENTO EM PEDRA NATURAL MOLEDO



REVESTIMENTO EM LÂMINA FREIJÓ



COMPENSADO VIROLA



ESPELHO CRISTAL COLADO

NOTAS

1. PILARES DA GARAGEM E MURETAS DO ACESSO SÃO EM CONCRETO APARENTE.

2. PAREDES INTERNAS SEM INDICAÇÃO DE REVESTIMENTO RECEBERÃO PINTURA ACRÍLICA COR BRANCO FOSCO.

3. PAREDES EXTERNAS SEM INDICAÇÃO DE REVESTIMENTO RECEBERÃO PINTURA TERRACOR PREDIAL BRANCO.

4. SOLEIRAS DAS PORTAS DOS APARTAMENTOS EM PEÇA ÚNICA SEGUNDO ESPECIFICAÇÃO DO PISO DA CIRCULAÇÃO COMUM.

PROJETO ARQUITETÔNICO
MAUI
INTERIORES AMBIENTAÇÃO - RTOP TERRAÇO
LAGOA / CIRCULAÇÃO

16/18

ETAPA	OUZ_MAU_ARQ_PROJETO EXECUTIVO AMBIENTAÇÃO	A1 EST.
DATA	14/03/2025	
ESCALA	1:50	
ENDEREÇO	Rodovia SC-406, s/n, Praia Mole, Florianópolis, Santa Catarina	
ASSINATURA:		
CLIENTE	OUZ CPF/CNPJ:	
ASSINATURA:		
RESPONSÁVEL:	HENRIQUE PIMONT CAU A 20832-9	
DESENHO:	MAYCON PASSIG; ARTHUR ANDRADE; MIRELA MOSER	