



MC22 | BANCADAS DO ESPAÇO GOURMET


MDF PRETO ÉBANO CHESS (ARAUCO)
PUXADORES LINEARES EURO ZEN PRETOS

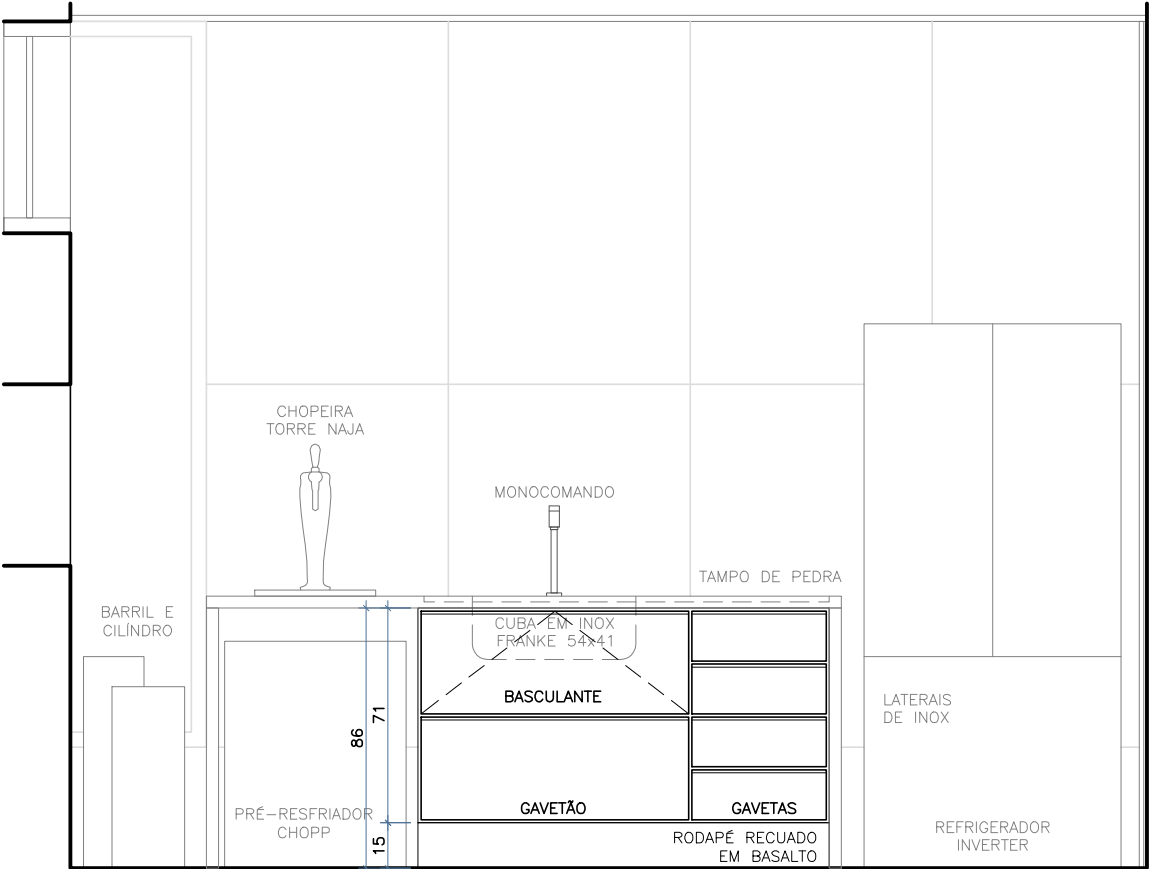


VISTA FRONTAL - BANCADA

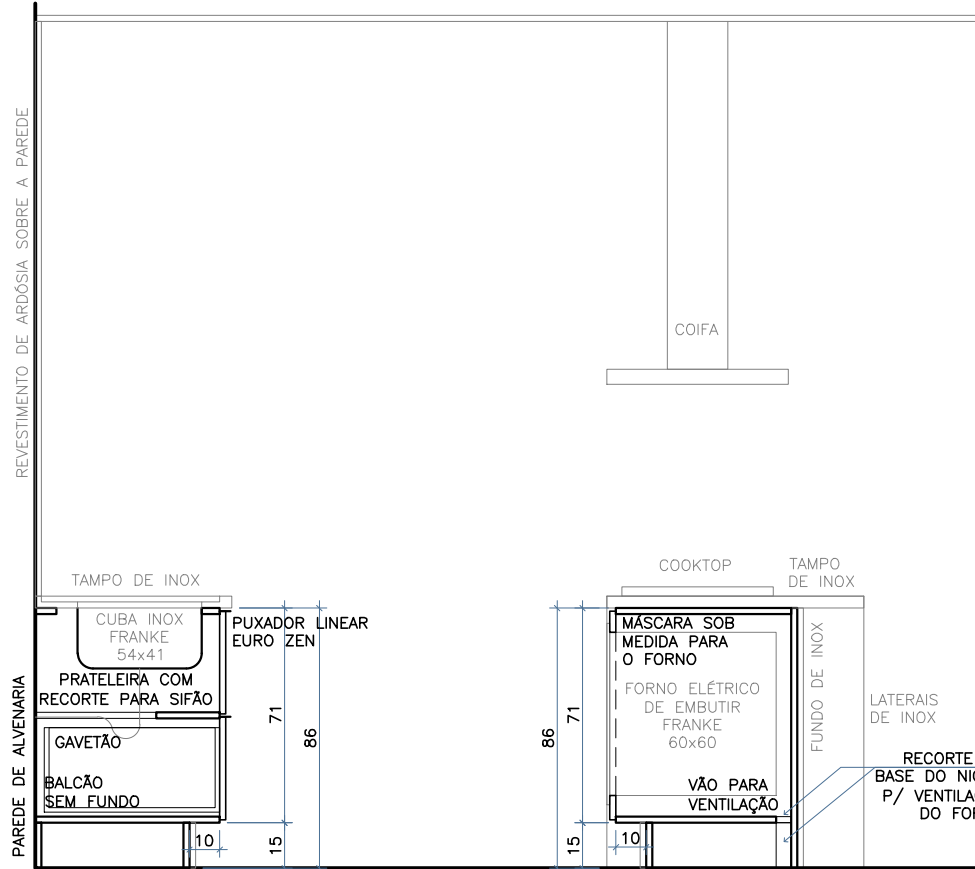


CORTE

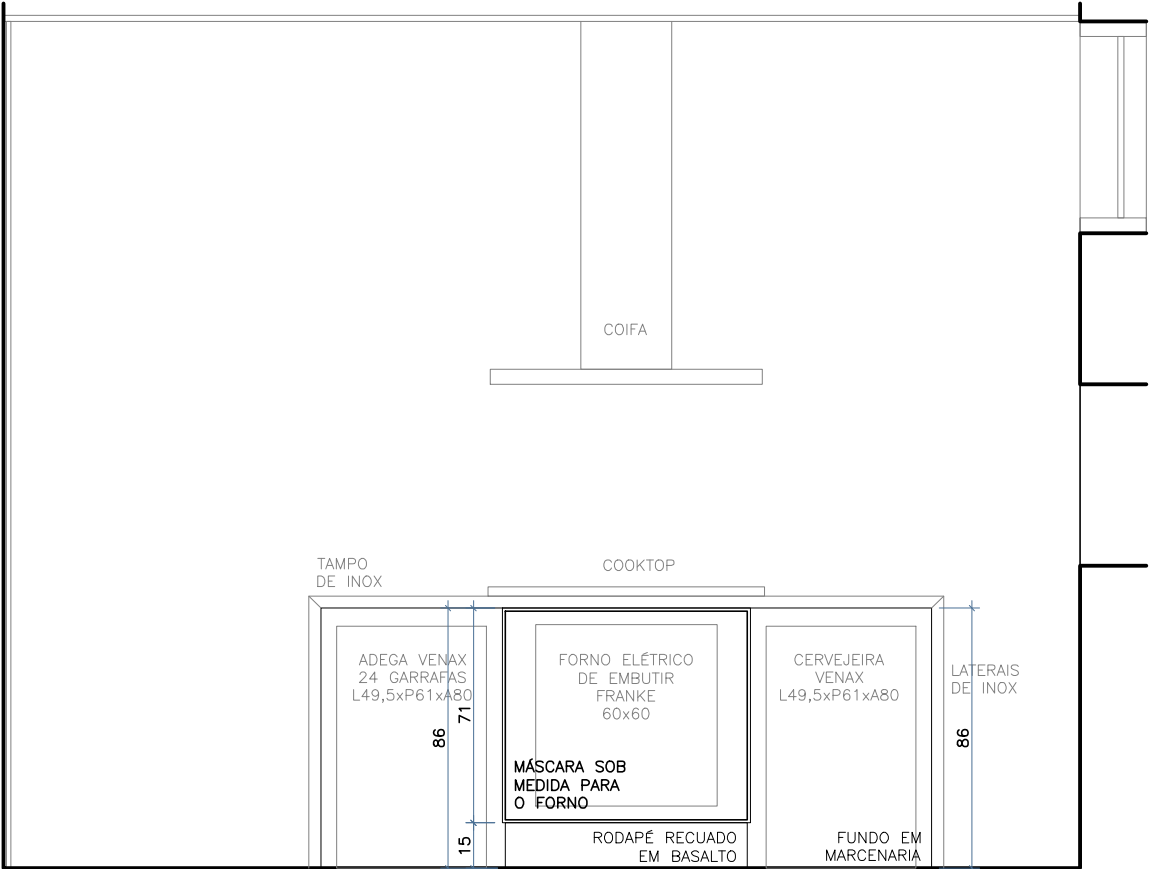

VISTA FRONTAL - ILHA

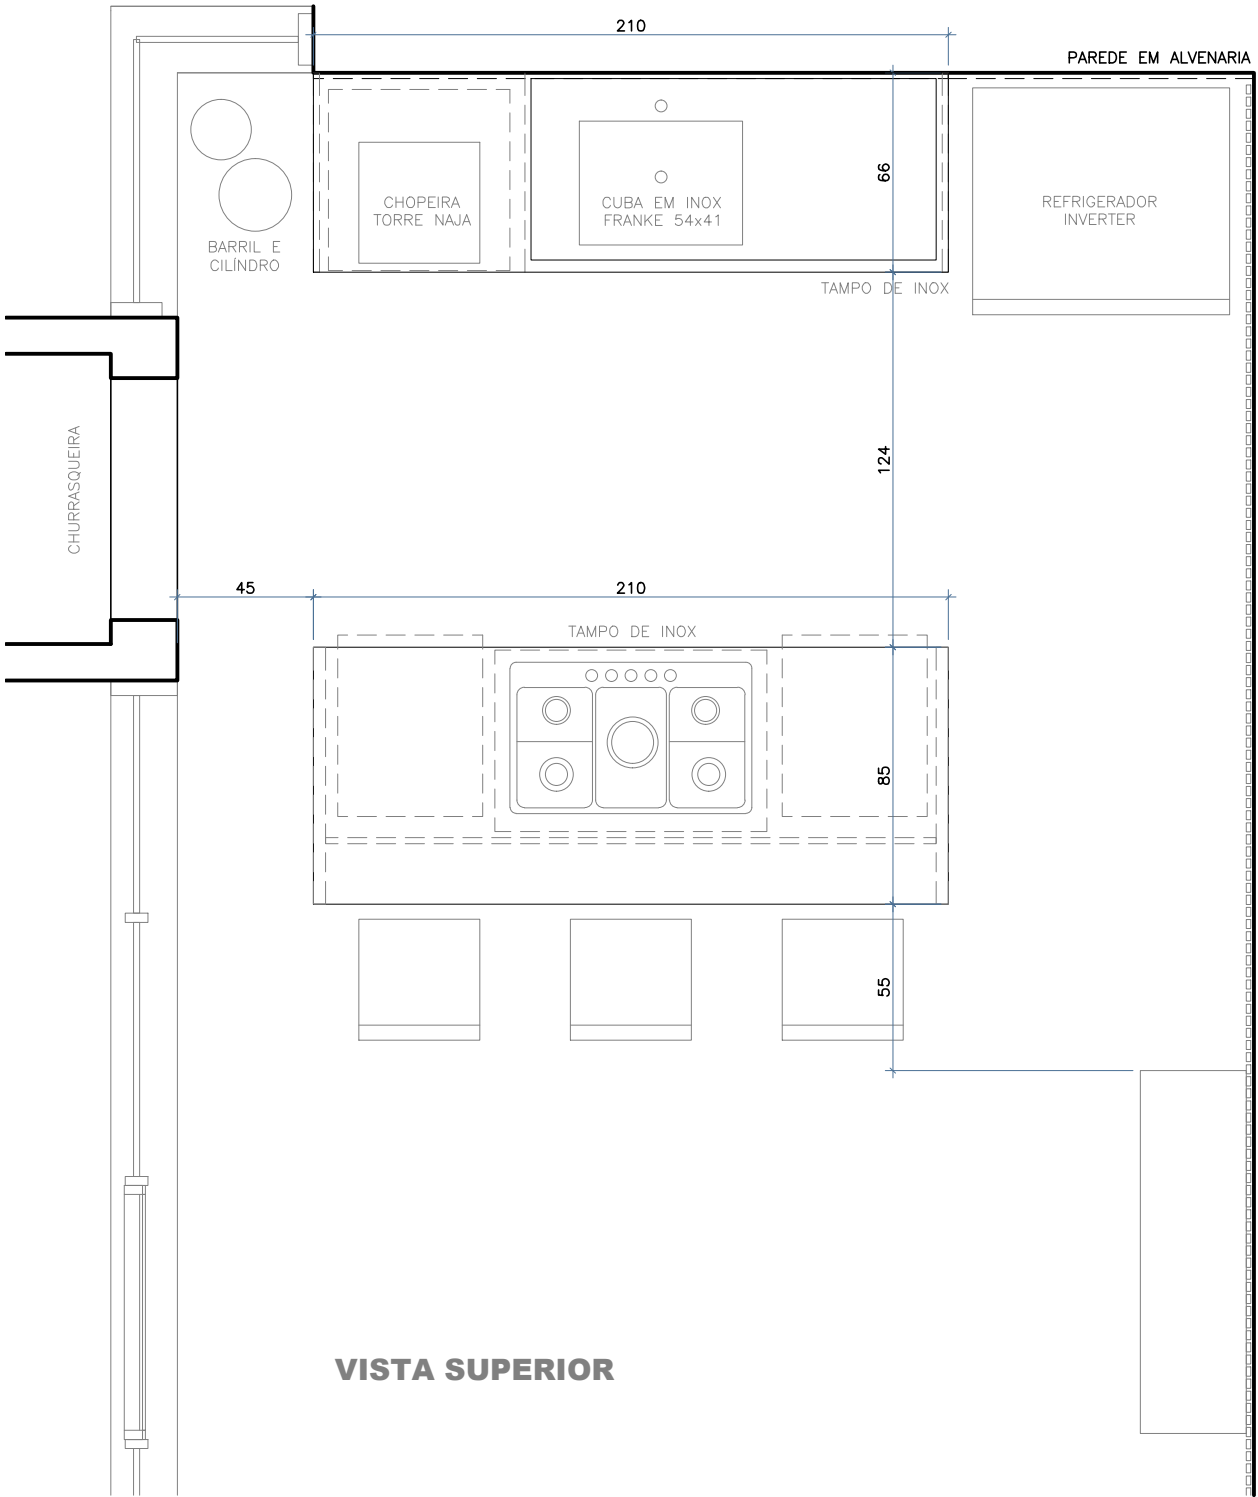


VISTA SUPERIOR

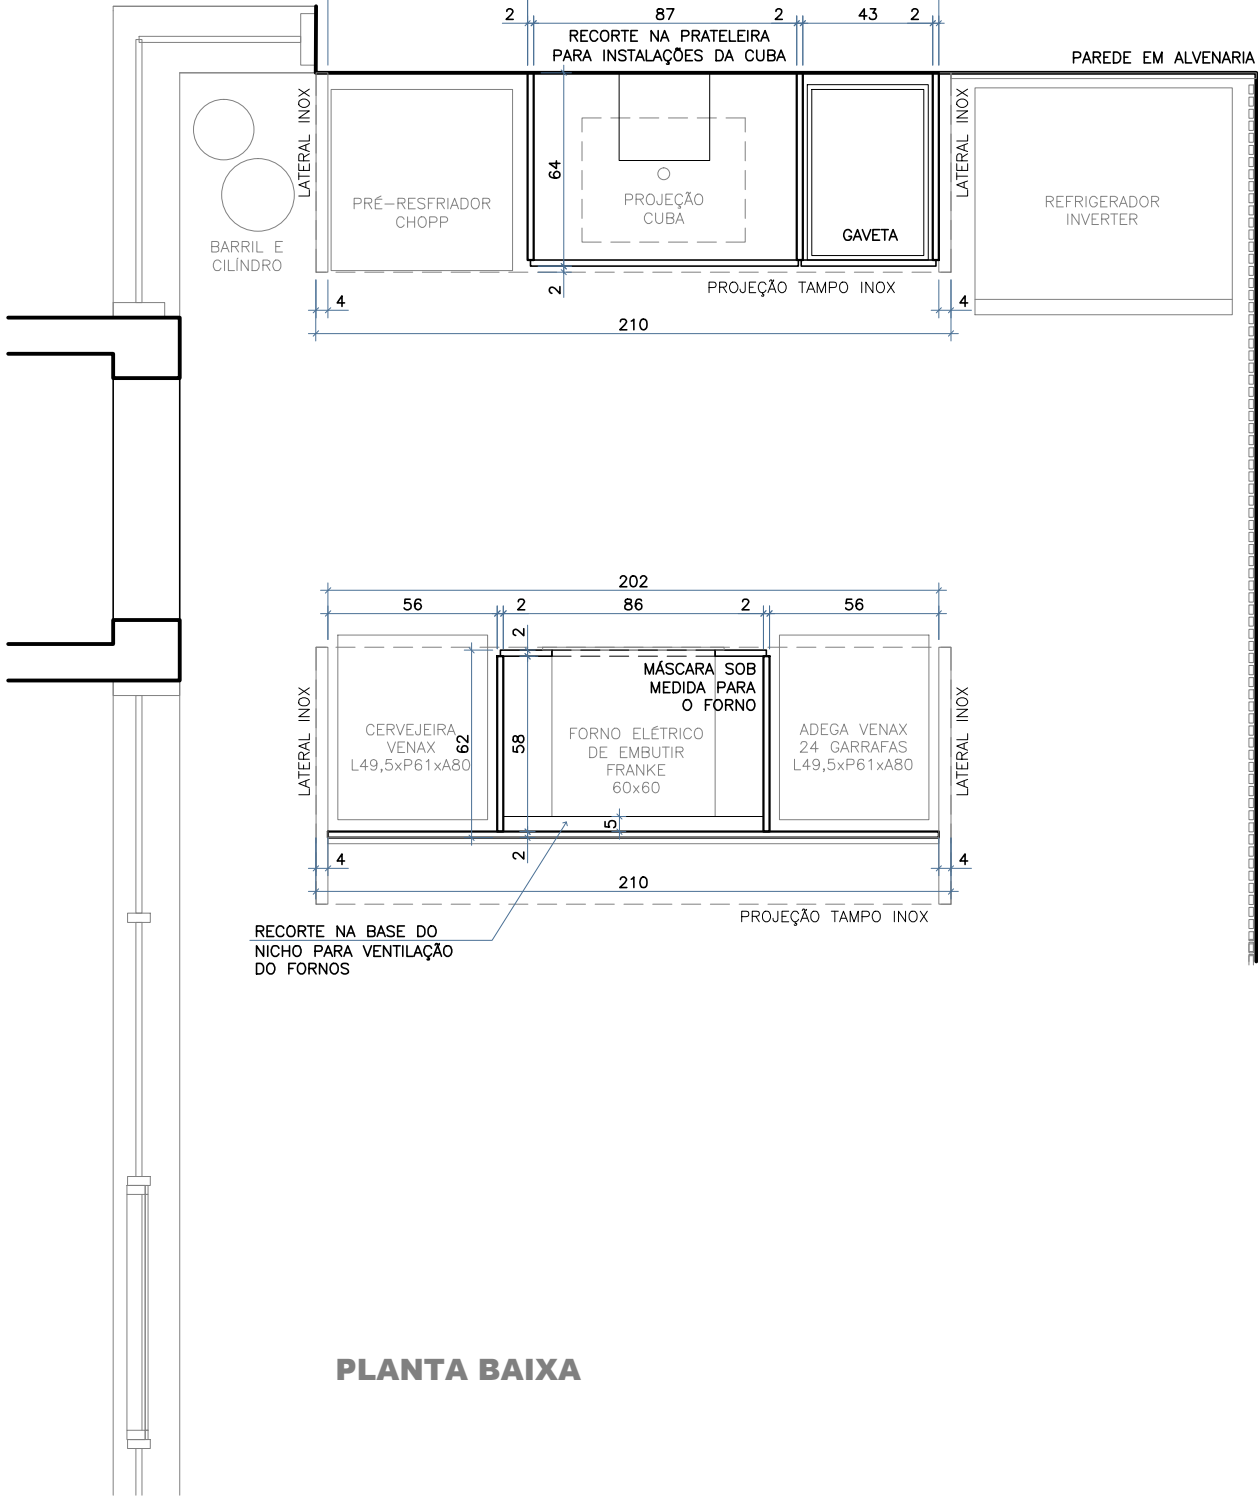


PLANTA BAIXA

MC23 | ARMÁRIO LOUÇEIRO


MDF PRETO ÉBANO CHESS (ARAUCO)
PUXADORES LINEARES EURO ZEN PRETOS

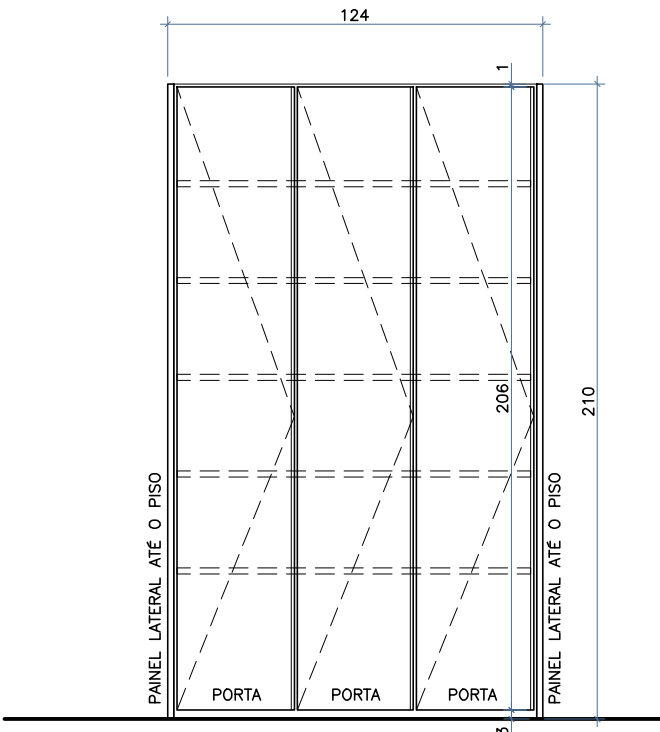

VISTA FRONTAL

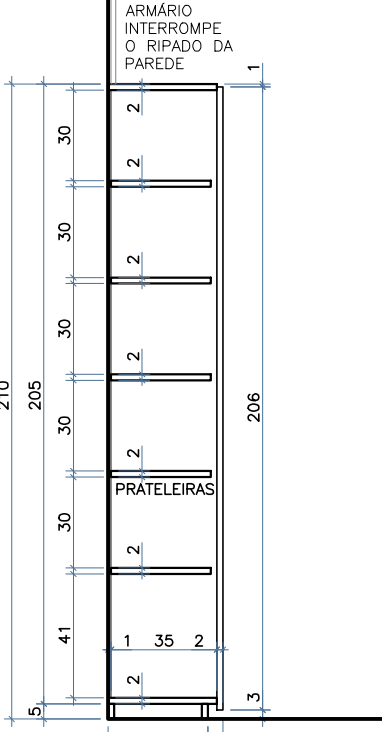

CORTE

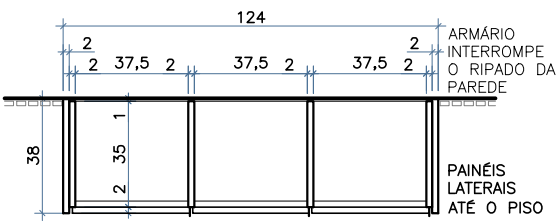

PLANTA BAIXA