



MC18 | RECORTE DO HIDRANTE E REGISTRO DE CORTE DO GÁS


RIPADO DE MADEIRA MACIÇA SOBRE PAINEL DE MDF PRETO RESISTENTE À UMIDADE (ULTRA)
02 UNIDADES

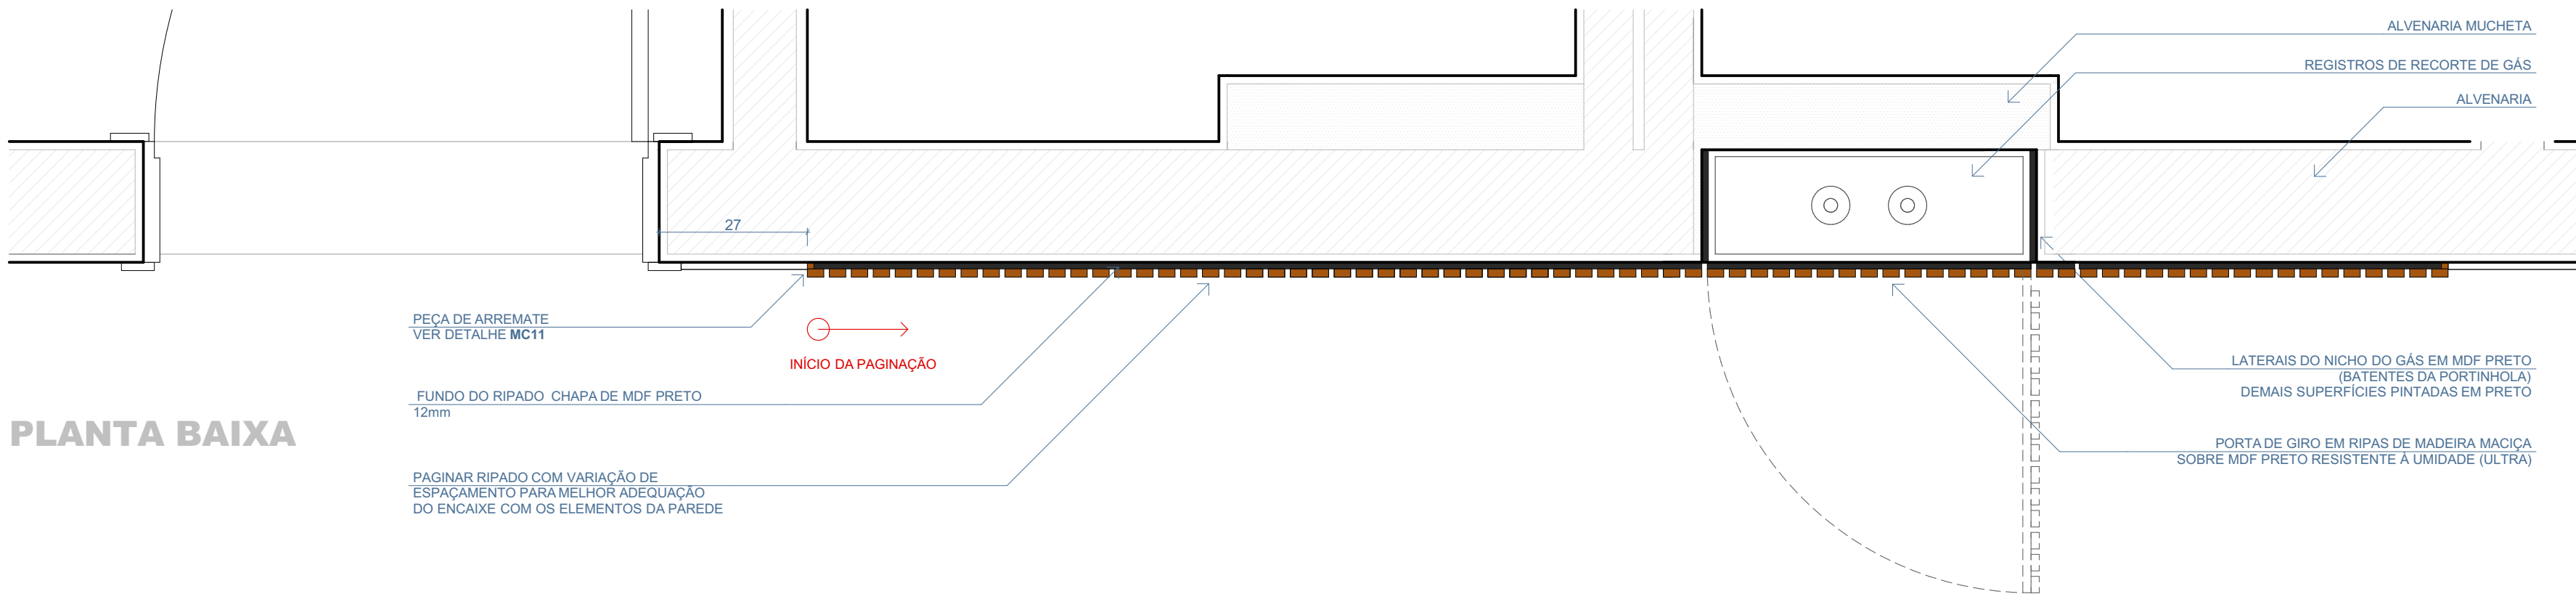

PLANTA BAIXA

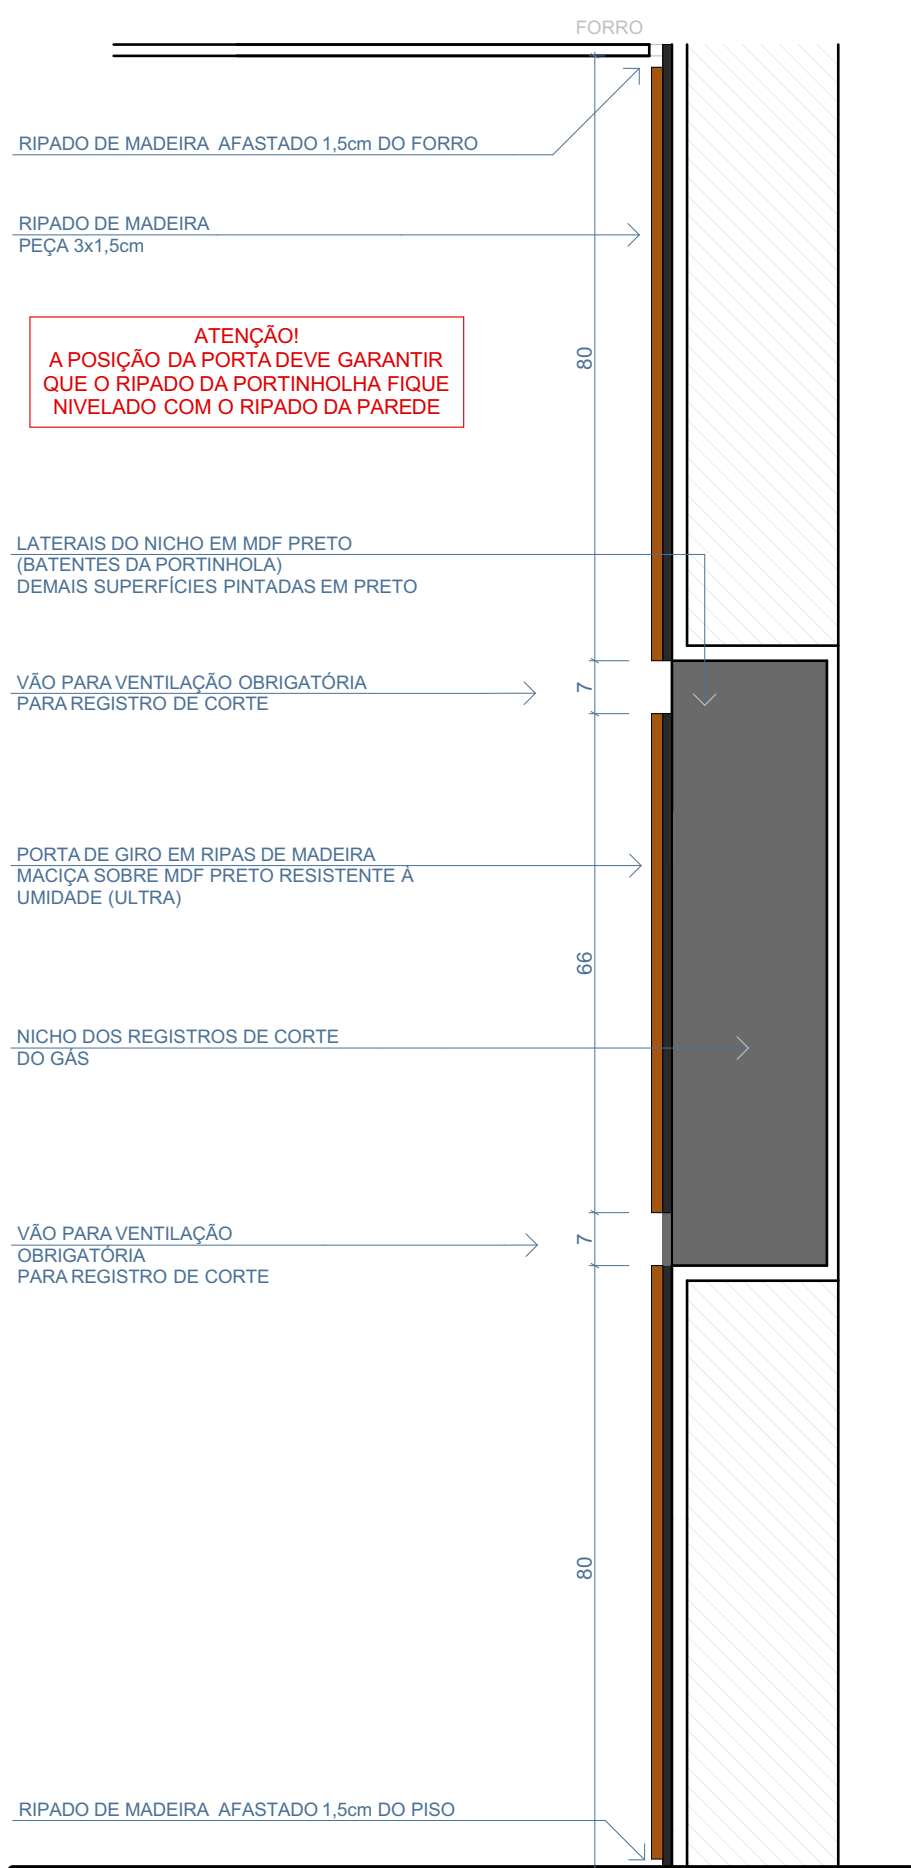


CORTE

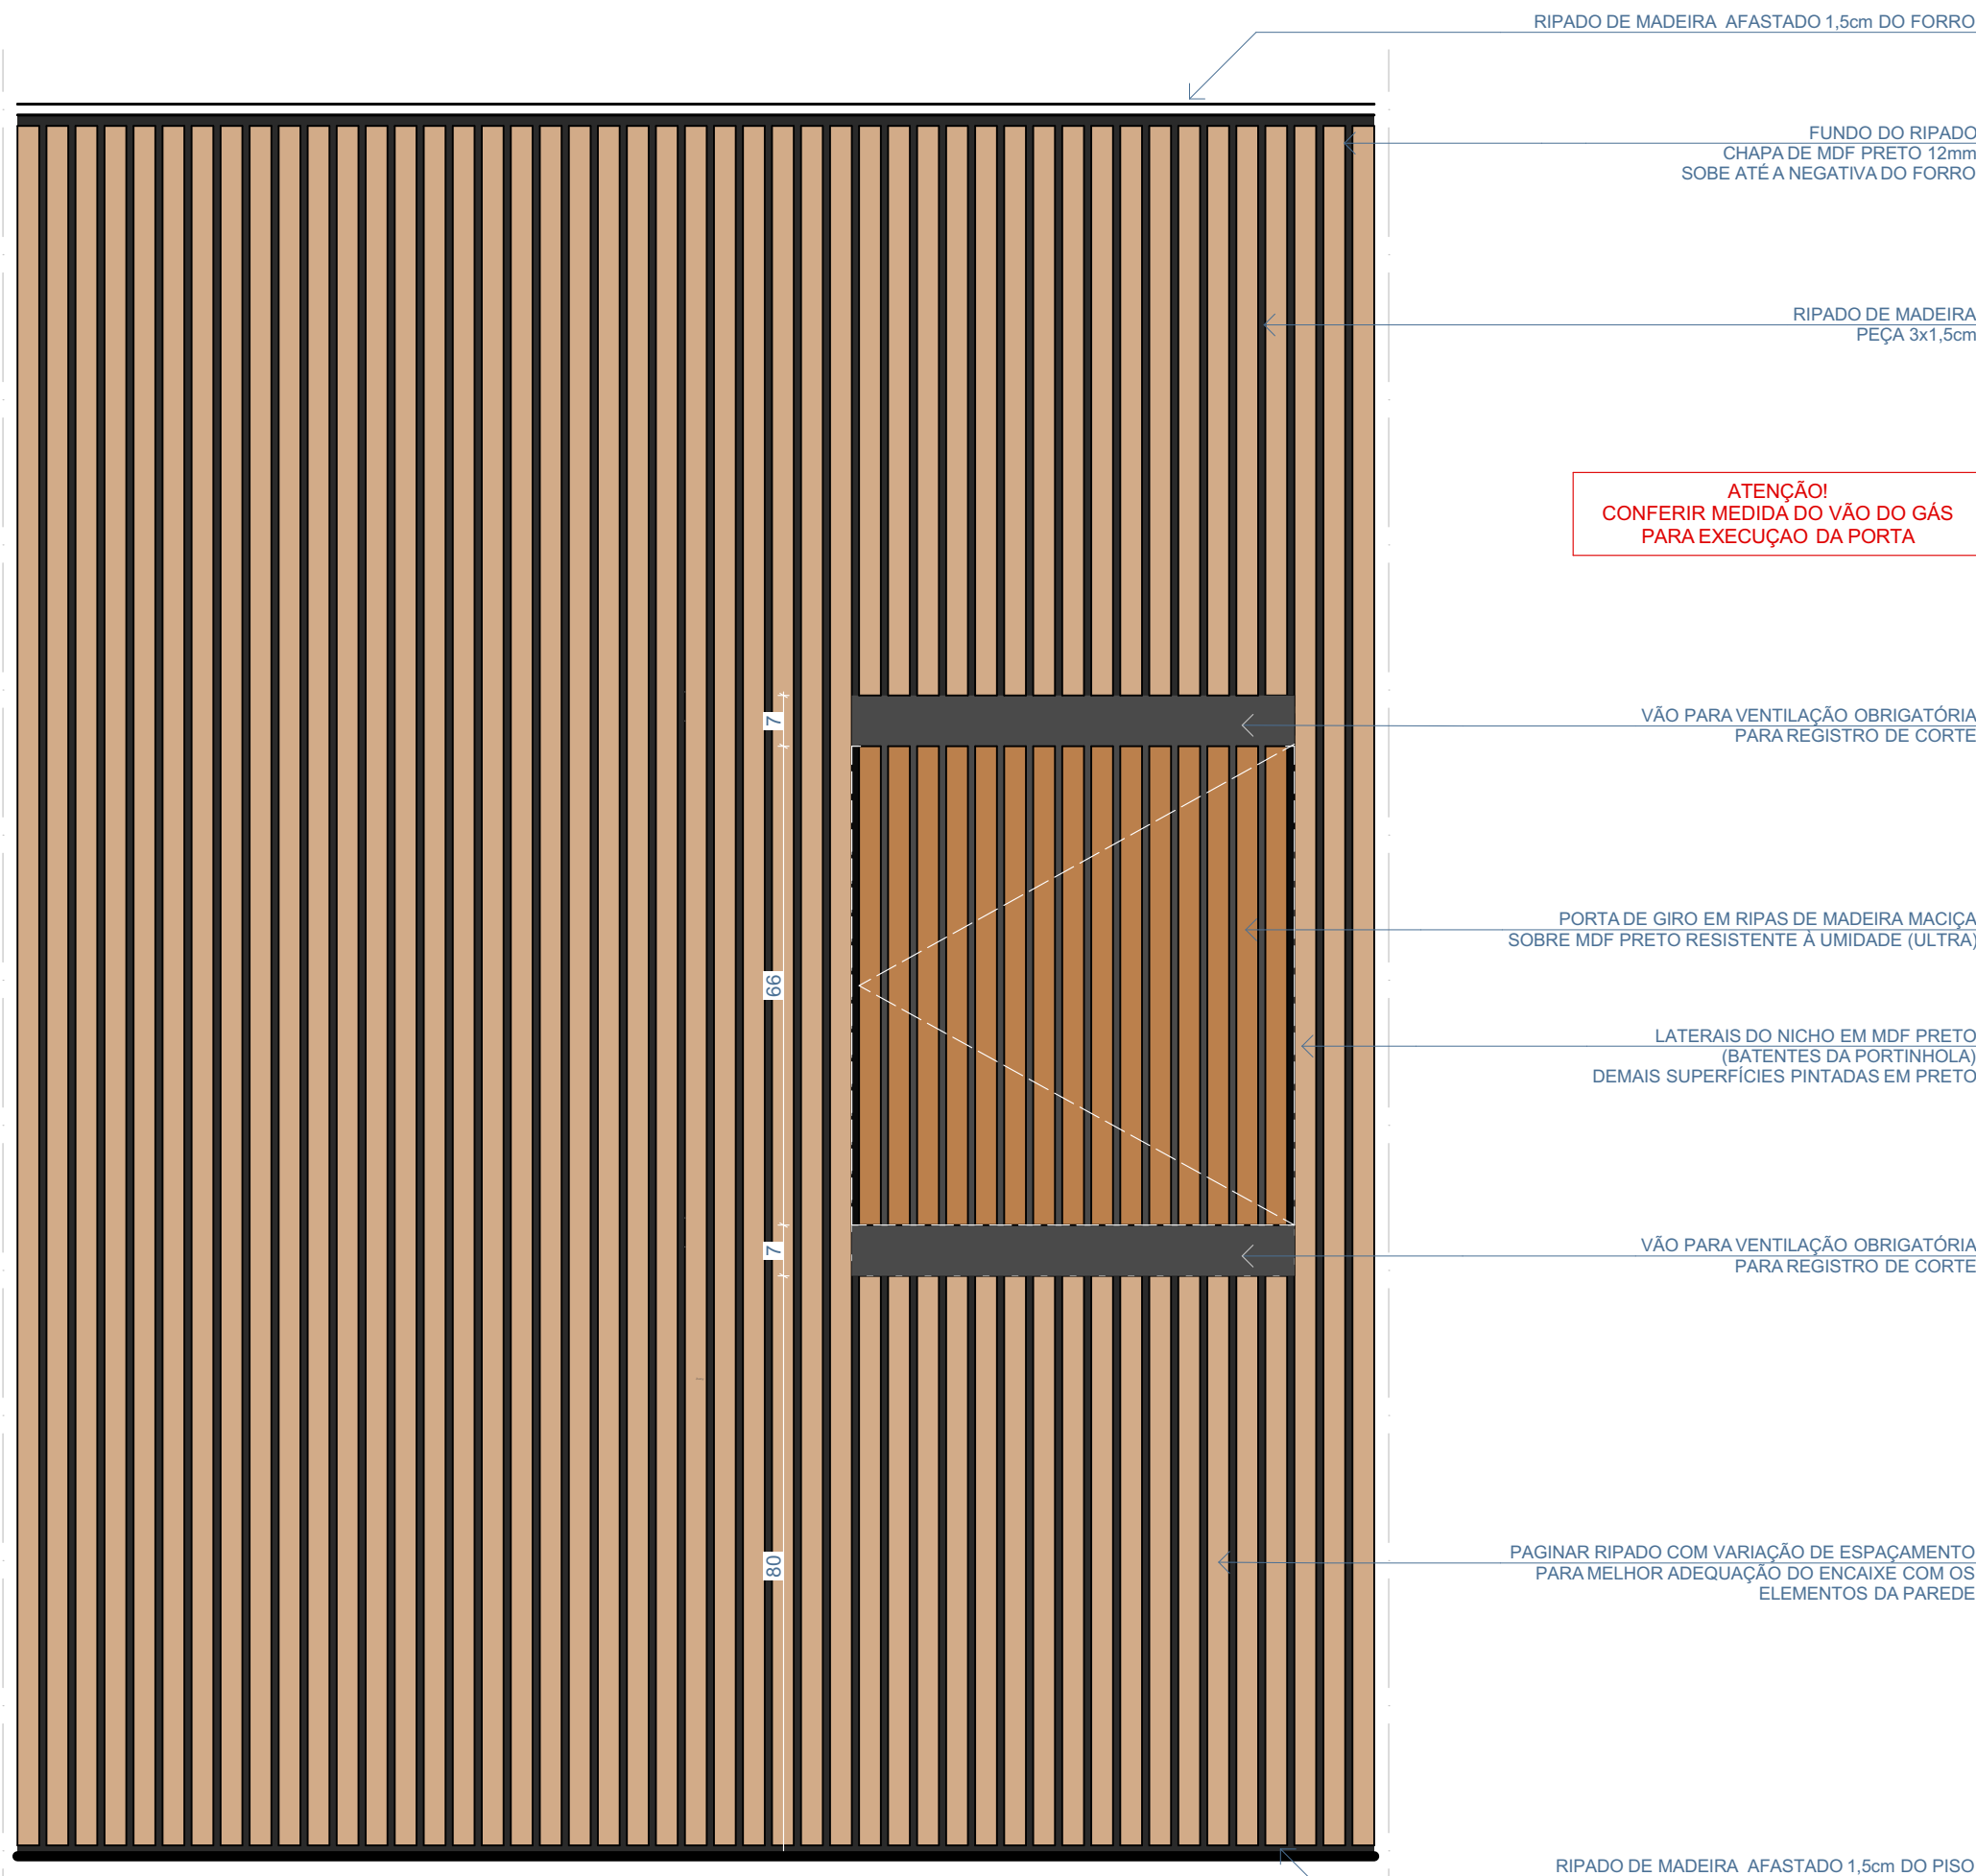


VISTA FRONTAL

MC11 | DETALHE DO PAINEL RIPADO

RIPADO DE MADEIRA MACIÇA SOBRE PAINEL DE MDF PRETO RESISTENTE À UMIDADE (ULTRA)

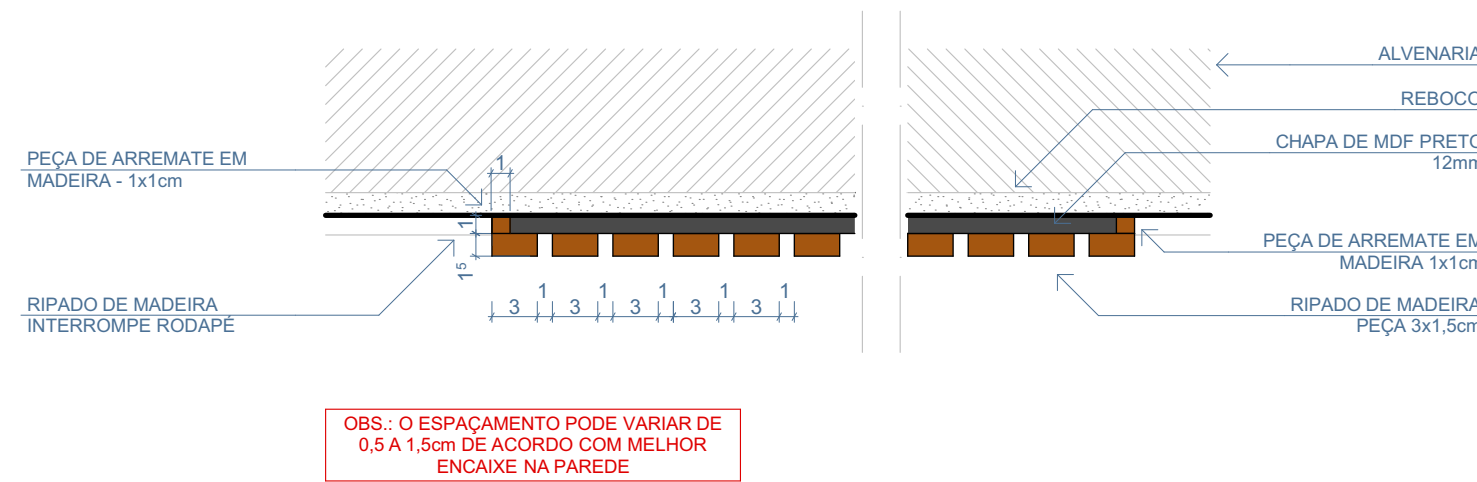

PLANTA BAIXA

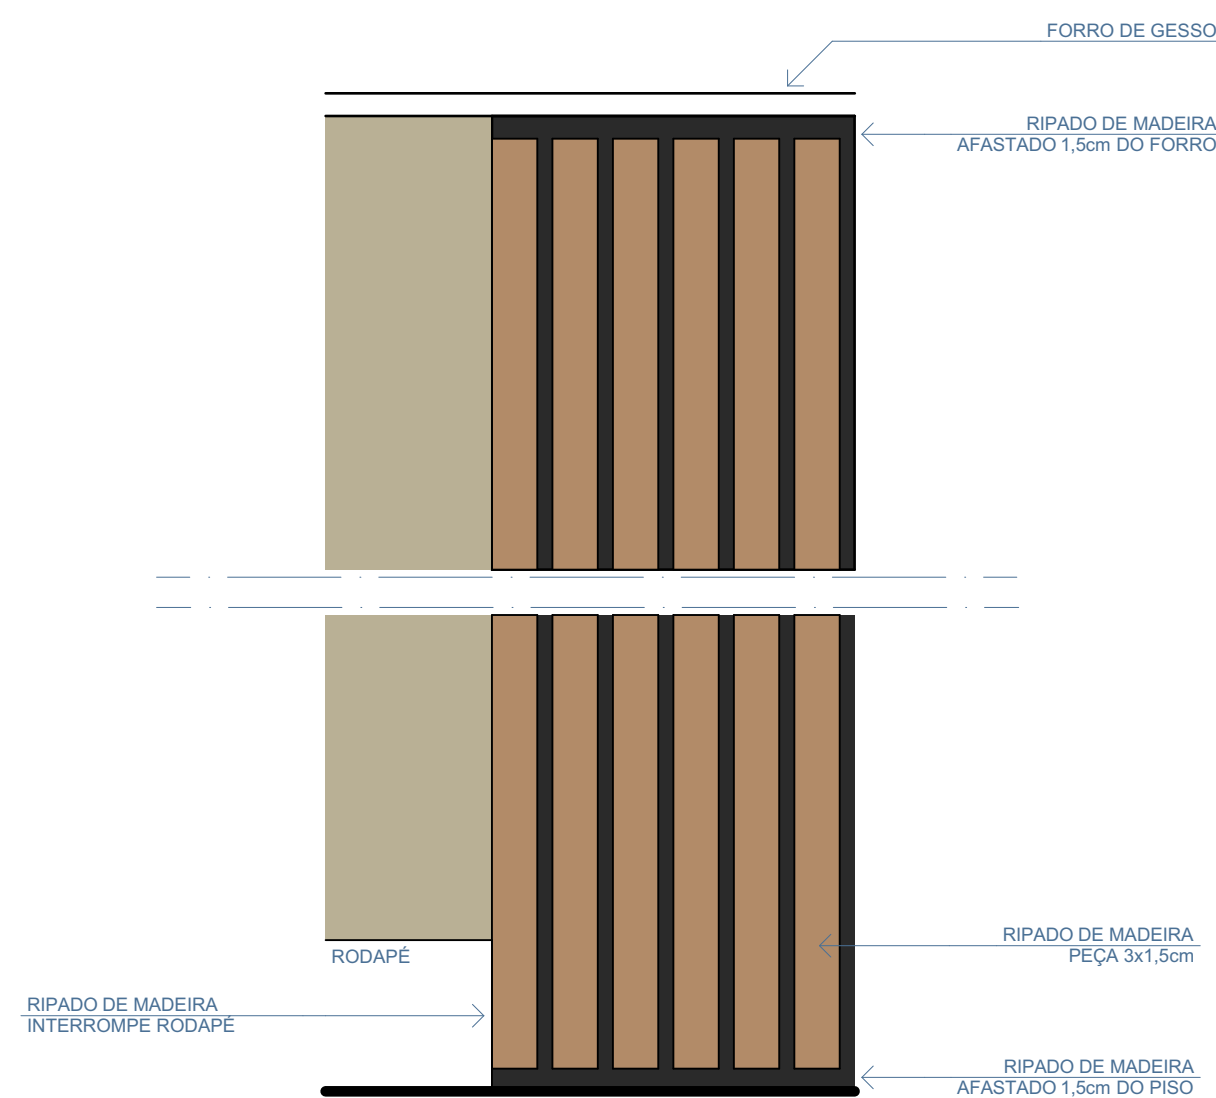

VISTA FRONTAL

PROJETO ARQUITETÔNICO

MAUI
INTERIORES DETALHAMENTO - MARCENARIA -
RIPADOS PAV. TIPO

5/10

ETAPA	OUZ_MAU_ ARQ_PROJETO EXECUTIVO DETALHAMENTOS AMBIENTAÇÃO	A1
DATA	13/03/2025	
ESCALA	1:10, 1:5	

ENDEREÇO Rodovia SC-406, s/n, Praia Mole, Florianópolis, Santa Catarina

ASSINATURA:

CLIENTE

OUZ

CPE/CNPJ:

ASSINATURA:

RESPONSÁVEL: HENRIQUE PIMONT

CAU A 20832-9

DESENHO:

MAYCON PASSIG; ARTHUR ANDRADE; MIRELA MOSER



PIMONT
ARQUITETURA

RUA ALVES DE BRITO, 141 - SALA 701
CENTRO - FLORIANÓPOLIS - SC
CEP: 88015-440

TELEFONE: 48 30251200
CELULAR: 48 99804485

WWW.PIMONTARQUITETURA.COM.BR
CONTATO@PIMONTARQUITETURA.COM.BR