

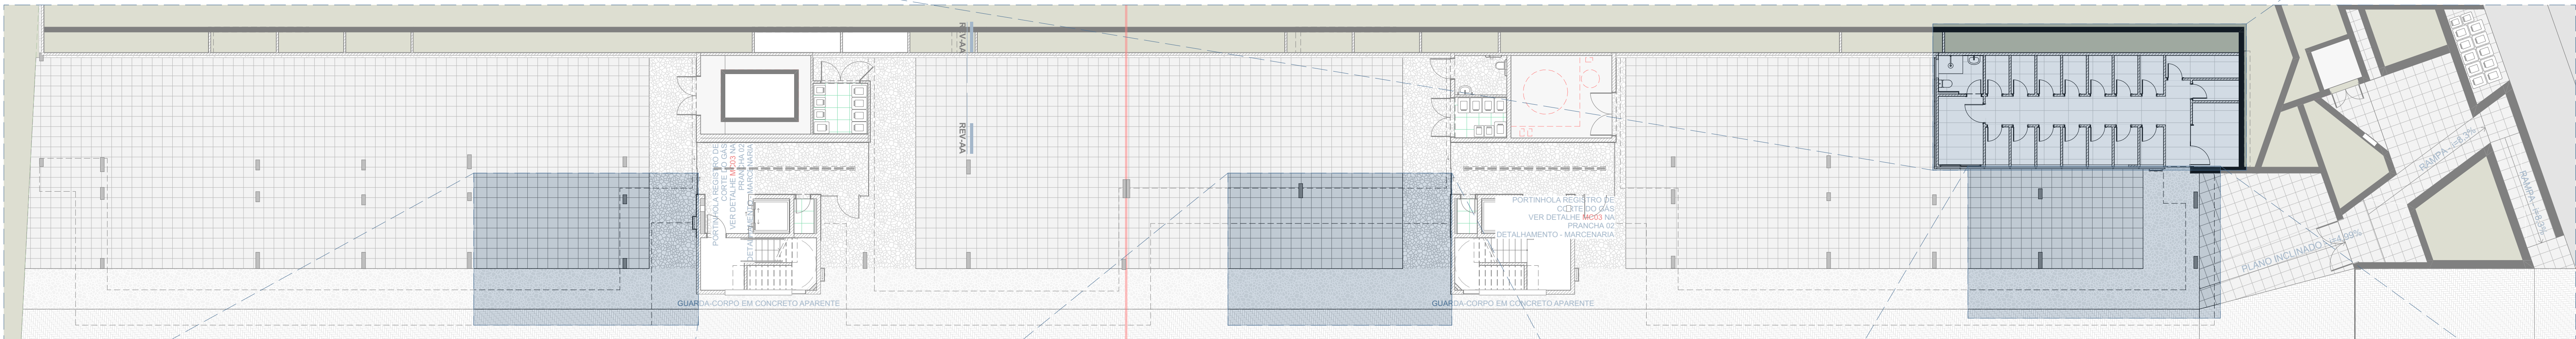
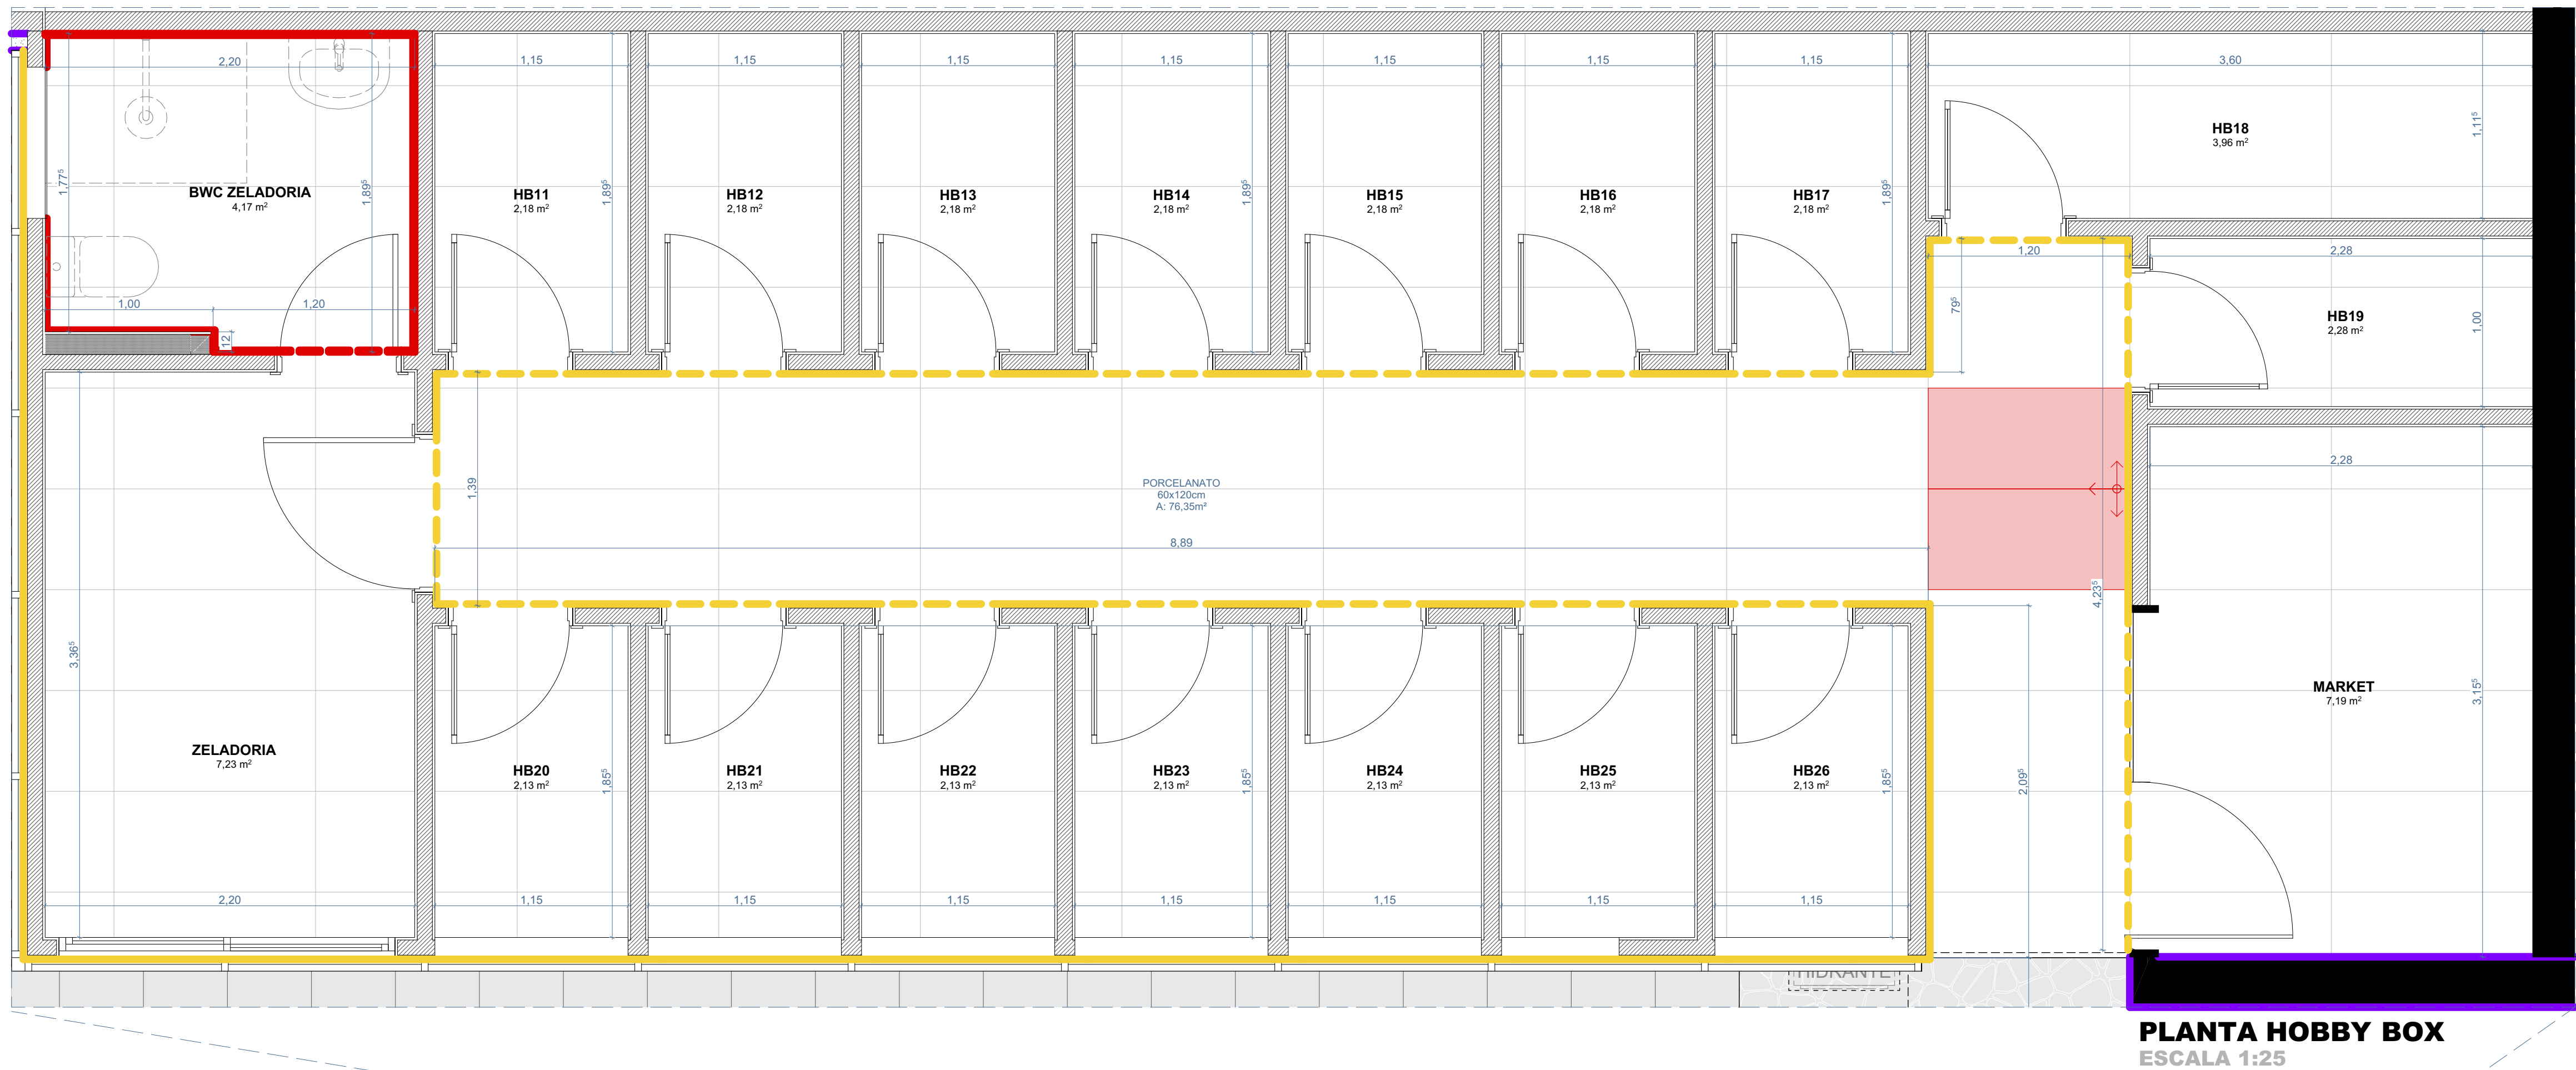
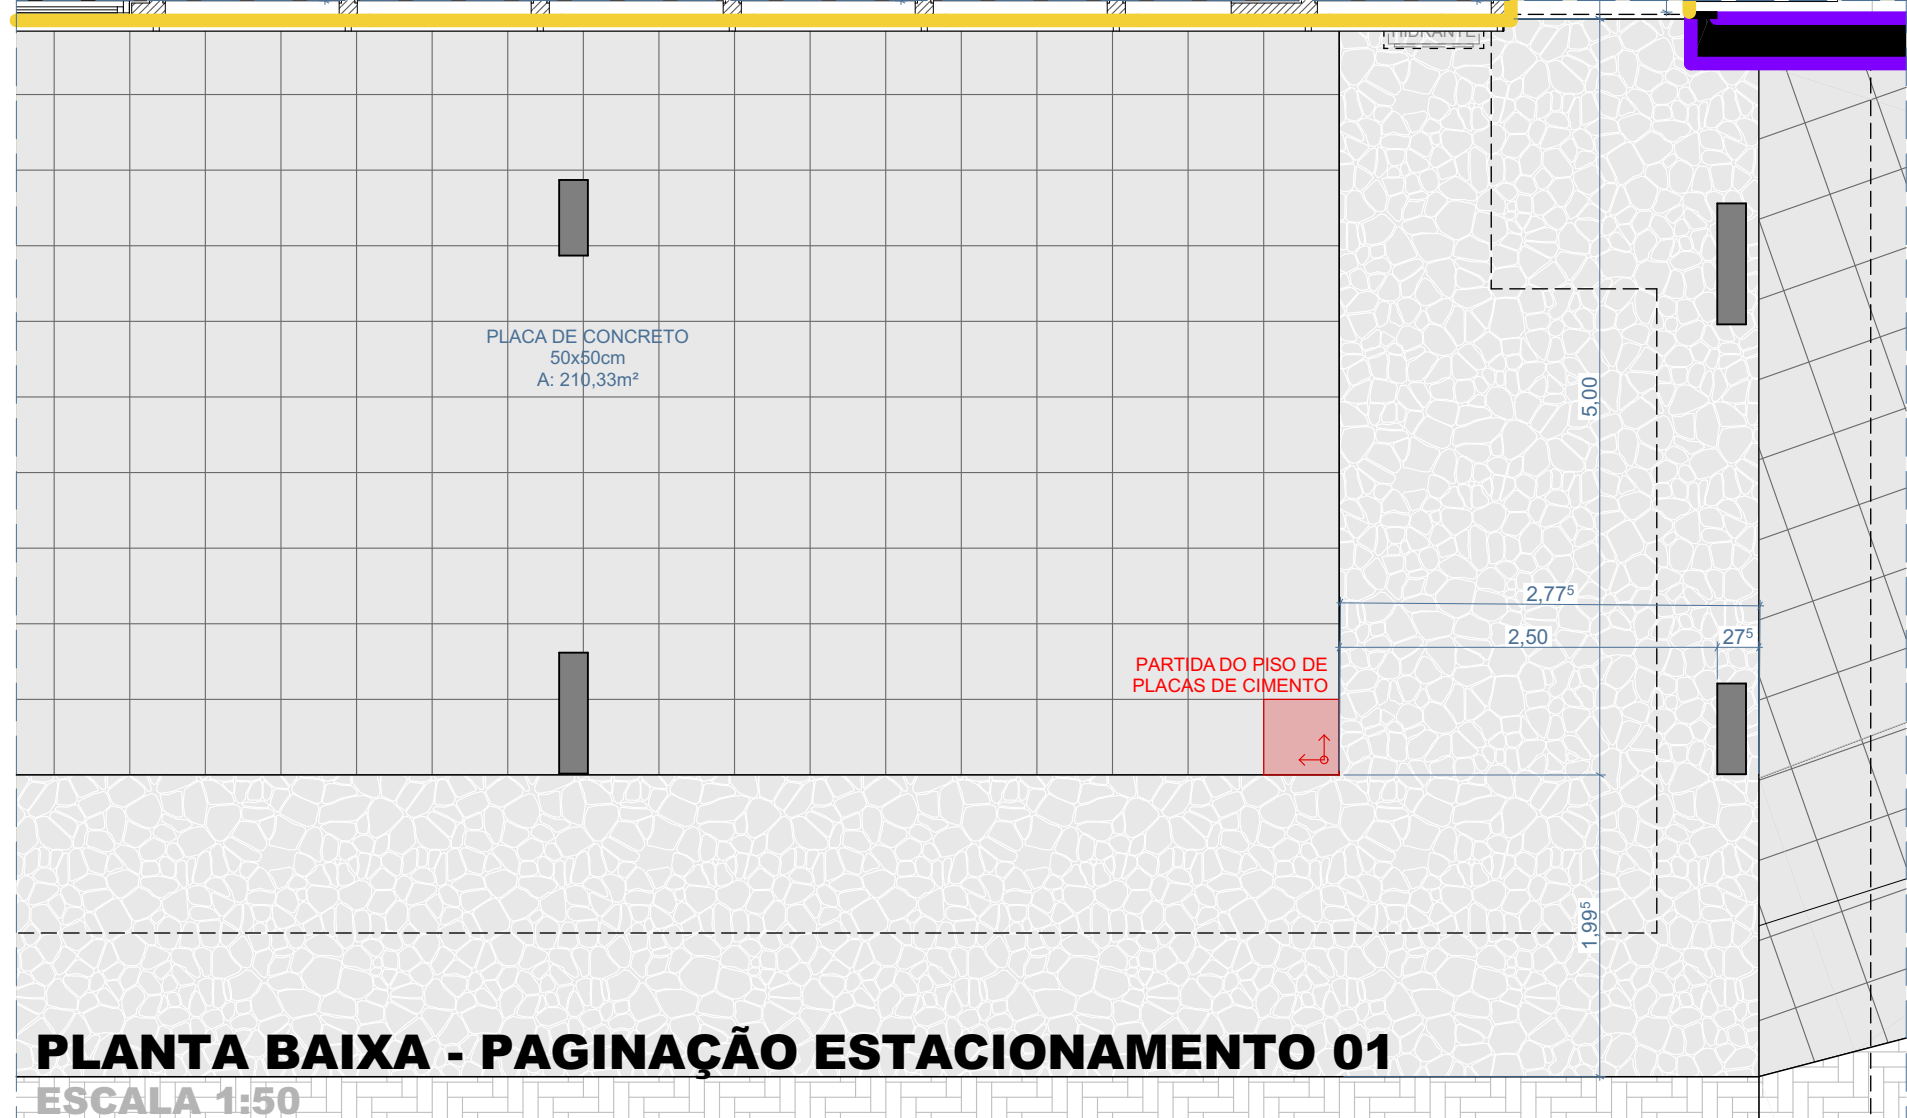


SUBSOLO - HALL TORRE B

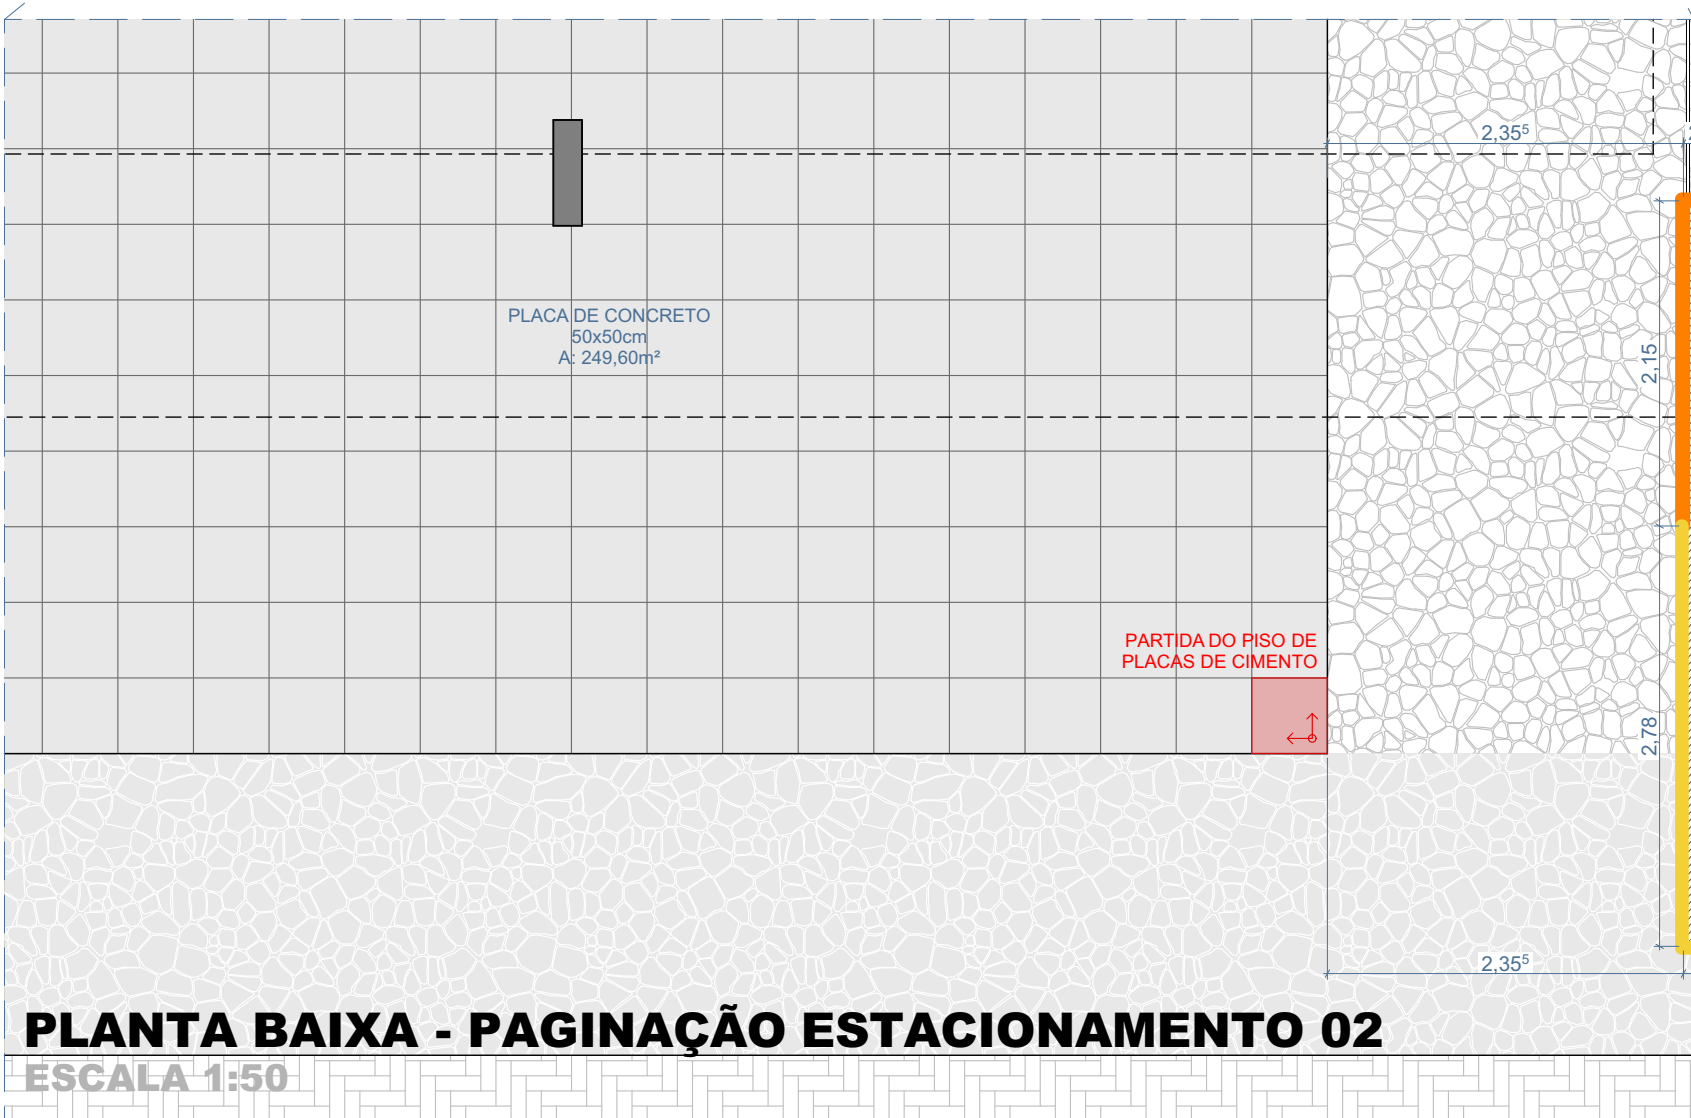

SUBSOLO 1:150  
ESCALA 1:150

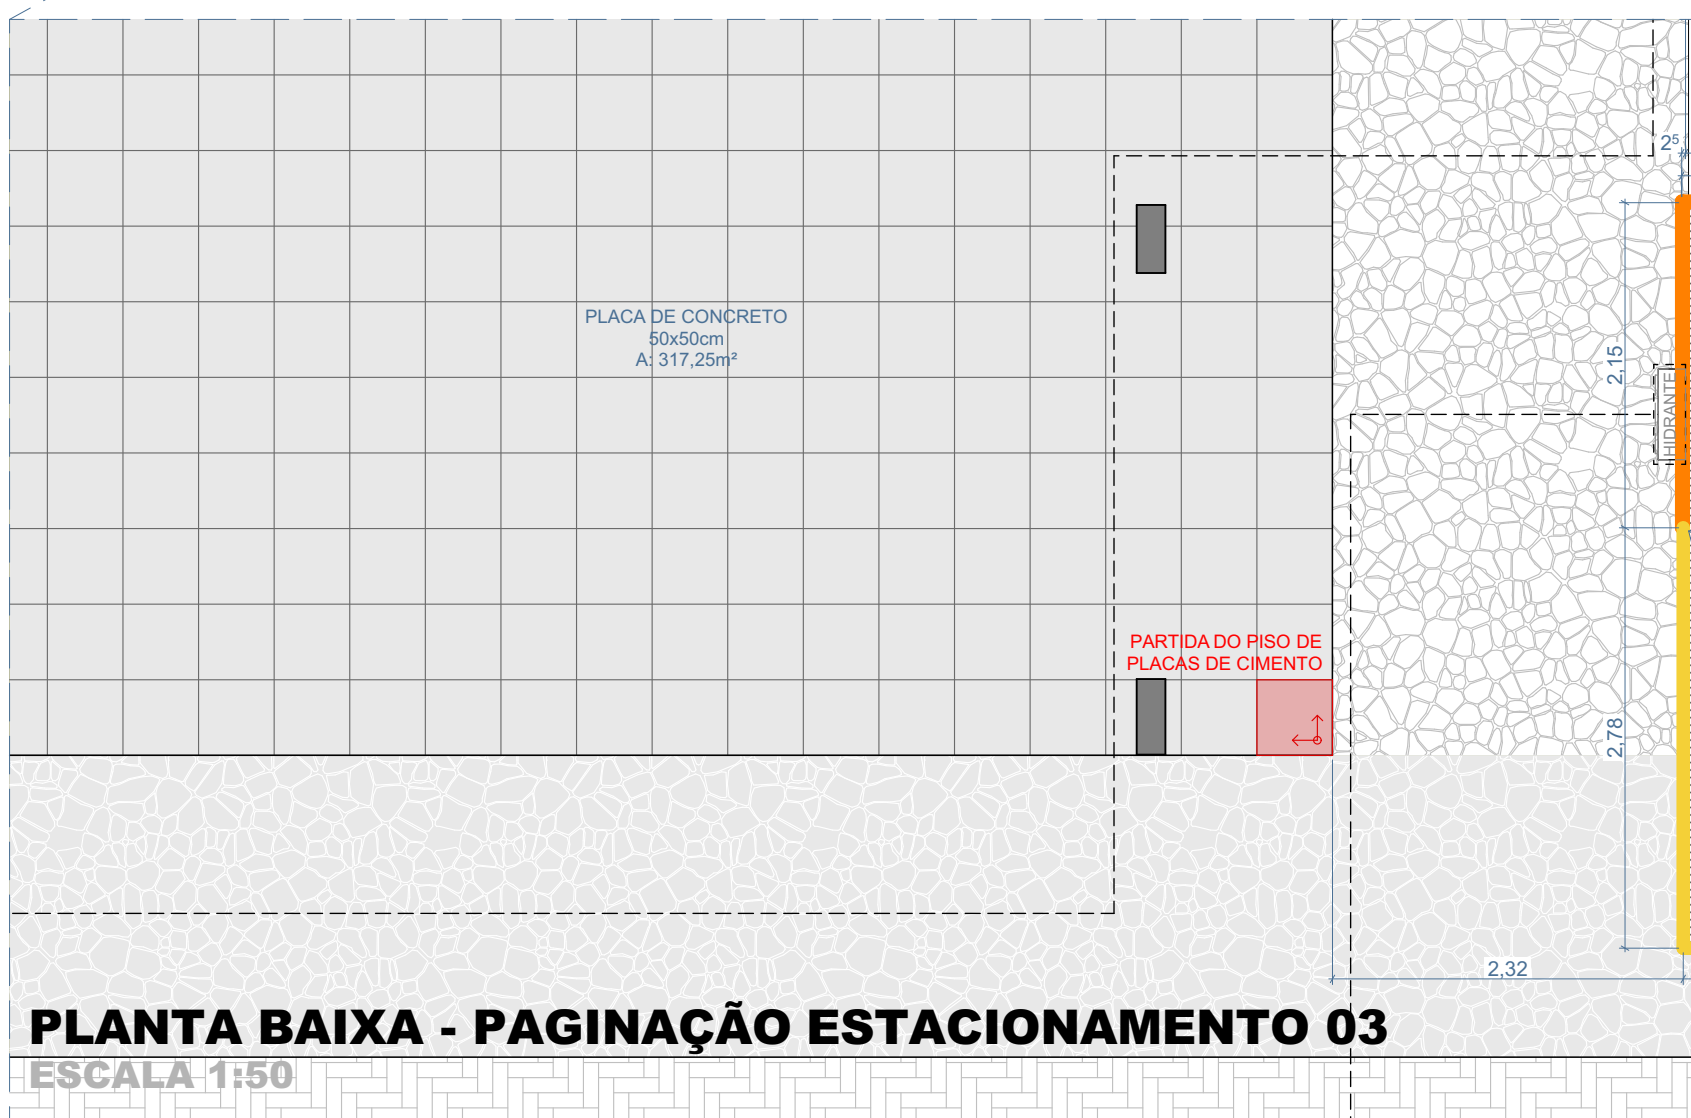

PLACA DE CONCRETO 50x50

PETIT PAVÉ BRANCO

PETIT PAVÉ PRETO

CIMENTO ALISADO

CONCRETO VASSOURADO

PORCELANATO 60x120

PORCELANATO 60x60

PORCELANATO 90x90

PISO DE MADEIRA

DECK DE MADEIRA

PISO ESPORTIVO EMBORRACHADO EM PLACAS 100x100

BASALTO RÚSTICO

BASALTO POLIDO

PISO CIMENTÍCIO SOLARIUM 50x50

AZULEJO 30x60 BRANCO ACETINADO RETIFICADO

TINTA DE PEDRA DIORRE DELICATO PRECIOSA COR NATURAL

TINTA DE PEDRA DIORRE ORNAMENTAL MAXI COR BEGE ARACAMA

TEXTURA TERRACOR PREDIAL PRETO

PINTURA ACRÍLICA PRETA - SUVINIL PATATIVA

BASALTO POLIDO

REVESTIMENTO EM PEDRA NATURAL MOLEDO

REVESTIMENTO EM LÂMINA FRELÔ

COMPENSADO VIROLA

ESPELHO CRISTAL COLADO

NOTAS

1. PILARES DA GARAGEM E MURETAS DO ACESSO SÃO EM CONCRETO APARENTE;

2. PAREDES INTERNAS SEM INDICAÇÃO DE REVESTIMENTO RECEBERÃO PINTURA ACRÍLICA COR BRANCO FOSCO;

3. PAREDES EXTERNAS SEM INDICAÇÃO DE REVESTIMENTO RECEBERÃO PINTURA TERRACOR PREDIAL BRANCO;

4. SOLEIRAS DAS PORTAS DOS APARTAMENTOS EM PEÇA ÚNICA SEQUINDO ESPECIFICAÇÃO DO PISO DA CIRCULAÇÃO COMUM

PROJETO ARQUITETÔNICO  
MAUI  
INTERIORES AMBIENTAÇÃO - SUB HOBBYBOX E  
ESTACIONAMENTOS

|              |                                                                |         |
|--------------|----------------------------------------------------------------|---------|
| ETAPA        | OUZ_MAU_ARQ_PROJETO EXECUTIVO AMBIENTAÇÃO                      | A1 EST. |
| DATA         | 14/03/2025                                                     |         |
| ESCALA       | 1:50, 1:150, 1:25                                              |         |
| ENDEREÇO     | Rodovia SC-406, s/n, Praia Mole, Florianópolis, Santa Catarina |         |
| ASSINATURA:  |                                                                |         |
| CLIENTE      | OUZ                                                            |         |
|              | CPF/CNPJ:                                                      |         |
| ASSINATURA:  |                                                                |         |
| RESPONSÁVEL: | HENRIQUE PIMONT                                                |         |
|              | CAU A 20832-9                                                  |         |
| DESENHO:     | MAYCON PASSIG; ARTHUR ANDRADE; MIRELA MOSER                    |         |