


ROOFTOP - WC PISCINA

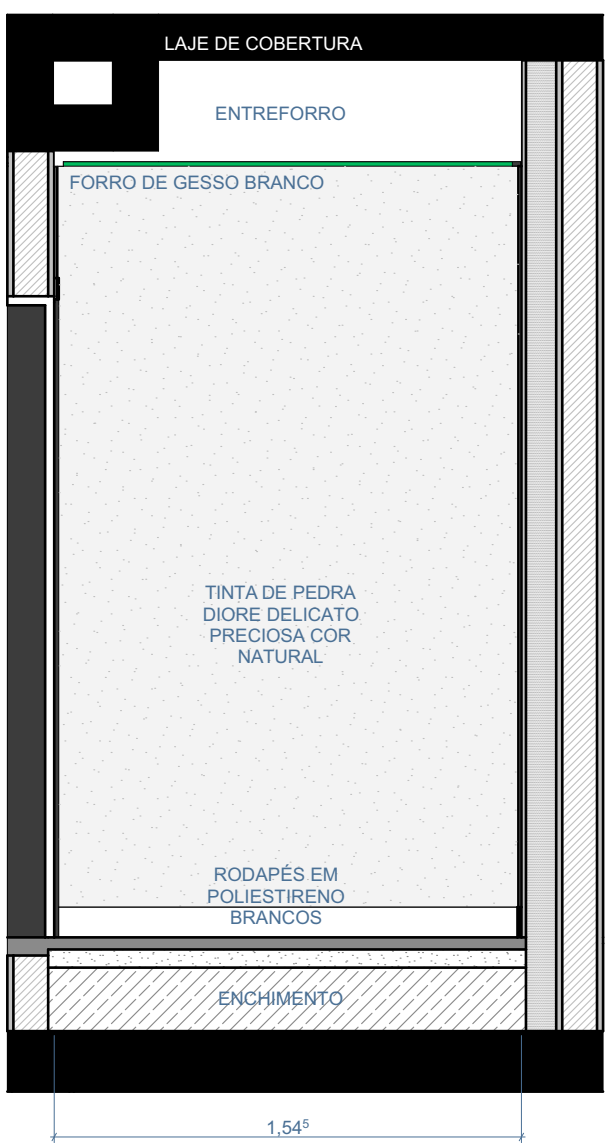


01
ESCALA 1:25



02
ESCALA 1:25



03
ESCALA 1:25

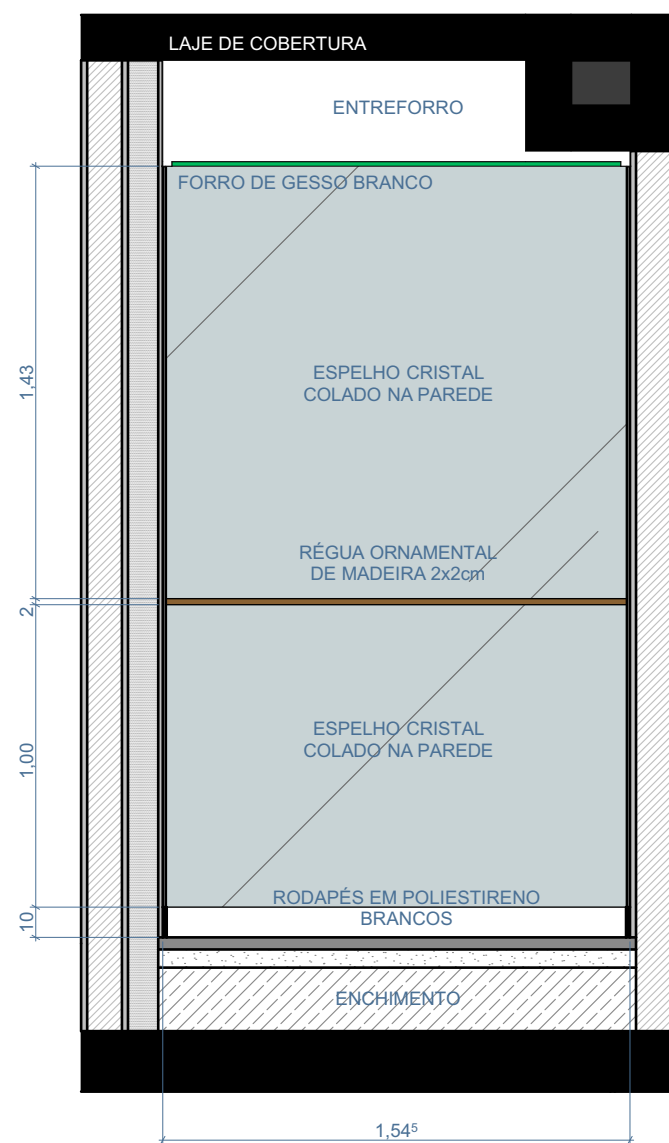

04
ESCALA 1:25

LEGENDA REVESTIMENTOS



PLACA DE CONCRETO 50x50



PETIT PAVÉ BRANCO



PETIT PAVÉ PRETO



CIMENTO ALISADO



CONCRETO VASSOURADO



PORCELANATO 60x120



PORCELANATO 60x60



PORCELANATO 90x90



PISO DE MADEIRA



DECK DE MADEIRA



PISO ESPORTIVO EMBORRACHADO EM PLACAS 100x100



BASALTO RÚSTICO



BASALTO POLIDO



PISO CIMENTÍCIO SOLARIUM 50x50

AZULEJO 30x60 BRANCO ACETINADO RETIFICADO

TINTA DE PEDRA DIORE DELICATO PRECIOSA COR NATURAL

TINTA DE PEDRA DIORE ORNAMENTALI MAXI COR BEGE ARACEMA

TEXTURA TERRACOR PREDIAL PRETO

PINTURA ACRÍLICA PRETA - SUVINIL PATATIVA

BASALTO POLIDO

REVESTIMENTO EM PEDRA NATURAL MOLEDO

REVESTIMENTO EM LÂMINA FREIJÓ


COMPENSADO VIROLA

ESPELHO CRISTAL COLADO


NOTAS

1. PILARES DA GARAGEM E MURETAS DO ACESSO SÃO EM CONCRETO APARENTE;
2. PAREDES INTERNAS SEM INDICAÇÃO DE REVESTIMENTO RECEBERÃO PINTURA ACRÍLICA COR BRANCO FOSCO.
3. PAREDES EXTERNAS SEM INDICAÇÃO DE REVESTIMENTO RECEBERÃO PINTURA TERRACOR PREDIAL BRANCO
4. SOLEIRAS DAS PORTAS DOS APARTAMENTOS EM PEÇA ÚNICA SEGUNDO ESPECIFICAÇÃO DO PISO DA CIRCULAÇÃO COMUM


ROOFTOP - WC PISCINA

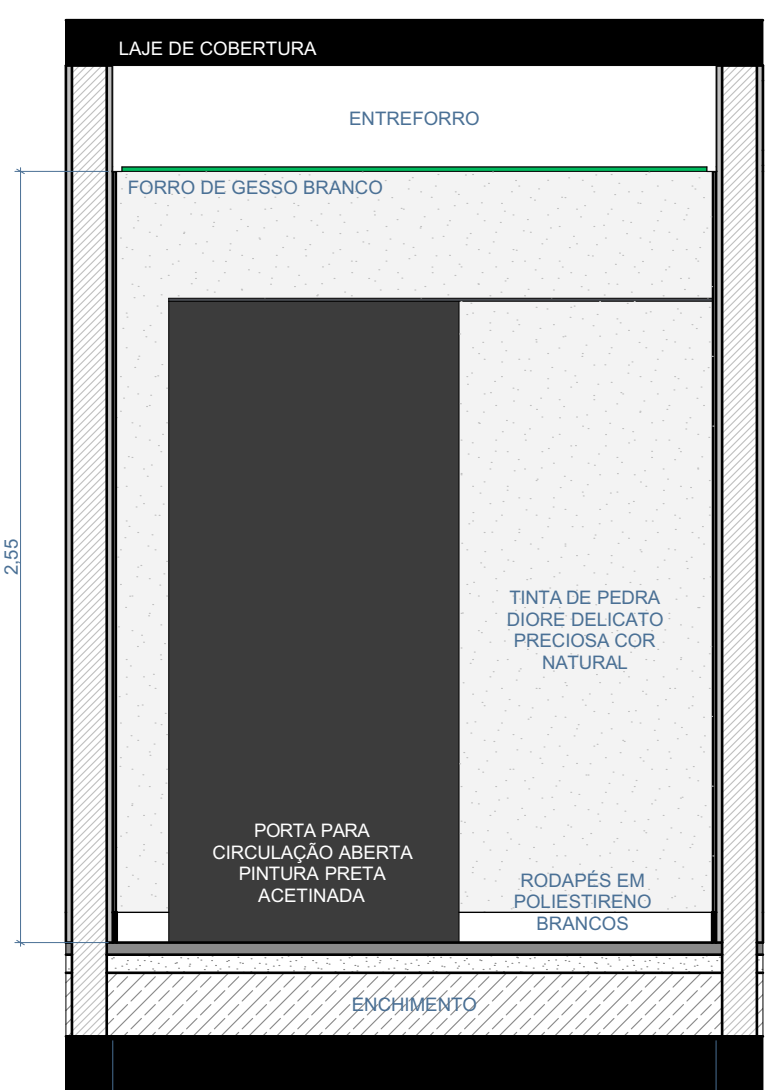

01
ESCALA 1:25

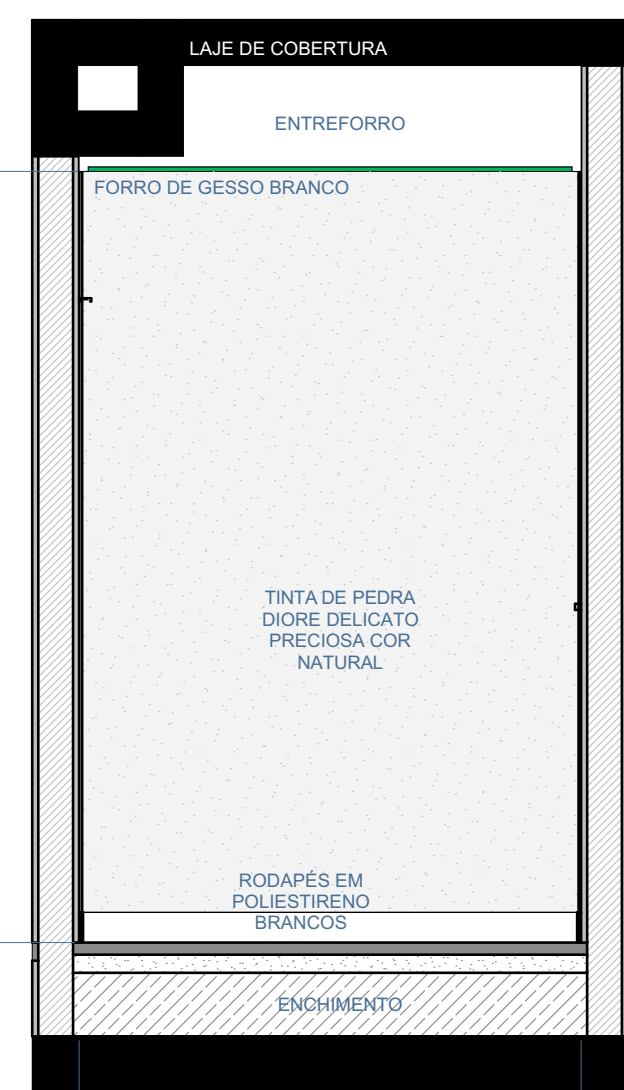


02
ESCALA 1:25

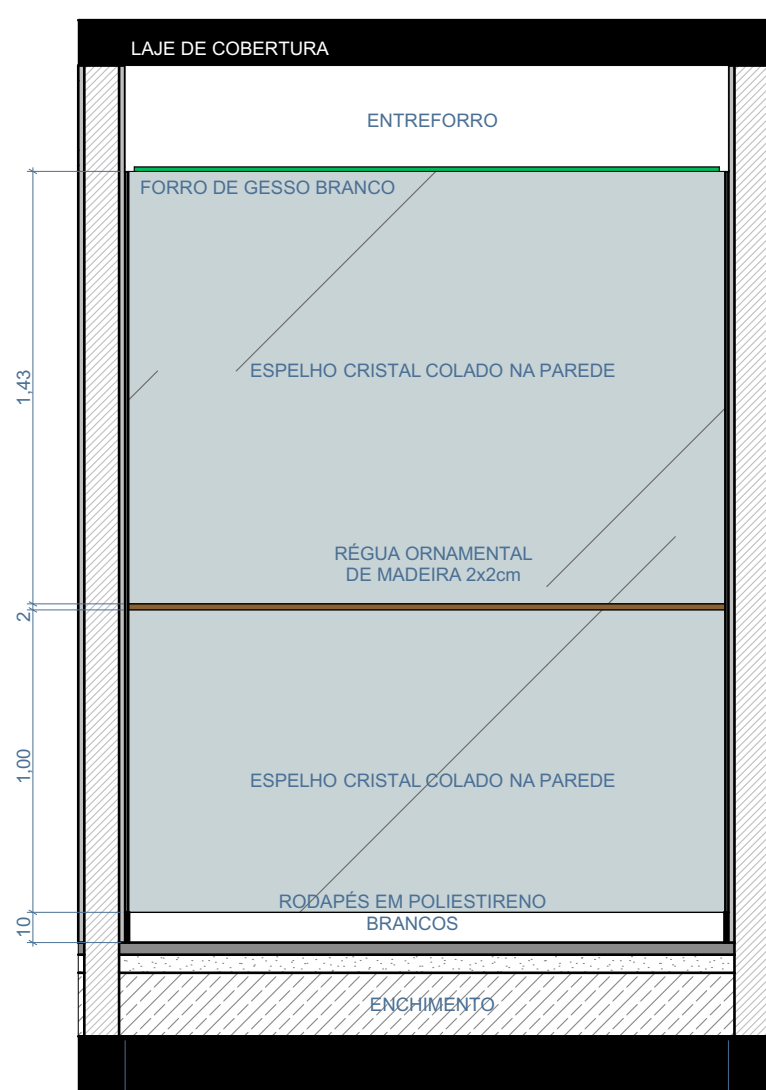

03
ESCALA 1:25



04
ESCALA 1:25

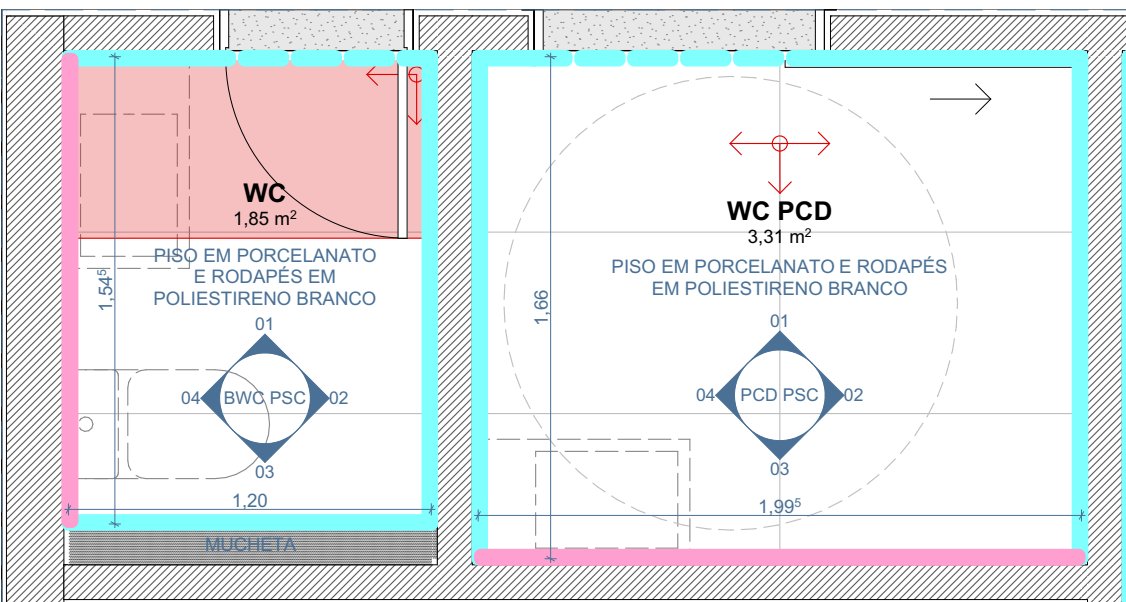

PLANTA BAIXA
ESCALA 1:25

PROJETO ARQUITETÔNICO

MAUI
INTERIORES AMBIENTAÇÃO - RTPC WC E WC PCD
PISCINA

14/18

ETAPA	OUZ_MAU_ARQ_PROJETO EXECUTIVO AMBIENTAÇÃO	A1
DATA	14/03/2025	
ESCALA	1:25, 1:50	

ENDEREÇO Rodovia SC-406, s/n, Praia Mole, Florianópolis, Santa Catarina

ASSINATURA: CLIENTE OUZ CPF/CNPJ:

ASSINATURA: RESPONSÁVEL: HENRIQUE PIMONT CAU A 20832-9

DESENHO: MAYCON PASSIG; ARTHUR ANDRADE; MIRELA MOSER



PIMONT
ARQUITETURA

RUA ALVES DE BRITO, 141 - SALA 701
CENTRO - FLORIANÓPOLIS - SC
CEP: 88015-440
TELEFONE: 48 30251200
CELULAR: 48 99804485

WWW.PIMONTARQUITETURA.COM.BR
CONTATO@PIMONTARQUITETURA.COM.BR