



MM03 | ACABAMENTO PORTA DE CORRER ROOFTOP

PEÇAS EM TRAVERTINO ROMANO RÚSTICO
04 PEÇAS VERTICAIS PARA 02 PORTAS DE CORRER

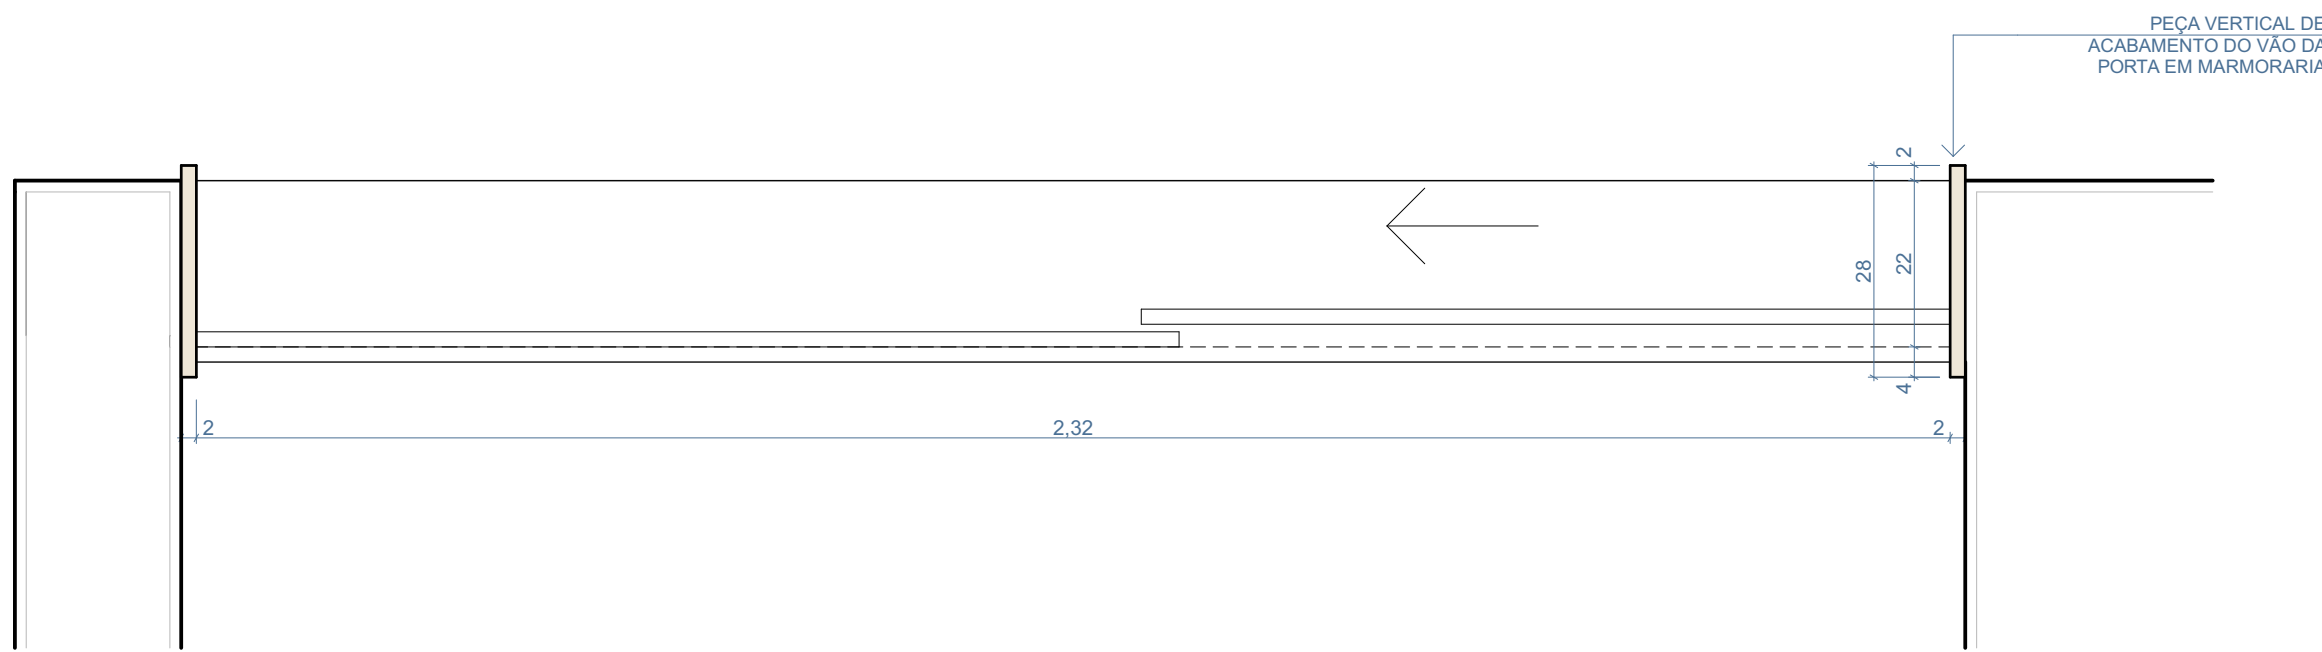

PLANTA BAIXA

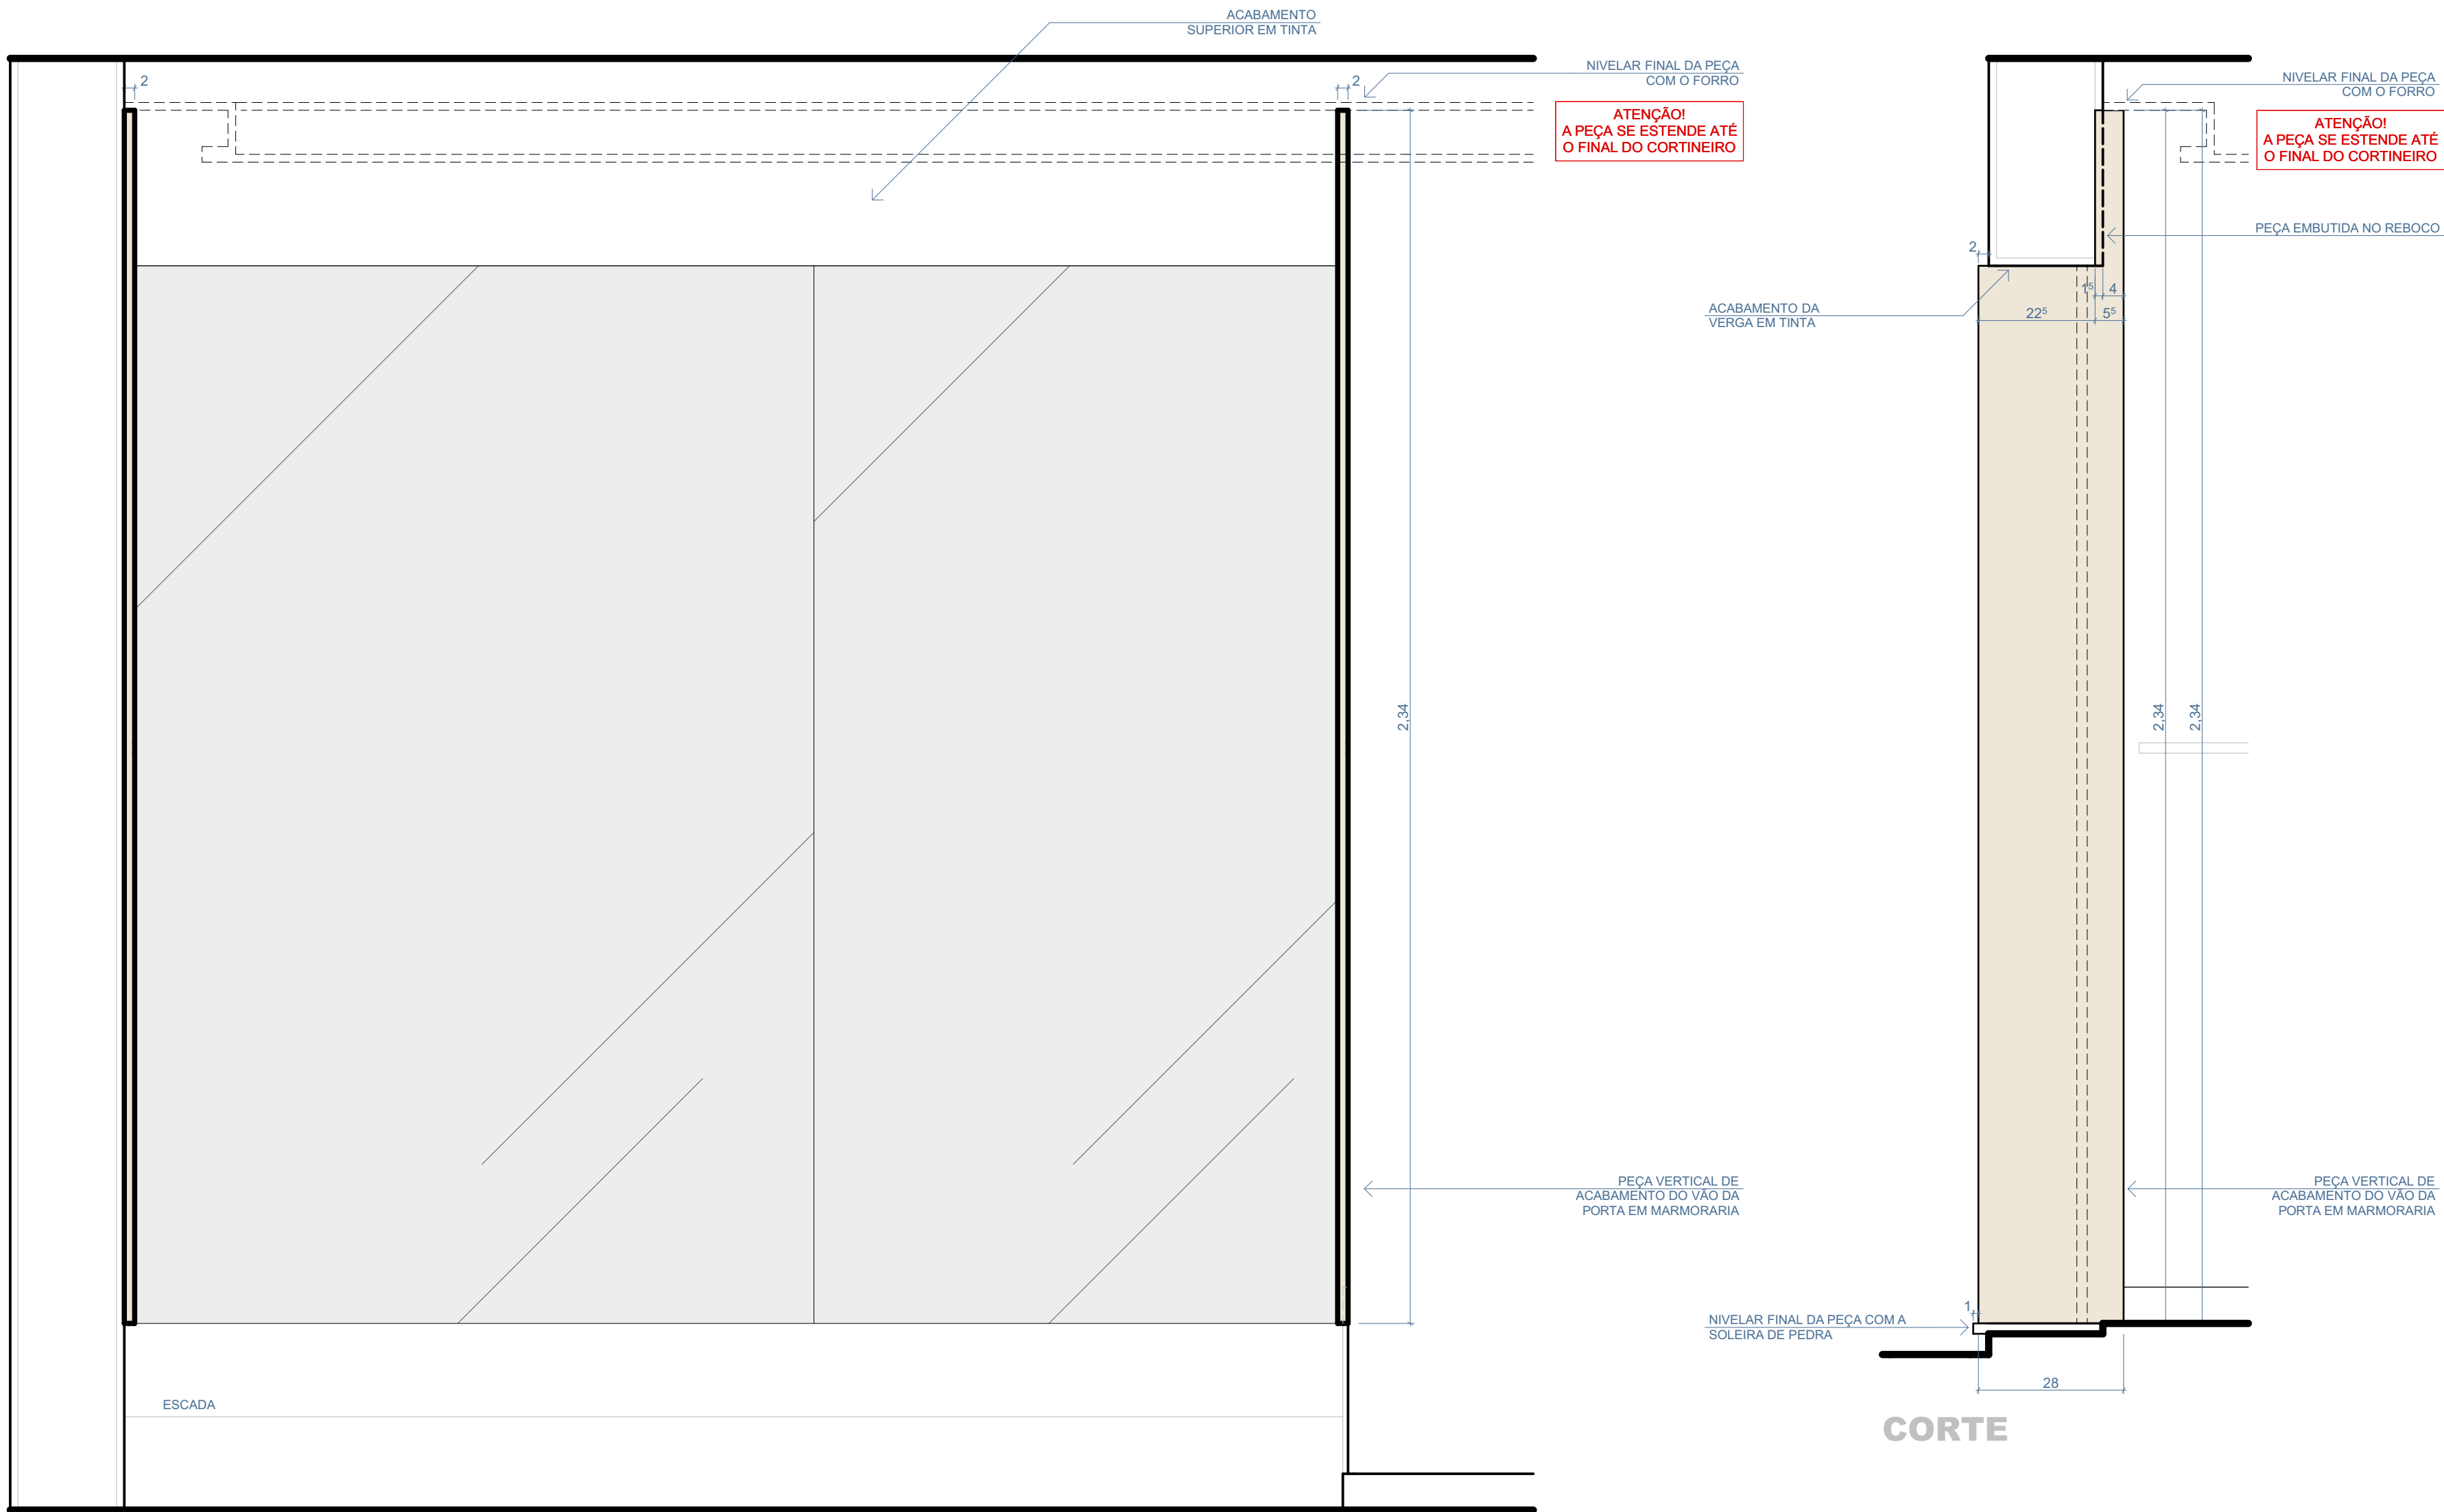


VISTA FRONTAL


CORTE

MM04 | ACABAMENTO PORTA DE ABRIR ROOFTOP

PEÇAS EM TRAVERTINO ROMANO RÚSTICO
04 PEÇAS VERTICAIS PARA 02 PORTAS PIVOTANTES

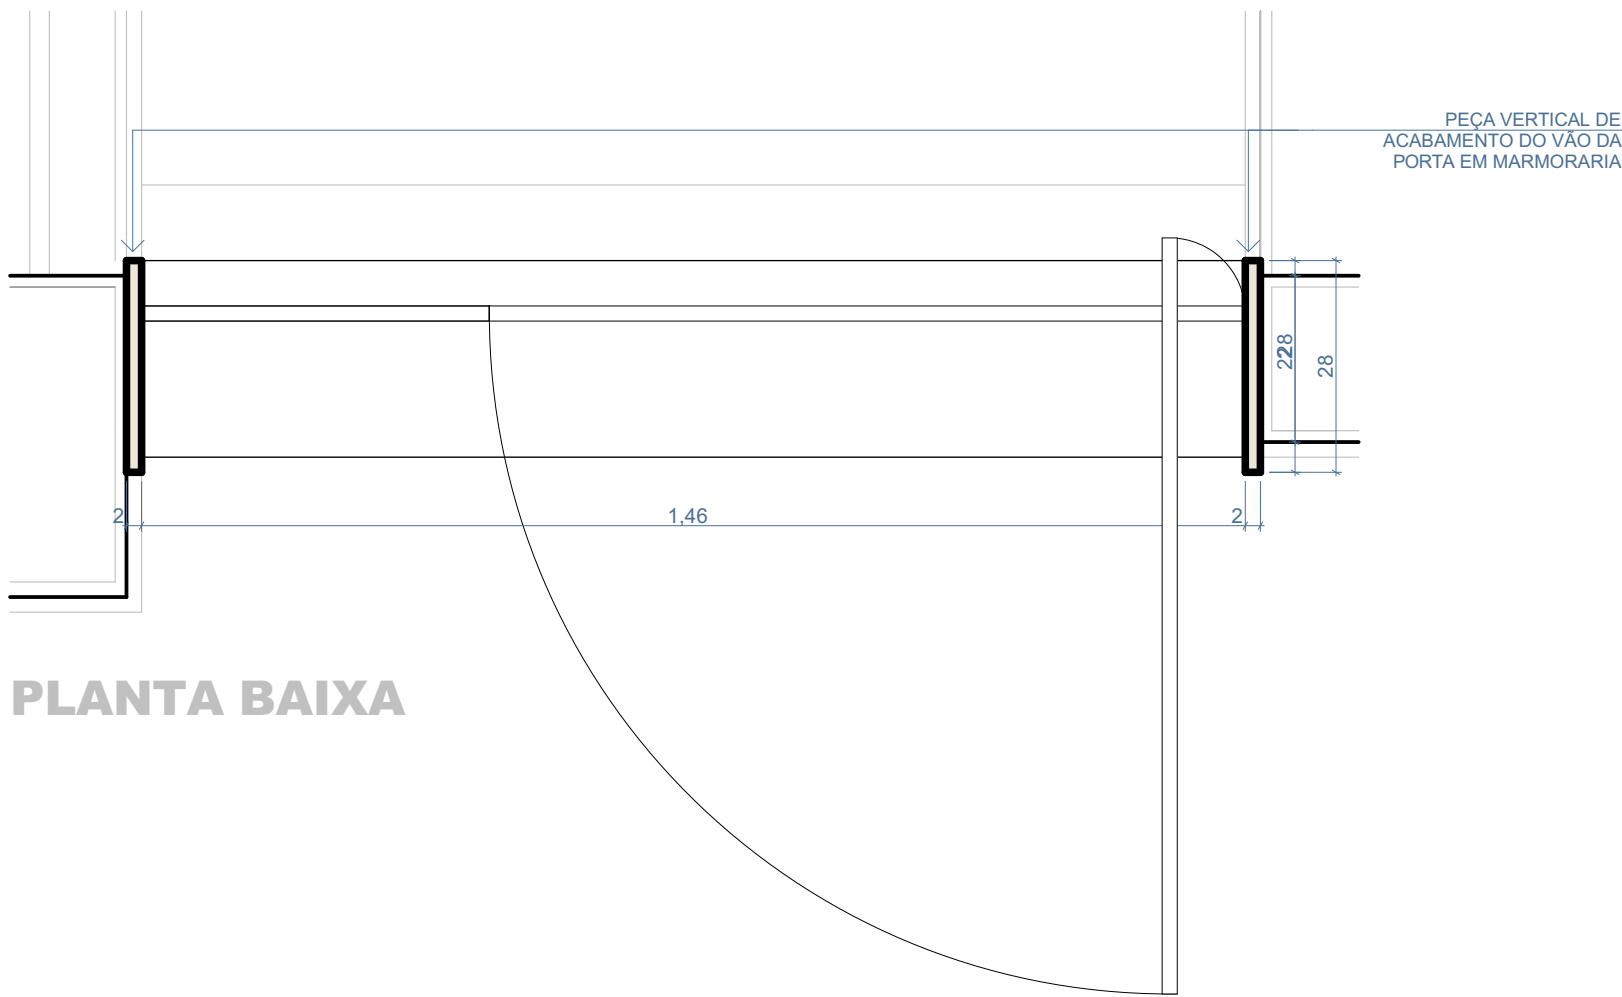

PLANTA BAIXA

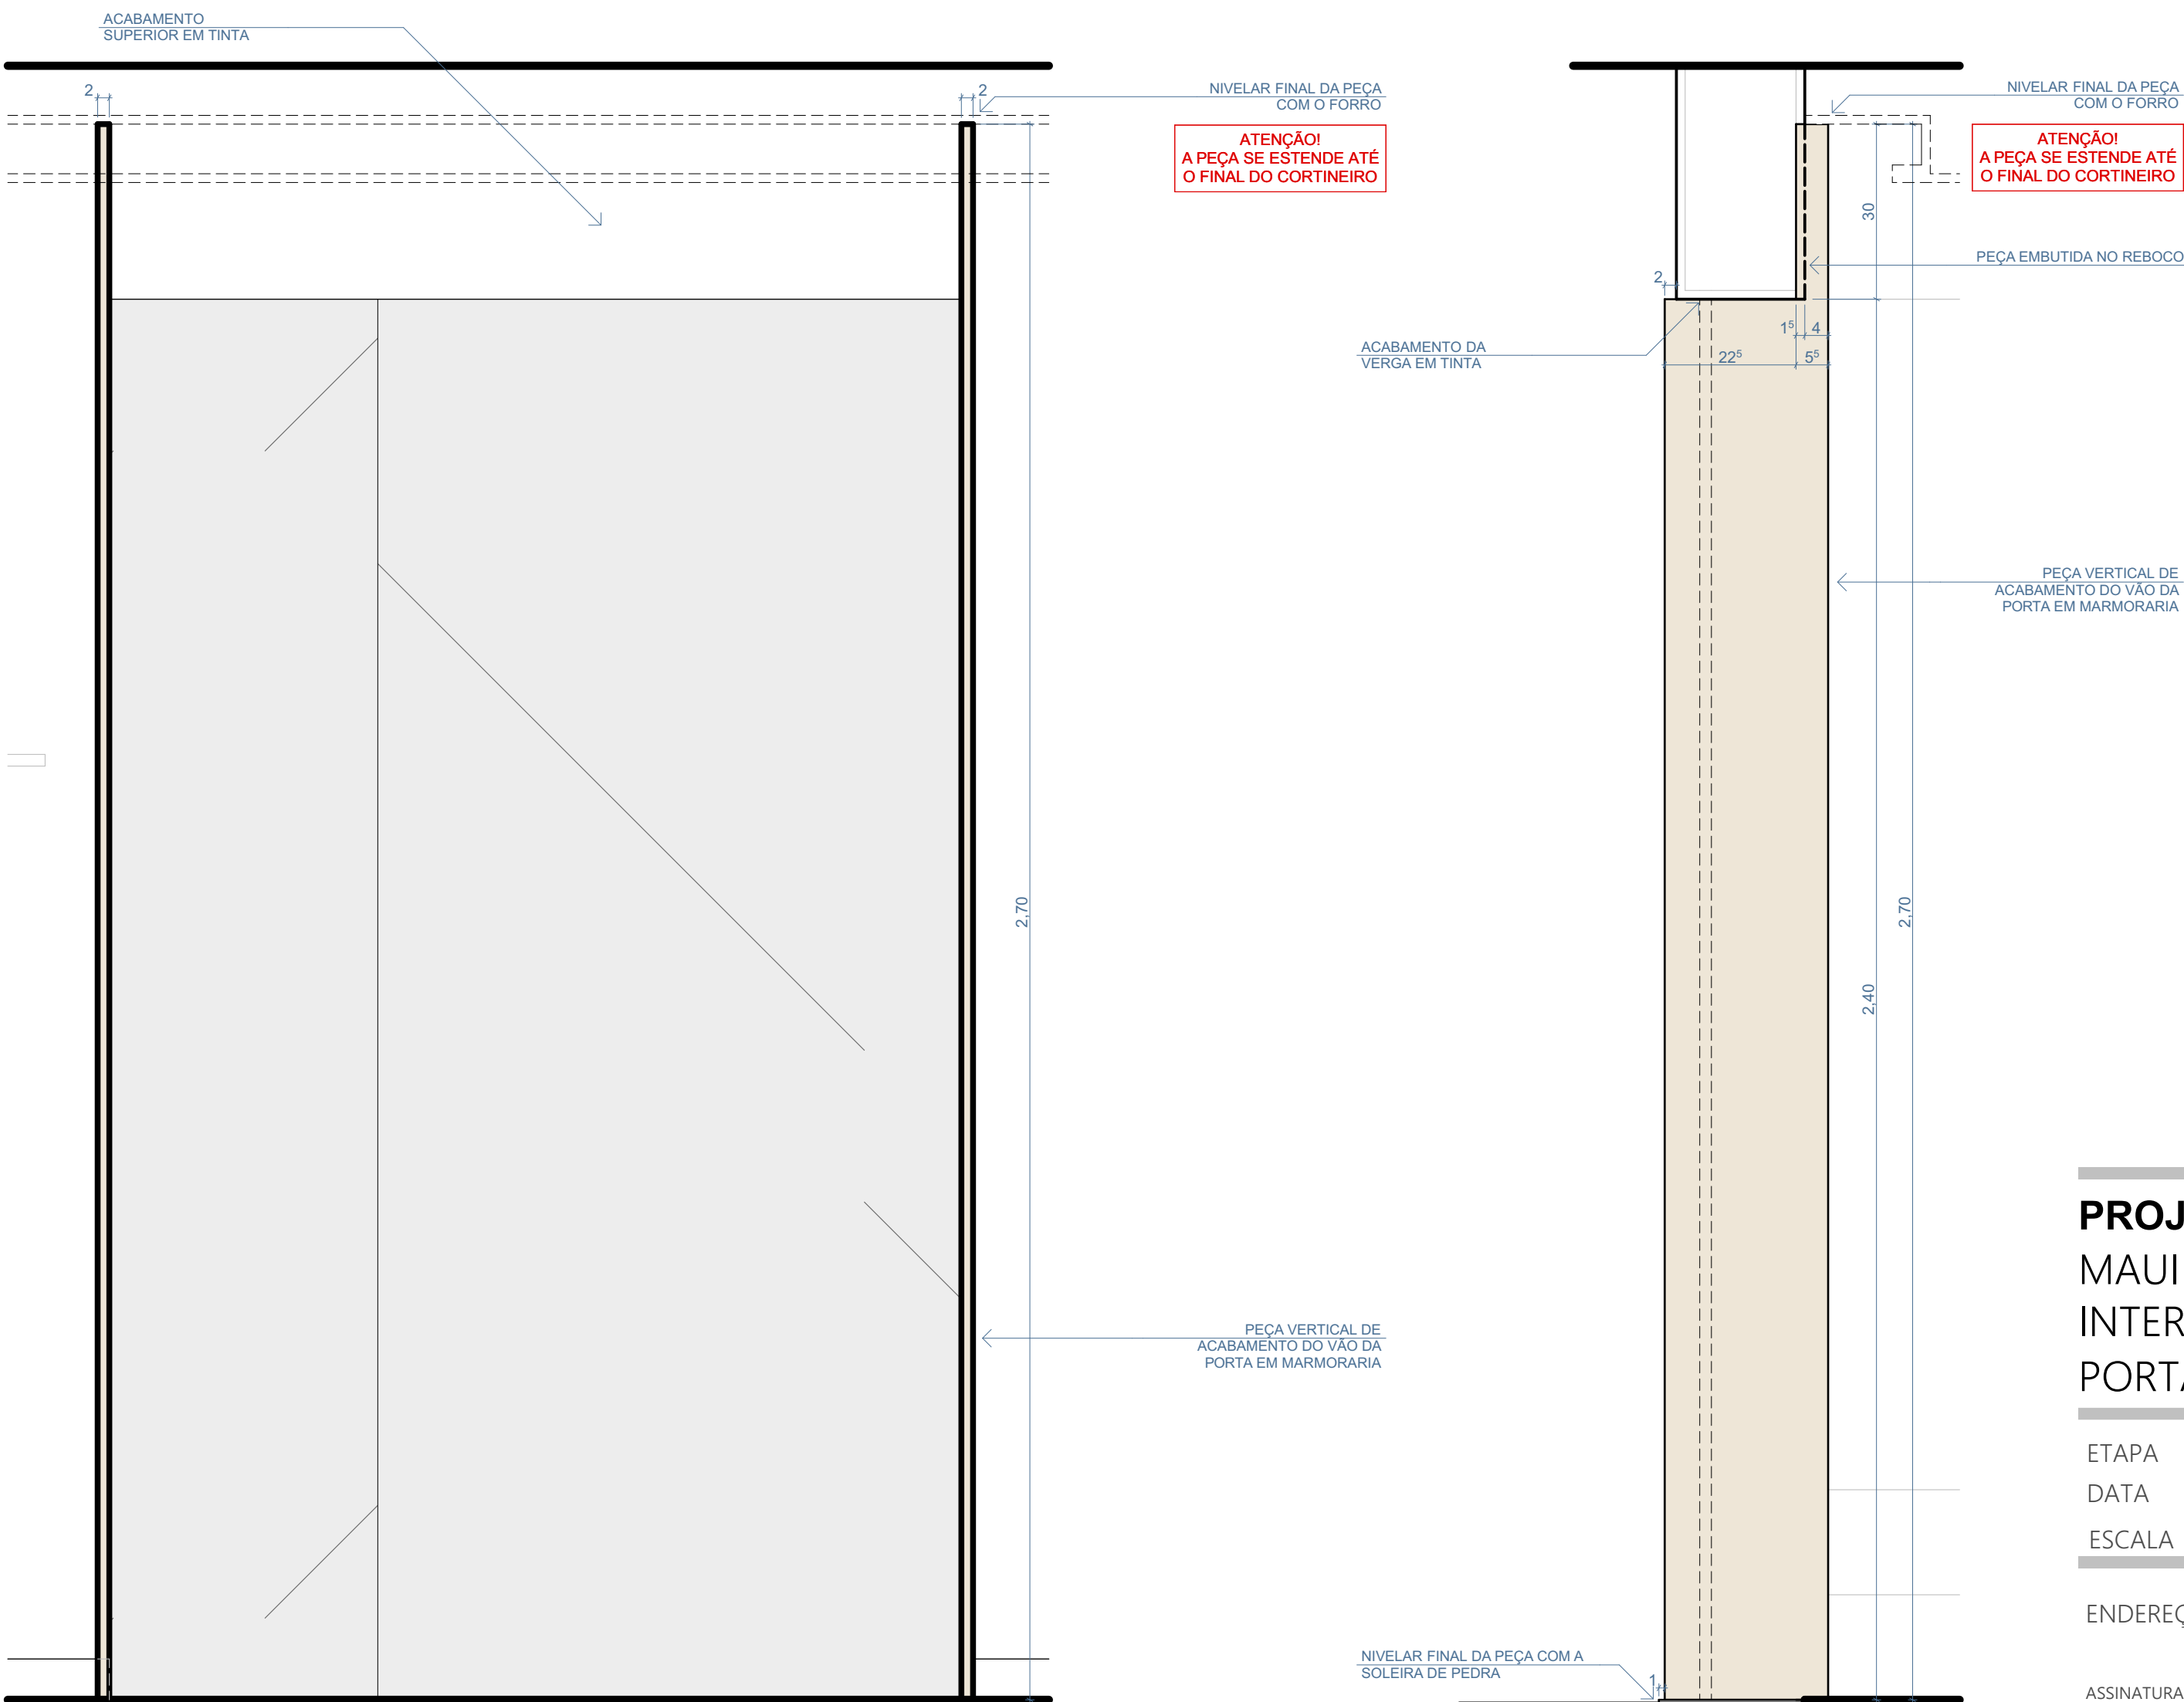

VISTA FRONTAL

CORTE

PROJETO ARQUITETÔNICO

MAUI
INTERIORES DETALHAMENTO - MARMORARIA -
PORTAS ROOFTOP

ETAPA	OUZ MAUI_ARQ_PROJETO EXECUTIVO DETALHAMENTOS	A1 EST.
DATA	AMBIENTAÇÃO 13/03/2025	
ESCALA	1:10	
ENDEREÇO	Rodovia SC-406, s/n, Praia Mole, Florianópolis, Santa Catarina	
ASSINATURA:		
CLIENTE	OUZ CPF/CNPJ:	
ASSINATURA:		
RESPONSÁVEL:	HENRIQUE PIMONT CAU A 20832-9	
DESENHO:	MAYCON PASSIG; ARTHUR ANDRADE; MIRELA MOSER	