


ROOFTOP - ESPAÇO GOURMET

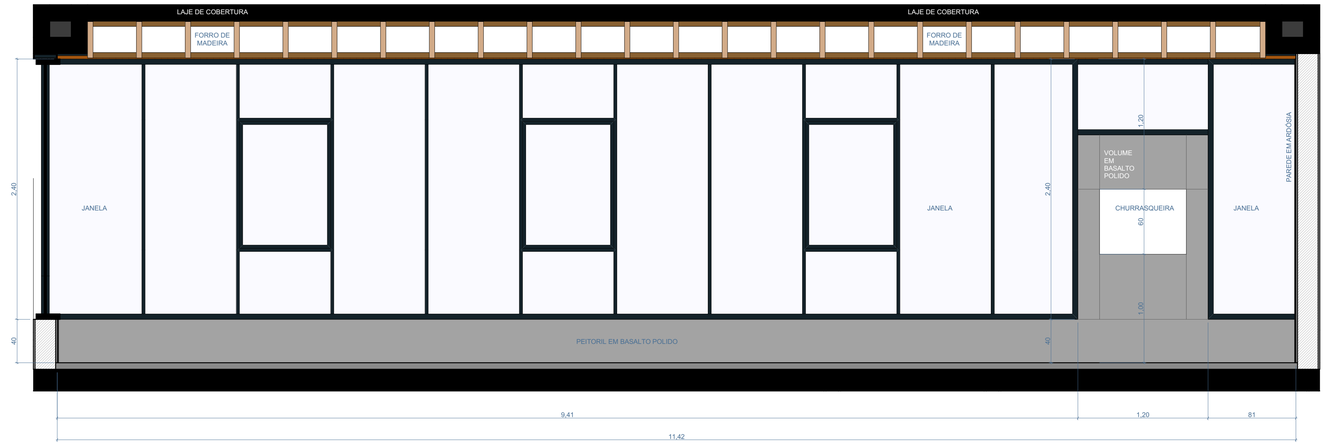


01
ESCALA 1:25

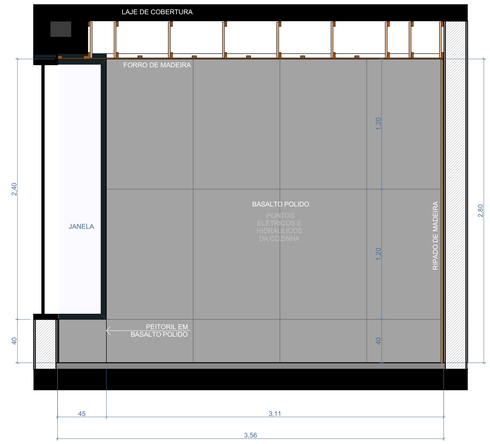


02
ESCALA 1:25

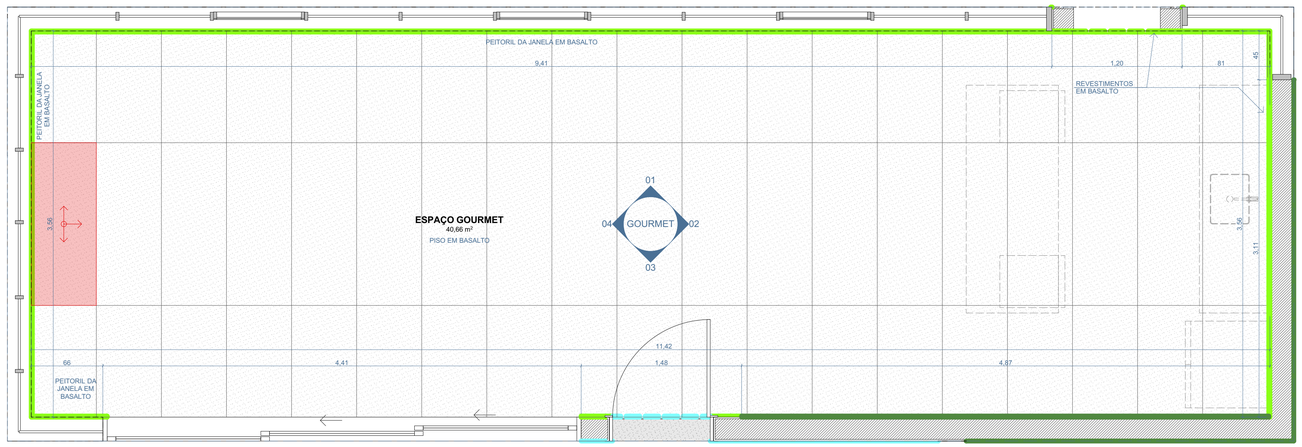

PLANTA BAIXA

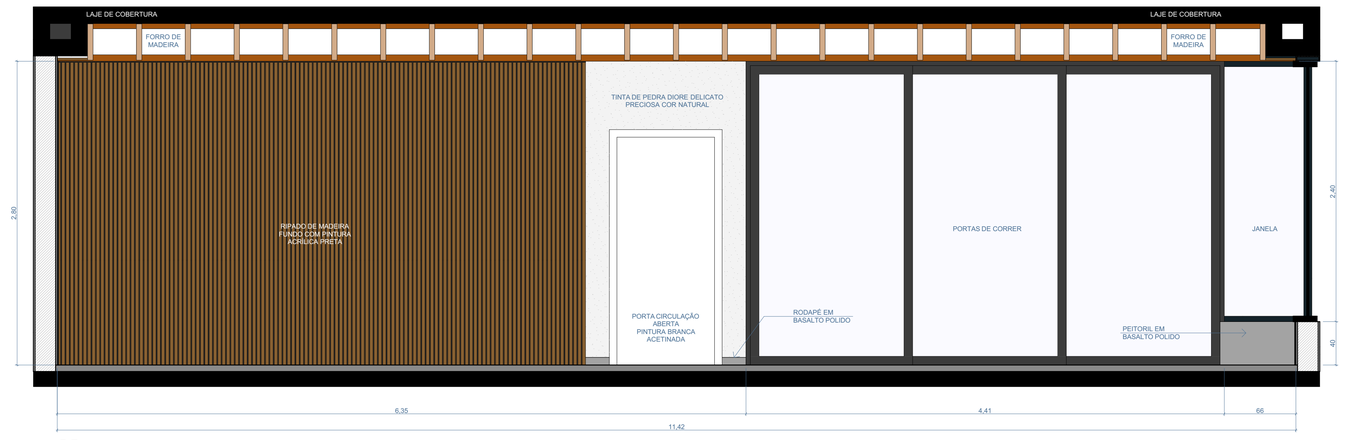

03
ESCALA 1:25

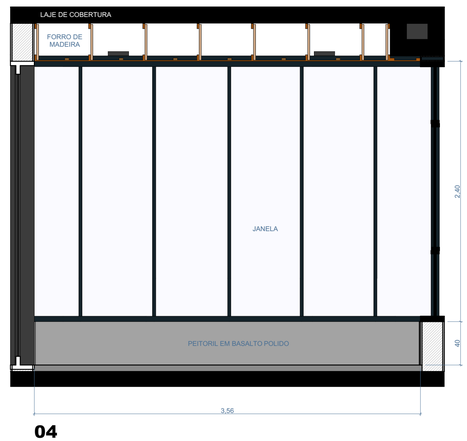

04
ESCALA 1:25

LEGENDA REVESTIMENTOS

- PLACA DE CONCRETO 50x50
- PETIT PAVÊ BRANCO
- PETIT PAVÊ PRETO
- CIMENTO ALISADO
- CONCRETO VASSOURADO
- PORCELANATO 60x120
- PORCELANATO 60x60
- PORCELANATO 90x90
- PISO DE MADEIRA
- DECK DE MADEIRA
- PISO ESPORTIVO EMBORRACHADO EM PLACAS 100x100
- BASALTO RÚSTICO
- BASALTO POLIDO
- PISO CIMENTÍCIO SOLARIUM 50x50
- AZULEJO 30x60 BRANCO ACETINADO RETIFICADO
- TINTA DE PEDRA DIORE DELICATO PRECIOSA COR NATURAL
- TINTA DE PEDRA DIORE ORNAMENTALI MAXI COR BEGE ARACEMA
- TEXTURA TERRACOR PREDIAL PRETO
- PINTURA ACRÍLICA PRETA - SUVINIL PATATIVA
- BASALTO POLIDO
- REVESTIMENTO EM PEDRA NATURAL MOLEDO
- REVESTIMENTO EM LÂMINA FREIJÓ
- COMPENSADO VIROLA
- ESPELHO CRISTAL COLADO

NOTAS

1. PILARES DA GARAGEM E MURETAS DO ACESSO SÃO EM CONCRETO APARENTE;
2. PAREDES INTERNAS SEM INDICAÇÃO DE REVESTIMENTO RECEBERÃO PINTURA ACRÍLICA COR BRANCO FOSCO.
3. PAREDES EXTERNAS SEM INDICAÇÃO DE REVESTIMENTO RECEBERÃO PINTURA TERRACOR PREDIAL BRANCO
4. SOLEIRAS DAS PORTAS DOS APARTAMENTOS EM PEÇA ÚNICA SEGUINDO ESPECIFICAÇÃO DO PISO DA CIRCULAÇÃO COMUM

PROJETO ARQUITETÔNICO
MAUI

6/18

INTERIORES AMBIENTAÇÃO - RTOP E. GOURMET

ETAPA	OUZ_MAUI_ARQ_PROJETO EXECUTIVO AMBIENTAÇÃO	A1 EST.
DATA	14/03/2025	
ESCALA	1:25, 1:50	

ENDEREÇO: Rodovia SC-406, s/n, Praia Mole, Florianópolis, Santa Catarina

ASSINATURA:
CLIENTE: OUZ
CPF/CNPJ:

ASSINATURA:
RESPONSÁVEL: HENRIQUE PIMONT
CAU A 20832-9

DESENHO: MAYCON PASSIG; ARTHUR ANDRADE; MIRELA MOSER

PIMONT ARQUITETURA

RUA ALVES DE BRITO, 141 - SALA 701
CENTRO - FLORIANÓPOLIS - SC
CEP: 88015-440

TELEFONE: 48 30251200
CELULAR: 48 99806485

WWW.PIMONTARQUITETURA.COM.BR
CONTATO@PIMONTARQUITETURA.COM.BR