


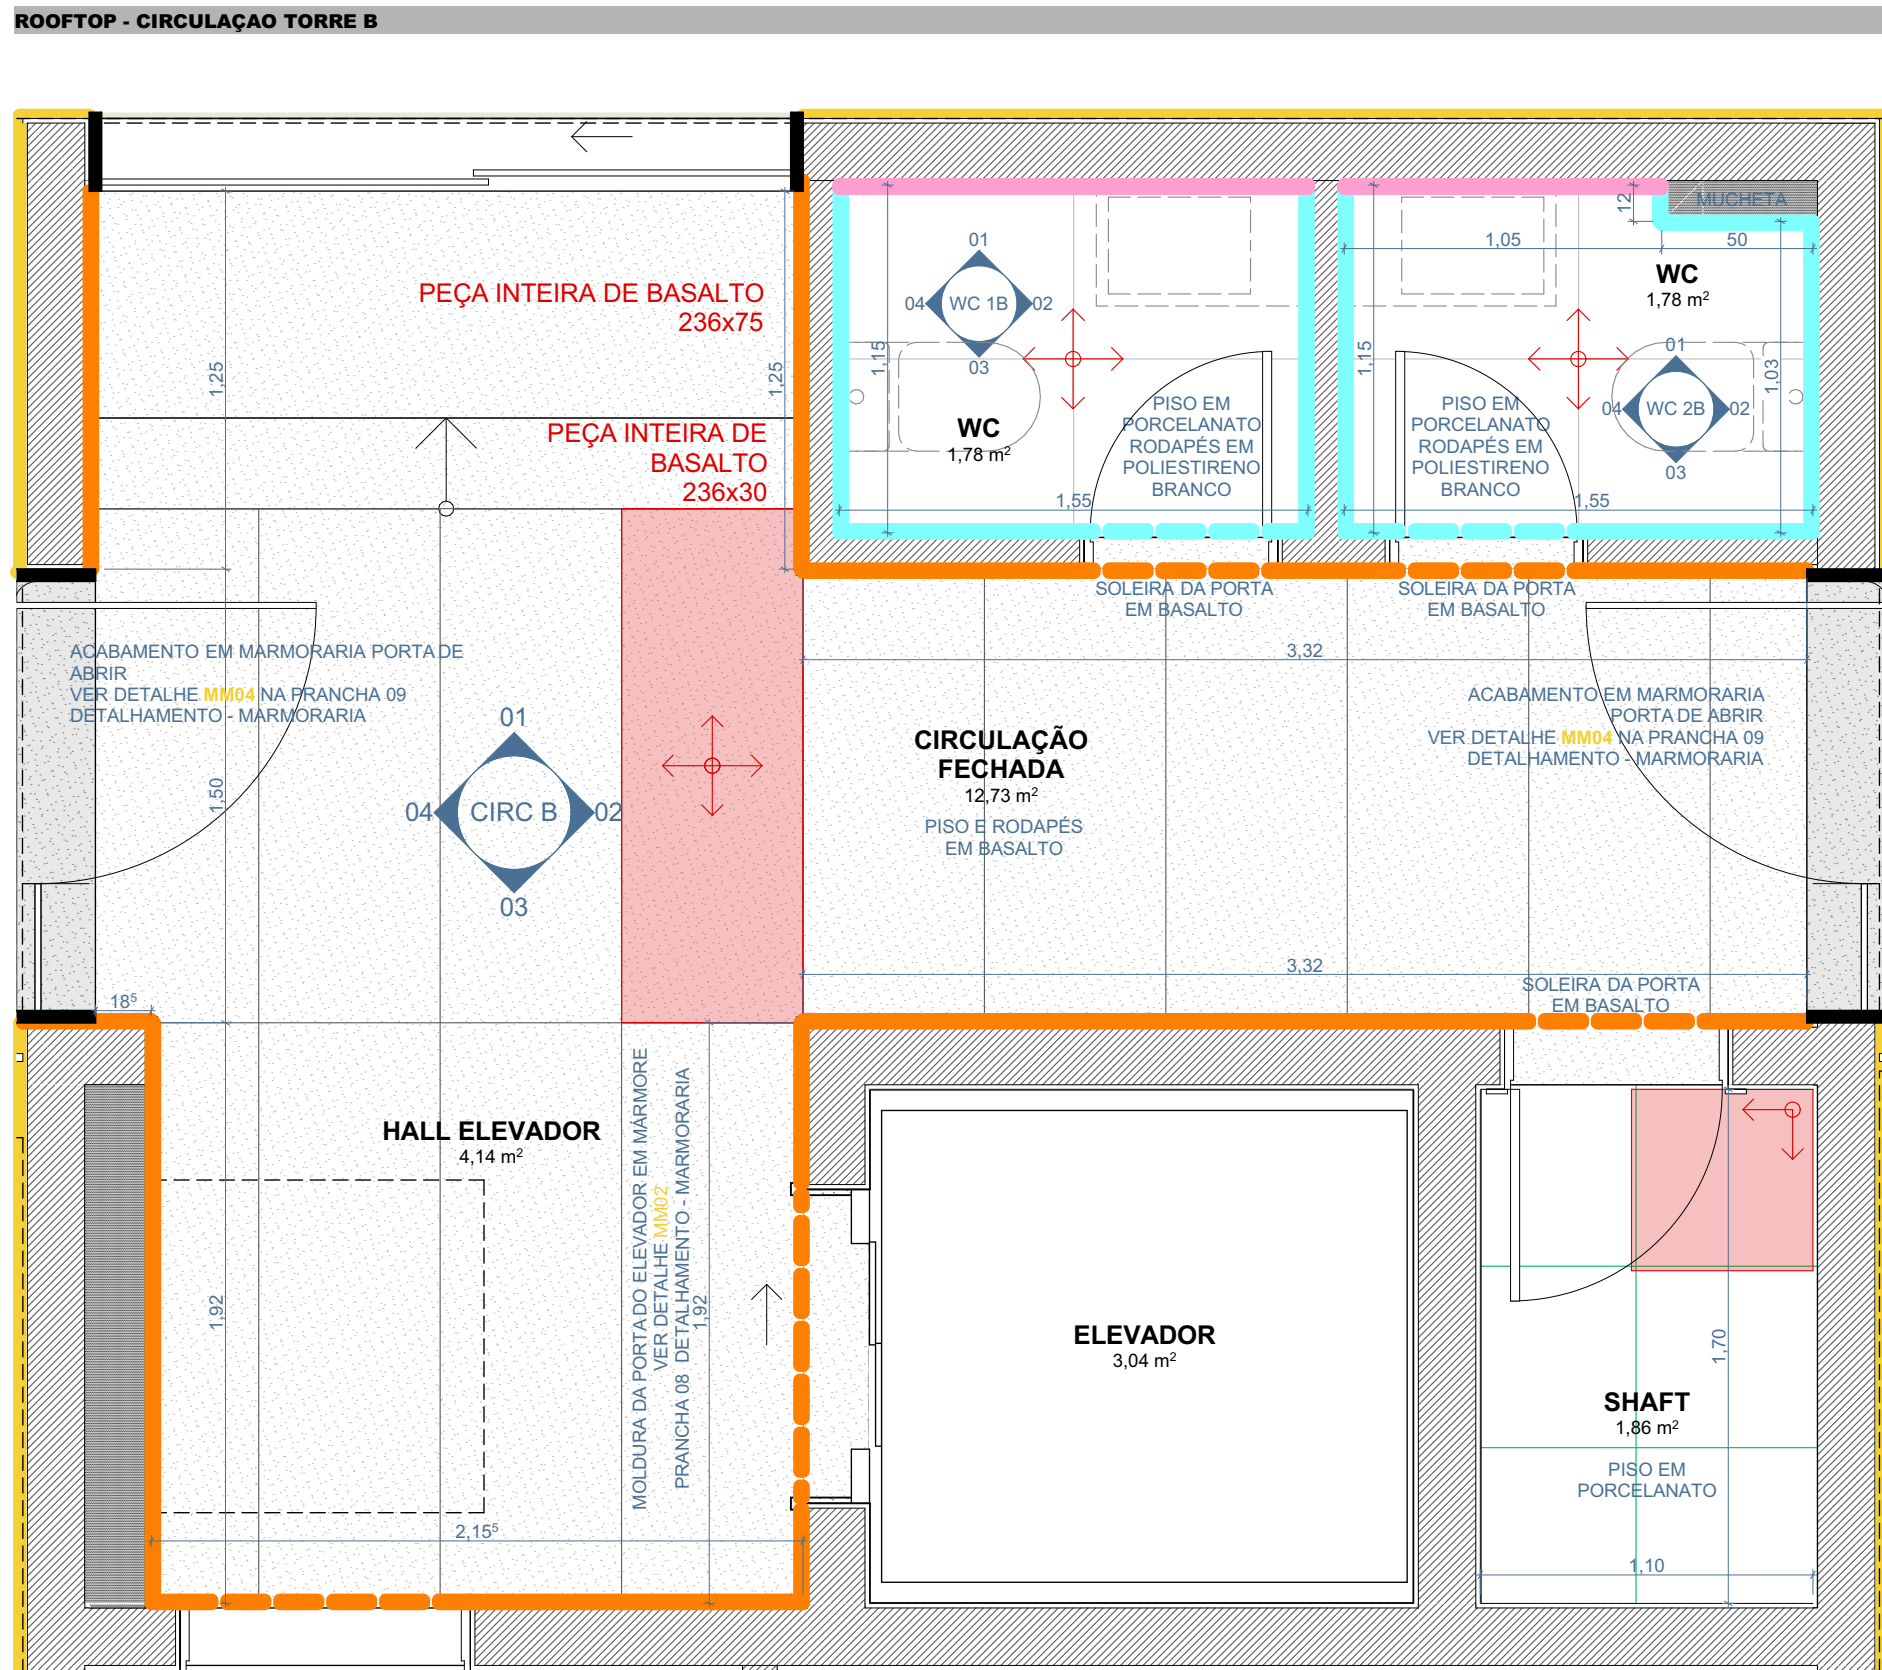
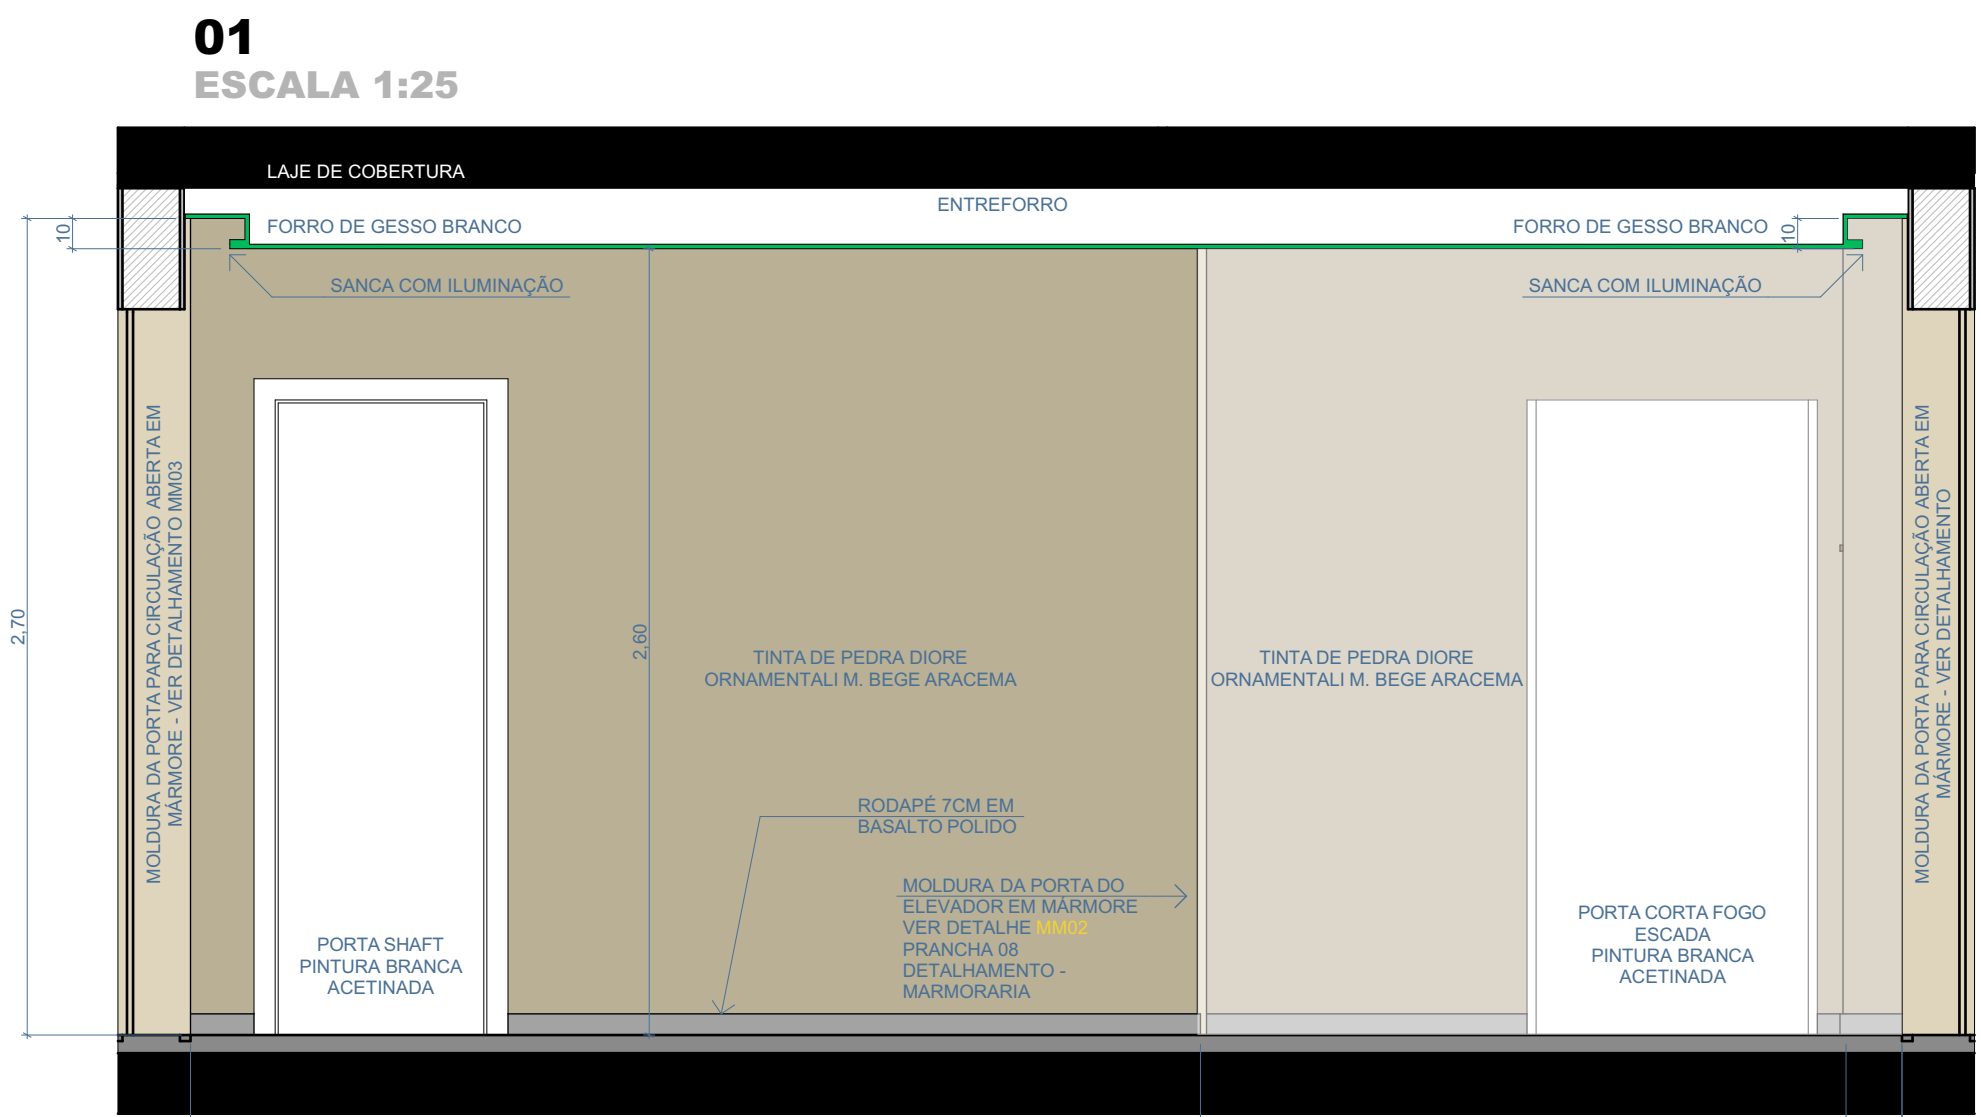


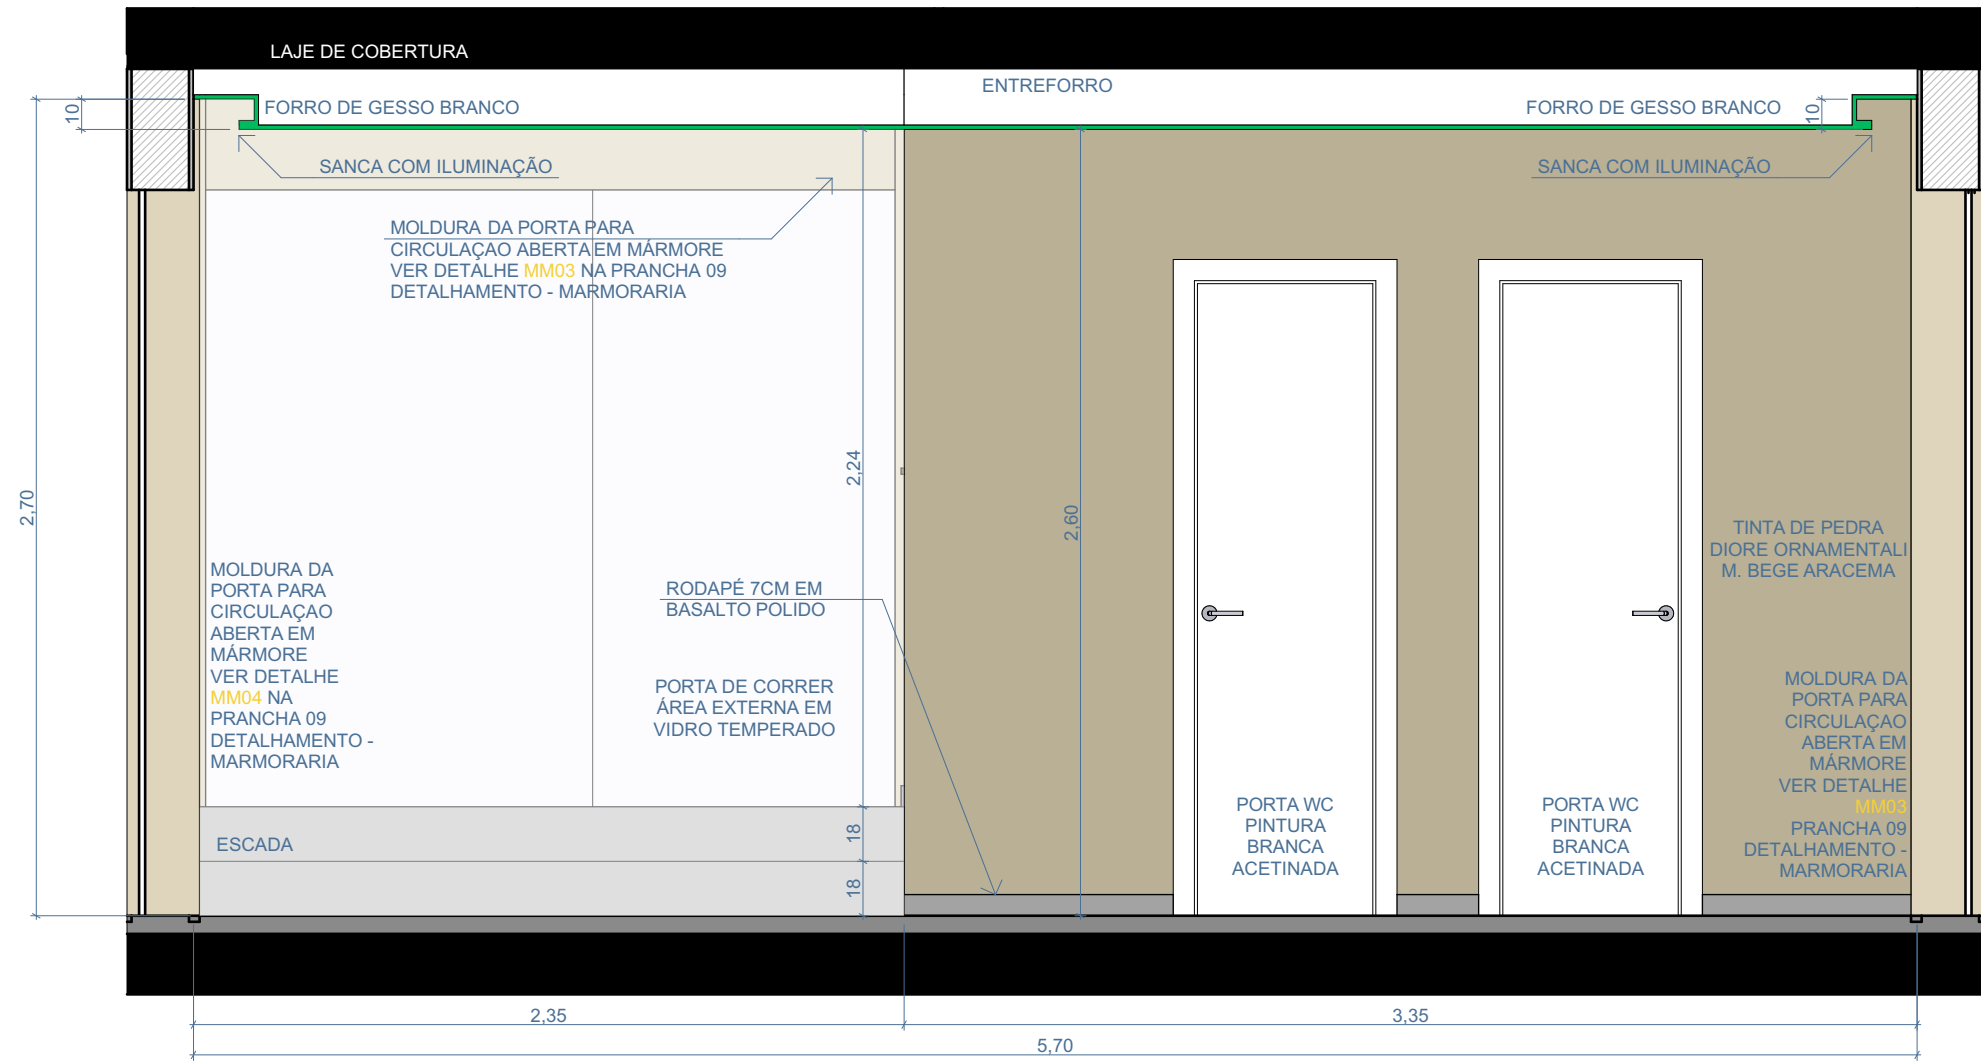

PLANTA BAIXA
ESCALA 1:25

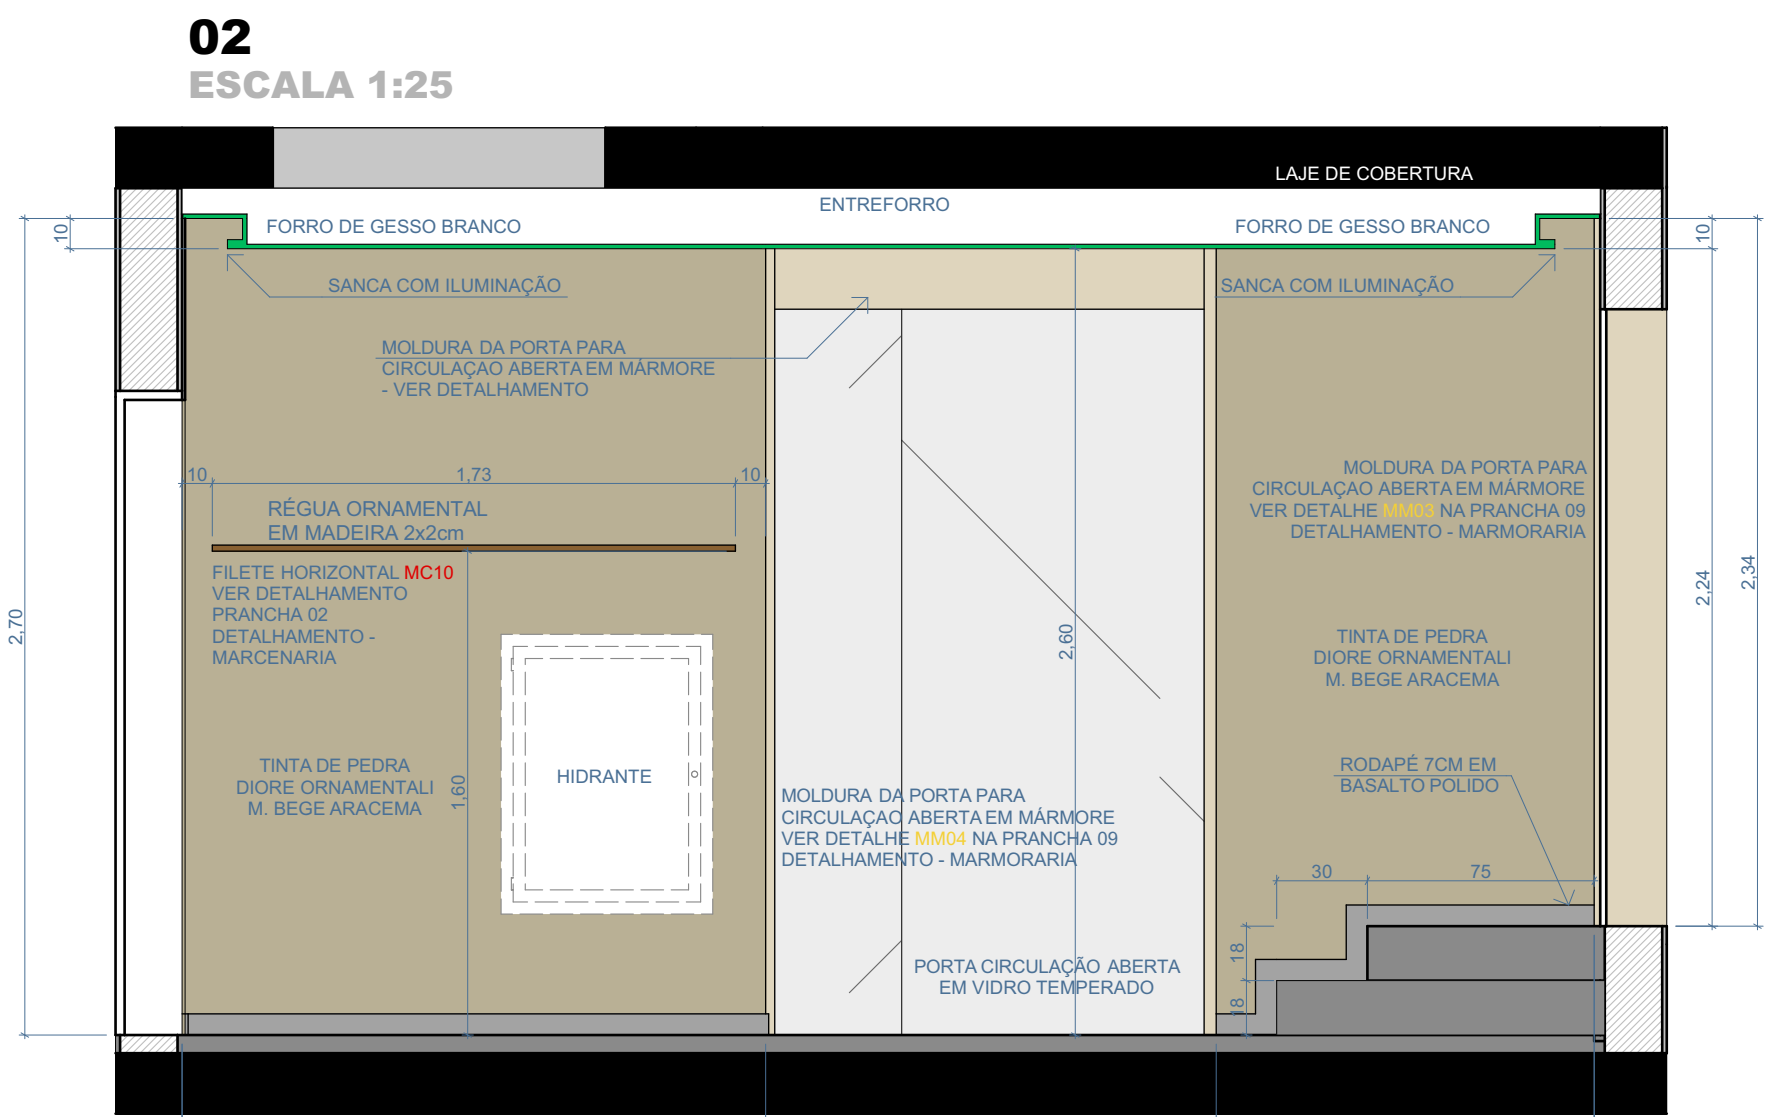

03
ESCALA 1:25

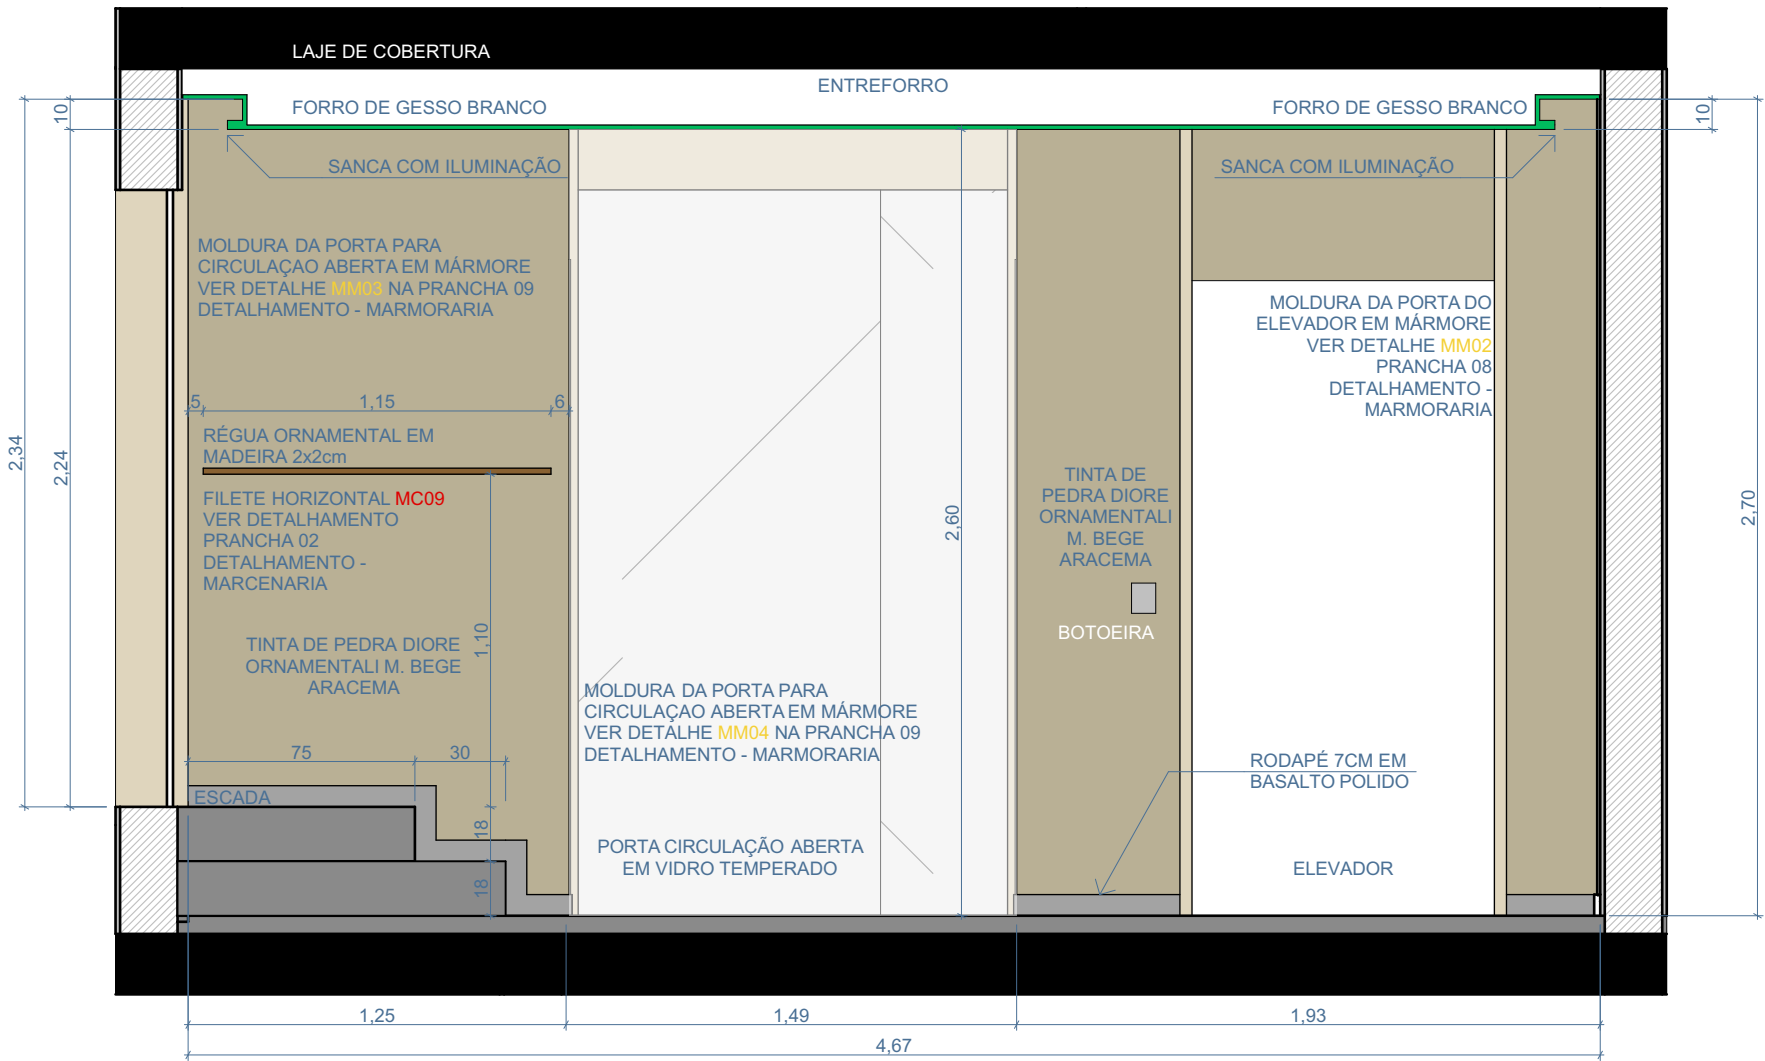


04
ESCALA 1:25

LEGENDA REVESTIMENTOS	
	PLACA DE CONCRETO 50x50
	PETIT PAVÉ BRANCO
	PETIT PAVÉ PRETO
	CIMENTO ALISADO
	CONCRETO VASSOURADO
	PORCELANATO 60x120
	PORCELANATO 60x60
	PORCELANATO 90x90
	PISO DE MADEIRA
	DECK DE MADEIRA
	PISO ESPORTIVO EMBORRACHADO EM PLACAS 100x100
	BASALTO RÚSTICO
	BASALTO POLIDO
	PISO CIMENTÍCIO SOLARIUM 50x50
	AZULEJO 30x60 BRANCO ACETINADO RETIFICADO
	TINTA DE PEDRA DIORE DELICATO PRECIOSA COR NATURAL
	TINTA DE PEDRA DIORE ORNAMENTAL MAXI COR BEGE ARACEMA
	TEXTURA TERRACOZ PREDIAL PRETO
	PINTURA ACRÍLICA PRETA - SUVINIL PATATIVA
	BASALTO POLIDO
	REVESTIMENTO EM PEDRA NATURAL MOLEDO
	REVESTIMENTO EM LÂMINA PRELO
	COMPENSADO VIROLA
	ESPELHO CRISTAL COLADO

NOTAS

1. PILARES DA GARAGEM E MURETAS DO ACESSO SÃO EM CONCRETO APARENTE;
2. PAREDES INTERNAS SEM INDICAÇÃO DE REVESTIMENTO RECEBERÃO PINTURA ACRÍLICA COR BRANCO FOSCO;
3. PAREDES EXTERNAS SEM INDICAÇÃO DE REVESTIMENTO RECEBERÃO PINTURA TERRACOZ PREDIAL BRANCO;
4. SOLZEIRAS DAS PORTAS DOS APARTAMENTOS EM PEÇA ÚNICA SEGUINDO ESPECIFICAÇÃO DO PISO DA CIRCULAÇÃO COMUM

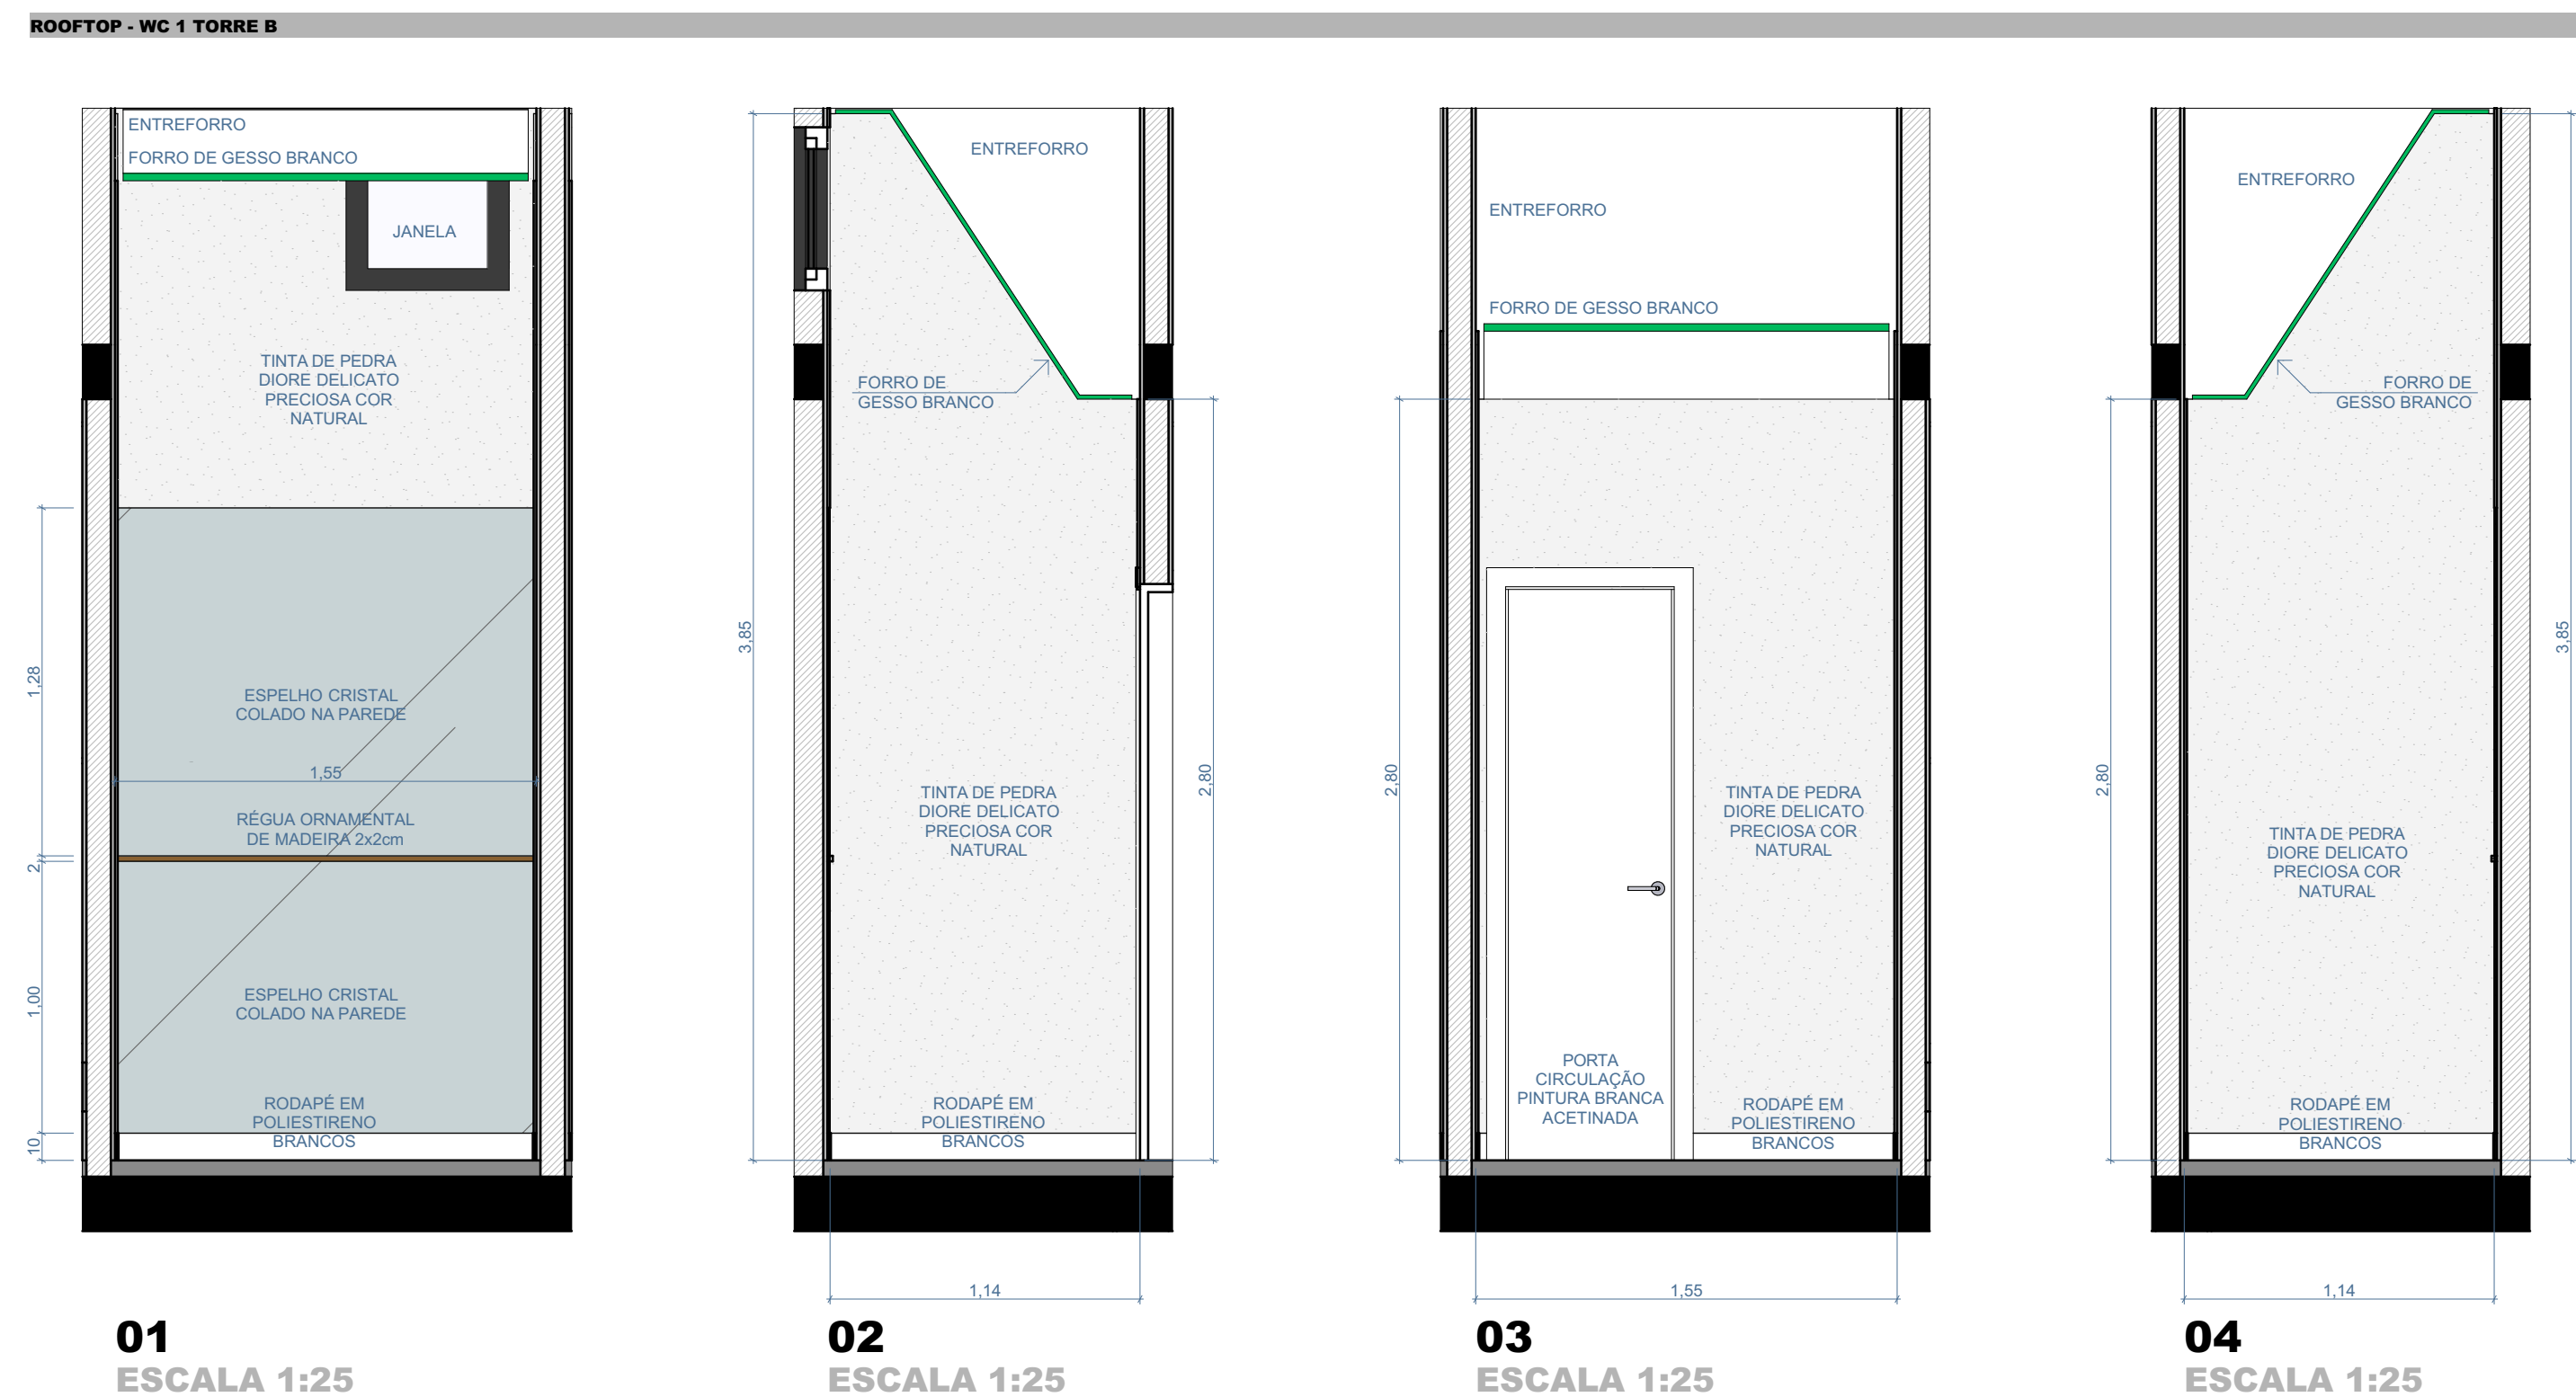


01
ESCALA 1:25

02
ESCALA 1:25

03
ESCALA 1:25

04
ESCALA 1:25

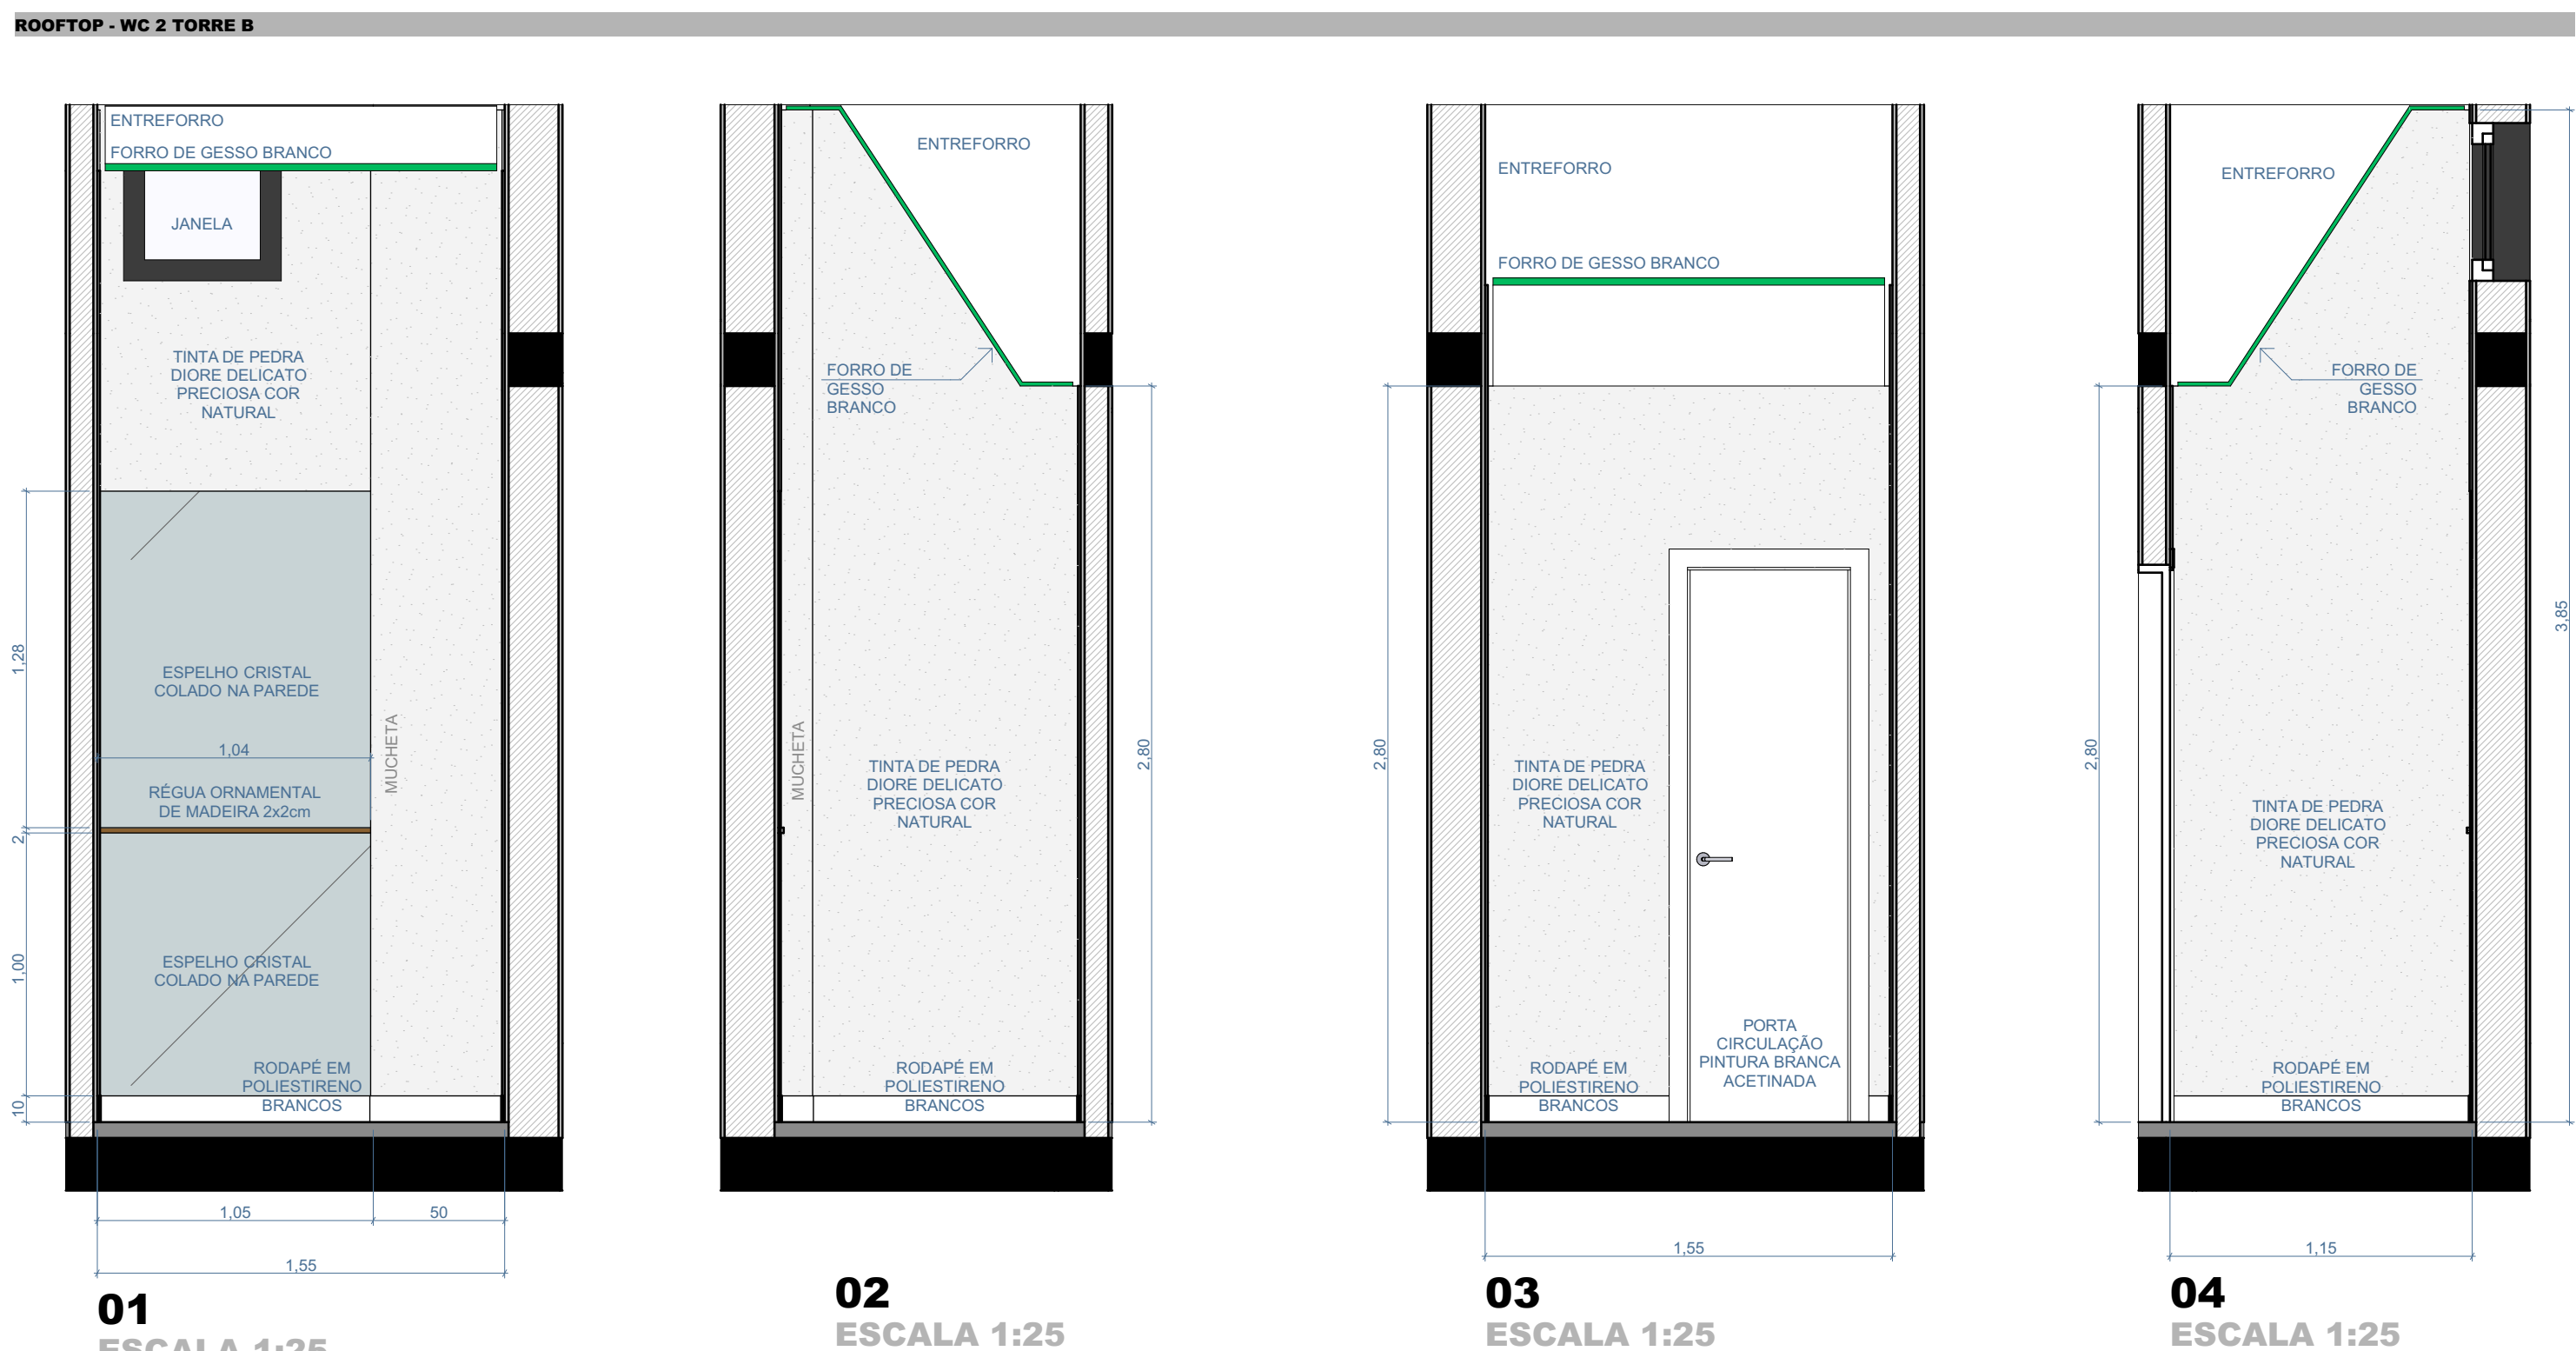

01
ESCALA 1:25

02
ESCALA 1:25

03
ESCALA 1:25

04
ESCALA 1:25

PROJETO ARQUITETÔNICO

MAUI

INTERIORES AMBIENTAÇÃO - RTOP HALL | WCS

TORRE B

ETAPA	OUZ_MAU_ARQ_PROJETO EXECUTIVO AMBIENTAÇÃO	A1 EST.
DATA	14/03/2025	
ESCALA	1:25, 1:50	

ENDEREÇO Rodovia SC-406, s/n, Praia Mole, Florianópolis, Santa Catarina

ASSINATURA: _____
CLIENTE OUZ
CPF/CNPJ: _____

ASSINATURA: _____
RESPONSÁVEL: HENRIQUE PIMONT
CAU A 20832-9

DESENHO: MAYCON PASSIG; ARTHUR ANDRADE; MIRELA MOSER

PIMONT
ARQUITETURA

RUA ALVES DE BRITO, 141 - SALA 701
CENTRO - FLORIANÓPOLIS - SC
CEP: 88015-440
TELEFONE: 48 30251200
CELULAR: 48 99804485

WWW.PIMONTARQUITETURA.COM.BR
CONTATO@PIMONTARQUITETURA.COM.BR