


MC15 | ENCONTRO DO RIPADO
COM PEÇA DE ACABAMENTO DO ELEVADOR

RIPADO DE MADEIRA MACIÇA SOBRE PAINEL DE MDF PRETO
RESISTENTE À UMIDADE (ULTRA)

04 UNIDADES

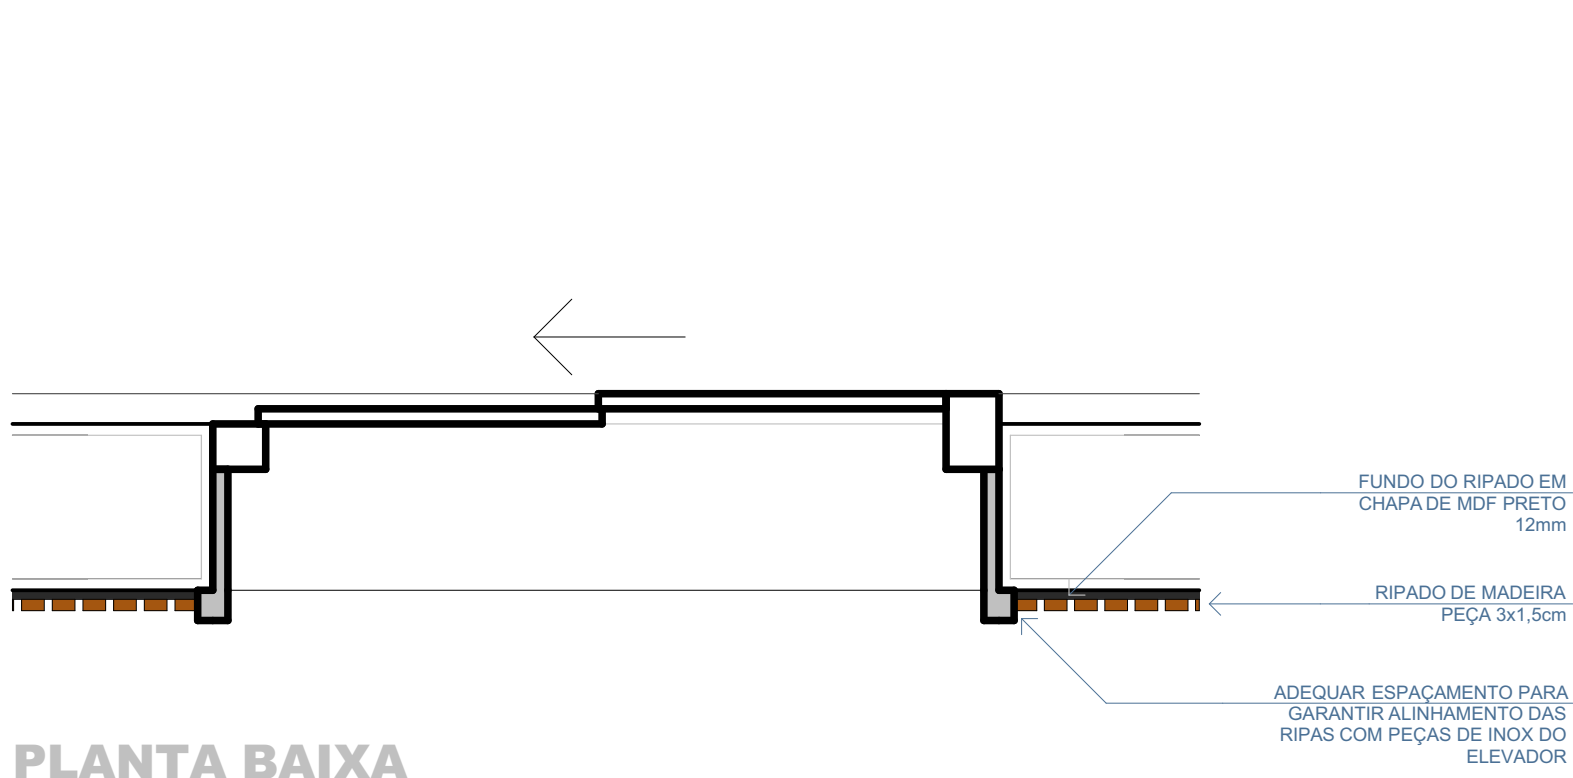


PLANTA BAIXA

MC16 | PORTA MIMETIZADA
PARA O SHAFT

RIPADO DE MADEIRA MACIÇA SOBRE PAINEL DE
MDF PRETO RESISTENTE À UMIDADE (ULTRA)

04 UNIDADES

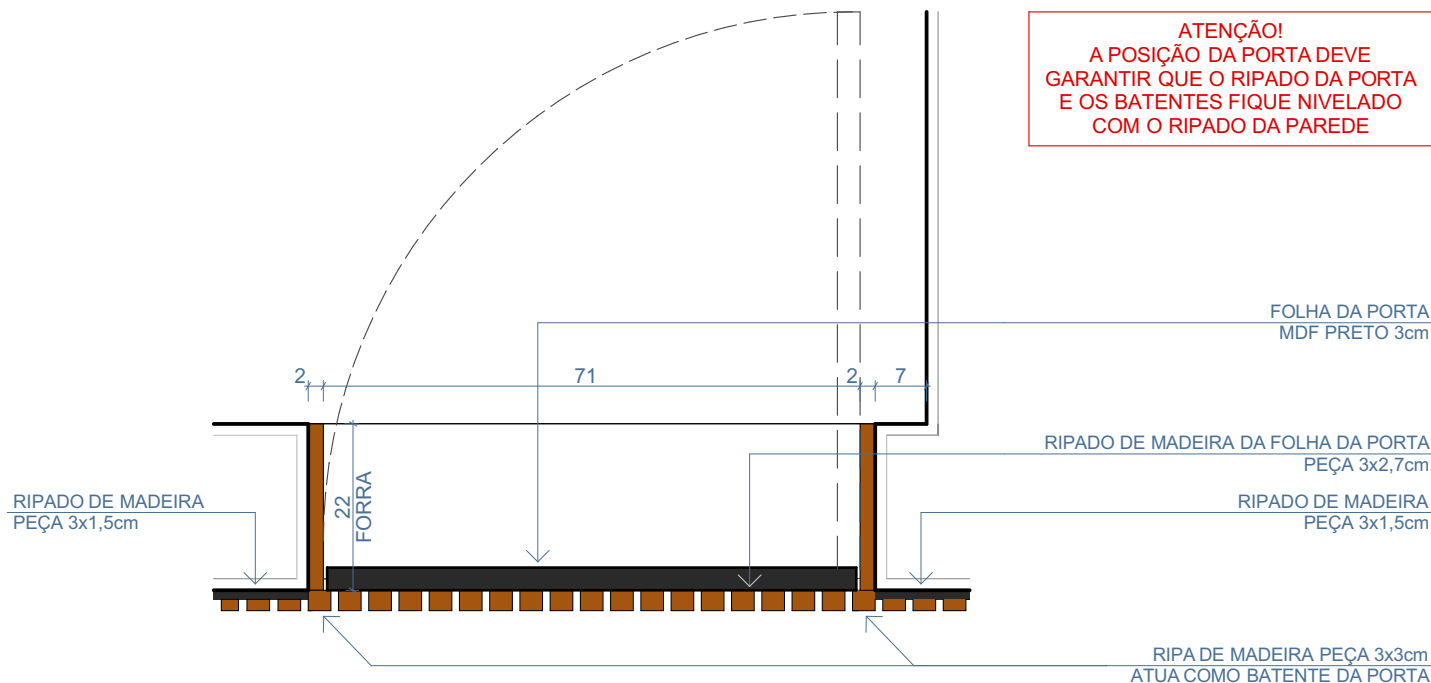


PLANTA BAIXA


MC17 | RIPA VERTICAL E LOGO APTOS.

RIPADO DE MADEIRA MACIÇA SOBRE PAINEL DE MDF PRETO RESISTENTE
À UMIDADE (ULTRA)


26 UNIDADES

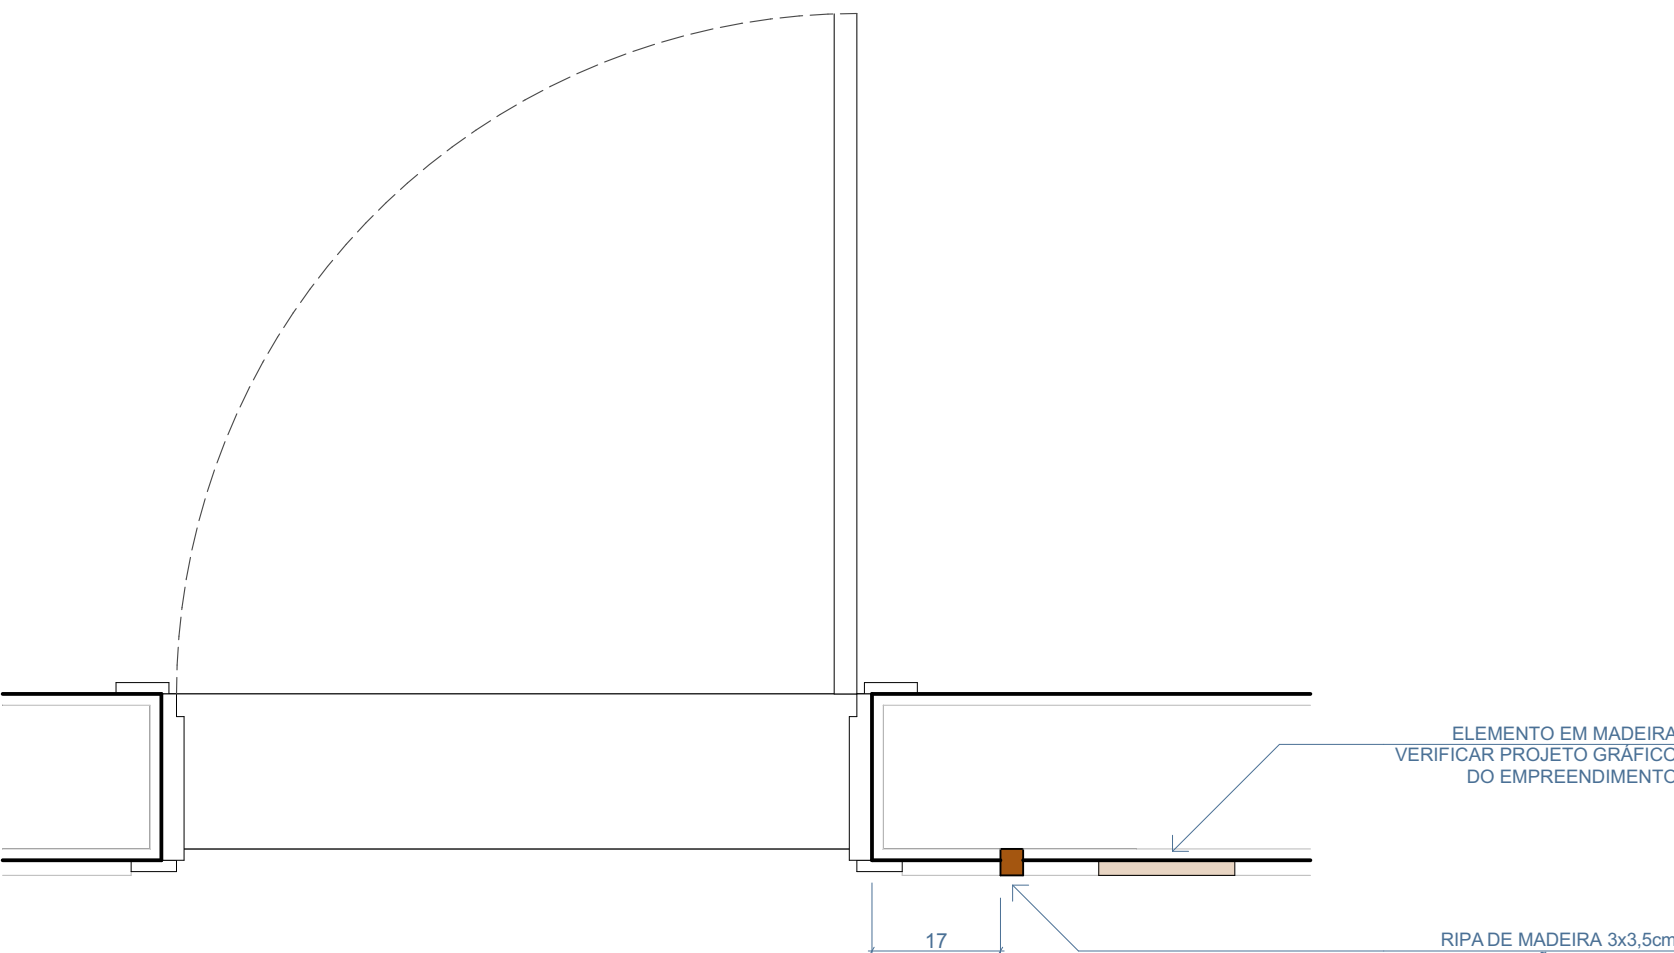


PLANTA BAIXA

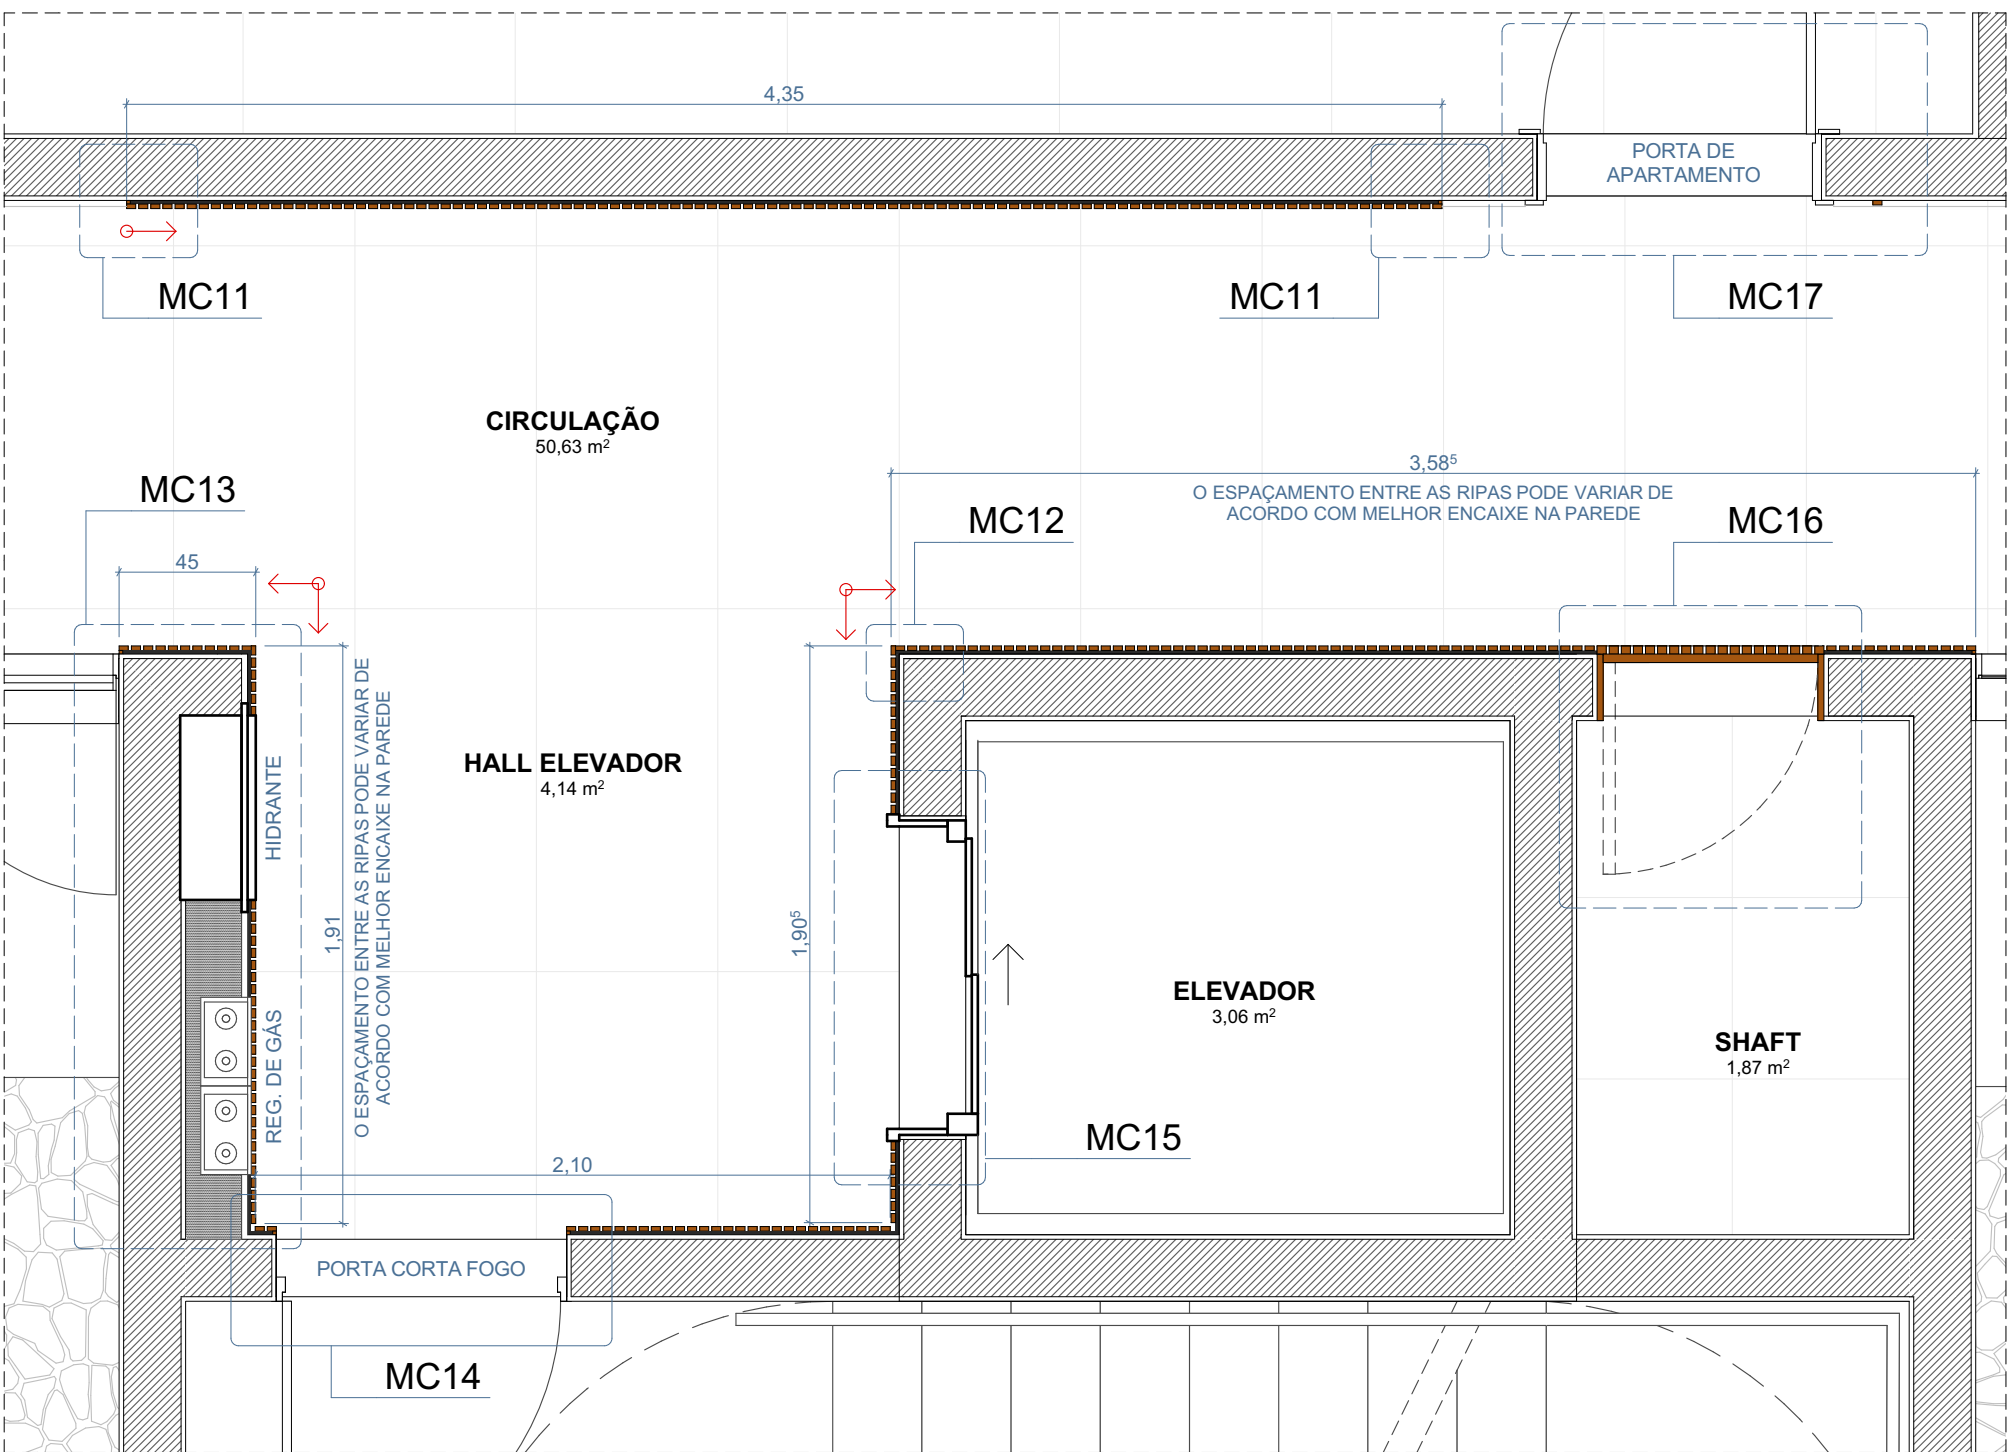


P.BAIXA HALL DOS ELEVADORES - PAGINAÇÃO E INDICAÇÃO DE DETALHES
ESCALA 1:25

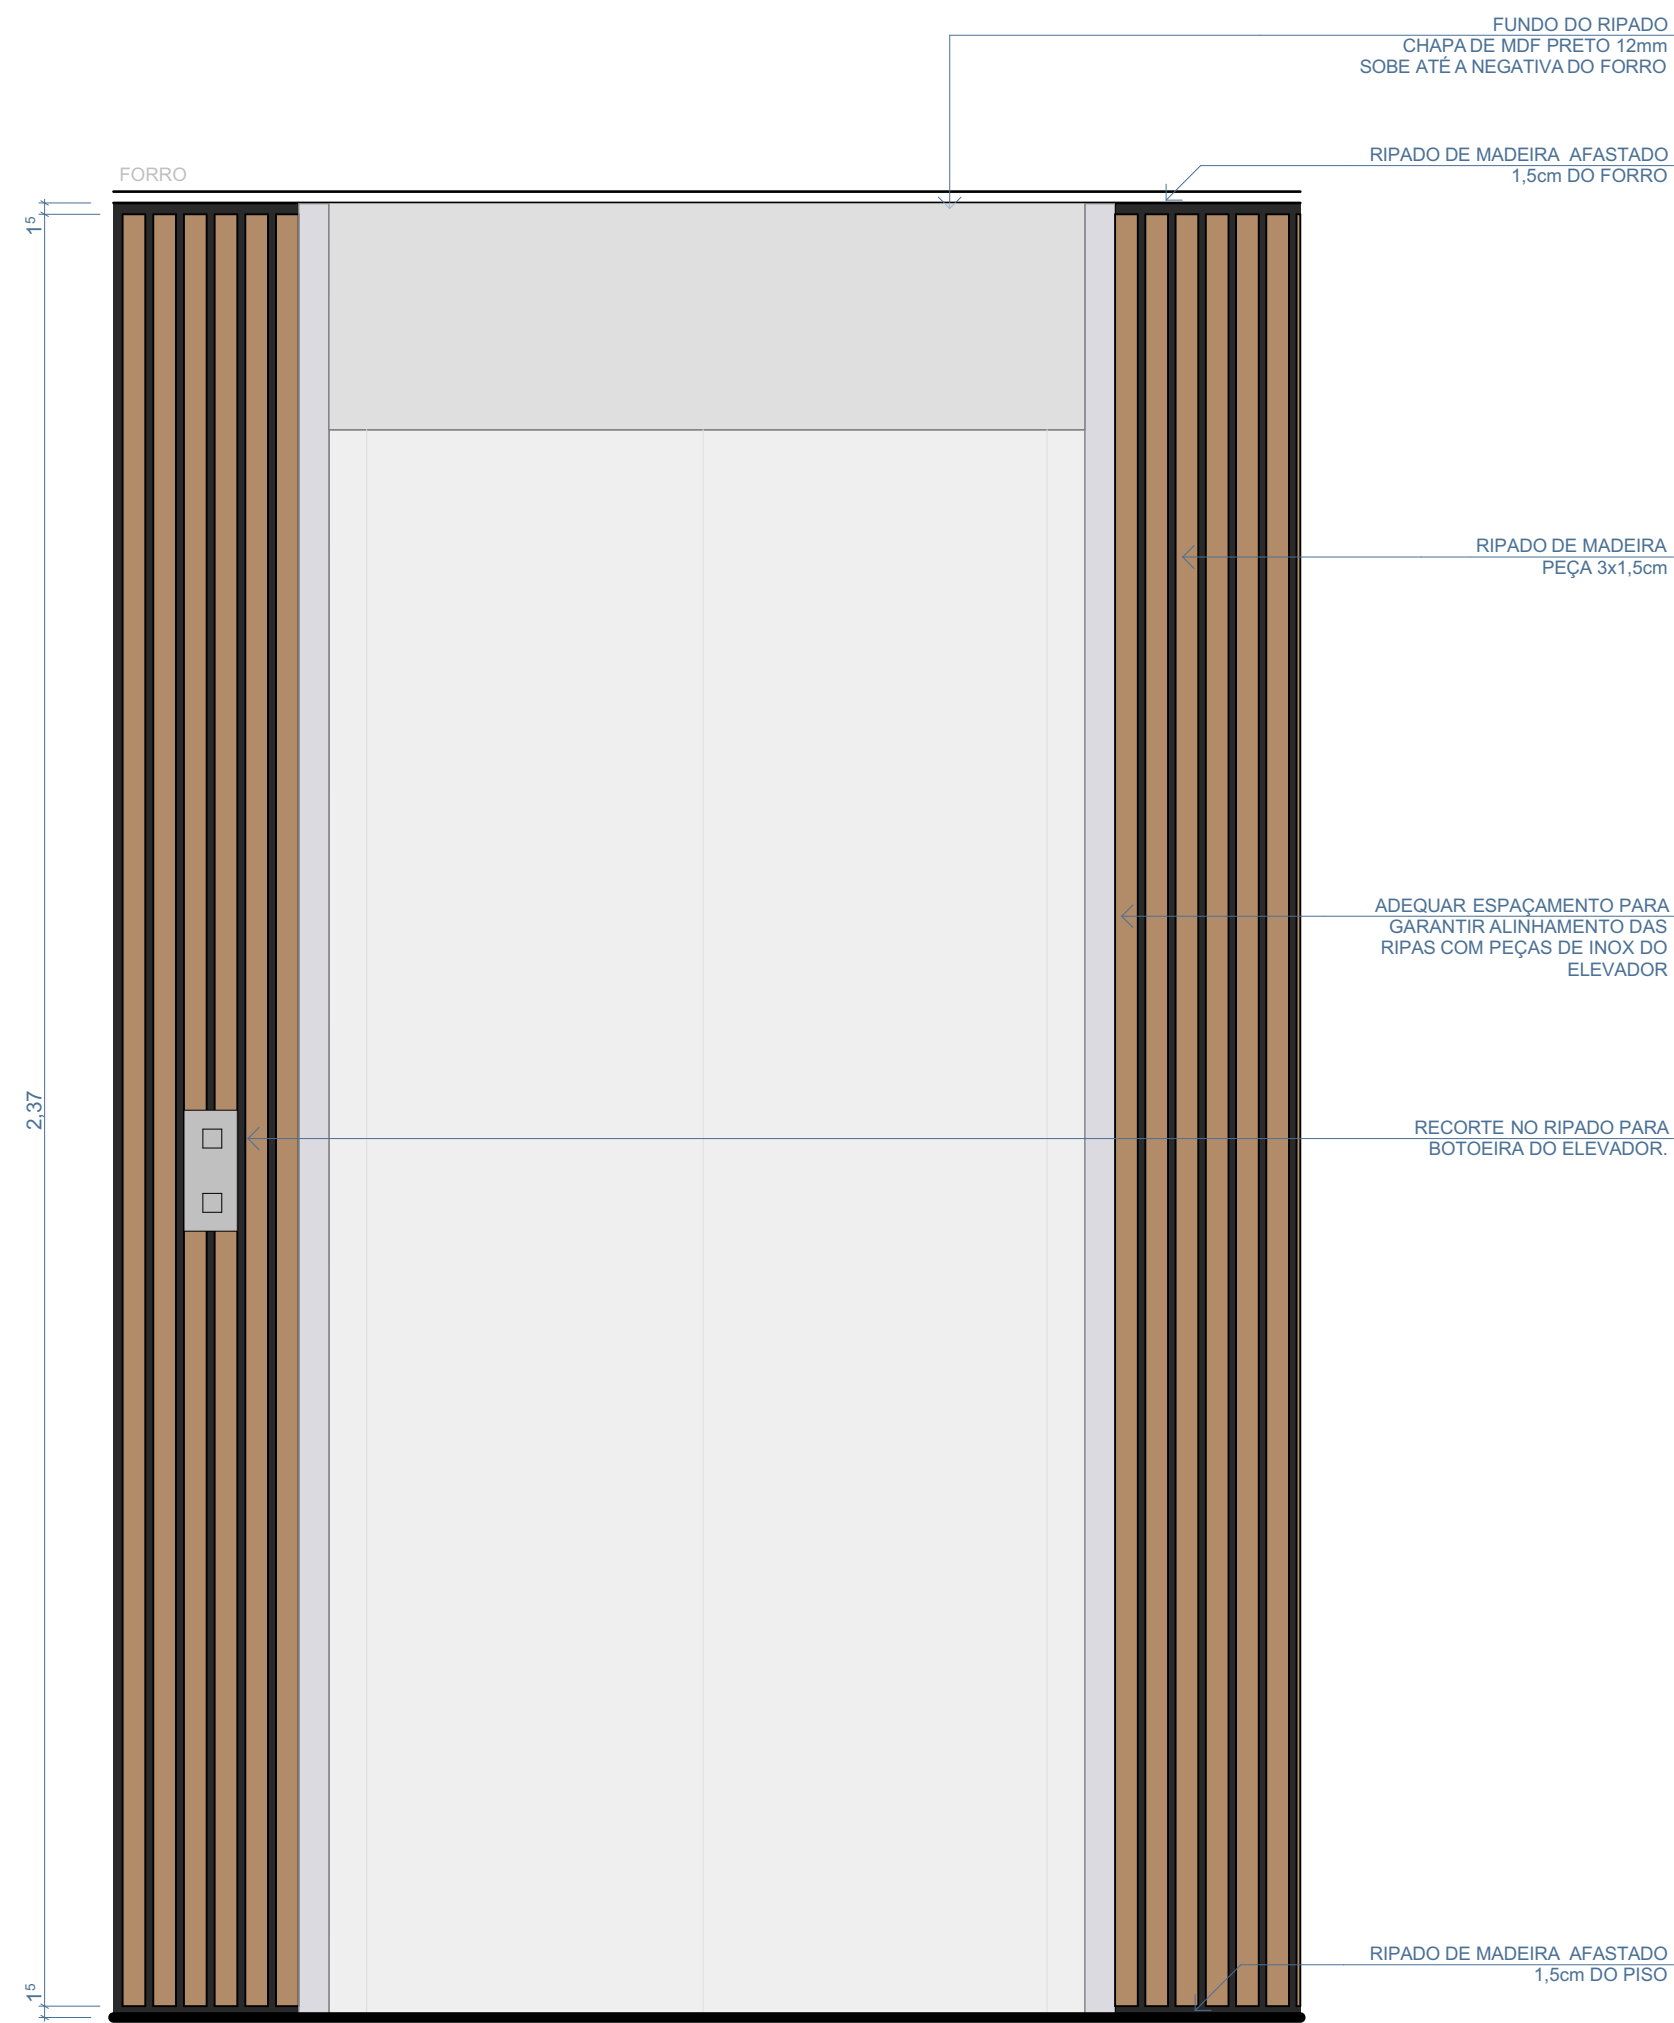


VISTA FRONTAL

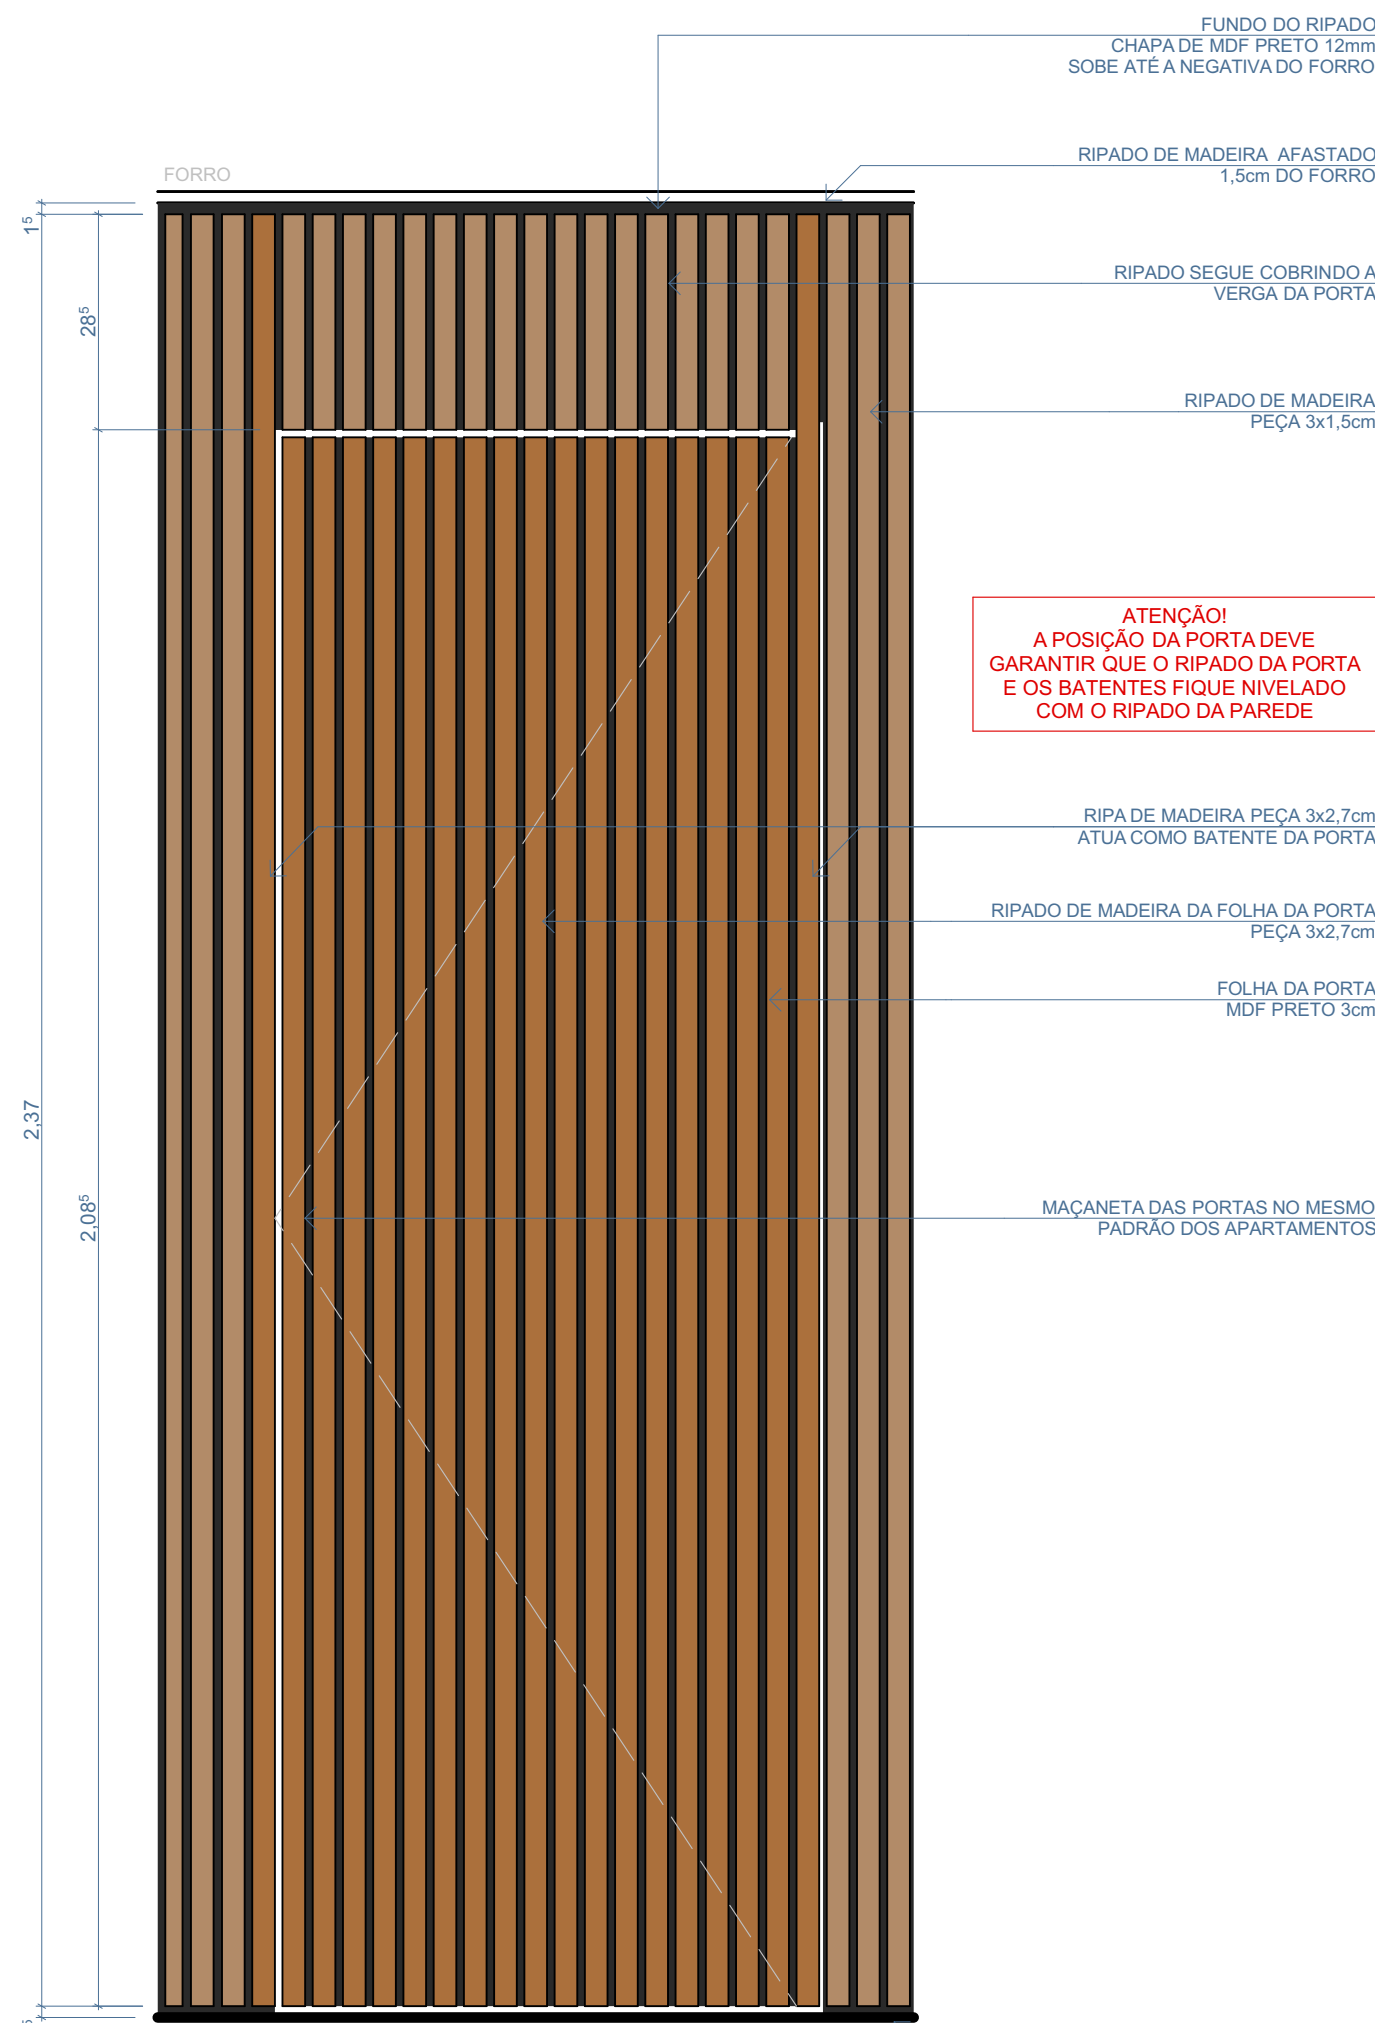

VISTA FRONTAL

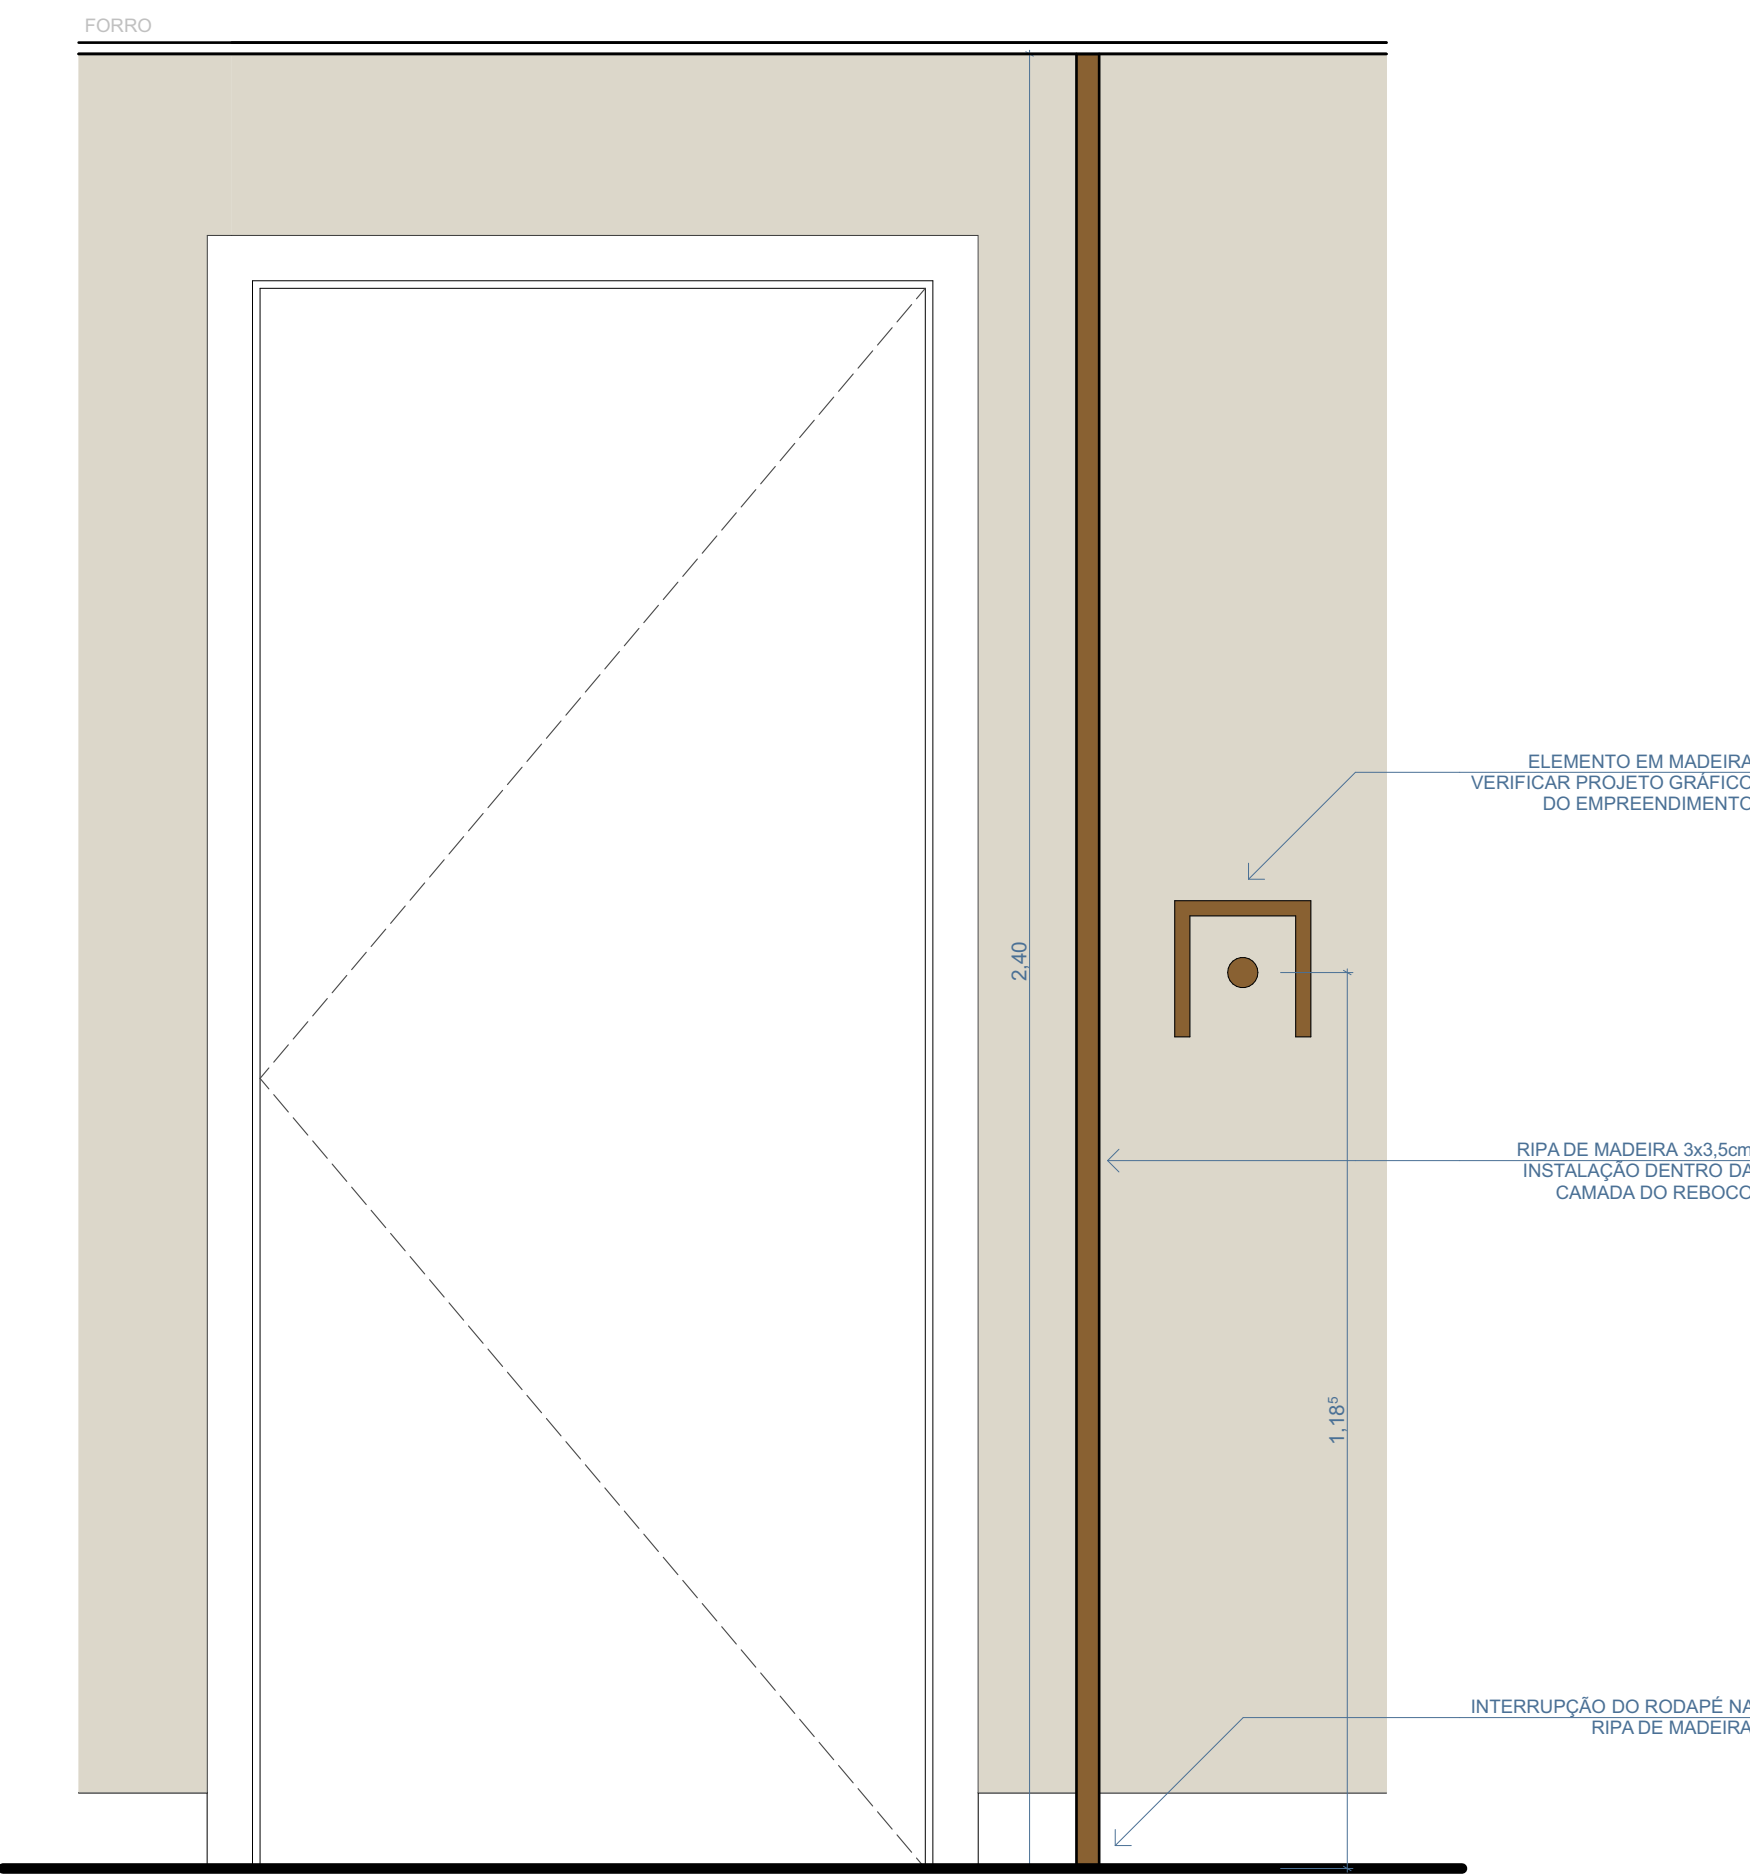

VISTA FRONTAL

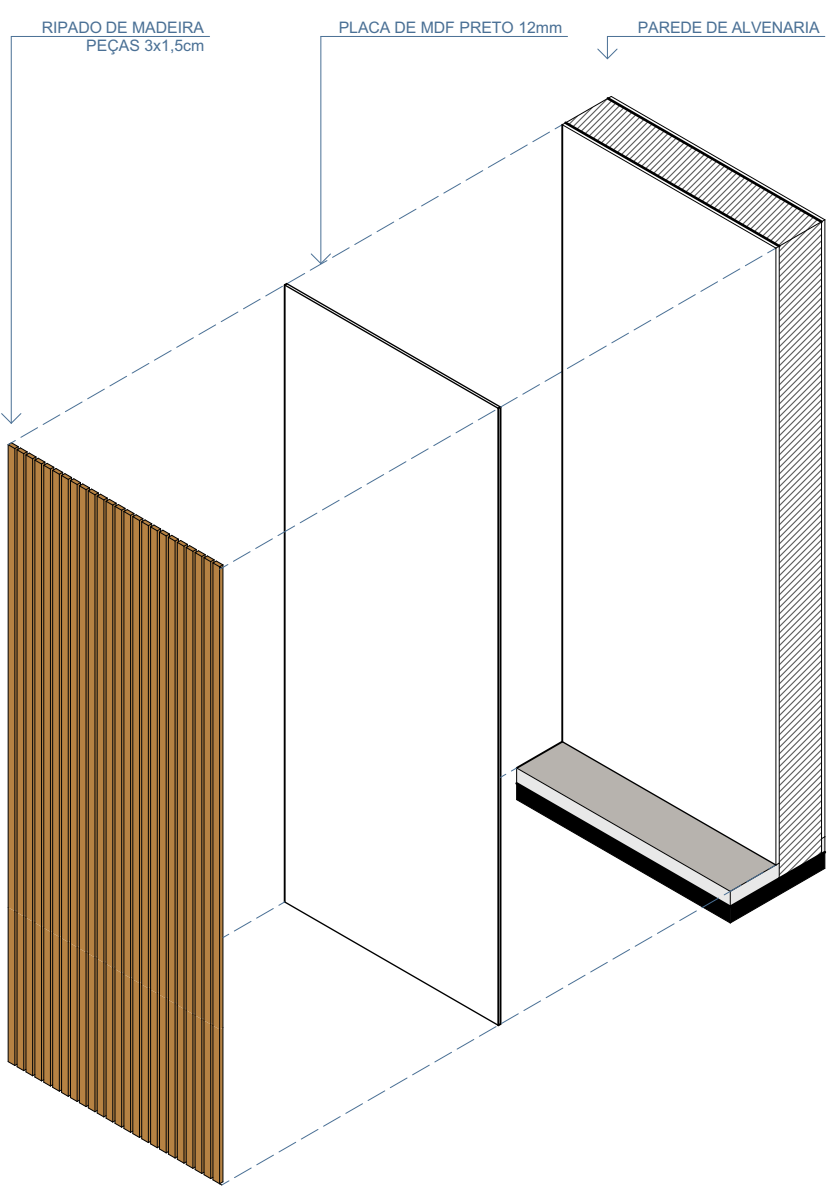

ISOMÉTRICA - RIPADO

PROJETO ARQUITETÔNICO

MAUI
INTERIORES DETALHAMENTO - MARCENARIA -
RIPADOS PAV. TIPO

ETAPA	OUZ MAUI_ARQ_PROJETO EXECUTIVO DETALHAMENTOS	A1 EST.
DATA	AMBIENTAÇÃO 13/03/2025	
ESCALA	1:25, 1:10	
ENDEREÇO	Rodovia SC-406, s/n, Praia Mole, Florianópolis, Santa Catarina	
ASSINATURA:		
CLIENTE	OUZ CPF/CNPJ:	
ASSINATURA:		
RESPONSÁVEL:	HENRIQUE PIMONT CAU A 20832-9	
DESENHO:	MAYCON PASSIG; ARTHUR ANDRADE; MIRELA MOSER	