



CP01 - PERGOLADO TERRAÇO - LOUNGE EXTERNO


MADEIRA MACIÇA
FIXAÇÕES E TRAVAMENTOS METÁLICOS
SISTEMA COMPLEMENTAR DE COBERTURA EM TECIDO RETRÁTIL

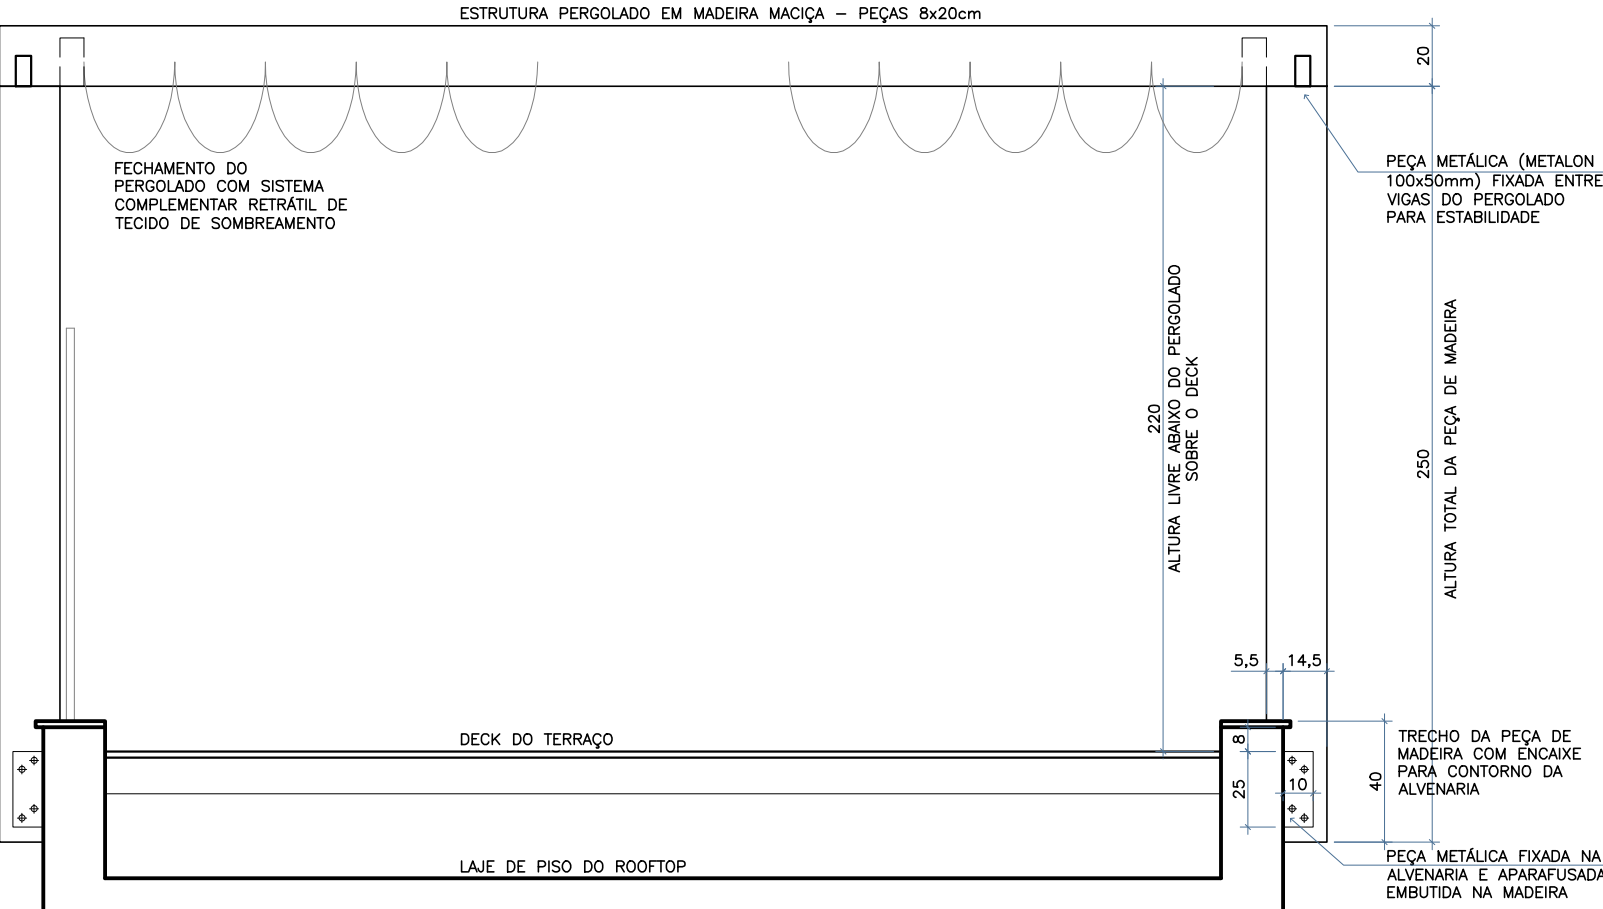

VISTA LATERAL

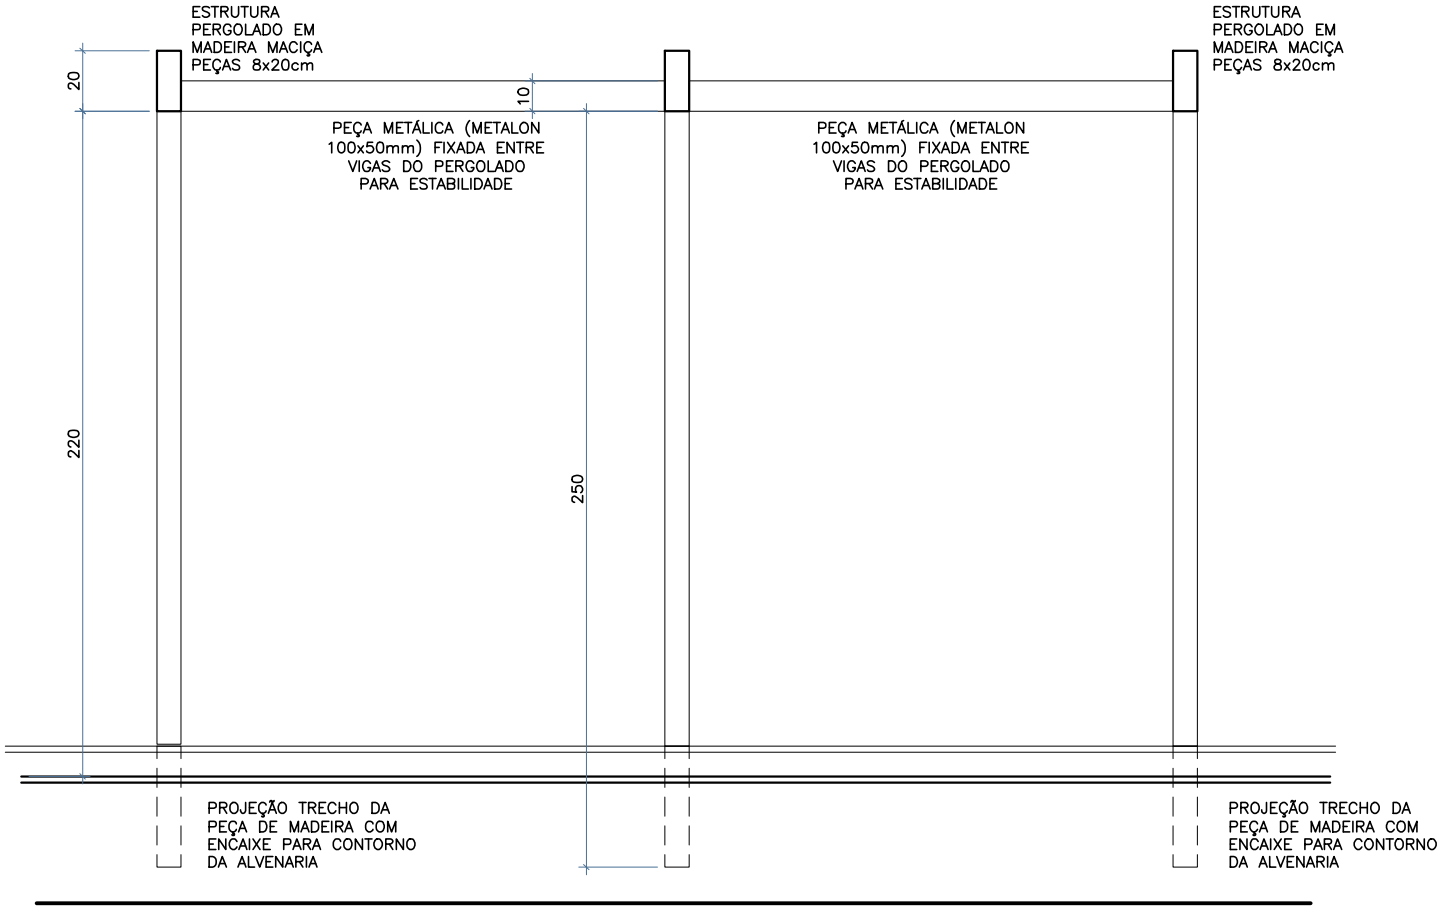

CORTE

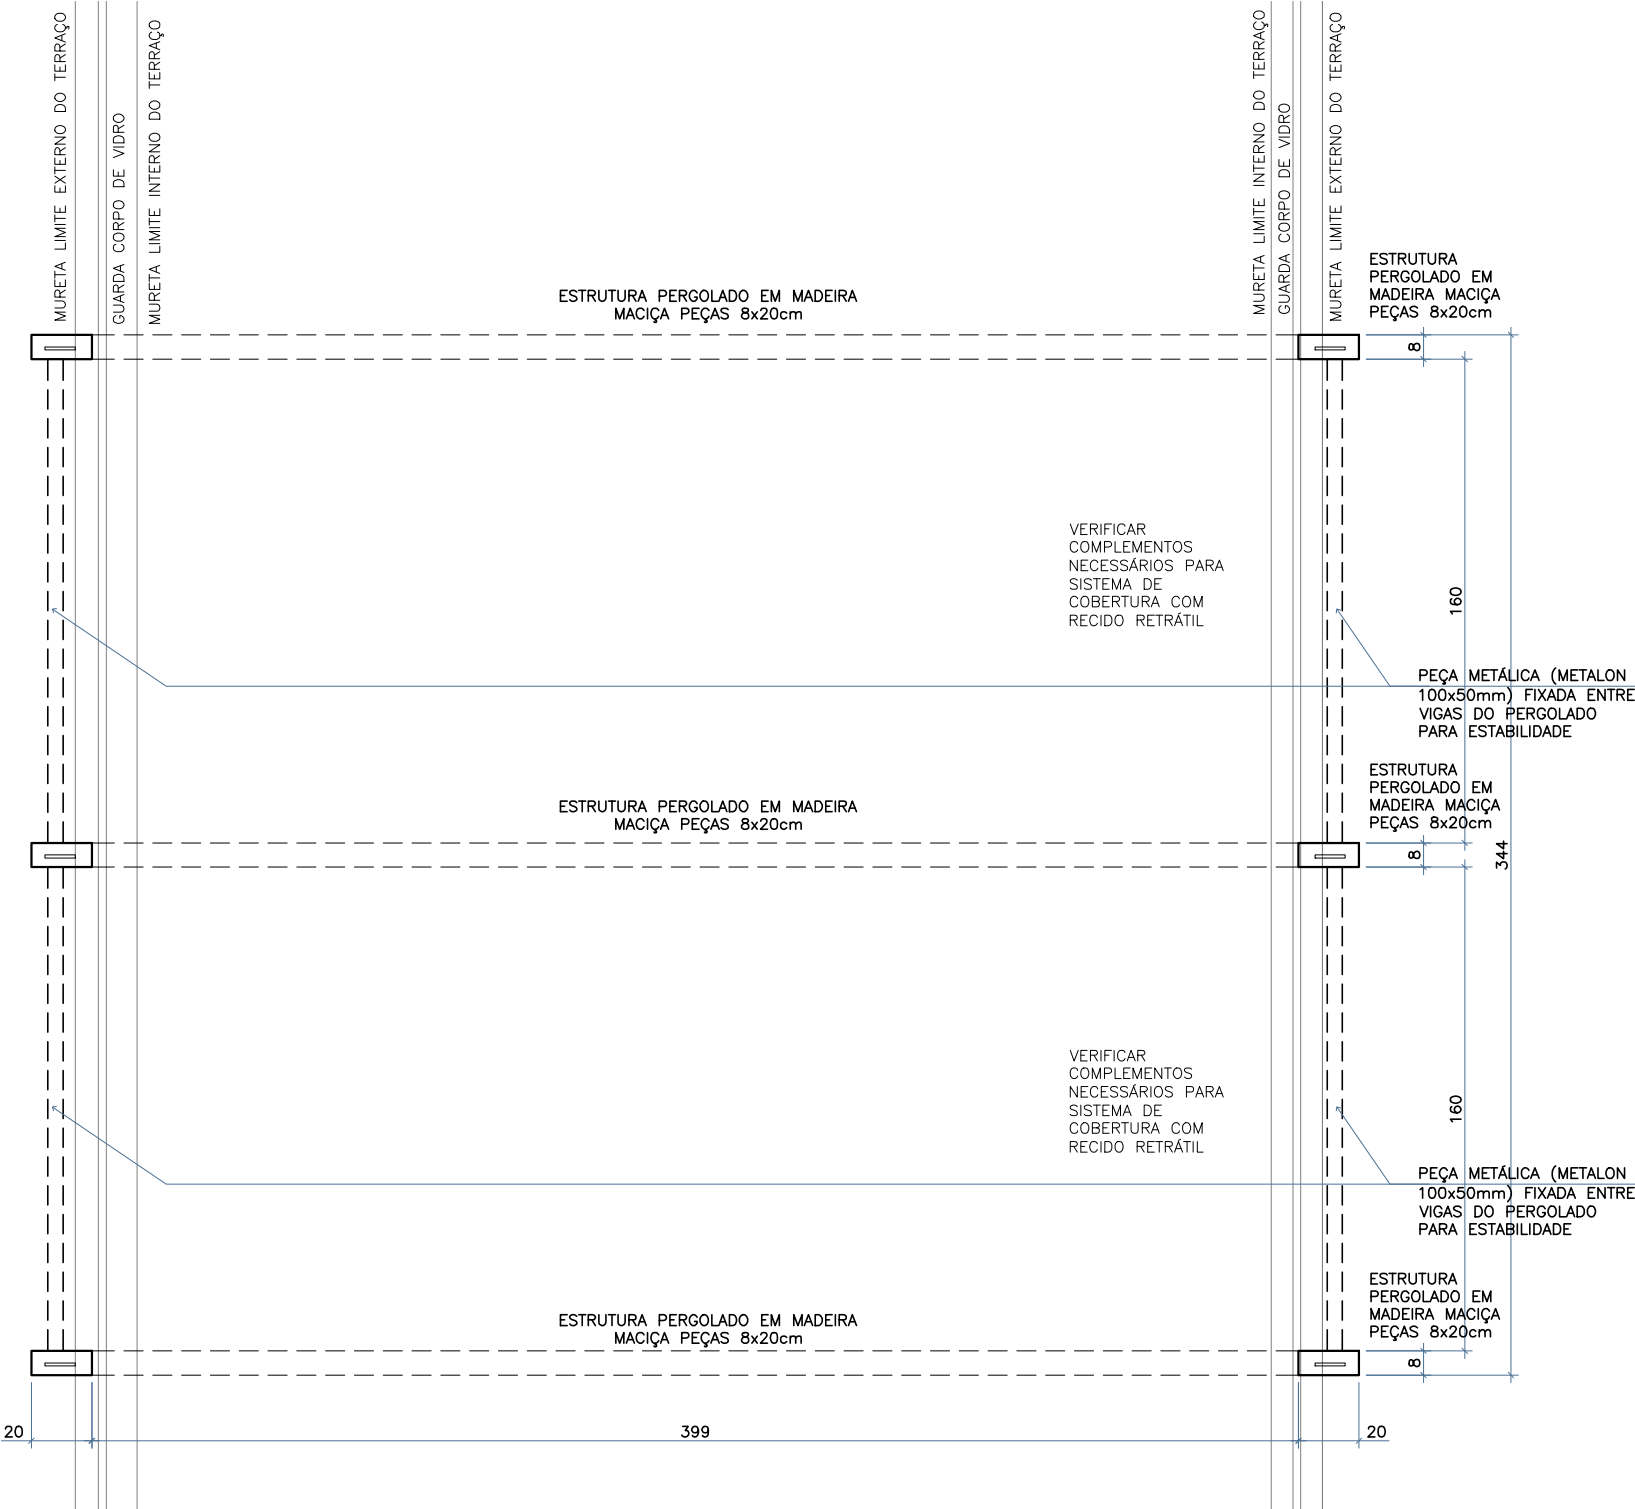

PLANTA BAIXA



ILUSTRAÇÃO TECIDO RETRÁTIL - MODELO ZEN FABRICANTE GAVIOTA

MAUI - INTERIORES - ROOFTOP

18 - PROJETO EXECUTIVO - DETALHAMENTO DE CARPINTARIA - PERGOLADO TERRAÇO LAGOA

ESCALA 1:25 - FOLHA A2