




ROOFTOP - CIRCULAÇÃO TORRE B

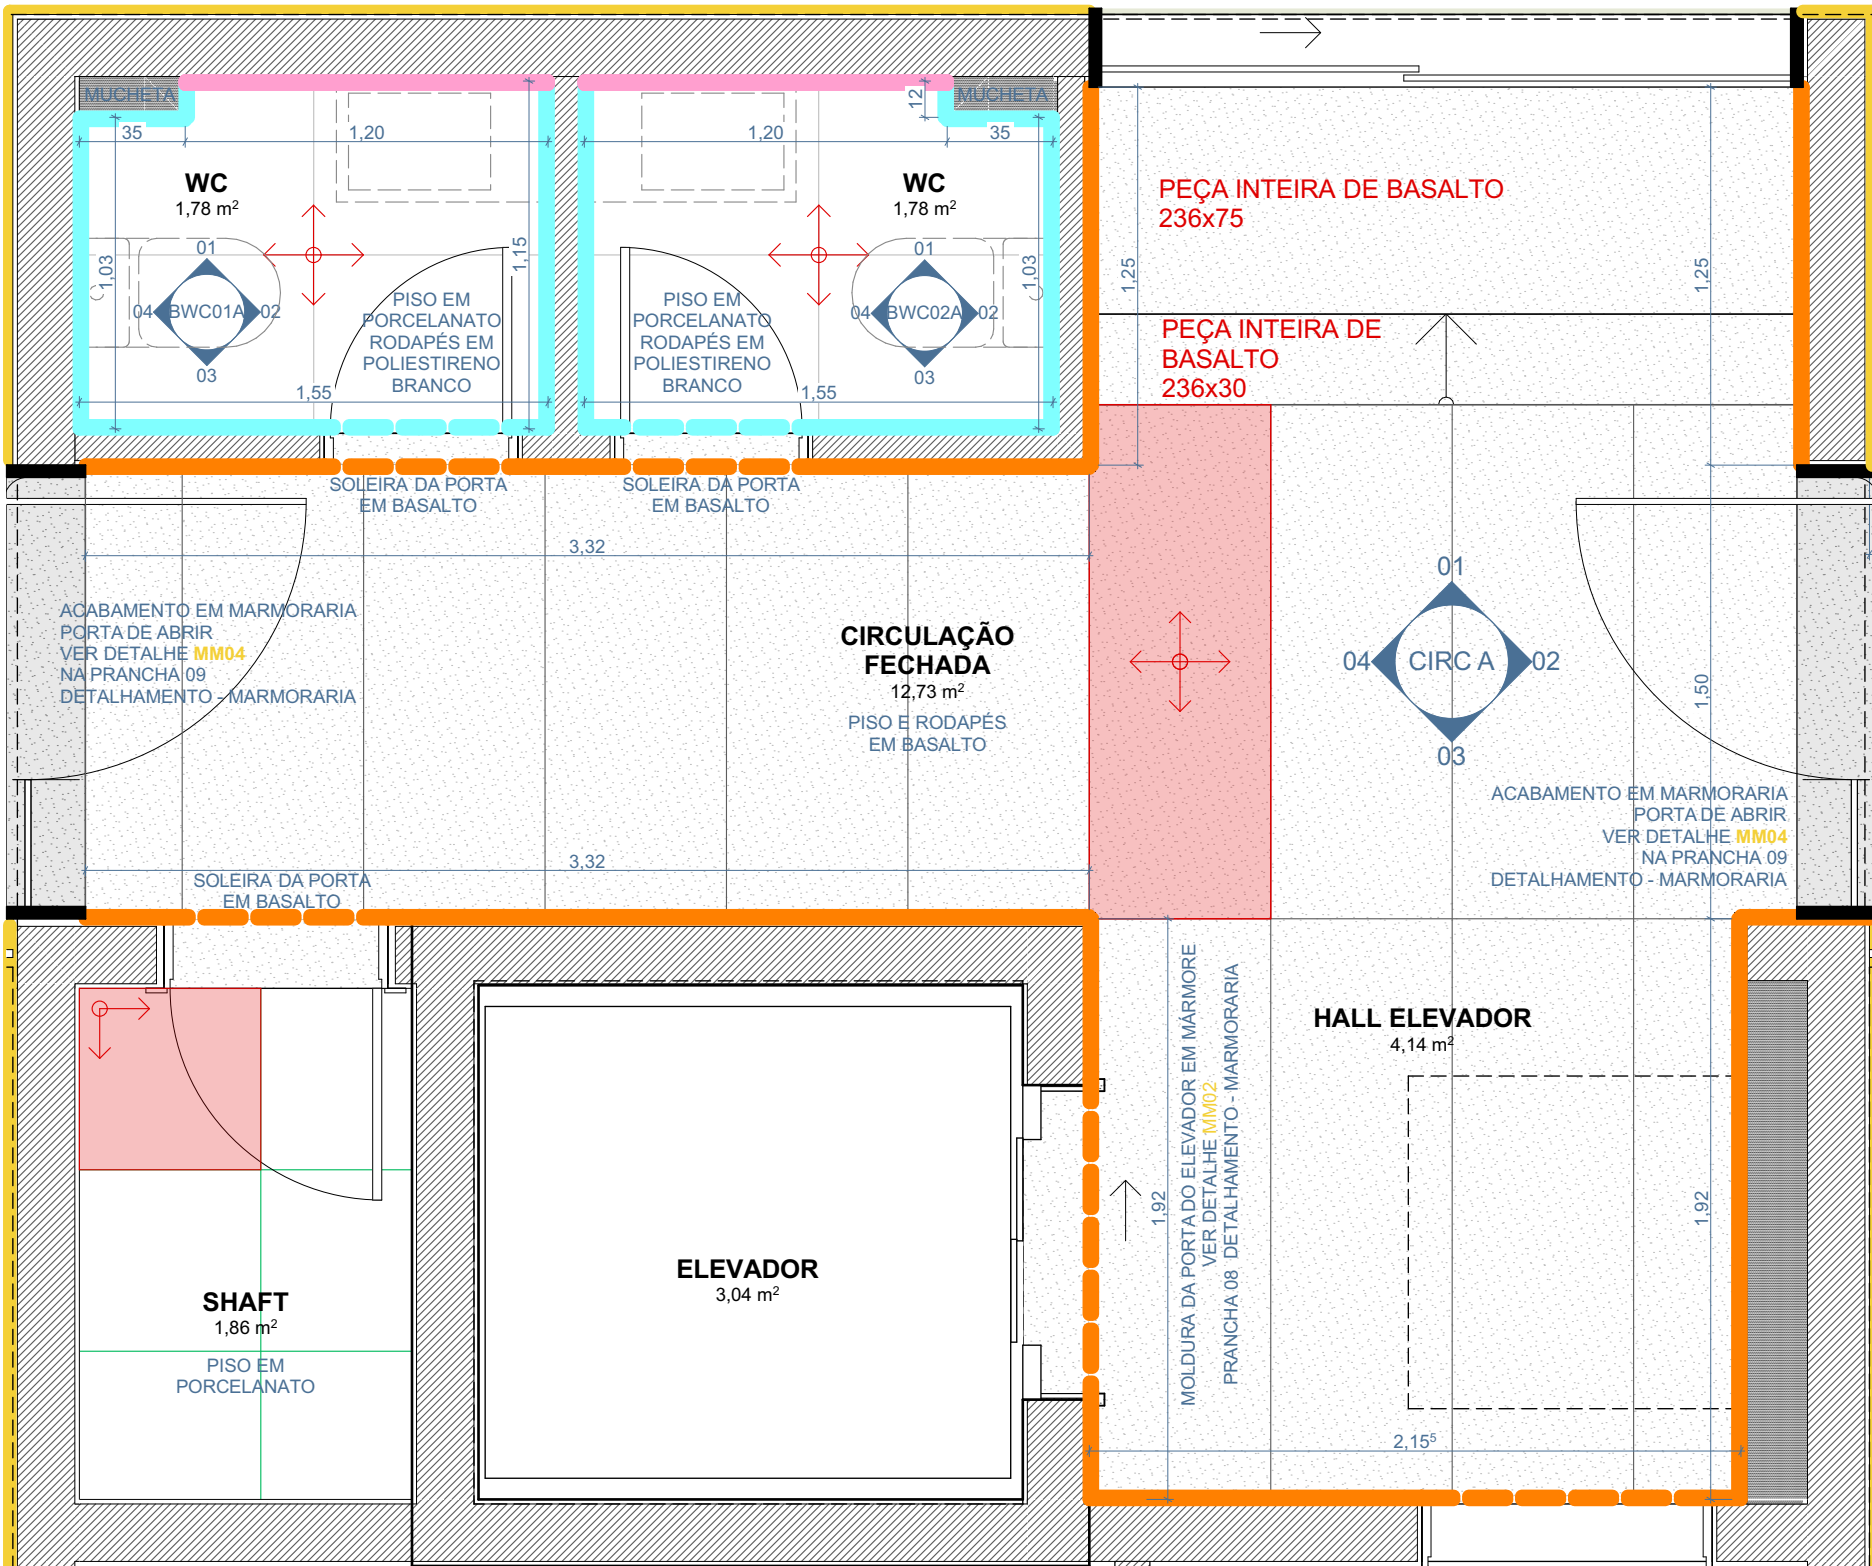


PLANTA BAIXA
ESCALA 1:25

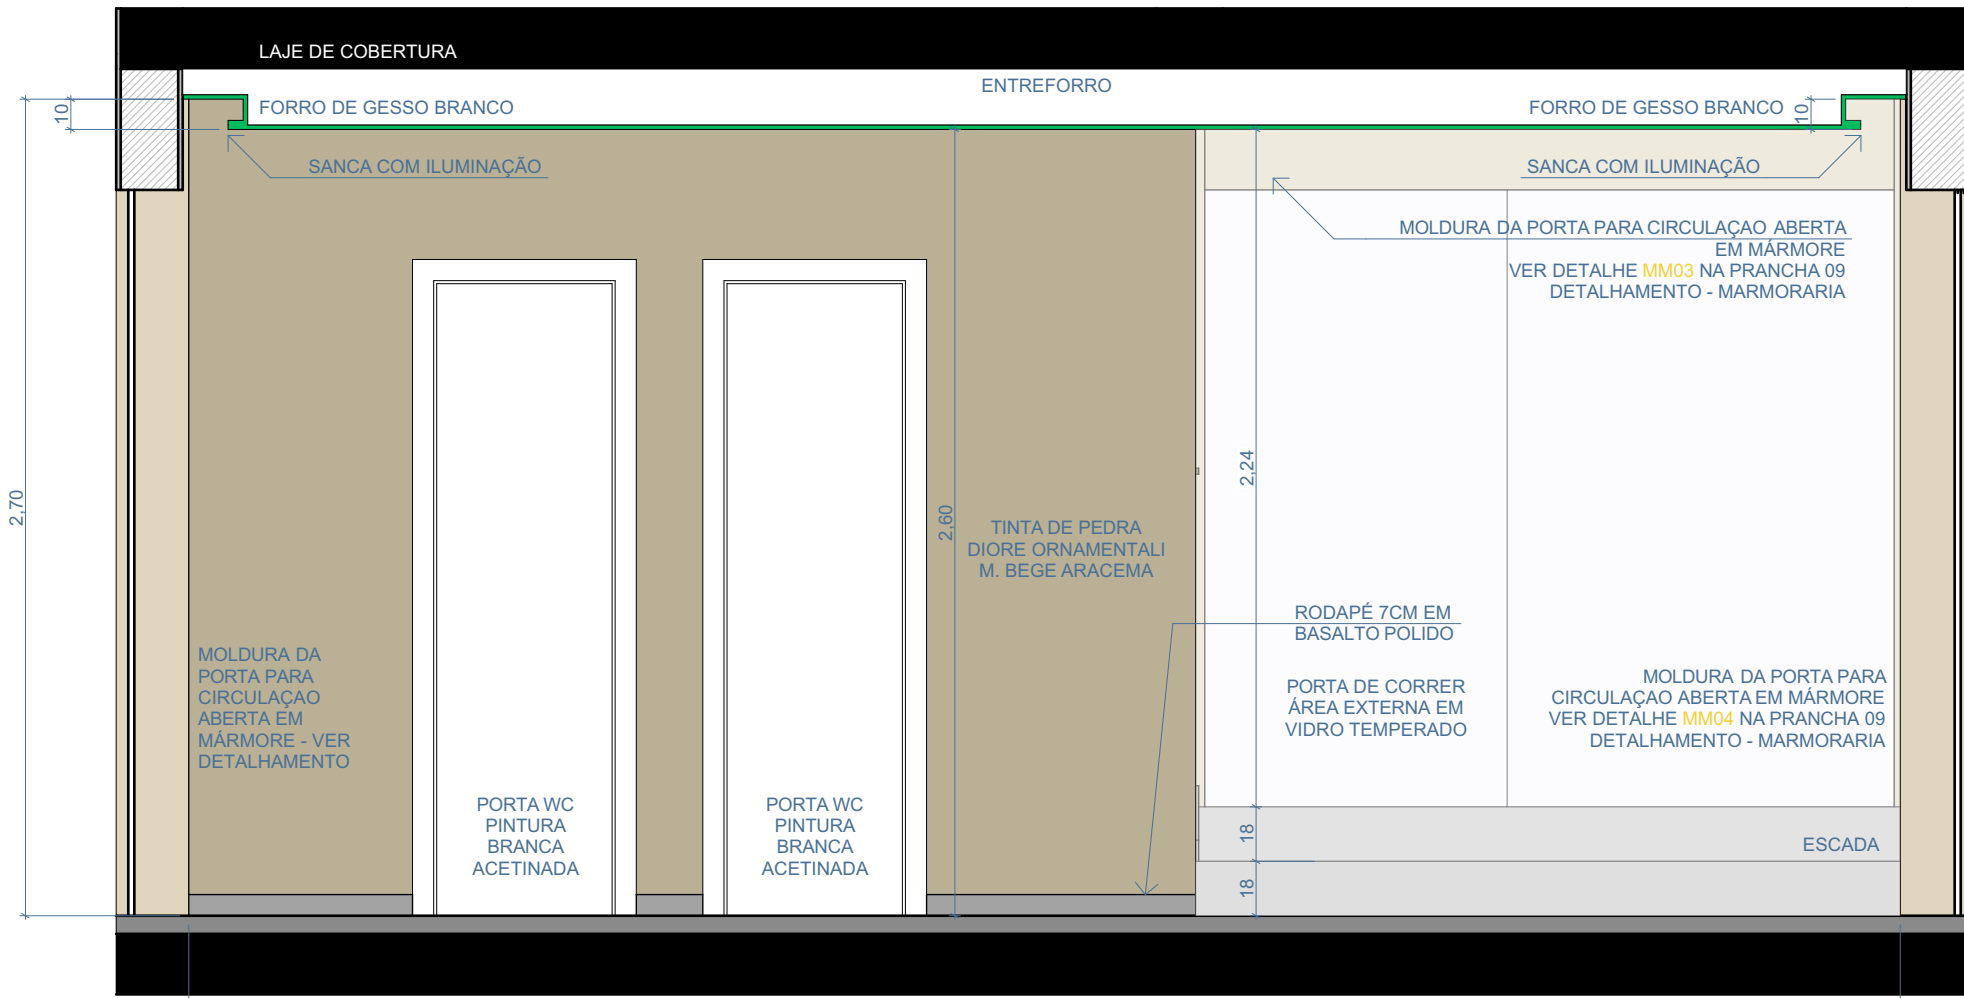


01
ESCALA 1:25

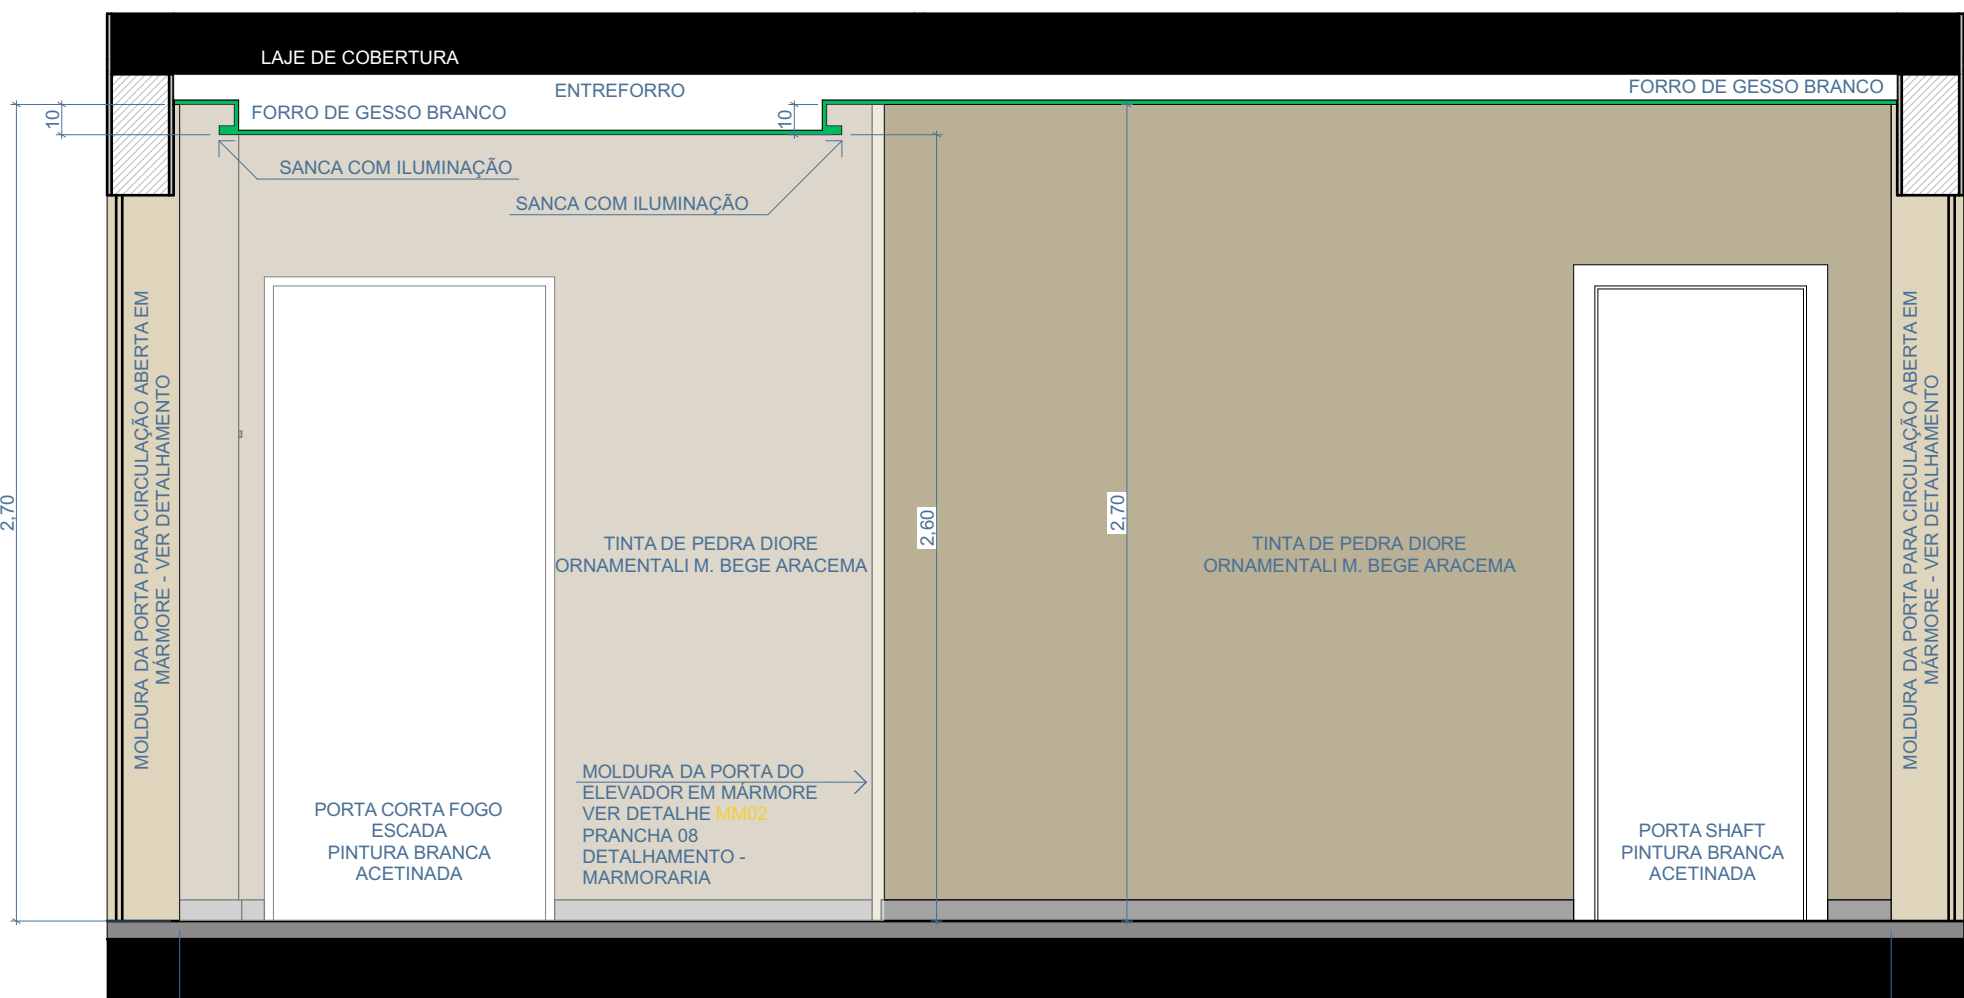

03
ESCALA 1:25

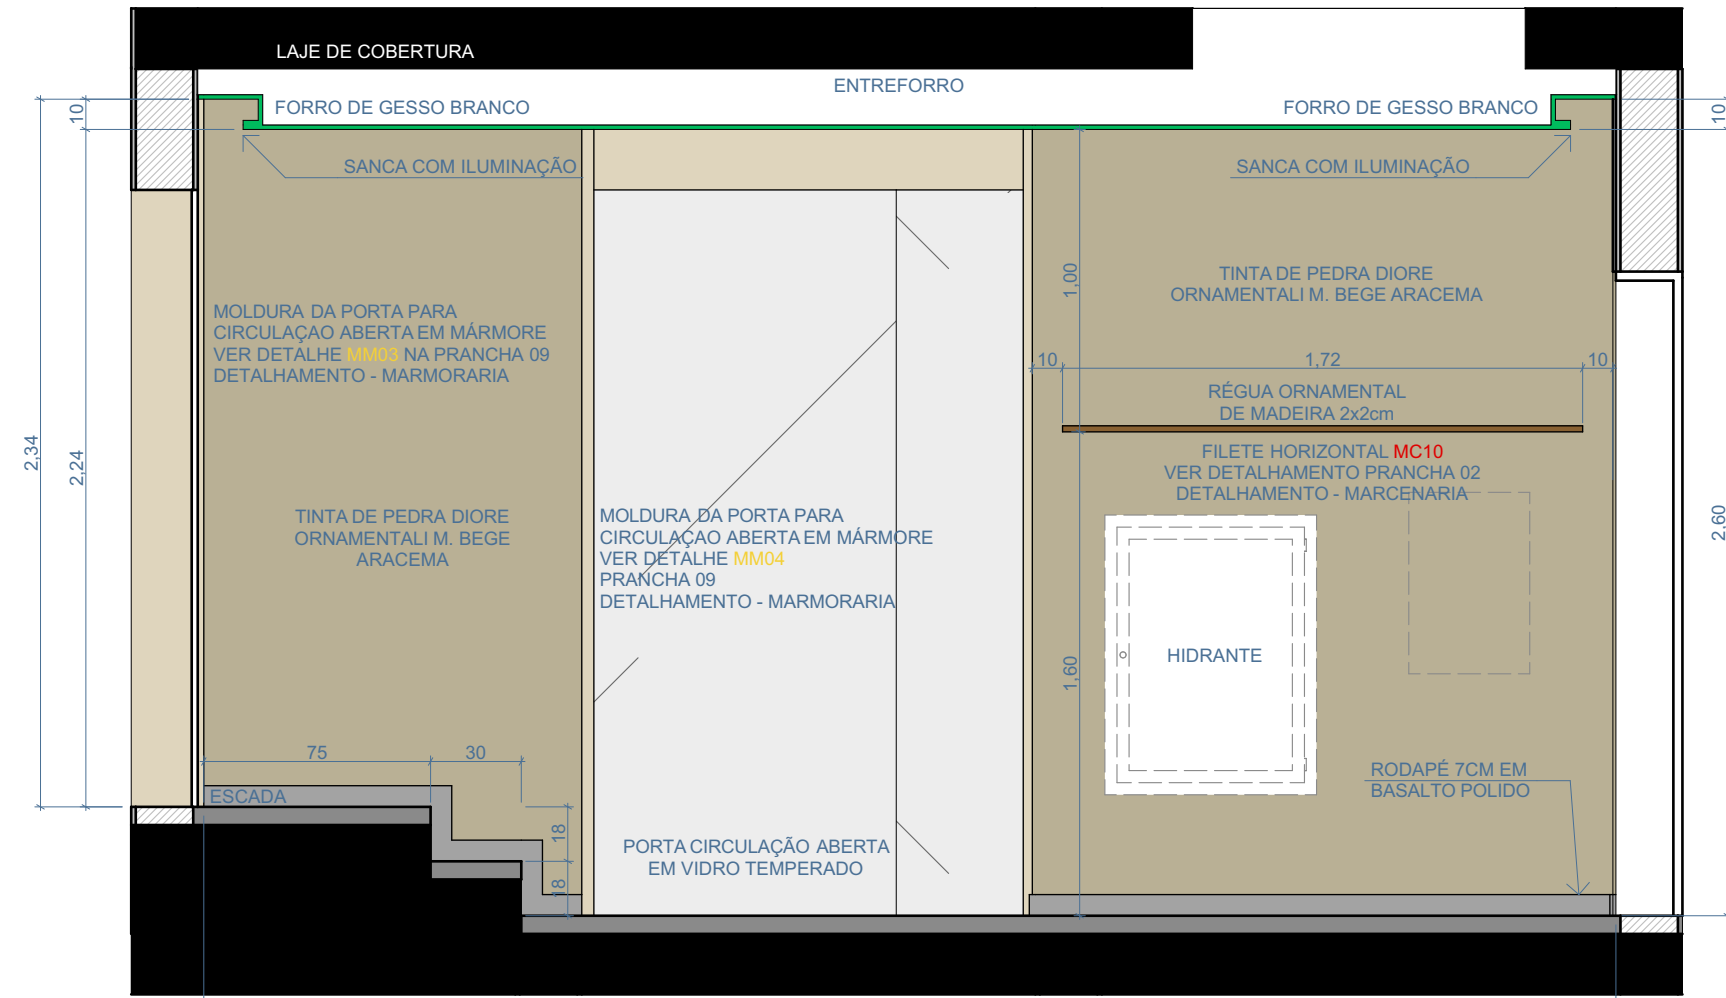

02
ESCALA 1:25

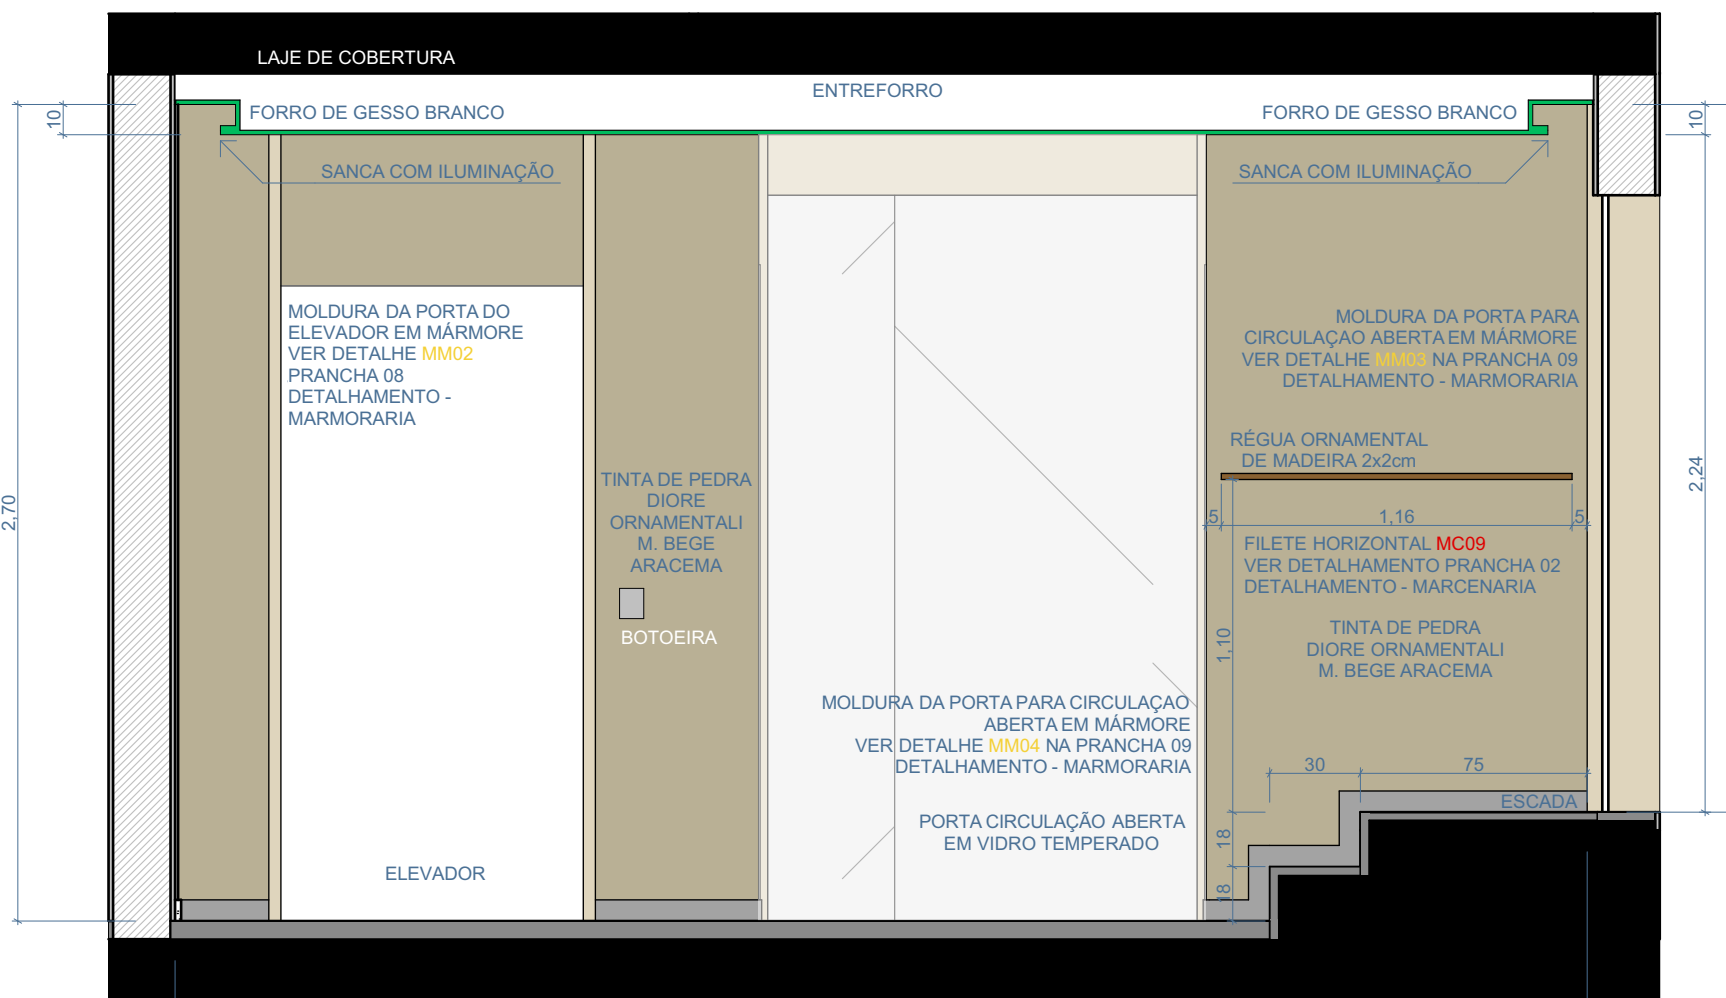


04
ESCALA 1:25

LEGENDA REVESTIMENTOS

	PLACA DE CONCRETO 50x50		AZULEJO 30x60 BRANCO ACETINADO RETIFICADO
	PETI PAVÉ BRANCO		TINTA DE PEDRA DIORE DELICATO PRECIOSA COR NATURAL
	PETI PAVÉ PRETO		TINTA DE PEDRA DIORE ORNAMENTAL MAXI COR BEGE ARACEMA
	CIMENTO ALISADO		TEXTURA TERRACOZ PREDIAL PRETO
	CONCRETO VASSOURADO		PINTURA ACRÍLICA PRETA - SUVINIL PATATIVA
	PORCELANATO 60x120		BASALTO POLIDO
	PORCELANATO 60x60		REVESTIMENTO EM PEDRA NATURAL MOLEDO
	PORCELANATO 90x90		REVESTIMENTO EM LÂMINA PRELO
	PISO DE MADEIRA		COMPENSADO VIROLA
	DECK DE MADEIRA		ESPELHO CRISTAL COLADO
	PISO ESPORTIVO EMBORRACHADO EM PLACAS 100x100		
	BASALTO RÚSTICO		
	BASALTO POLIDO		
	PISO CIMENTÍCIO SOLARIUM 50x50		

- NOTAS
1. PILARES DA GARAGEM E MURETAS DO ACESSO SÃO EM CONCRETO APARENTE;
 2. PAREDES INTERNAS SEM INDICAÇÃO DE REVESTIMENTO RECEBERÃO PINTURA ACRÍLICA COR BRANCO FOSCO;
 3. PAREDES EXTERNAS SEM INDICAÇÃO DE REVESTIMENTO RECEBERÃO PINTURA TERRACOZ PREDIAL BRANCO;
 4. SOLEIRAS DAS PORTAS DOS APARTAMENTOS EM PEÇA ÚNICA SEQUINDO ESPECIFICAÇÃO DO PISO DA CIRCULAÇÃO COMUM

ROOFTOP - WC 1 TORRE B

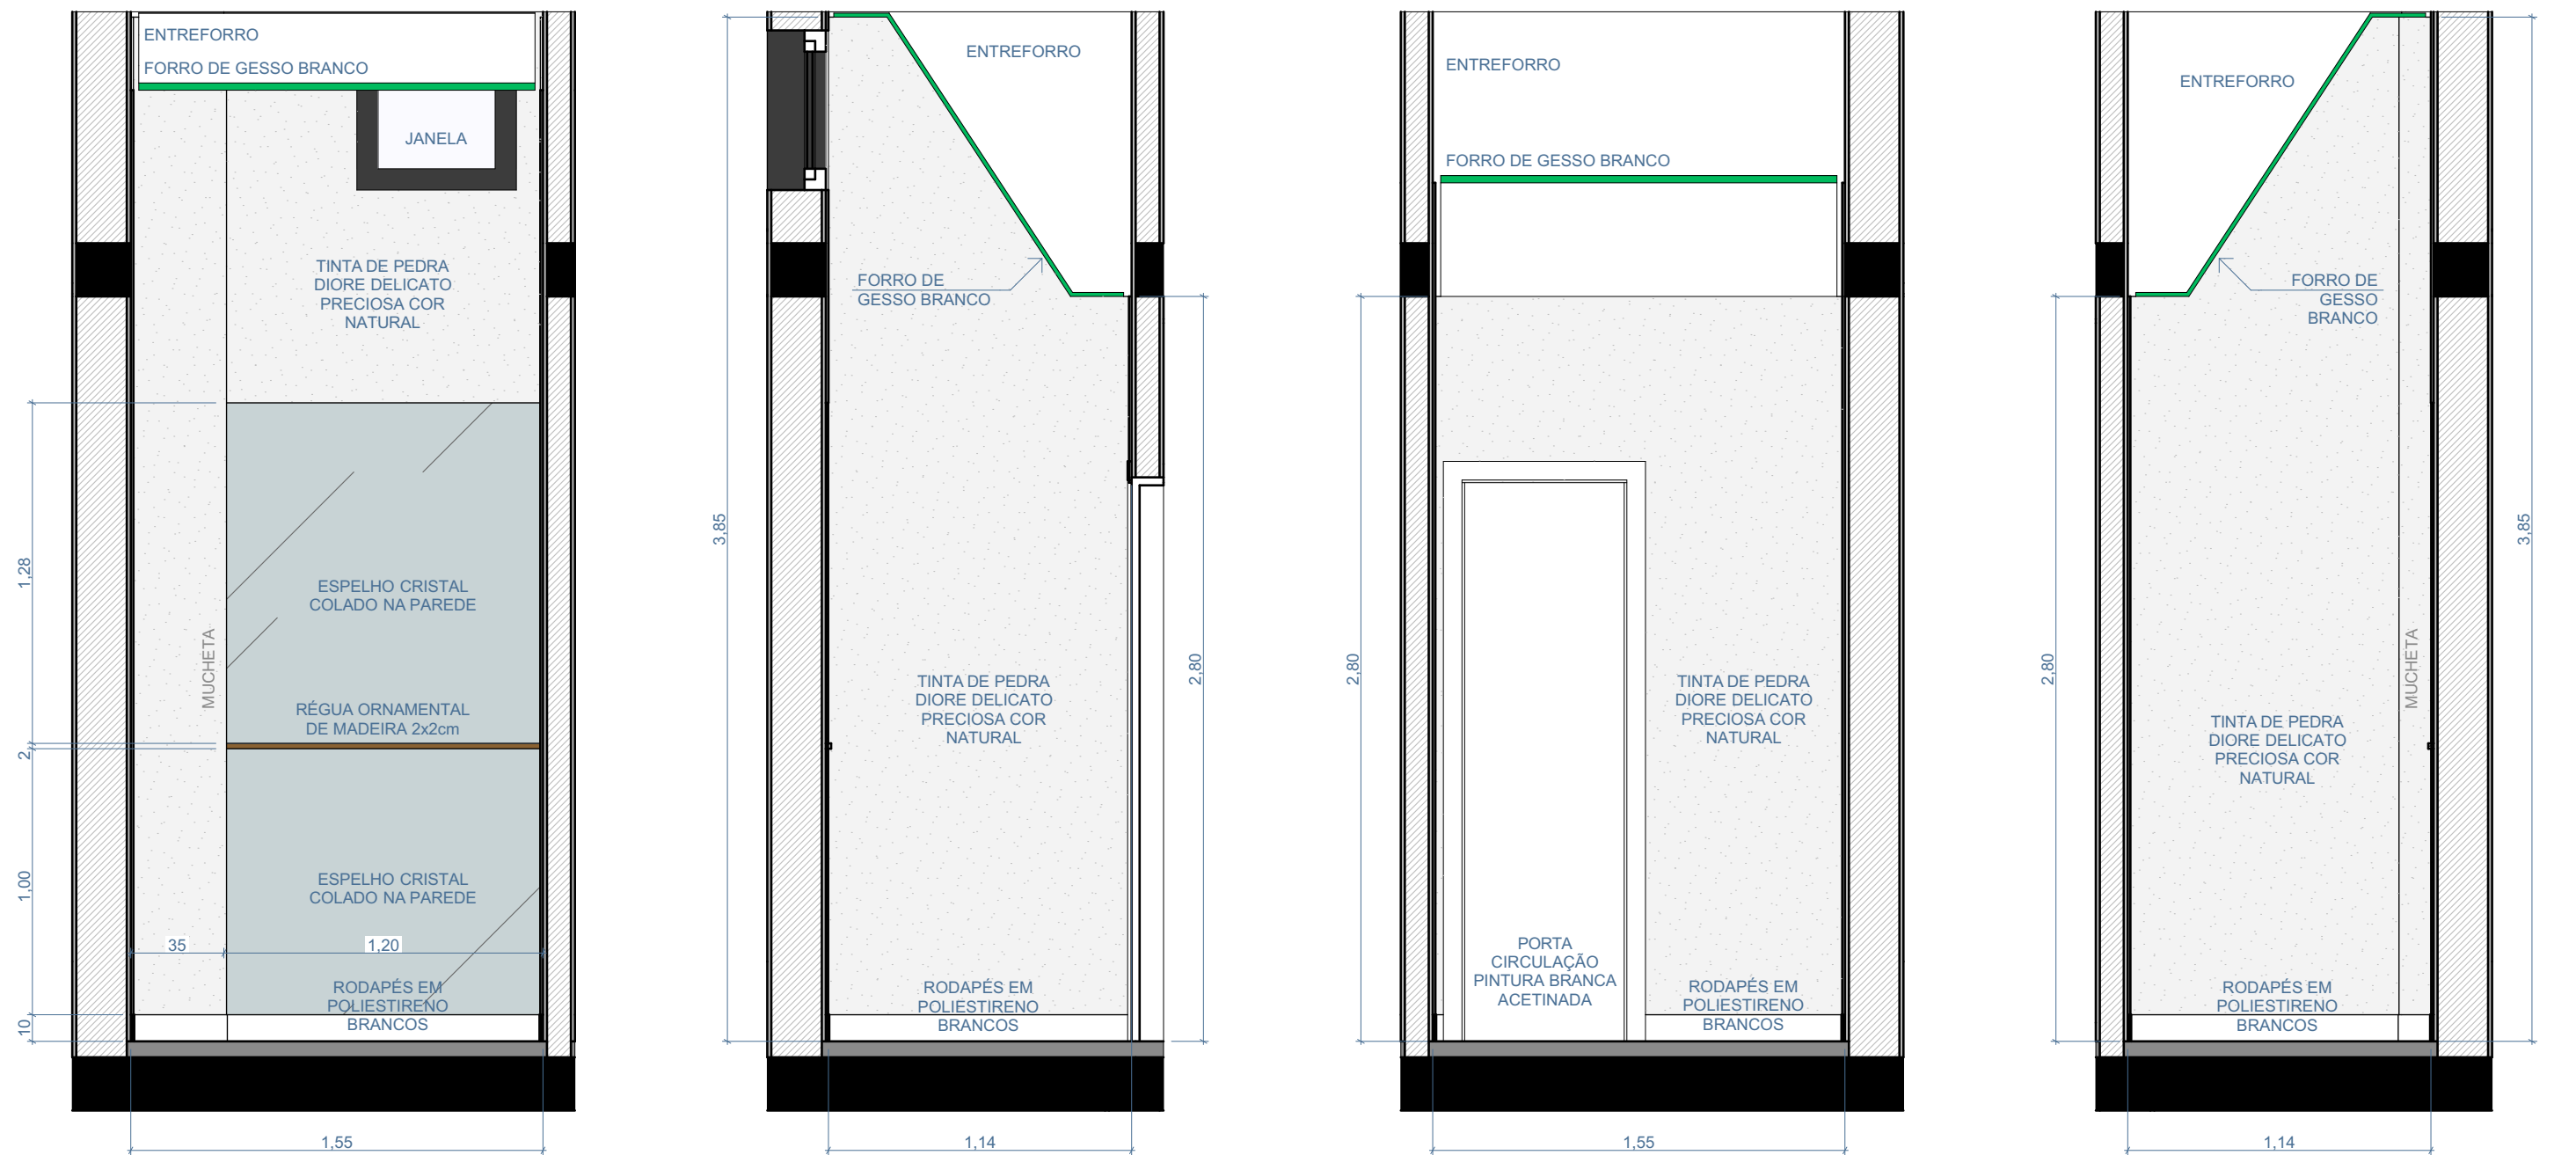


01
ESCALA 1:25

02
ESCALA 1:25

03
ESCALA 1:25

04
ESCALA 1:25

ROOFTOP - WC 2 TORRE B

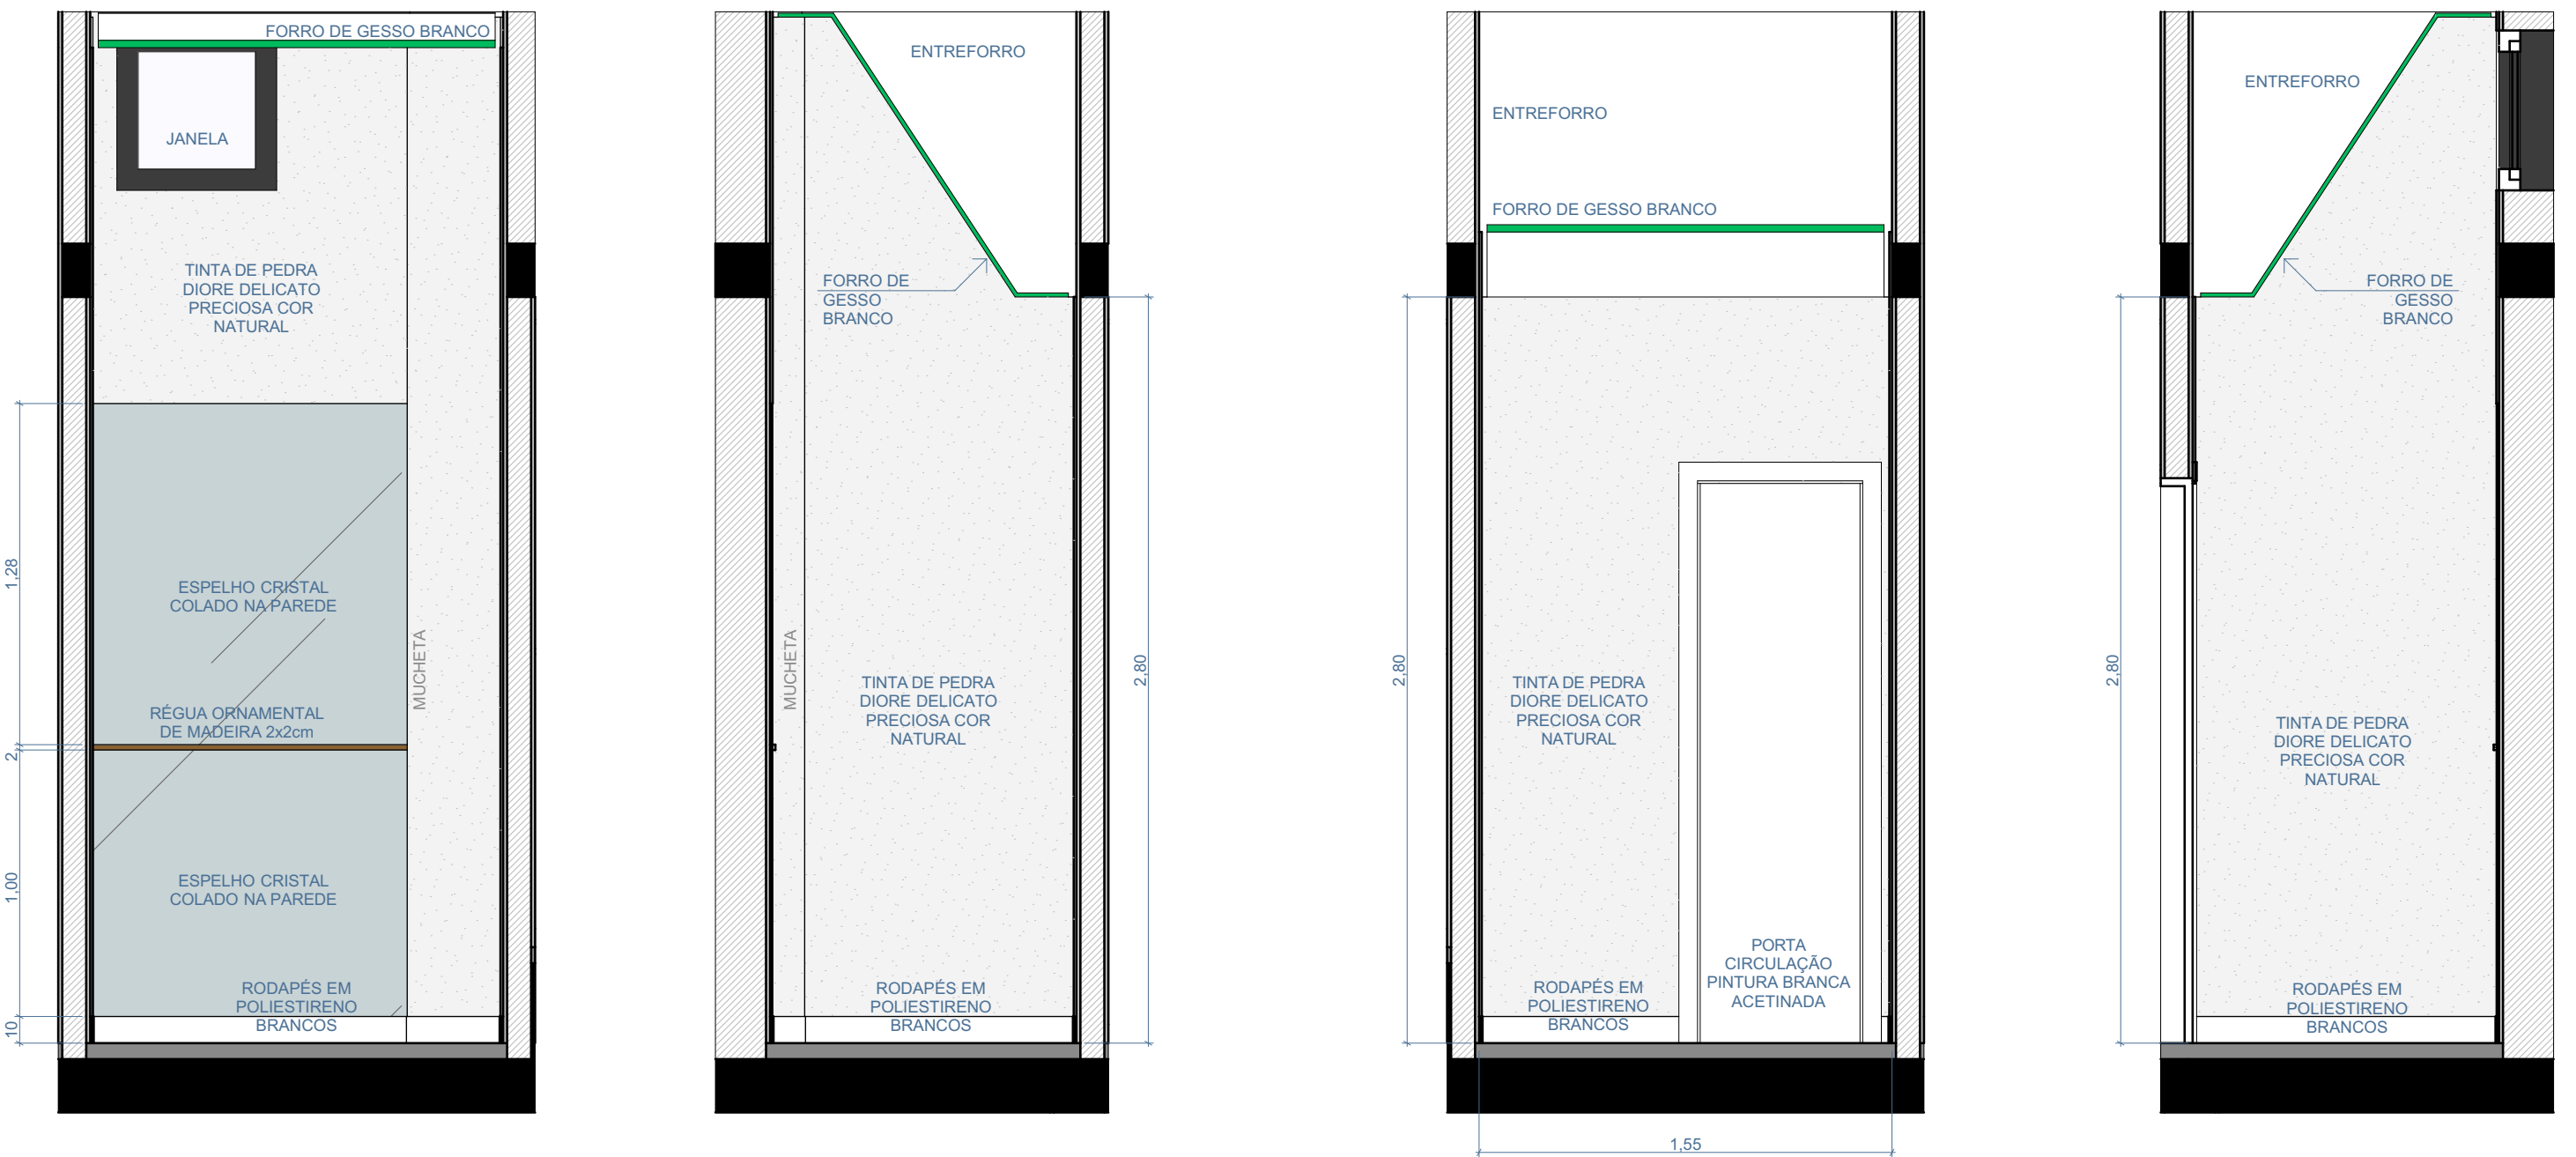

01
ESCALA 1:25

02
ESCALA 1:25

03
ESCALA 1:25

04
ESCALA 1:25

PROJETO ARQUITETÔNICO

MAUI
INTERIORES AMBIENTAÇÃO - RTOP HALL | WCS
TORRE A

ETAPA	OUZ_MAU_ARQ_PROJETO EXECUTIVO AMBIENTAÇÃO	A1 EST.
DATA	14/03/2025	
ESCALA	1:25, 1:50	
ENDEREÇO	Rodovia SC-406, s/n, Praia Mole, Florianópolis, Santa Catarina	
ASSINATURA:		
CLIENTE	OUZ	
CPF/CNPJ:		
ASSINATURA:		
RESPONSÁVEL:	HENRIQUE PIMONT	
CAU A 20832-9		
DESENHO:	MAYCON PASSIG; ARTHUR ANDRADE; MIRELA MOSER	

PIMONT
ARQUITETURA

RUA ALVES DE BRITO, 141 - SALA 701
CENTRO - FLORIANÓPOLIS - SC
CEP: 88015-440
TELEFONE: 48 30251 200
CELULAR: 48 99804485

WWW.PIMONTARQUITETURA.COM.BR
CONTATO@PIMONTARQUITETURA.COM.BR