



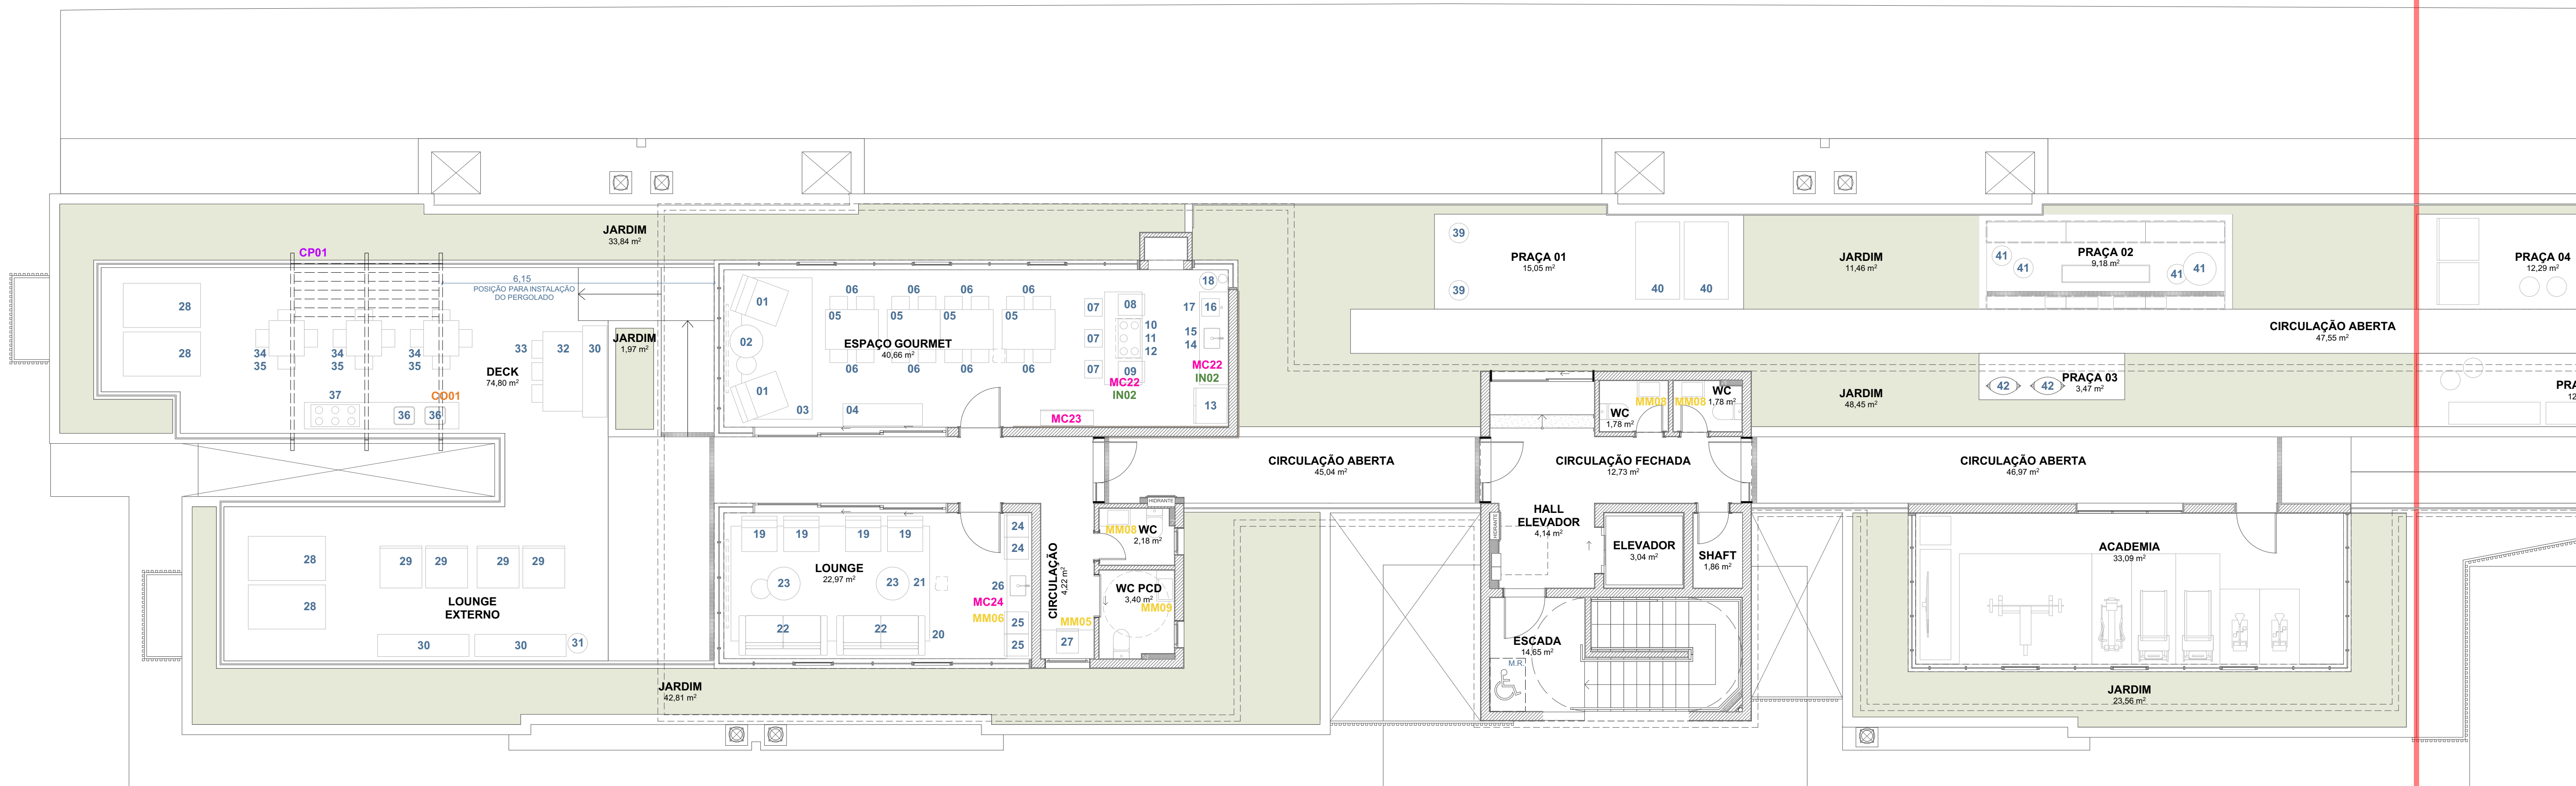

PLANTA BAIXA
ESCALA 1:75
TRECHO 1

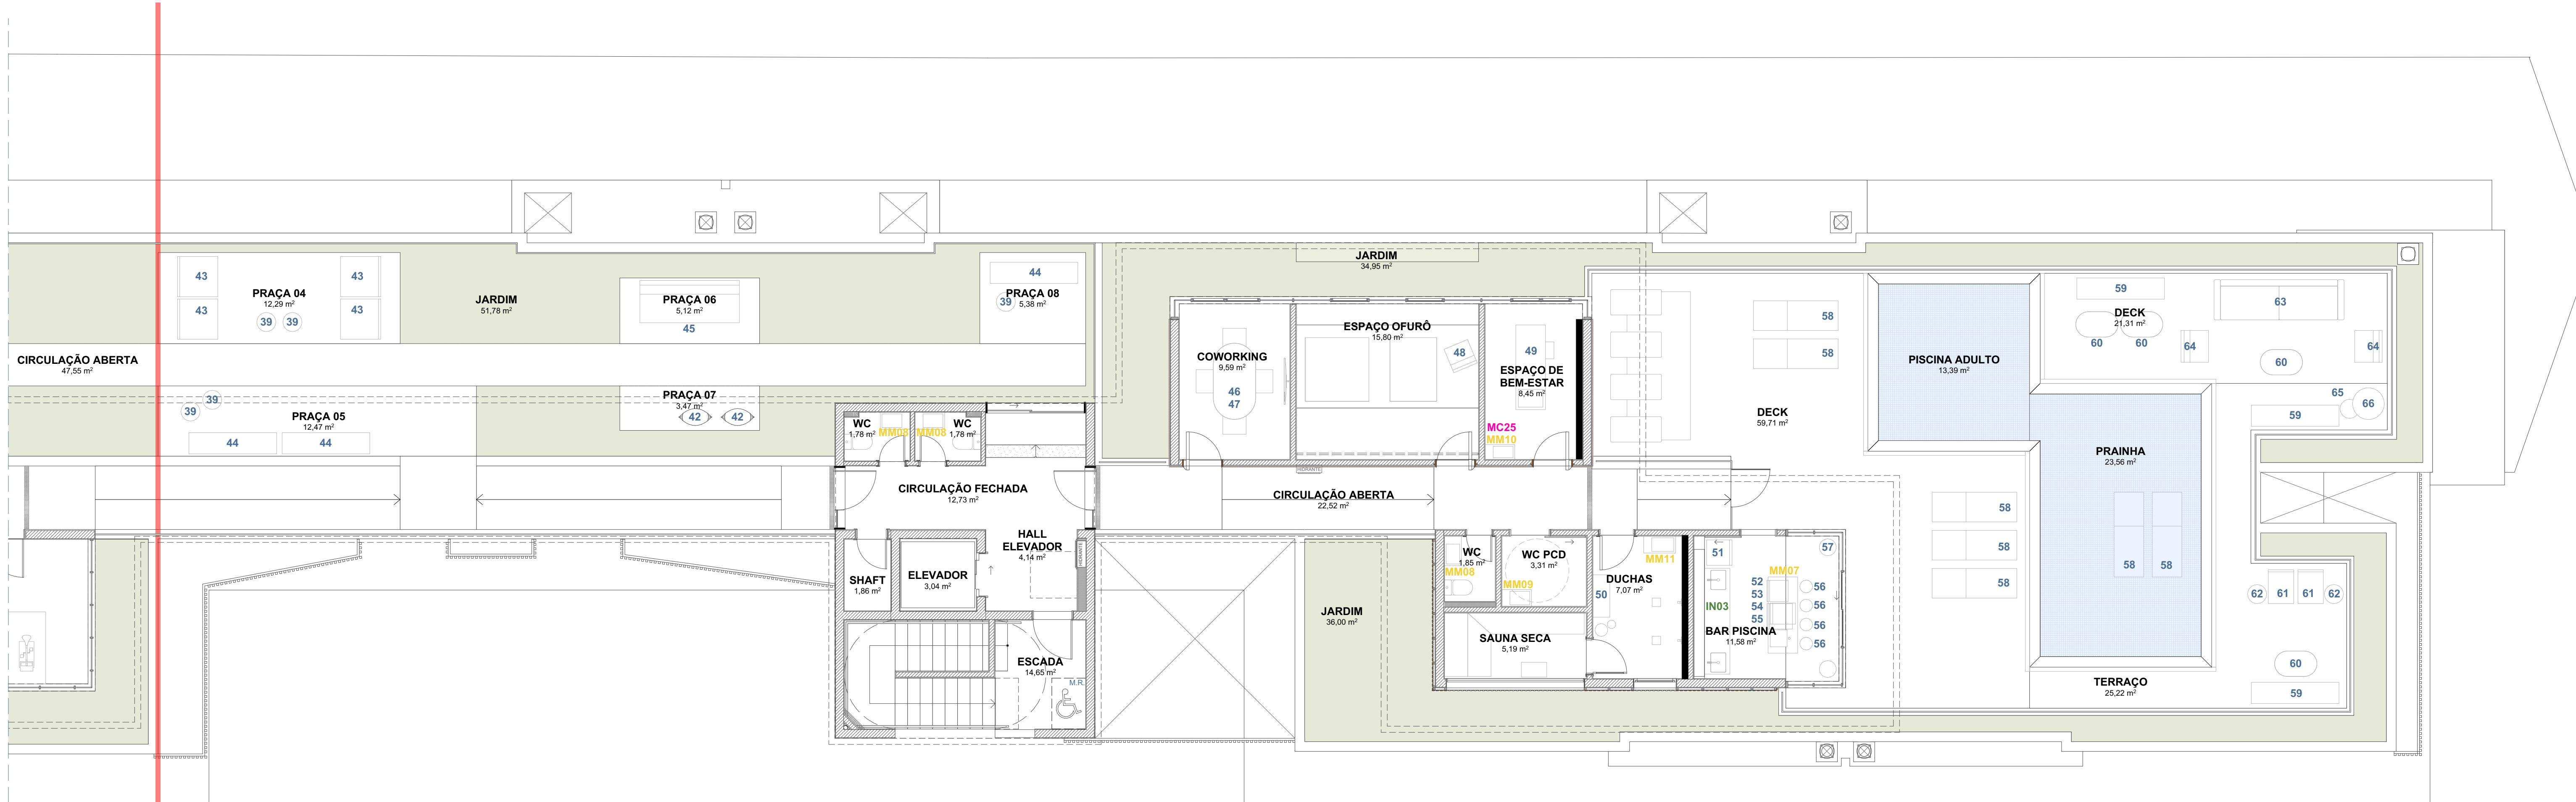

PLANTA BAIXA
ESCALA 1:75
TRECHO 2

LISTA MOBILIÁRIO SOLTO

AMBIENTE	CÓDIGO	ITEM	QUANT.	DIMENSÃO (LxPxA)
ESPAÇO GOURMET	01	POLTRONAS	2	0,70 x 0,80
	02	MESAS LATERAIS	3	0,45 x 0,45
	03	TAPETE	1	3,30 x 1,40
	04	BANCO	1	2,00 x 0,45
	05	MESAS	4	1,20 x 0,80
	06	CADEIRAS	16	0,43 x 0,57
	07	BANQUETAS	3	0,42 x 0,30
	08	CERVEJEIRA VENAX	1	0,50 x 0,61 x 0,80
	09	ADEGA VENAX	1	0,90 x 0,61 x 0,80
	10	COOKTOP	1	0,90 x 0,50
	11	FORNO ELÉTRICO	1	0,80 x 0,61 x 0,80
	12	COFAL ILHA	1	0,90 x 0,60
	13	REFRIGERADOR INVERTER (3 PORTAS)	1	0,80 x 0,75 x 1,80
	14	CUBA BOX INOX EMBUTIR FRANGE TORNEIRA	1	0,84 x 0,41 x 0,20
	15	NAJÁ E BANDEJA	1	0,40 x 0,40
	16	PRIE REFRIGERADOR	1	0,80 x 0,60 x 0,75
	17	BARRIL E CILINDRO CO2	1	-
LOUNGE	19	POLTRONAS	4	0,70 x 0,80
	20	MESAS LATERAIS	4	0,45 x 0,45
	21	TAPETE	1	4,70 x 2,50
	22	SOFÁS	2	2,00 x 0,98
	23	MESAS DE CENTRO	3	0,75 x 0,50
	24	CERVEJEIRA VENAX	1	0,50 x 0,61 x 0,80
	25	ADEGA VENAX	1	0,90 x 0,61 x 0,80
	26	CUBA SUPRAHIDE MONOCOMANDO	1	0,53 x 0,45 x 0,20
CIRCULAÇÃO	27	MÁQUINA DE GELO	1	0,50 x 0,50 x 0,75
LOUNGE EXTERNO	28	RECAMIER	4	1,80 x 1,00
	29	POLTRONAS	4	0,95 x 0,95
	30	BANCO DE MADEIRA COM ENCONSTO	3	2,07 x 0,51
	31	PUFES	1	0,45
	32	MESA RETANGULAR	1	1,80 x 0,90
	33	CADEIRAS EXTERNAS	3	0,50 x 0,50
	34	MESA QUADRADA	3	0,80 x 0,80
	35	CADEIRAS EXTERNAS	12	0,50 x 0,50
	36	CUBA DE INOX	2	0,40 x 0,35
	37	PARRILLA	1	1,10 x 0,50
	38	-	-	-
PRAÇAS	39	PUFES	7	0,45
	40	RECAMIER	2	1,80 x 1,00
	41	PUFES/MESA FOGO DE CHÃO	4	0,45
	42	BALANÇO	4	0,80 x 0,80
	43	POLTRONAS	4	0,95 x 0,95
COWORK	45	BANCO DE MADEIRA COM ENCONSTO	3	2,07 x 0,51
	46	SOFA	1	2,35 x 0,85
ESPAÇO OFURÔ	47	MESA	1	1,90 x 1,00
	48	CADEIRAS	4	0,68 x 0,68
BEM ESTAR	49	MACA MASSAGEM	1	0,70 x 2,10
DUCHAS	50	BANCO	1	1,00 x 0,40
BAR DA PISCINA	51	CERVEJEIRA	2	0,60 x 0,60 x 1,40
	52	MÁQUINA DE GELO	1	0,50 x 0,50 x 0,75
	53	PRIE REFRIGERADOR	1	0,80 x 0,60
	54	BARRIL E CILINDRO CO2	1	-
	55	NAJÁ E BANDEJA	1	0,40 x 0,40
	56	BANQUETA	4	0,62 x 0,36
	57	BANCOS	2	0,61 x 0,48
	58	-	-	-
PISCINA	59	ESPREGUÇADEIRAS	7	2,00 x 0,75
	60	BANCO DE MADEIRA COM ENCONSTO	3	2,07 x 0,51
	61	MESA AUXILIAR	4	1,00 x 0,90
	62	POLTRONAS	2	0,60 x 0,80
	63	PUFES	2	0,45
	64	SOFA	1	2,35 x 0,95
	65	POLTRONAS	2	0,75 x 0,65
	66	MESA LATERAL	1	0,45
	67	MESA LATERAL	1	0,60
	68	-	-	-

LISTA MOBILIÁRIO SOB MEDIDA

AMBIENTE	CÓDIGO	ITEM	QUANT.	DIMENSÃO (LxPxA)
MC MARCENARIA	MC22	BANCADAS DO ESPAÇO GOURMET	1	2,10 x 0,66 x 0,86
	MC23	BANCADA ILHA	1	2,10 x 0,85 x 0,86
	MC24	ARMÁRIO LOUÇEIRO	1	1,24 x 0,36 x 2,10
	MC25	ARMÁRIO / ESTANTE DO LOUNGE	1	3,05 x 0,60 x 2,80
MM MARMORARIA	MM05	NICHO MÁQUINA DE GELO	1	1,20 x 0,60 x 0,94
	MM06	TAPO E FUNDO NO LOUNGE	1	3,01 x 0,59 x 0,88
	MM07	ILHA DO BAR DA PISCINA	1	1,80 x 0,70 x 0,90
	MM08	CUBA ESCULPIDA BWC (CIRCULAÇÕES)	6	0,70 x 0,40 x 0,85
	MM09	CUBA ESCULPIDA BWC-PD	2	0,70 x 0,40 x 0,20
	MM10	CUBA ESCULPIDA BEM ESTAR	1	0,70 x 0,35 x 0,37
	MM11	CUBA ESCULPIDA DUCHAS	1	0,80 x 0,40 x 0,75
	MM12	-	-	-
IN INOX	IN02	BANCADAS DO ESPAÇO GOURMET	1	2,10 x 0,66 x 0,80
	IN03	BANCADA ILHA	1	2,10 x 0,85 x 0,80
	IN04	BANCADA DO BAR DA PISCINA	1	3,20 x 0,70 x 1,10
CP CARPINTARIA	CP01	PERGOLADO TERRAÇO LOUNGE EXT.	1	4,39 x 3,44 x 2,70
CO CONCRETO	CO01	BANCADA GOURMET DO TERRAÇO	1	3,50 x 0,60 x 1,32

PROJETO ARQUITETÔNICO MAUI INTERIORES - LOCALIZAÇÃO MOBILIÁRIO SOLTO E MOBILIÁRIO SOB MEDIDA

ETAPA	OUZ, MAUI, ARQ, PROJETO EXECUTIVO LOCALIZAÇÃO MOBILIÁRIO	A0
DATA	13/03/2025	
ESCALA	1:75, 1:1	
ENDEREÇO	Rodovia SC-406, s/n, Praia Mole, Florianópolis, Santa Catarina	
ASSINATURA:		
CLIENTE	OUZ	
RESPONSÁVEL:	HENRIQUE PIMONT	
DESENHO:	CAU A 20832-9	
	MAYCON PASSIG; ARTHUR ANDRADE; MIRELA MOSER	

IMAGENS MOBILIÁRIO SOLTO



POLTRONA MAPA
ESTUDIO ORTH



POLTRONA KATINSKY
BOOBAM



BANCO NENA
BOOBAM



CADEIRA SAGAIÁ
ESTUDIO CRUZETA



BANCO M2
BOOBAM



SOFA CRIO
STUDIO AMBIENTES



MESA BALEIA
BOOBAM



POLTRONA TAHITI
BOOBAM



SOFÁ TAHITI
BOOBAM



BANQUETA SOHO
DESMOBILIA



BANCO BASSO
JADER ALMEIDA



ESPREGUADEIRA RISE
STUDIO AMBIENTES



CADEIRA KITA
DESMOBILIA



MESA SAARINEN



BANCO HARRIS
METALCO