


MC20 | PORTA MIMETIZADA COWORKING


RIPADO DE MADEIRA MACIÇA SOBRE RIPAMENTO COM ESPAÇAMENTO DE APROXIMADAMENTE 40cm ENTRE PEÇAS
01 UNIDADE

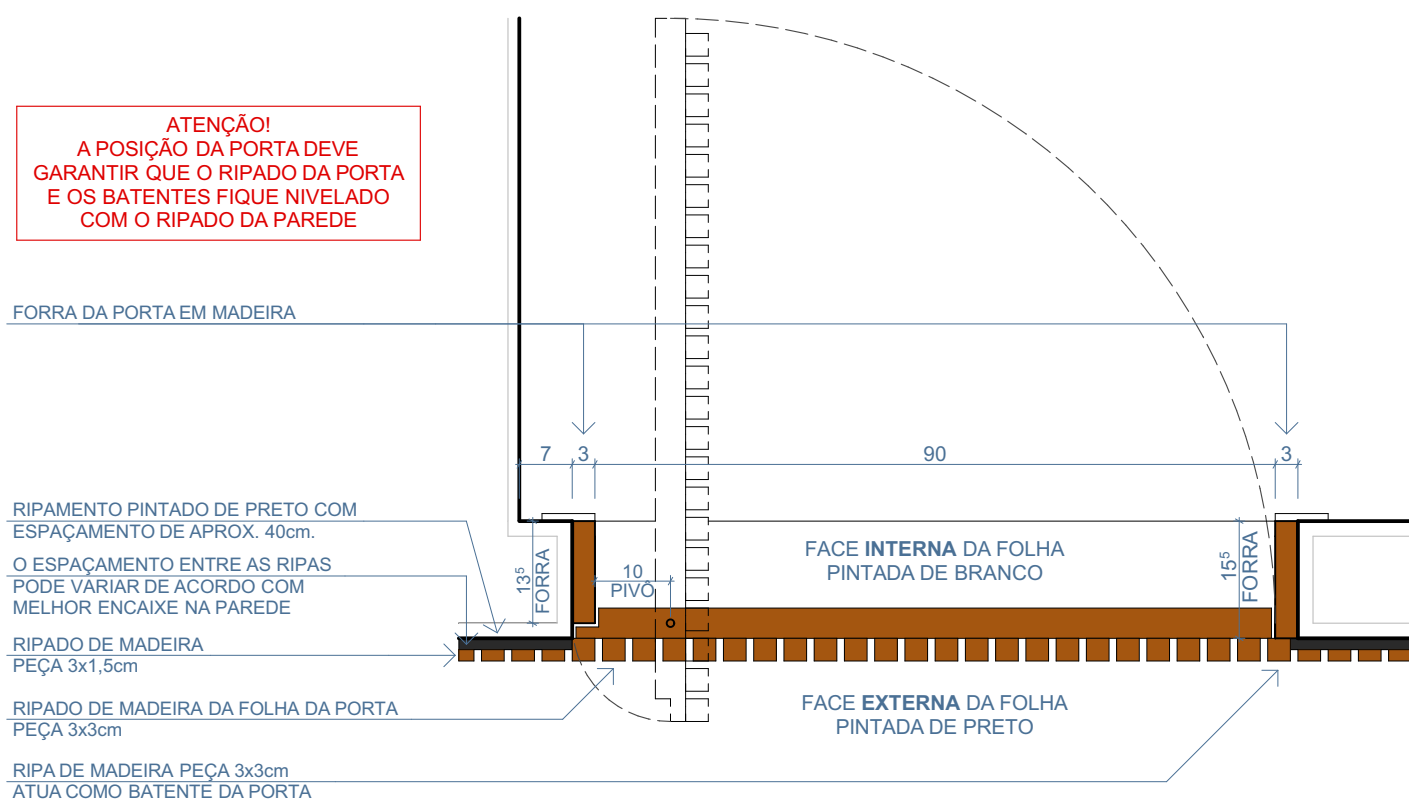


PLANTA BAIXA

MC21 | PORTA MIMETIZADA OFURÔ E BEM-ESTAR


RIPADO DE MADEIRA MACIÇA SOBRE RIPAMENTO COM ESPAÇAMENTO DE APROXIMADAMENTE 40cm ENTRE PEÇAS
01 UNIDADE

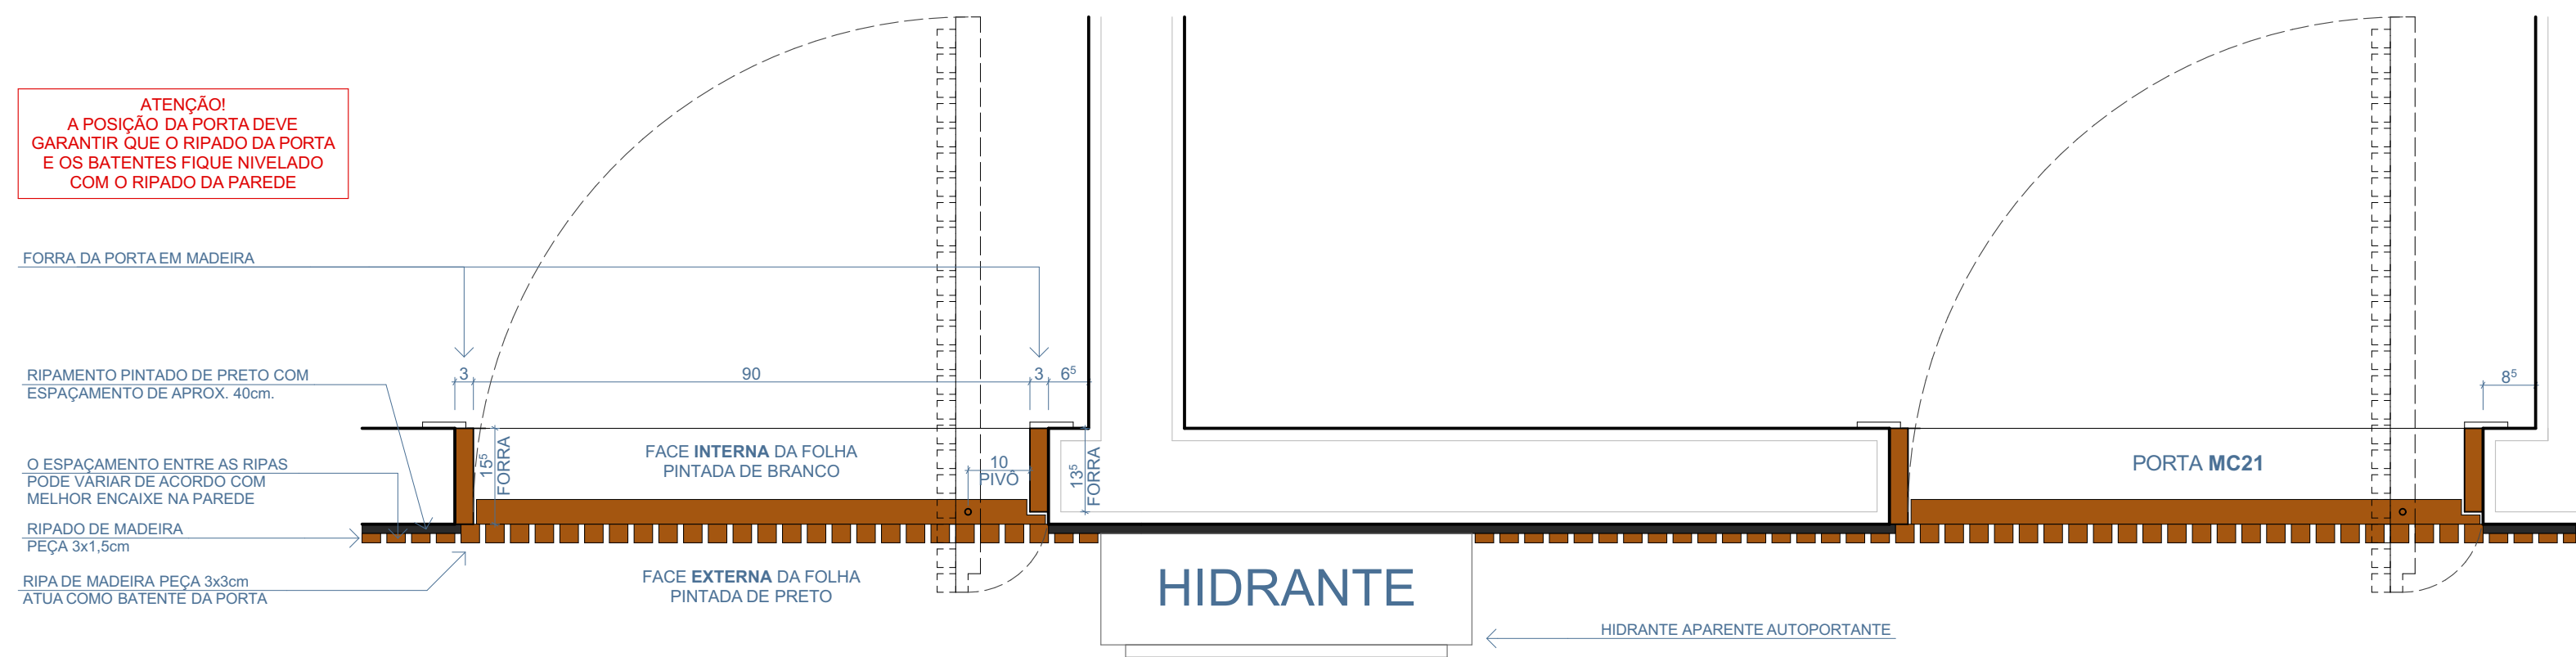


PLANTA BAIXA

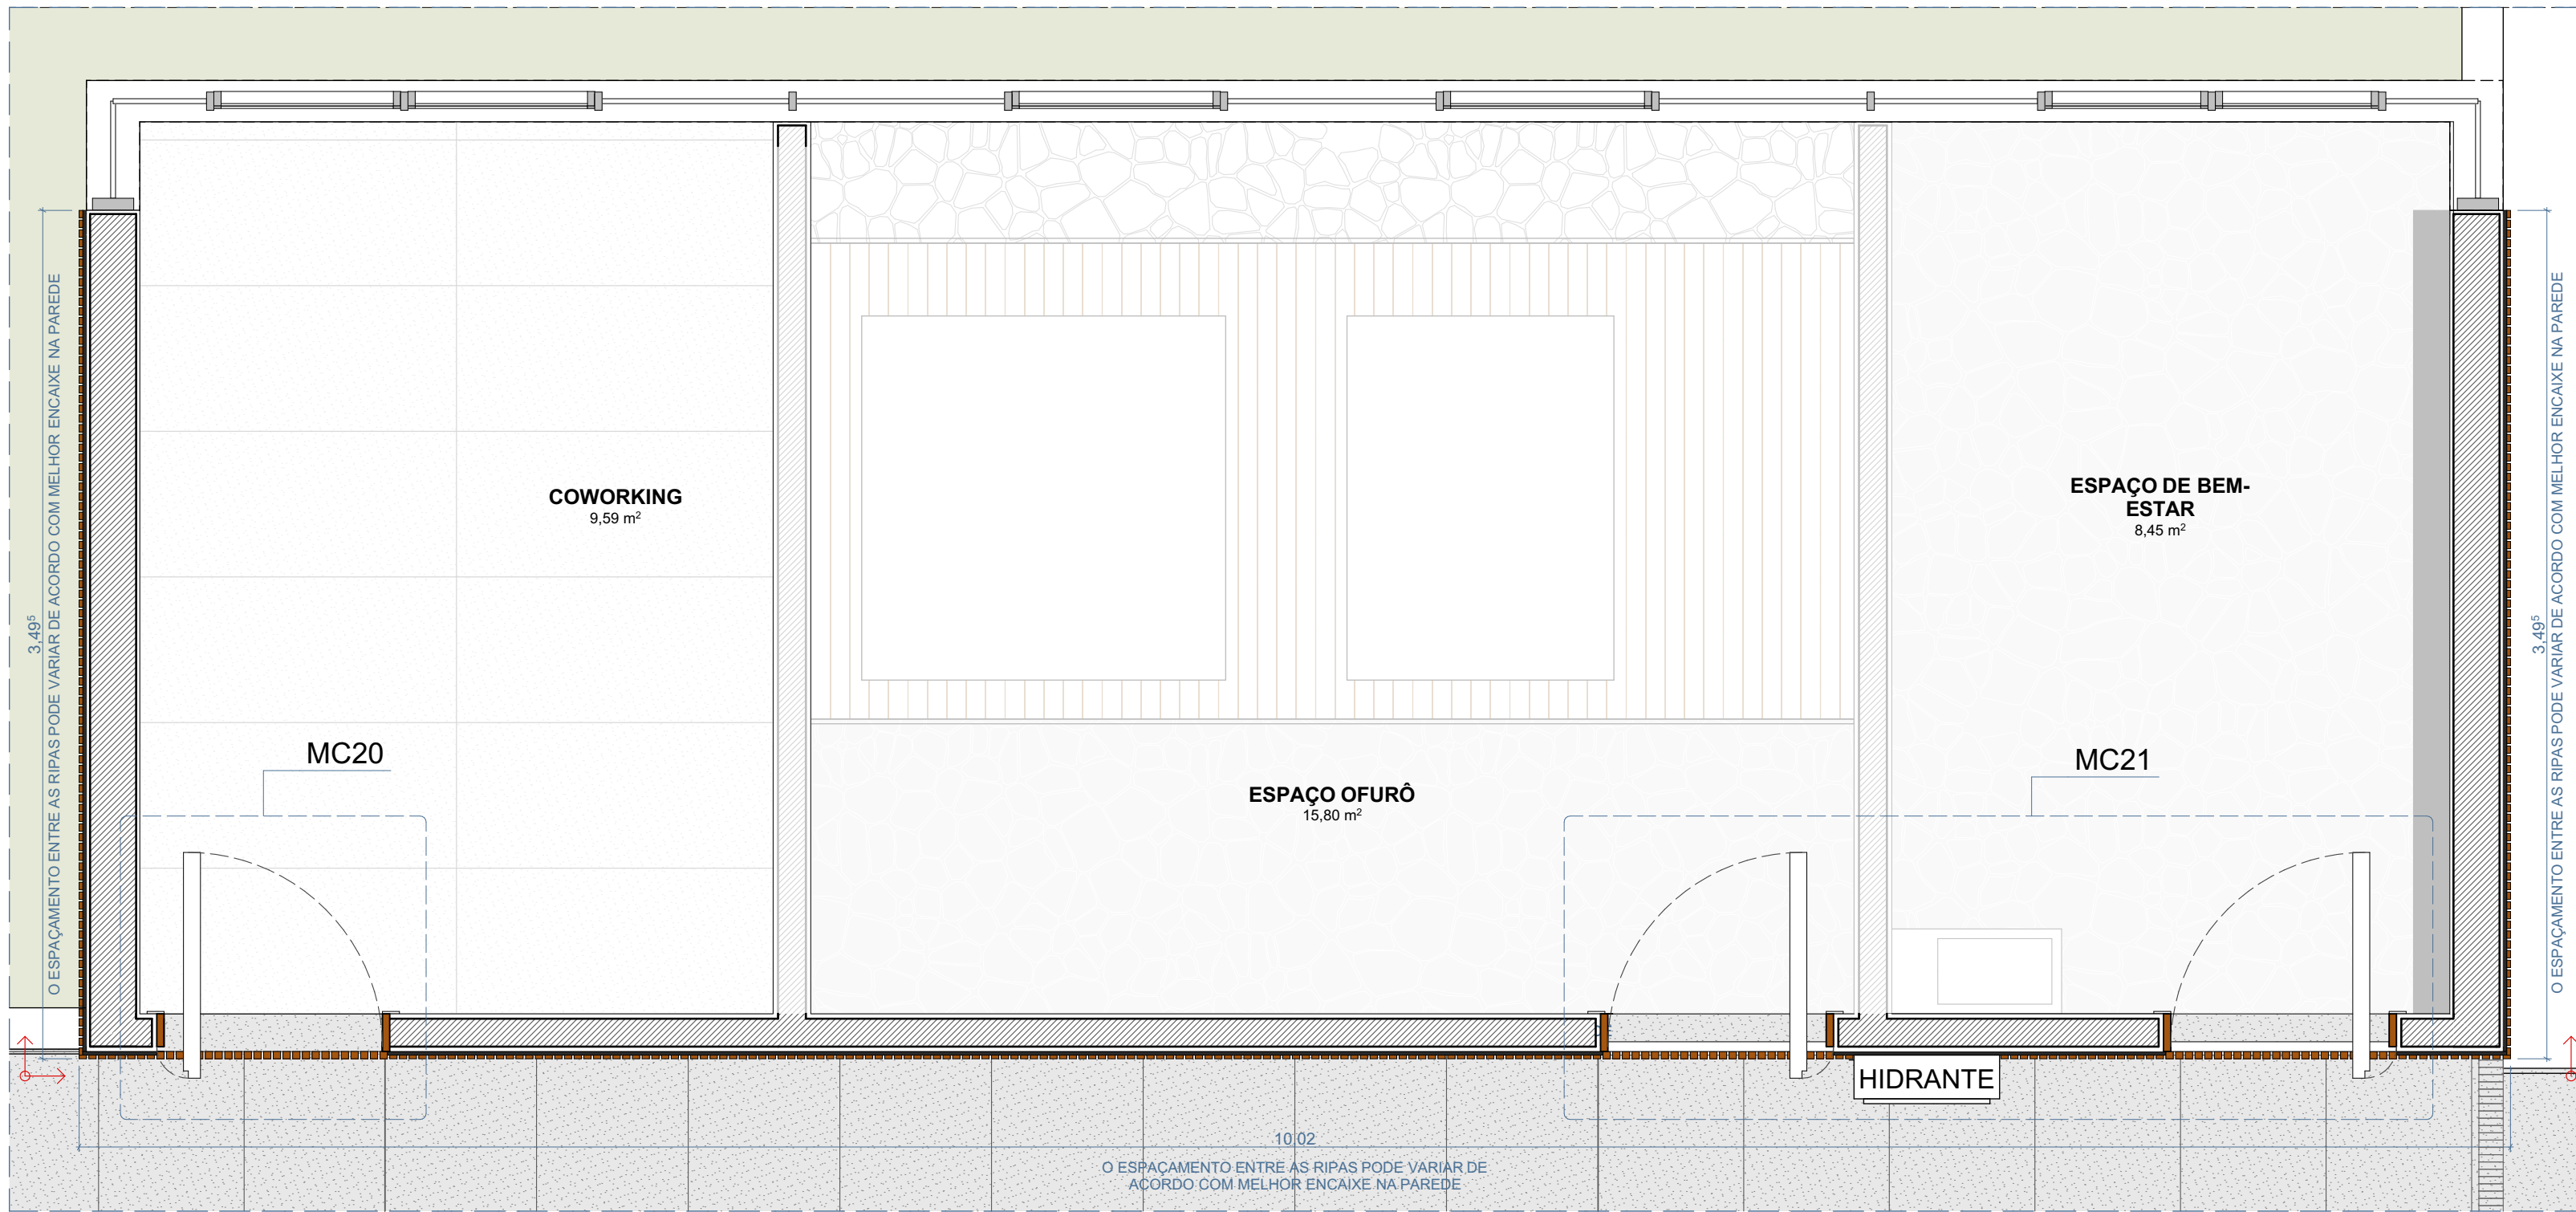


PLANTA BAIXA CIRCULAÇÃO ROOFTOP - PAGINAÇÃO DO RIPADO E INDICAÇÃO DE DETALHES
ESCALA 1:25

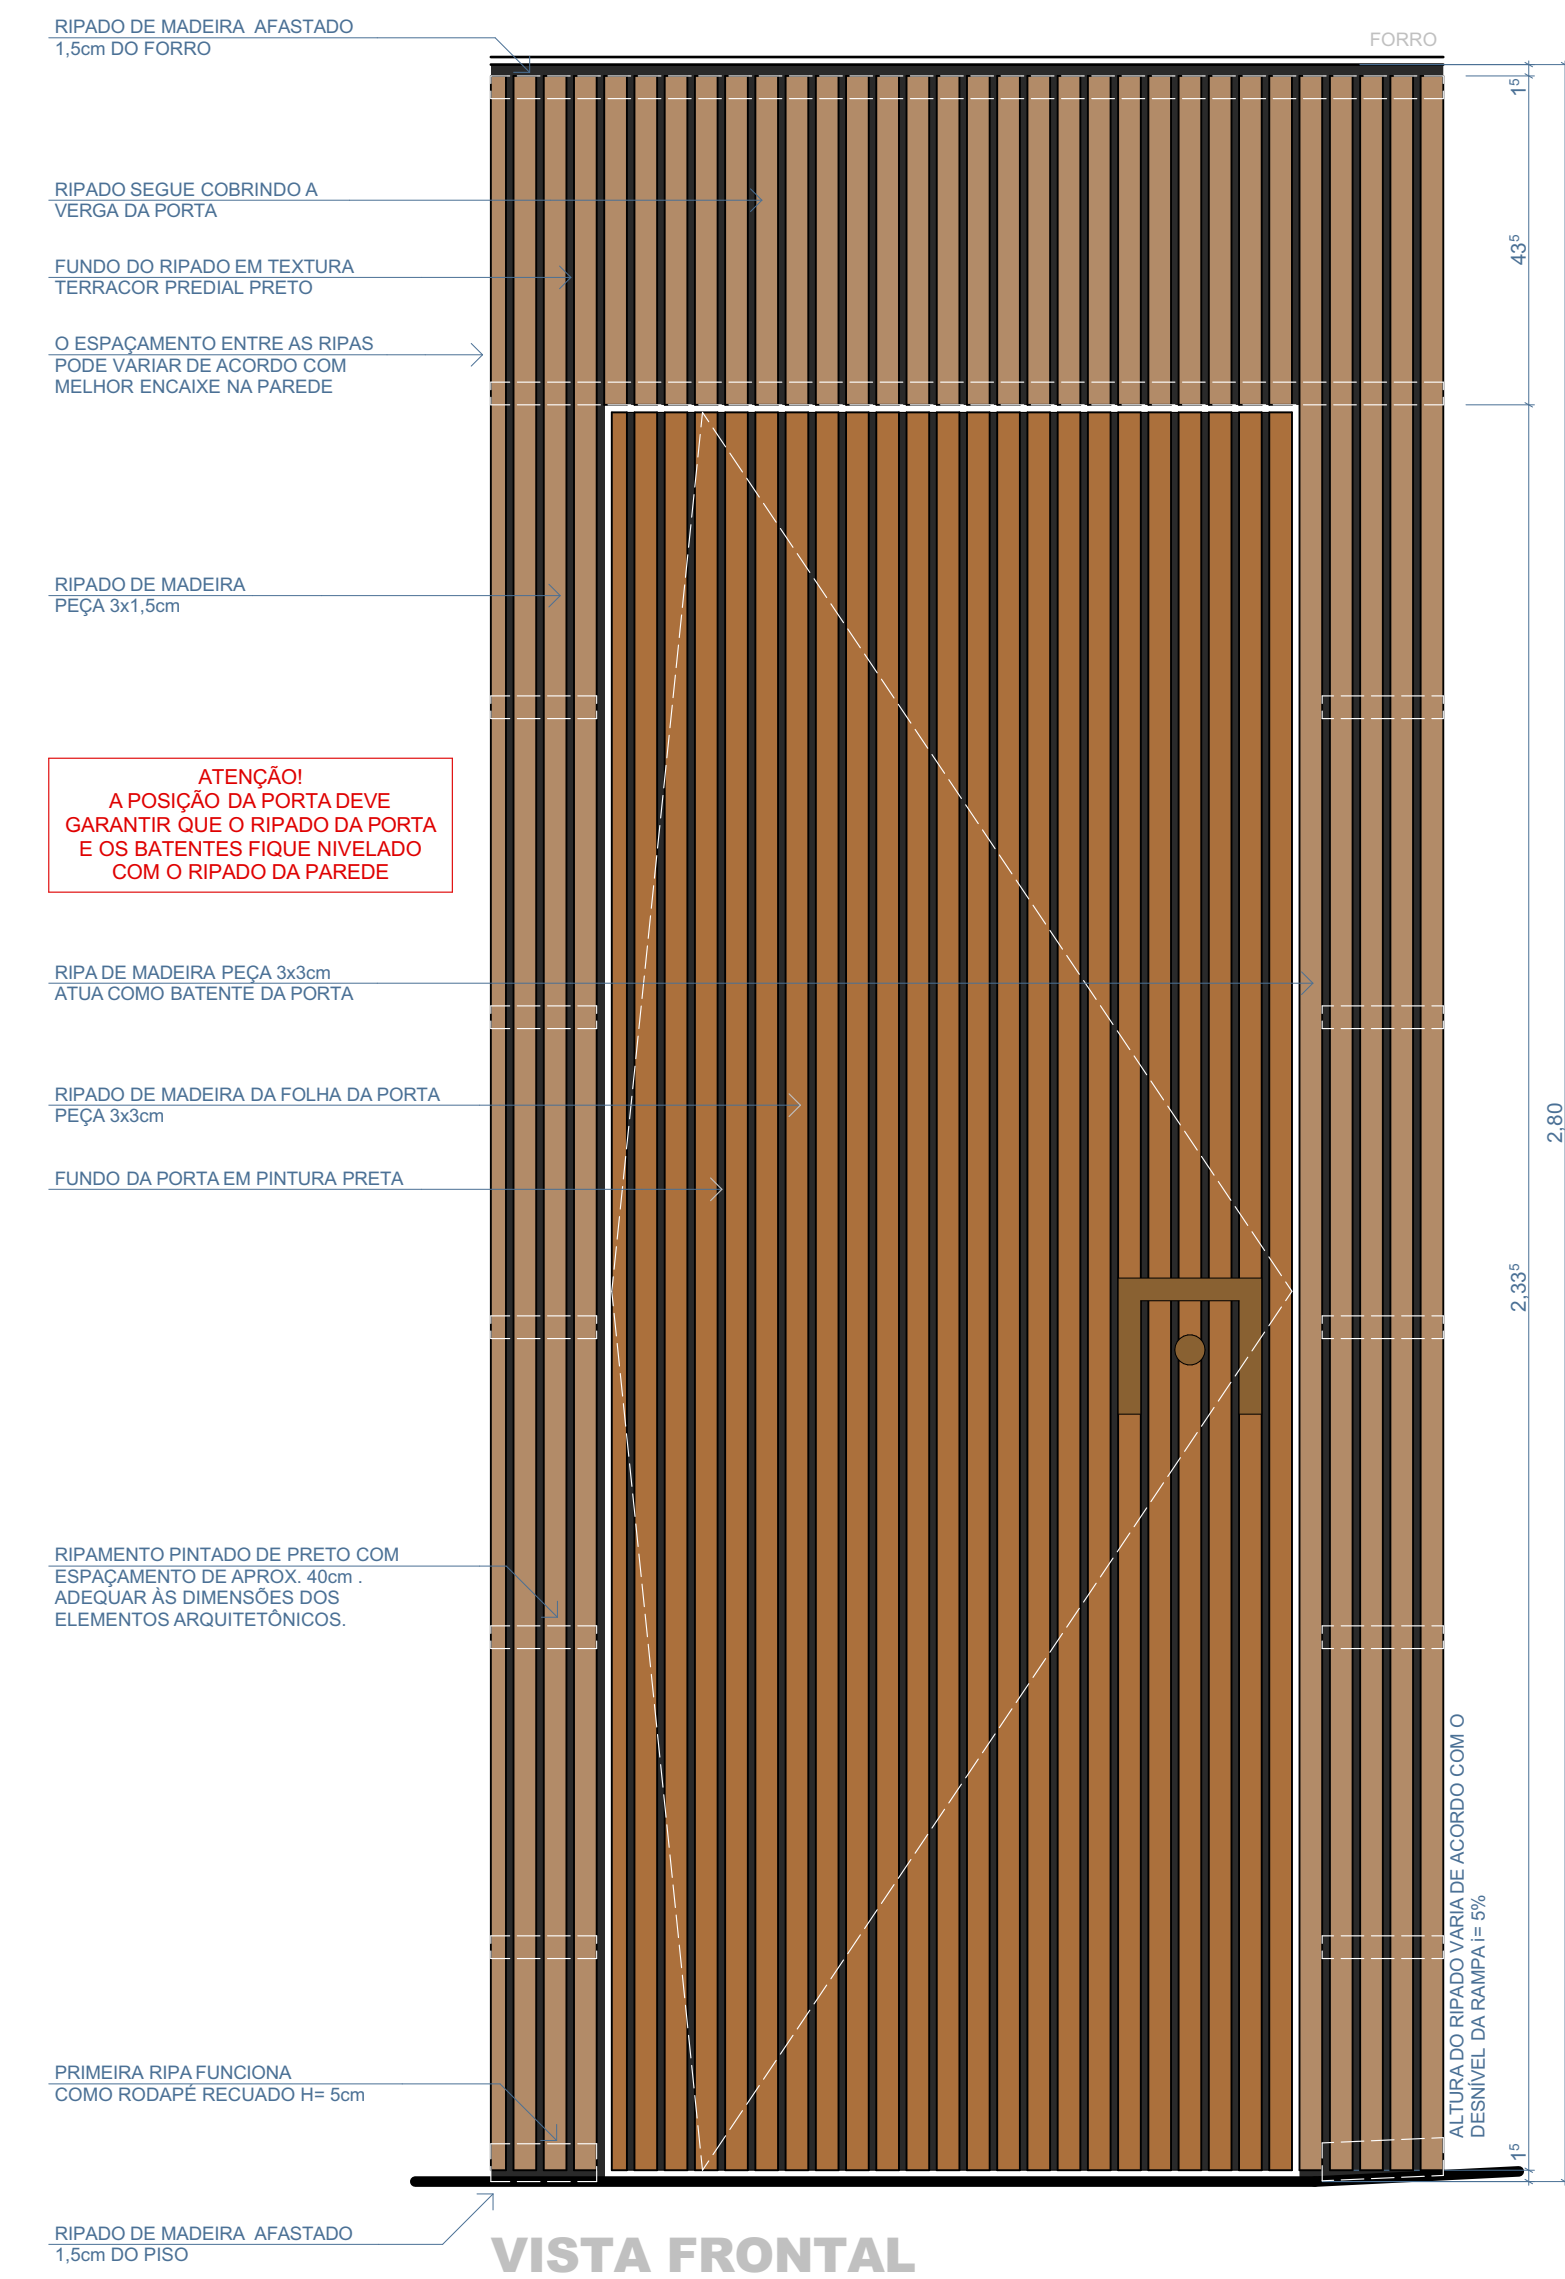

VISTA FRONTAL

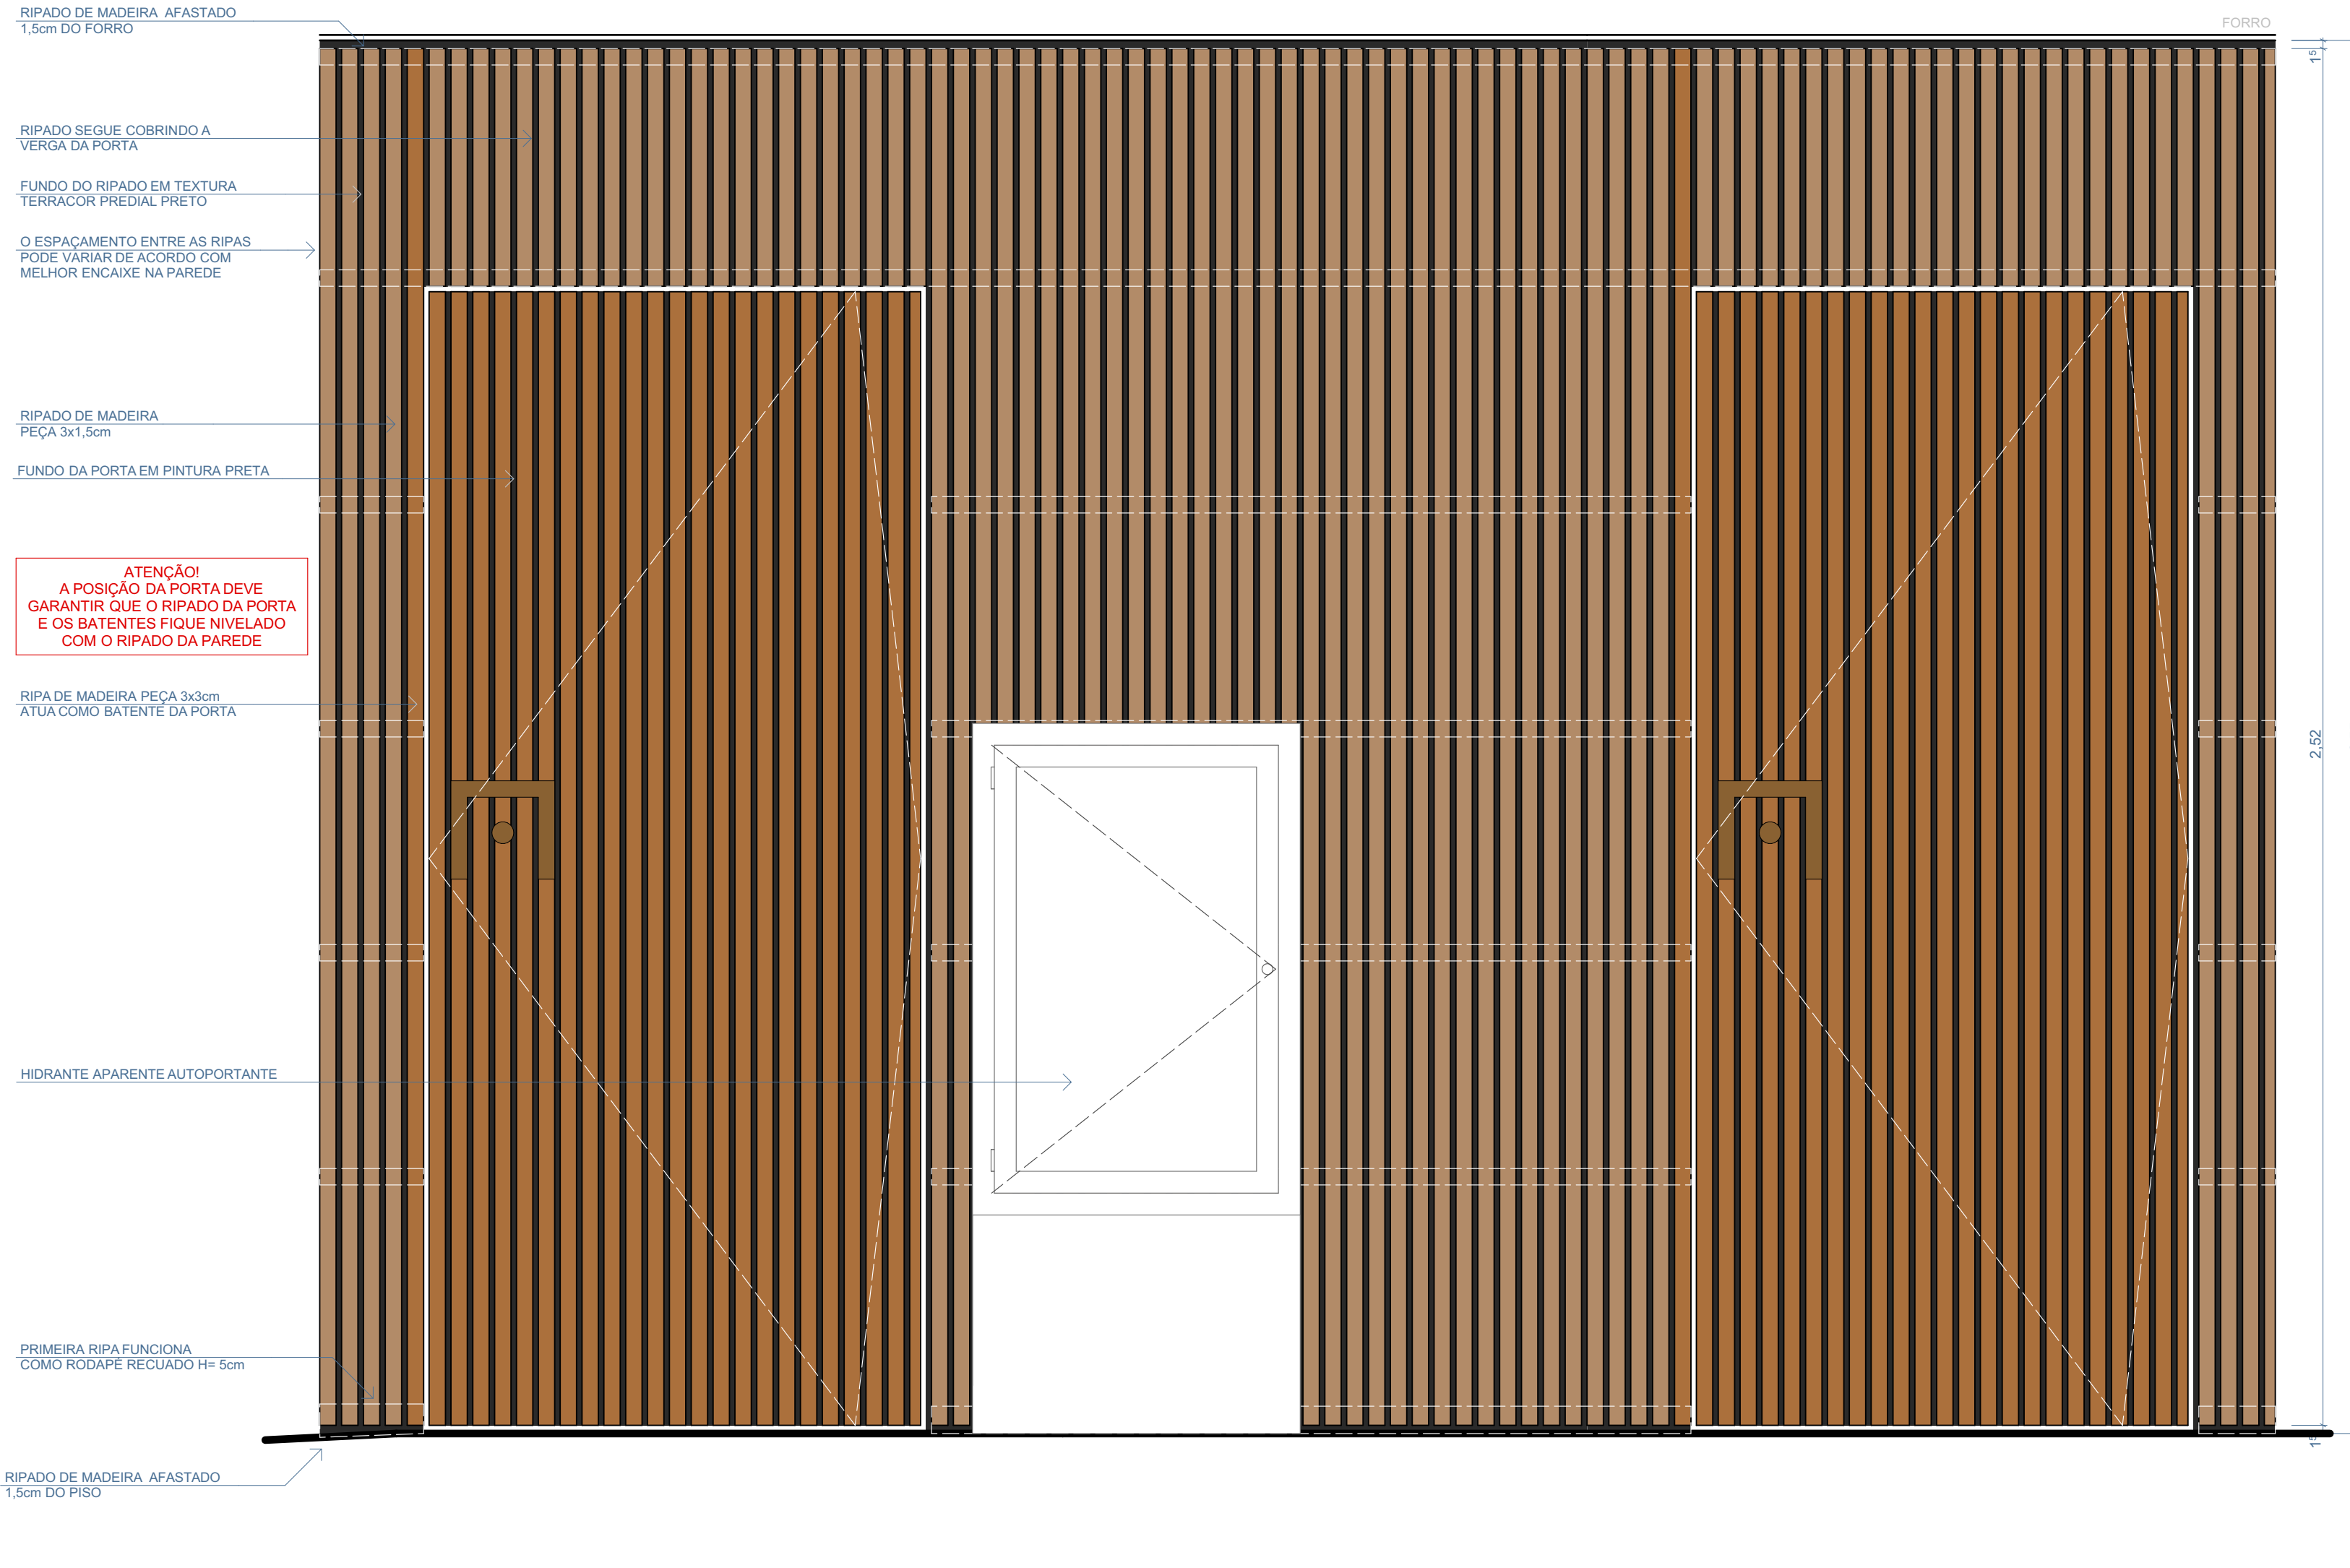

VISTA FRONTAL

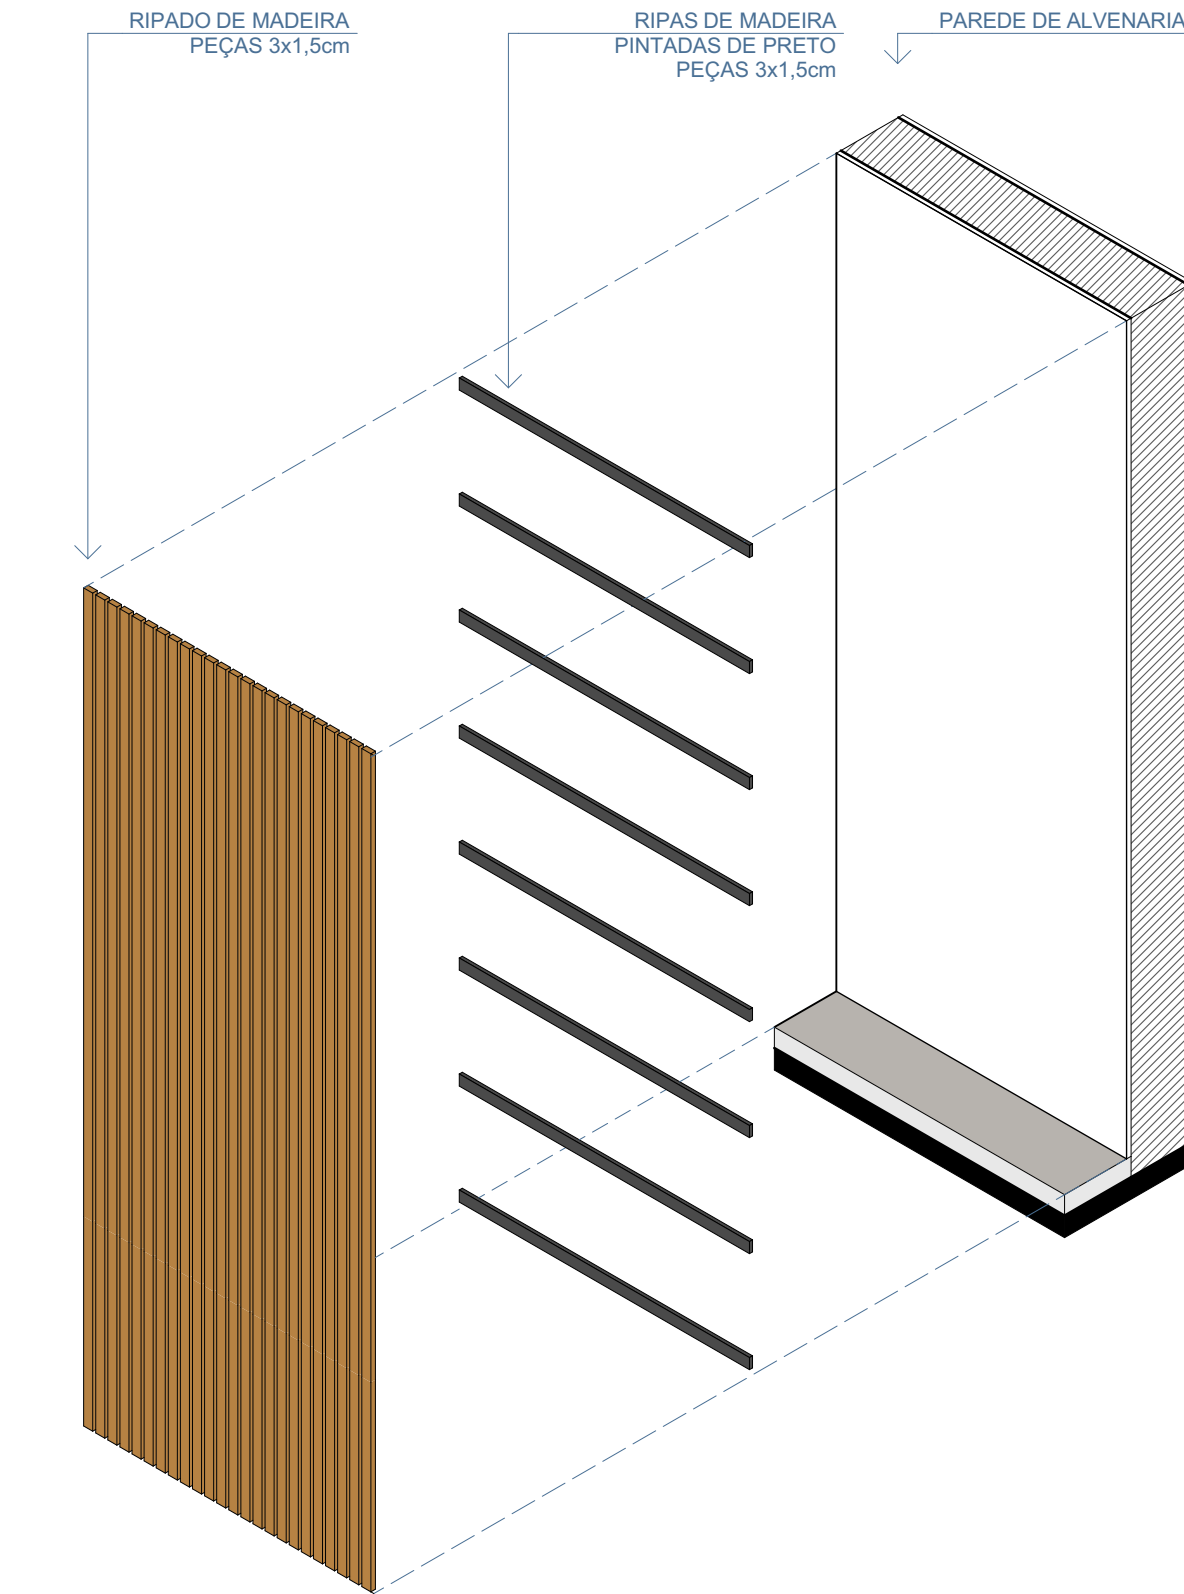

ISOMÉTRICA - RIPADO

PROJETO ARQUITETÔNICO

MAUI
INTERIORES DETALHAMENTO - MARCENARIA -
RIPADO CIRCULAÇÃO ABERTA ROOFTOP

ETAPA	OUZ, MAUI, ARO, PROJETO EXECUTIVO DETALHAMENTOS	A1 EST.
DATA	12/05/2024	
ESCALA	1:25, 1:10	
ENDEREÇO	Rodovia SC-406, s/n, Praia Mole, Florianópolis, Santa Catarina	
ASSINATURA:		
CLIENTE	OUZ CPF/CNPJ:	
ASSINATURA:		
RESPONSÁVEL:	HENRIQUE PIMONT CAU A 20832-9	
DESENHO:	MAYCON PASSIG; ARTHUR ANDRADE; MIRELA MOSER	